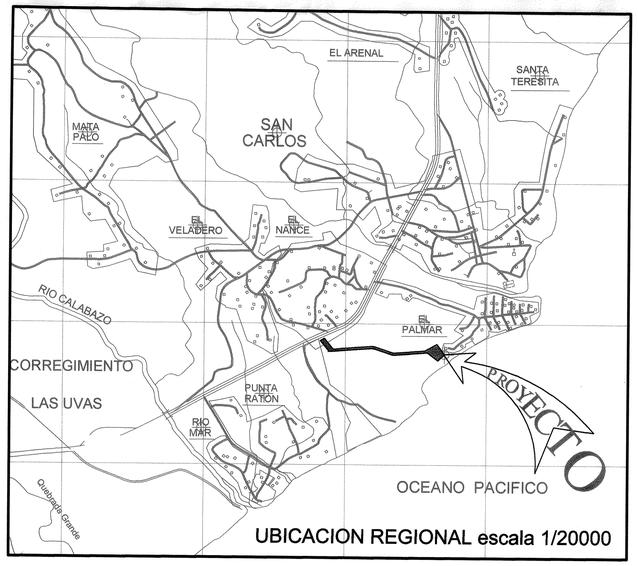

UBICACION REGIONAL escala 1/20000

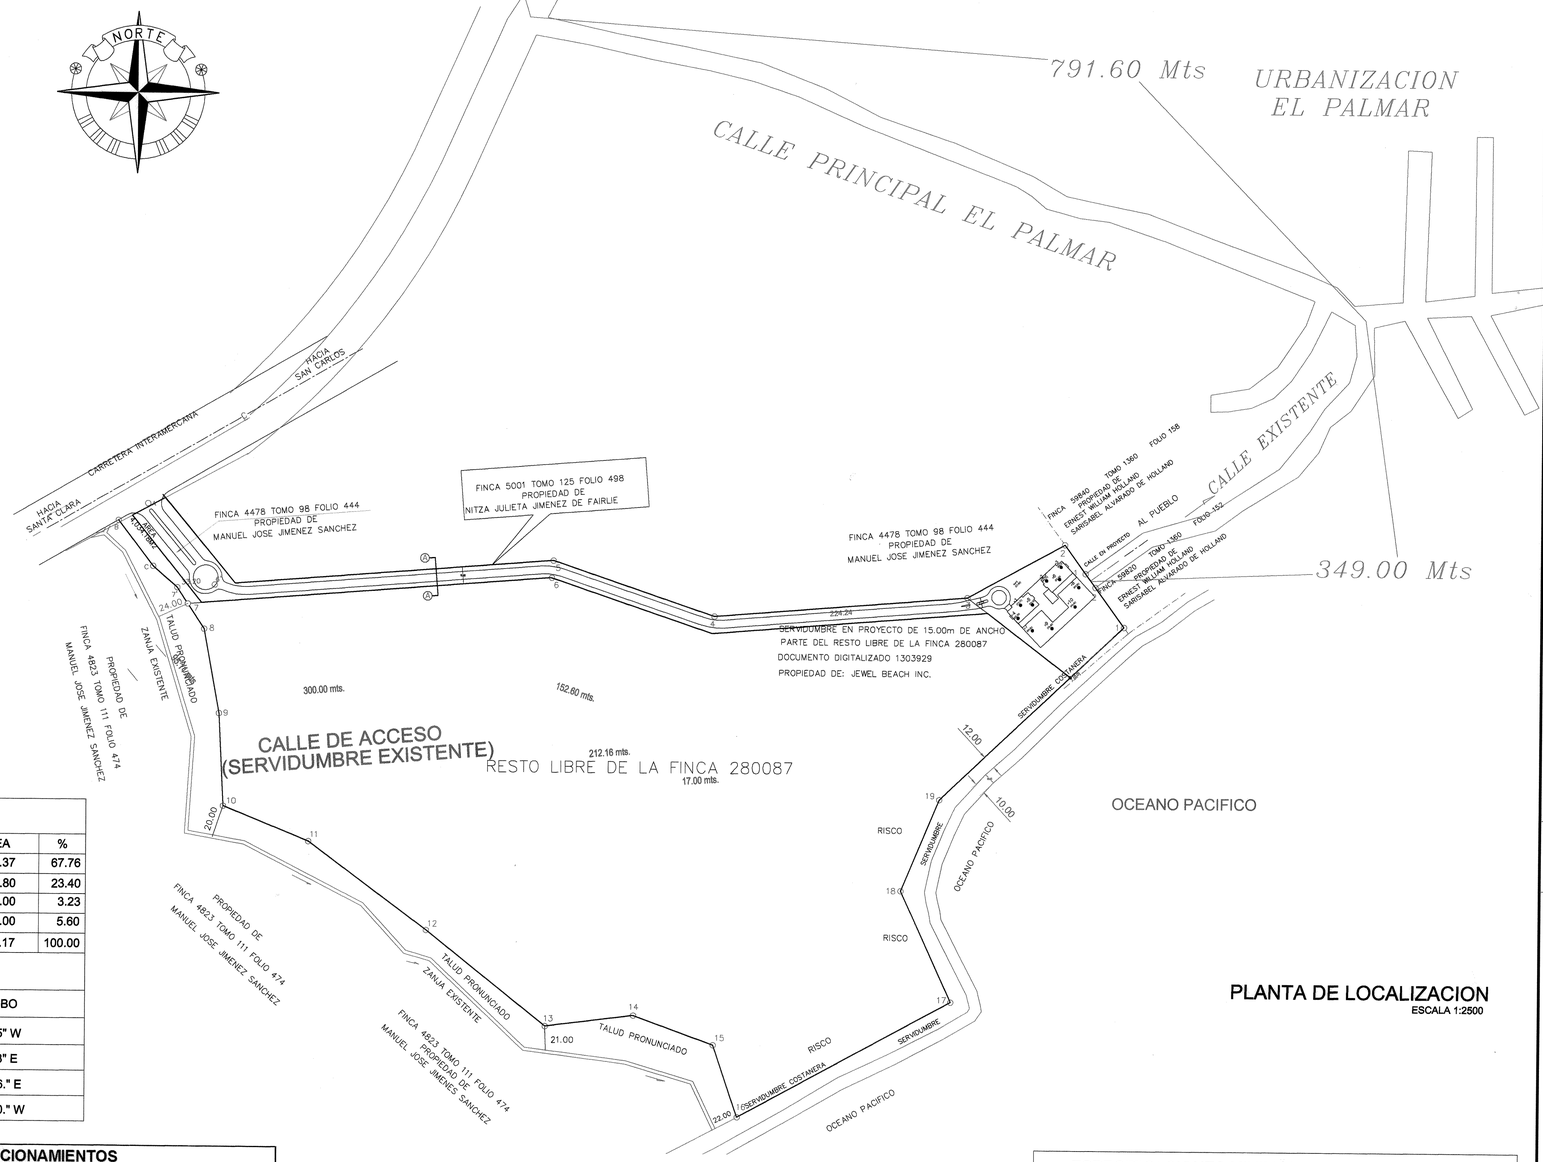

PLANTA DE LOCALIZACION
ESCALA 1:2500

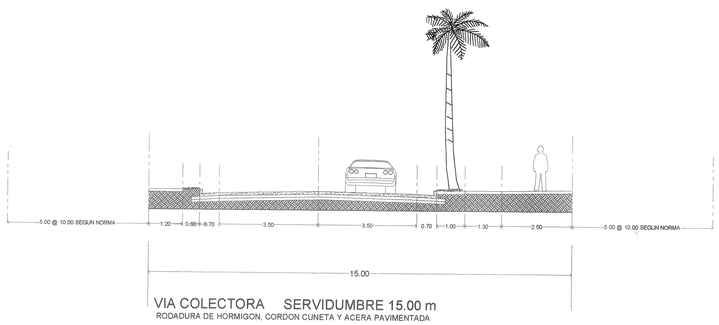

VIA COLECTORA SERVIDUMBRE 15.00 m
RODADURA DE HORMIGON, CORDON CUNETA Y ACERA PAVIMENTADA

INDICE DE PLANOS	
ARQUITECTURA	
1	LOC. REGIONAL Y DATOS GENERALES DEL LOTE
2	PLANTA ARQUITECTONICA N-400 (COMPLETO)
3	PLANTA DE ESTAC. Y APTOS. N-400 / TORRE C
4	PLANTA DE AREA SOCIAL N-400
5	PLANTA N-400 / DETALLE A / TORRE C
6	PLANTA N-400 / DETALLE B / TORRE C
7	PLANTA DE ESTAC. Y APTOS. N-200@-300 / TORRE C
8	PLANTA N-100@-300 / DETALLE A / TORRE C
9	PLANTA N-100@-300 / DETALLE B / TORRE C
10	PLANTA DE ESTAC. Y APTOS N-100 / TORRE C
11	PLANTA ARQUITECTONICA N 000 (COMPLETO)
12	PLANTA N 000
13	PLANTA N 000 / DETALLE A
14	PLANTA N 000 / DETALLE B
15	PLANTA N000 / DETALLE C
16	PLANTA ARQUITECTONICA N100 / TORRE A
17	PLANTA ARQUITECTONICA N100 / TORRE B
18	PLANTA ARQUITECTONICA N200@500 / TORRE A
19	PLANTA ARQUITECTONICA N200@500 / TORRE B
20	PLANTA ARQUITECTONICA N600@2200 / TORRE A
21	PLANTA ARQUITECTONICA N600@2200 / TORRE B
22	PLANTA ARQUITECTONICA N2300@2500 / TORRE A
23	PLANTA ARQUITECTONICA N2300@2500 / TORRE B
24	PLANTA ARQUITECTONICA N2600 / TORRE A
25	PLANTA ARQUITECTONICA N2600 / TORRE B
26	PLANTA ARQUITECTONICA N2700 / TORRE A
27	PLANTA ARQUITECTONICA N2700 / TORRE B
28	PLANTA ARQUITECTONICA N2800 / TORRE A
29	PLANTA ARQUITECTONICA N2800 / TORRE B
30	PLANTA ARQUITECTONICA N2900 / TORRE A
31	PLANTA ARQUITECTONICA N2900 7 TORRE B
32	DETALLES DE COCINAS
33	DETALLES DE COCINAS
34	DETALLES DE COCINAS
35	DETALLES DE BAÑOS
36	DETALLES DE BAÑOS
37	DETALLES DE BAÑOS
38	DETALLES DE BAÑOS
39	DETALLES DE BAÑOS
40	DETALLES DE BAÑOS
41	DETALLES DE BAÑOS
42	DETALLES DE CLOSETS
43	DETALLES DE CLOSETS
44	ELEVACION FRONTAL
45	ELEVACION LATERAL DERECHA
46	ELEVACION POSTERIOR
47	ELEVACION LATERAL IZQUIERDA
48	SECCION A
49	SECCION B
50	SECCION C
51	SECCION D
52	CUADRO DE ACABADOS Y DETALLES
53	CUADRO DE PUERTAS / TORRE A
54	CUADRO DE PUERTAS / TORRE A
55	CUADRO DE PUERTAS / TORRE B
56	CUADRO DE PUERTAS / TORRE B
57	CUADRO DE VENTANAS / TORRE A
58	CUADRO DE VENTANAS / TORRE B
59	CUADRO DE PUERTAS Y VENTANAS / TORRE C
60	DETALLE DE CIELO RASO N100@2700
61	DETALLE DE CIELO RASO N-400 (AMPLIACION A)
62	DETALLE DE CIELO RASO N-400 (AMPLIACION B)
63	DETALLE DE CIELO RASO N-100@-300 (AMPLIACION A)
64	DETALLE DE CIELO RASO N-100@-300 (AMPLIACION B)
65	DETALLE DE CIELO RASO N 000

DATOS DE LA FINCA

FINCA: 285335
DOCUMENTO DIGITALIZADO: 1401047
CODIGO DE UBICACION: 8801

NORMA ZONIFICACIÓN

ZONIFICACIÓN: RM2 (1000 personas/hectarea)
SUPERFICIE FINCA: 8069.36 m2
DENSIDAD PERMITIDA: 800 personas
DENSIDAD PROPUESTA: 734 personas

DESGLOSE DE AREAS

DESCRIPCION	AREA	%
SUPERFICIE RESIDENCIAL	25964.37	67.76
SUPERFCIE DE ESTACIONAMIENTOS	8698.80	23.40
SUPERFICIE AREA SOCIAL PLANTA BAJA	1200.00	3.23
SUPERFICIE DE AREA SOCIAL NIVEL -400	2086.00	5.60
TOTAL DE SUPERFICIE	37949.17	100.00

DATOS DE CAMPO

ESTAC		DISTANCIA	RUMBO
1	2	98.16	S 61°07'45" W
2	3	115.24	S 52°37'03" E
3	4	65.00	N 46°29'46." E
4	1	89.76	N 36°00'00." W

CUADRO DE ESTACIONAMIENTOS

APARTAMENTOS				ESTAC.S REQUERIDOS		
TIPO	TORRE A	TORRE B	TORRE C	EST/APART.	TOTAL	VISITA
PH	2	2		2	8	10%TOTAL
3R	6	6	8	2	40	
2R	44	44		1	88	
1R	44	44	31	1	119	
TOTAL	96	96	39		255	26
					281	

ESTAC. PROPUESTOS	
NIVEL 000	10
NIVEL -100	66
NIVEL -200	68
NIVEL -300	68
NIVEL -400	70
TOTAL CUBIERTOS=	272
TOTAL DESCUBIERTOS=	10
TOTAL ESTACIONAMIENTOS=	**282**

ESPECIFICACIONES MINIMAS DE CALLES

RODADURA DE ASFALTO Y CUNETA PLUVIAL ABIERTA

1.- DOBLE TRATAMIENTO SUPERFICIAL.
- A- IMPRIMACION Y DOBLE SELLO CON PIEDRA DE 3/4" Y 3/8".
- B- PENDIENTE DE LA CORONA 3 %.

2.- BASE DE MATERIAL PETREO DE 15 CMS. DE ESPESOR.
- A.- TAMAÑO MAXIMO 1 1 /2 ".
- B.- COMPACTACION 100 % (A.A.S.HTO T-99).
- C.- C. B. R. MINIMO AL 80 %.

3.- SUB-BASE DE MATERIAL SELECTO DE 15 CMS. DE ESPESOR
- A.- TAMAÑO MAXIMO DE 3 ".
- B.- COMPACTACION 100
- C.- C. B. R. MINIMO AL 80 %.

4.- ALINEAMIENTO.
- A.- PENDIENTE MINIMA DE 1 %.
- B.- PENDIENTE MAXIMA DE 12 %.

5.- SUB - RASANTE.
- A.- COMPACTACION DE LOS ULTIMOS 30 CMS. 100 % (A.A.S.HTO T-99).
- B.- COMPACTACION DEL RESTO DEL RELLENO 95 % (A.A.S.HTO T-99).

6.- CUNETAS.
- A.- LA CUNETA SERA

7.- ACERAS
- A.- HORMIGON DE 1,500 LIBRAS / PULGADAS CUADRADAS
- B.- ESPESOR .10 m
- C.- COMPACTACION 95% (A.A.S.HTO T-99).

Ministerio de Salud
Gestión Panamá Crisol de Salud
Dirección de Ingeniería y Arquitectura de Salud
D.I.S.
25 MAR 2011
APROBADO
Sanidad Ambiental
No. Rótulo

INGENIERIA MUNICIPAL
DISTRITO DE SAN CARLOS
APROBADO
INGENIERO MUNICIPAL

DIRECCION DE INFRAESTRUCTURAS DE SALUD
Salud
Ministerio de Salud
Región Coclé Oeste

Cuerpo de Bomberos
OFICINA DE SEGURIDAD
La Chorrera
Resolución No. Plano No.
Se aprueba el plano por llenar los condiciones requeridas

Vo.Bo. de la Oficina de Seguridad

RICAUTER A. BOWENT.
INGENIERO CIVIL
LICENCIA No. 2000-005-040
FIRMA
Ley 15 del 26 de Enero de 1959
Junta Técnica de Ingeniería y Arquitectura

FELIPE GONZÁLEZ LINCK
ARQUITECTO
LICENCIA No. 97-180
LEY 15 DE 26 DE ENERO DE 1959
JUNTA TECNICA DE INGENIERIA Y ARQUITECTURA

FELIFE GONZÁLEZ LINCK
ARQUITECTO
Tel. -- 66771610 -- Fax 392-2457 | 64035839

DISEÑO ARQUITECTÓNICO	Arq. Vicente Cortes Arq. Igor Cortes
DESARROLLO	Arq. Igor Cortes Arq. Ilem Segismond Arq. Nancy Urriola
PROYECTO ESTRUCTURAL	Ing. Ricauter Bowen
PROYECTO ELÉCTRICO	Ing. Edgar Naranjo
PROYECTO DE PLOMERÍA	Ing. Gilberto Ayala

PROYECTO
Residencial El Palmar

UBICACIÓN
COMUNIDAD DE 'EL PALMAR'
DTTO. DE SAN CARLOS - CORREGIMIENTO DE SAN CARLOS
PANAMÁ

SOCIEDAD PROMOTORA
Inversiones Decuria, S.A.
Representante legal: IGOR CORTES
Número de cédula o pasaporte: PC054493

INGENIERÍA MUNICIPAL

PLANO
- UBICACION REGIONAL
- LOCALIZACION GENERAL
- DATOS DE LA FINCA
- CALCULOS

ARCHIVO .DWG	LOC. REG Y DATOS DE FINCA
FECHA	30/08/2010
FECHA MODIFICACIÓN	DD/MM/AAAA

ARQUITECTURA | HOJA: 1 | DE: 65

AR ESTACIONAMIENTO Y PLANTA ARQUITECTONICA NIVEL -400

ESCALA: 1:200

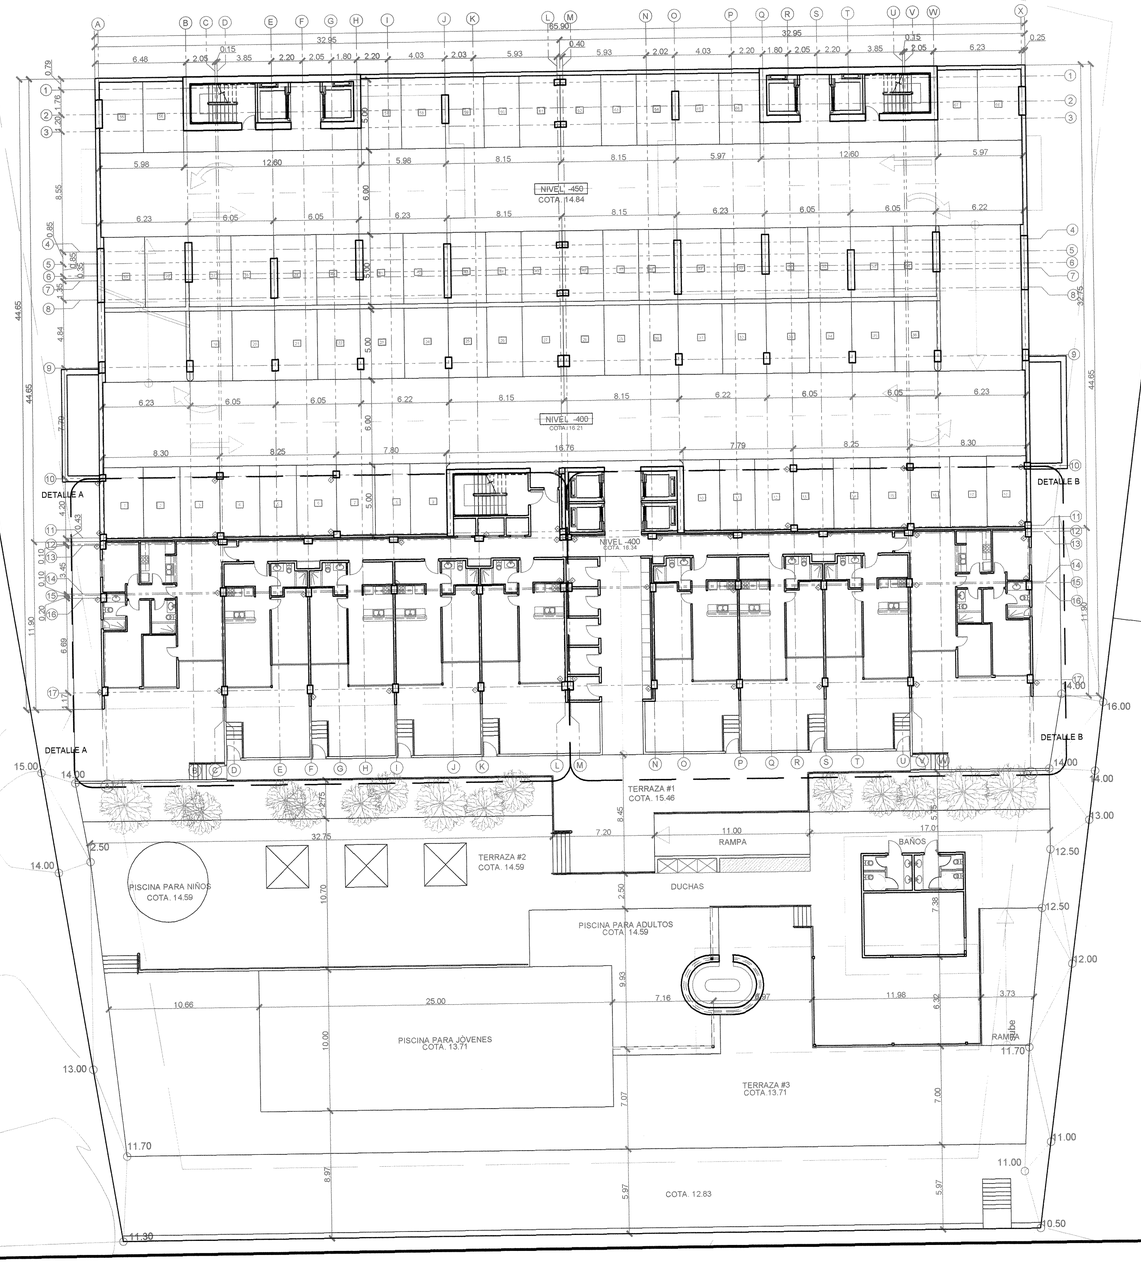

INGENIERIA MUNICIPAL
DISTRITO DE SAN CARLOS
APROBADO
INGENIERO MUNICIPAL
FECHA 22/8/11

Cuerpo de Bomberos
OFICINA Prev. de San Carlos

La Chorrera 11 de Agosto de 2011
Resolución No. 376 Plano No. 40-11
Se aprueba el registro de este plano por cumplir las condiciones requeridas

Jefe de la Oficina de Seguridad

FELIPE GONZÁLEZ LINCK
ARQUITECTO
LICENCIA No. 10-11102
LEY 15 DEL 26 DE ENERO DE 1959
JUNTA TECNICA DE INGENIERIA Y ARQUITECTURA

FELIFE GONZÁLEZ LINCK
ARQUITECTO
Tel. – 66771610 – Fax 392-2457 | 64035830

DISEÑO ARQUITECTÓNICO	Arq. Vicente Cortes Arq. Igor Cortes
DESARROLLO	Arq. Igor Cortes Arq. Ilem Segismond Arq. Nancy Urriola
PROYECTO ESTRUCTURAL	Ing. Ricauter Bowen
PROYECTO ELÉCTRICO	Ing. Edgar Naranjo
PROYECTO DE PLOMERÍA	Ing. Gilberto Ayala

PROYECTO

Residencial El Palmar

UBICACIÓN

COMUNIDAD DE 'EL PALMAR'
DTTO. DE SAN CARLOS - CORREGIMIENTO DE SAN CARLOS
PANAMÁ

SOCIEDAD PROMOTORA

Inversiones Decuria, S.A.

Representante legal: IGOR CORTES
Número de cédula o pasaporte: 8C054493

INGENIERÍA MUNICIPAL

PLANO

- PLANTA ARQUITECTONICA N-400
  ESCALA 1/200

ARCHIVO .DWG	NIVEL-400
FECHA	30/08/2010
FECHA MODIFICACIÓN	DD/MM/AAAA

ARQUITECTURA | HOJA: 2

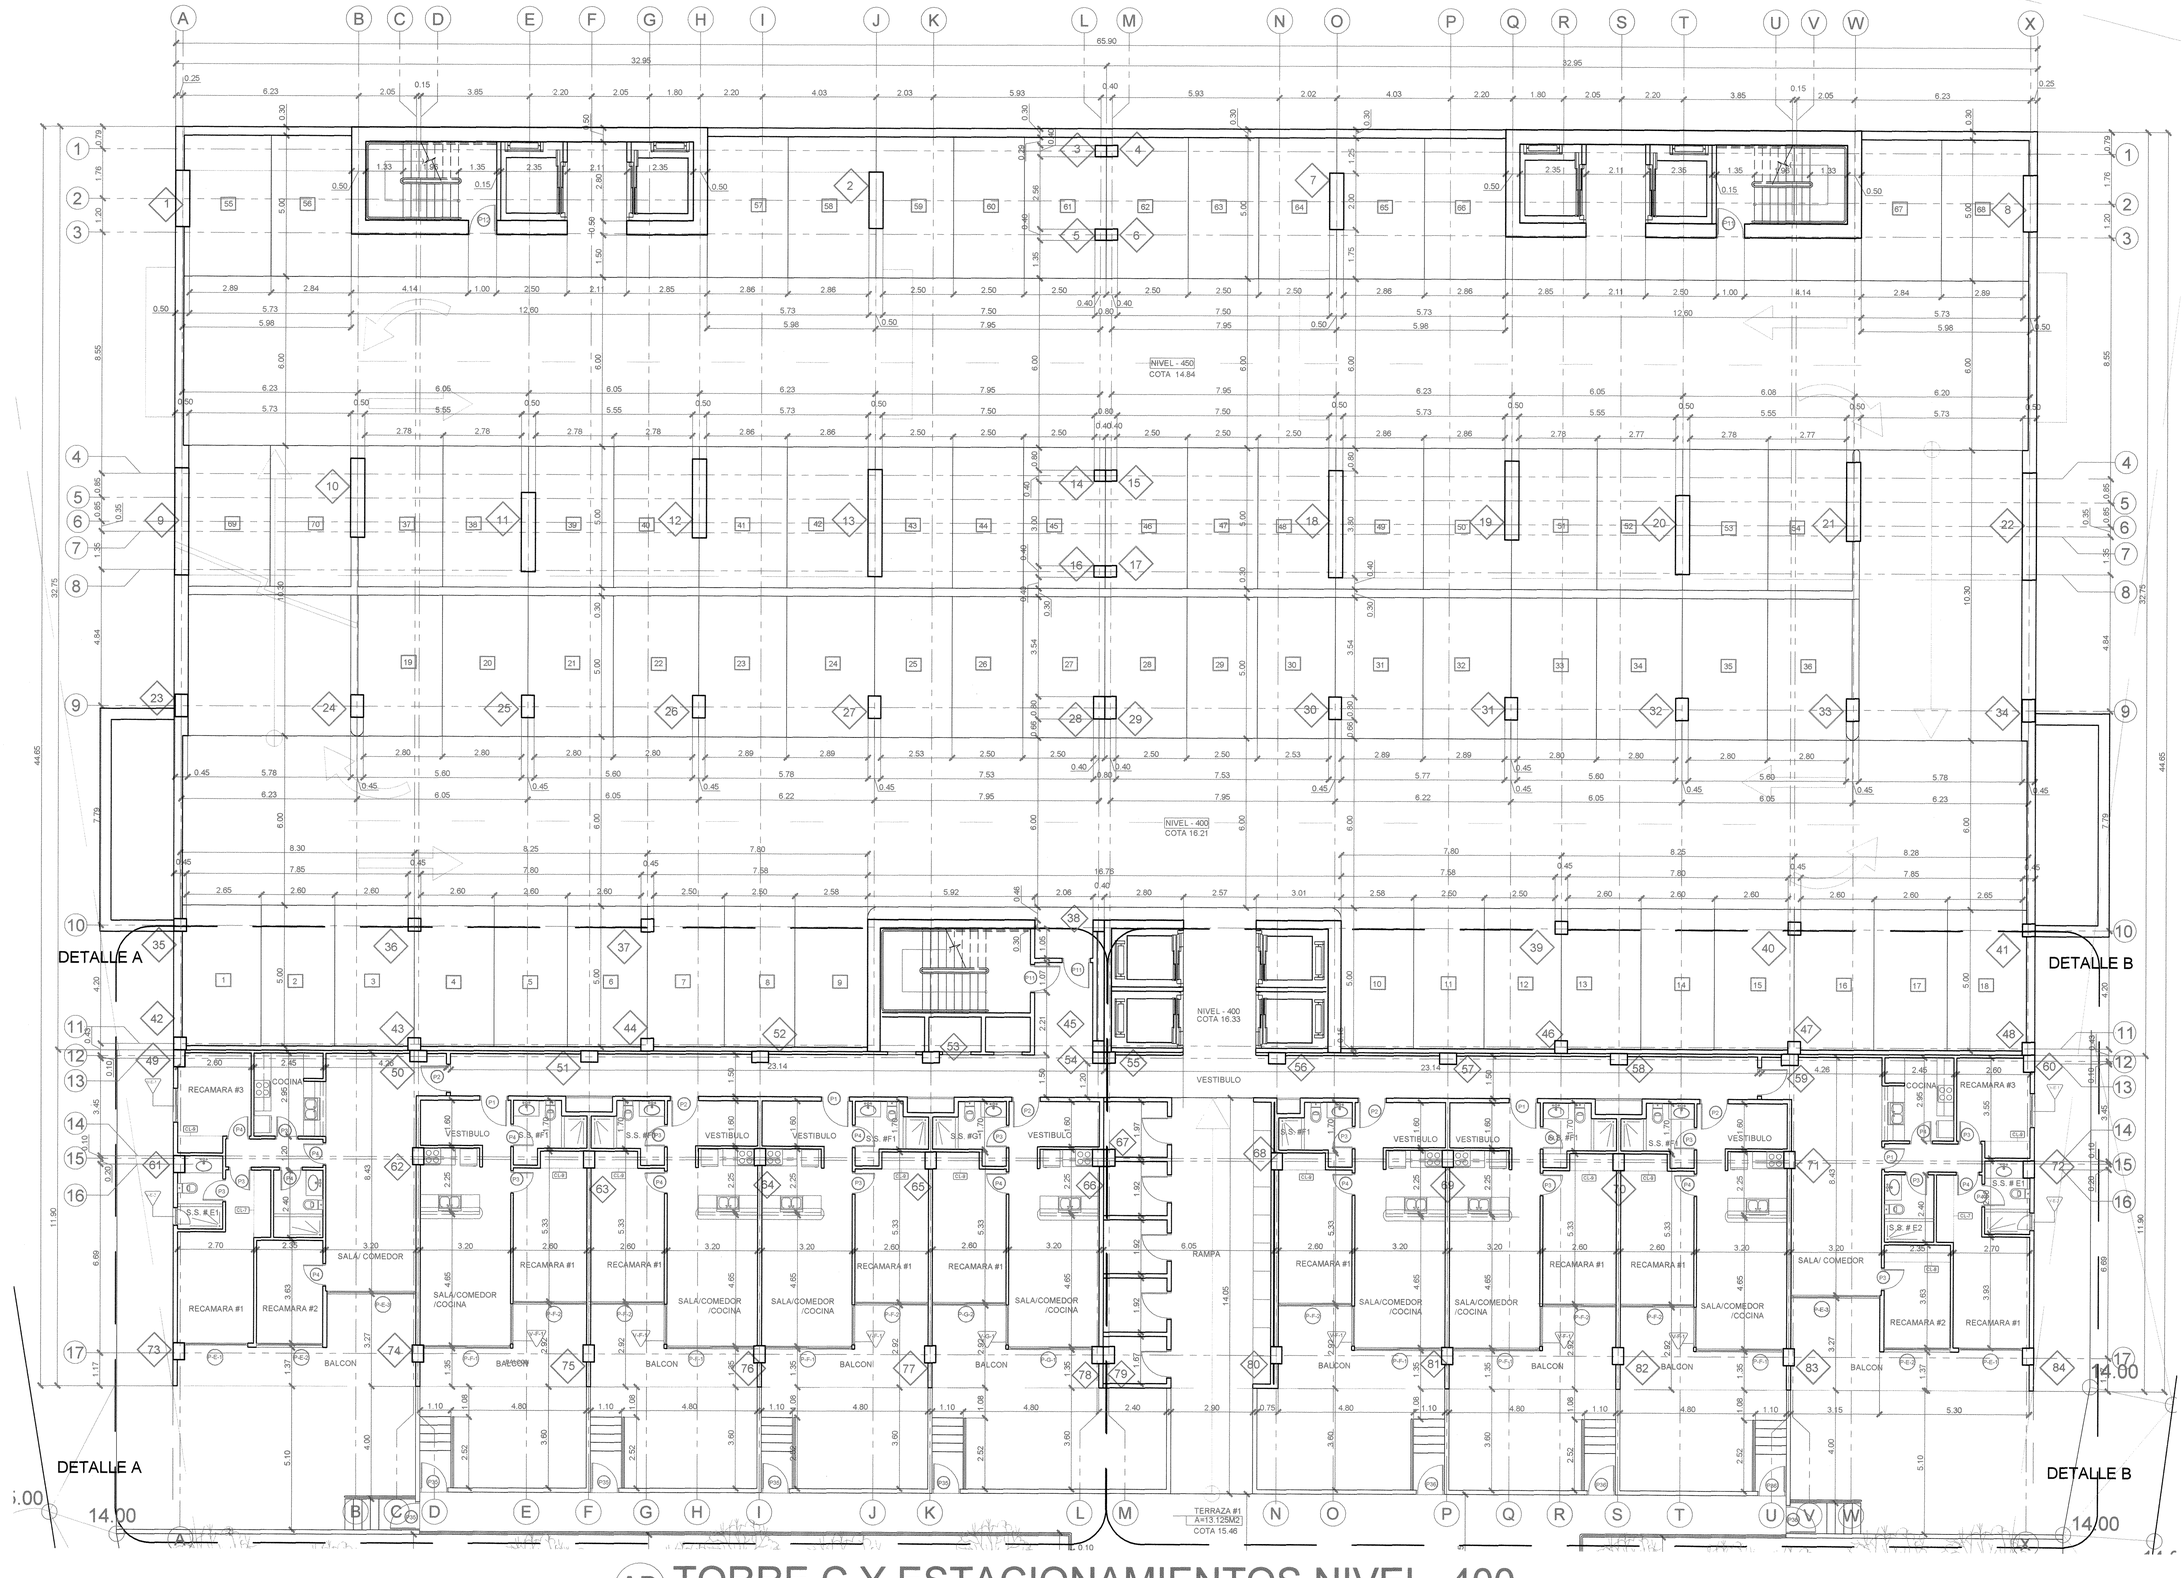

TORRE C Y ESTACIONAMIENTOS NIVEL -400

ESCALA 1/100

INGENIERIA MUNICIPAL
DISTRITO DE SAN CARLOS
APROBADO
INGENIERO MUNICIPAL
FECHA 22/8/11

Cuerpo de Bomberos
OFICINA DE SEGURIDAD
La Chorrera 11 de agosto de 2011
Resolución No. 316 Plano No. 11-8
Se aprueba el presente plano por llenar las condiciones requeridas.
Jefe de la Oficina de Seguridad

FELIPE GONZALEZ LINCK
ARQUITECTO
LICENCIA No. 7-1182
LEY 15 DEL 26 DE ENERO DE 1959
JUNTA TECNICA DE INGENIERIA Y ARQUITECTURA

FELIFE GONZÁLEZ LINCK
ARQUITECTO
Tel. – 66771610 – Fax 392-2457 | 64035030

DISEÑO ARQUITECTÓNICO	Arq. Vicente Cortes Arq. Igor Cortes
DESARROLLO	Arq. Igor Cortes Arq. Ilem Segismond Arq. Nancy Urriola
PROYECTO ESTRUCTURAL	Ing. Ricauter Bowen
PROYECTO ELÉCTRICO	Ing. Edgar Naranjo
PROYECTO DE PLOMERÍA	Ing. Gilberto Ayala

PROYECTO

Residencial El Palmar

UBICACIÓN
COMUNIDAD DE 'EL PALMAR'
DTTO. DE SAN CARLOS - CORREGIMIENTO DE SAN CARLOS
PANAMÁ

SOCIEDAD PROMOTORA
Inversiones Decuria, S.A.
Representante legal: IGOR CORTES
Número de cédula o pasaporte: 8C054493

INGENIERÍA MUNICIPAL

PLANO
- TORRE C Y ESTACIONAMIENTO
NIVEL -400
ESCALA 1:100

ARCHIVO .DWG	NIVEL-400
FECHA	30/08/2010
FECHA MODIFICACIÓN	DD/MM/AAAA

ARQUITECTURA | HOJA: 3 | DE: 65

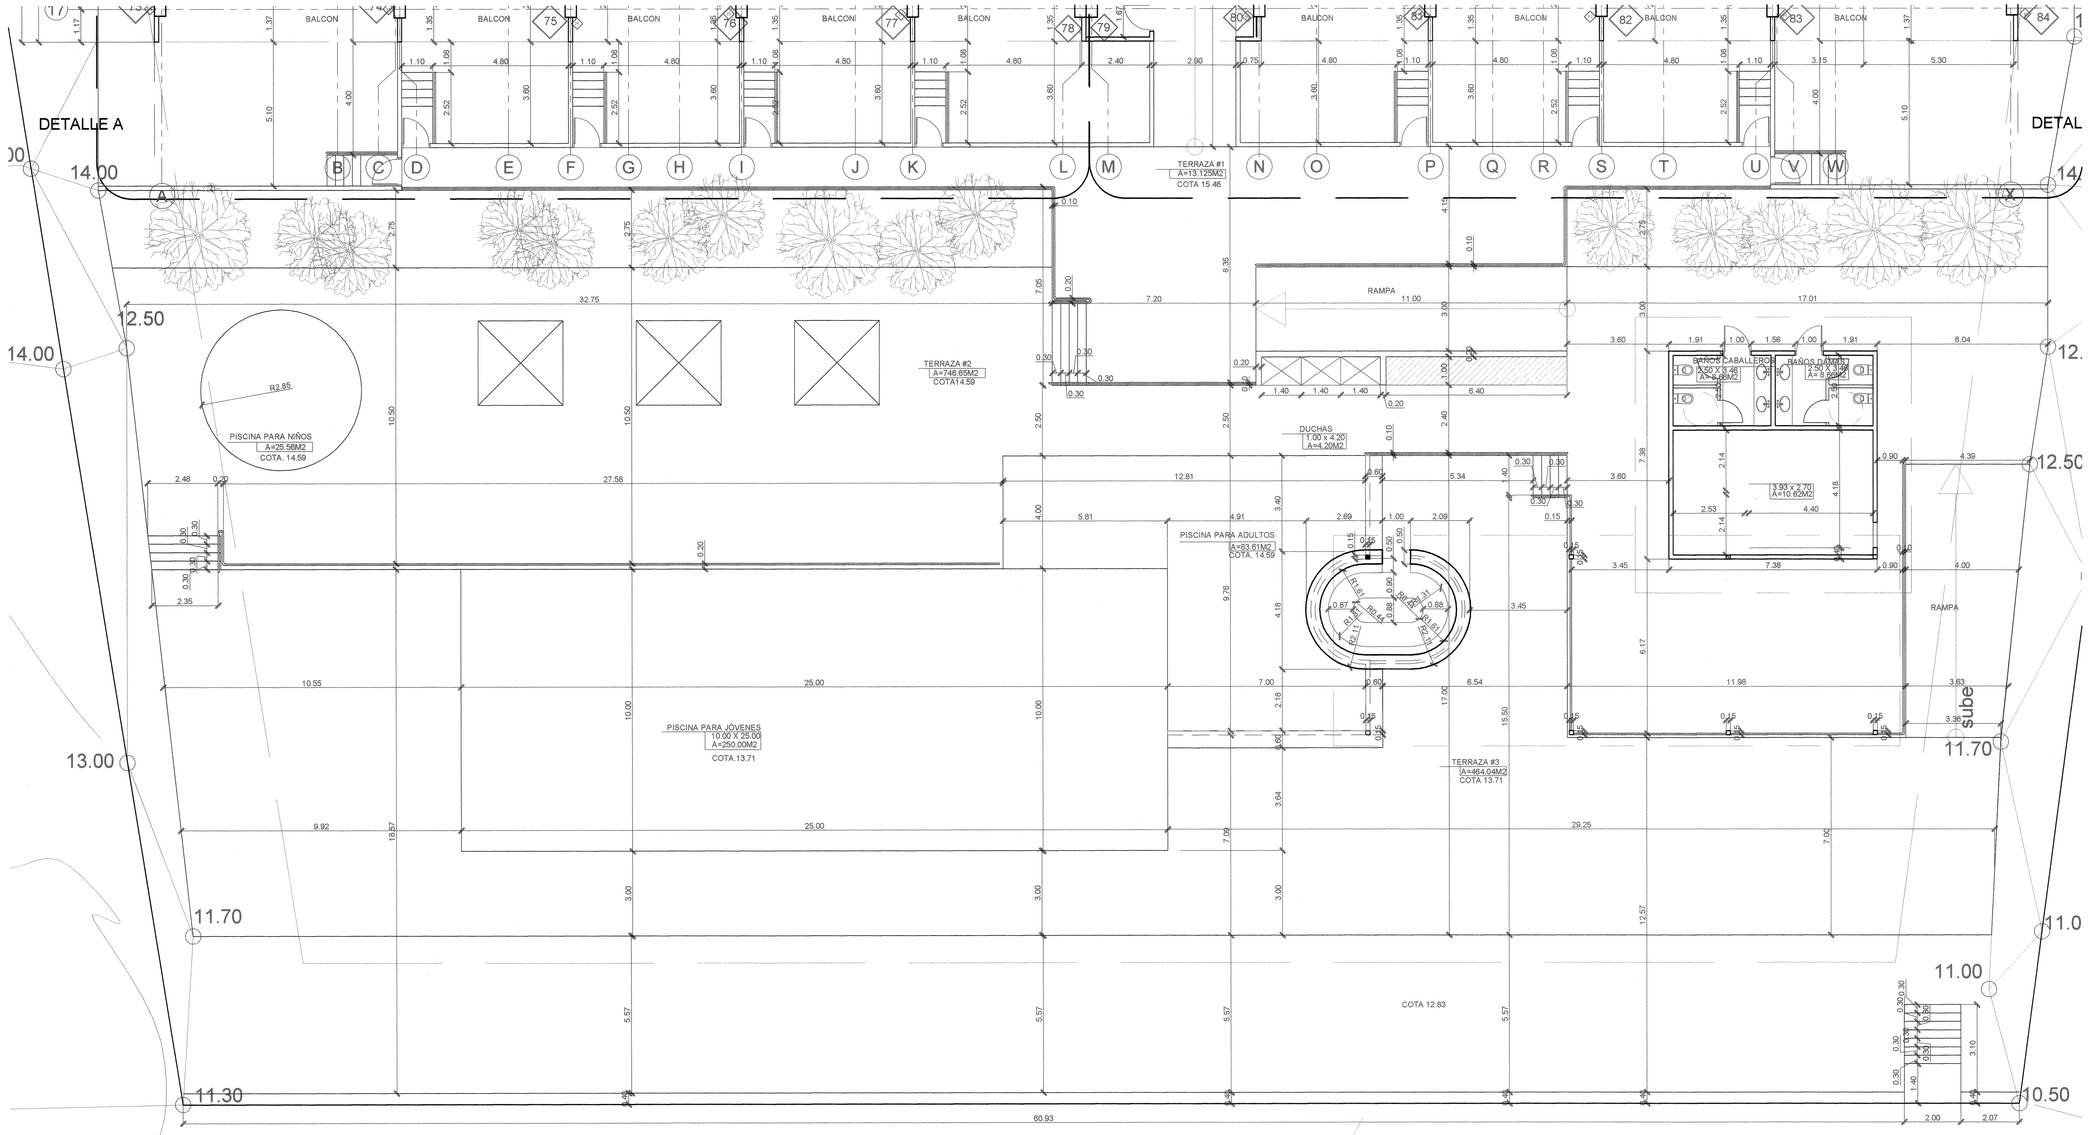

AREA SOCIAL NIVEL -400

ESCALA: 1:100

INGENIERIA MUNICIPAL
DISTRITO DE SAN CARLOS
APROBADO
INGENIERO MUNICIPAL
FECHA

Cuerpo de Bomberos
OFICINA DE SEGURIDAD
La Chorrera, ... de .....
Revisado: ..... Plano No. .....
Se aprueba el presente plano por llenar las condiciones respectivas.

Jefe de la Oficina de Seguridad

FELIPE GONZALEZ LINCK
ARQUITECTO
LICENCIA No. 7711-198
LEY 15 DEL 26 DE ENERO DE 1959
JUNTA TECNICA DE INGENIERIA Y ARQUITECTURA

FELIFE GONZÁLEZ LINCK
ARQUITECTO
Tel. -- 66771610 -- Fax 392-2457 | 64035839

DISEÑO ARQUITECTÓNICO	Arq. Vicente Cortes Arq. Igor Cortes
DESARROLLO	Arq. Igor Cortes Arq. Ilem Segismond Arq. Nancy Urriola
PROYECTO ESTRUCTURAL	Ing. Ricauter Bowen
PROYECTO ELÉCTRICO	Ing. Edgar Naranjo
PROYECTO DE PLOMERÍA	Ing. Gilberto Ayala

PROYECTO

Residencial El Palmar

UBICACIÓN

COMUNIDAD DE 'EL PALMAR'
DTTO. DE SAN CARLOS - CORREGIMIENTO DE SAN CARLOS
PANAMÁ

SOCIEDAD PROMOTORA

Inversiones Decuria, S.A.
Representante legal: IGOR CORTES
Número de cédula o pasaporte: 8COS4483

INGENIERÍA MUNICIPAL

PLANO

- AREA SOCIAL NIVEL-400
ESCALA 1:100

ARCHIVO .DWG	NIVEL-400
FECHA	30/08/2010
FECHA MODIFICACIÓN	DD/MM/AAAA

ARQUITECTURA | HOJA: 4 | DE: 65

DETALLE A

DETALLE A

14.00

RECAMARA #3
2.95 x 2.80
A= 8.46 M2

COCINA
2.95 x 2.45
A= 7.23 M2

S.S. #E1
A= 4.16 M2

S.S. #E2

RECAMARA #1
3.83 x 2.70
A=10.62M2

RECAMARA #2
3.83 x 2.35
A= 8.54M2

SALA/ COMEDOR
8.43 x 3.20
A=26.99M2

VESTIBULO
1.60 x 3.20
A=5.11M2

S.S. #F1
A= 4.43M2

RECAMARA #1
5.33 x 2.60
A=13.22M2

SALA/COMEDOR
/COCINA
7.00 x 3.20
A=22.25M2

BALCON
A=91.46M2

BALCON
A=33.14M2

S.S. #G1
A= 4.43M2

SALA/COMEDOR
/COCINA
A=22.25M2
7.00 x 3.20

RECAMARA #1
5.33 x 2.60
A=13.22M2

SALA/COMEDOR
/COCINA
7.00 x 3.20
A=22.25M2

BALCON
A=33.14M2

AR DETALLE A DE APARTAMENTOS TORRE C NIVEL - 400

ESCALA: 1:50

INGENIERIA MUNICIPAL
DISTRITO DE SAN CARLOS
APROBADO
INGENIERO MUNICIPAL
FECHA 22/6/11

Cuerpo de Bomberos
OFICINA DE SEGURIDAD
La Chorrera, 11 de agosto de 2011
Resolución No. 346
Se aprueba el respectivo plano, por llenar las condiciones requeridas.
Jefe de la Oficina de Seguridad

FELIPE GONZALEZ LINCK
ARQUITECTO
LICENCIA No. 7-1-1988
LEY 15 DE 26 DE ENERO DE 1959
JUNTA TECNICA DE INGENIERIA Y ARQUITECTURA

FELIFE GONZÁLEZ LINCK
ARQUITECTO
Tel. – 66771610 – Fax 392-2457 | 64035839

DISEÑO ARQUITECTÓNICO	Arq. Vicente Cortes Arq. Igor Cortes
DESARROLLO	Arq. Igor Cortes Arq. Ilem Segismond Arq. Nancy Urriola
PROYECTO ESTRUCTURAL	Ing. Ricauter Bowen
PROYECTO ELÉCTRICO	Ing. Edgar Naranjo
PROYECTO DE PLOMERÍA	Ing. Gilberto Ayala

PROYECTO

Residencial El Palmar

UBICACIÓN

COMUNIDAD DE 'EL PALMAR'
DTTO. DE SAN CARLOS - CORREGIMIENTO DE SAN CARLOS
PANAMÁ

SOCIEDAD PROMOTORA

Inversiones Decuria, S.A.

Representante legal: IGOR CORTES
Número de cédula o pasaporte: BC054493

INGENIERÍA MUNICIPAL

PLANO

- DETALLE A DE APARTAMENTOS
TORRE C - NIVEL-400
ESCALA 1:50

ARCHIVO .DWG	NIVEL-400
FECHA	30/08/2010
FECHA MODIFICACIÓN	DD/MM/AAAA

ARQUITECTURA | HOJA: 5 | DE: 6

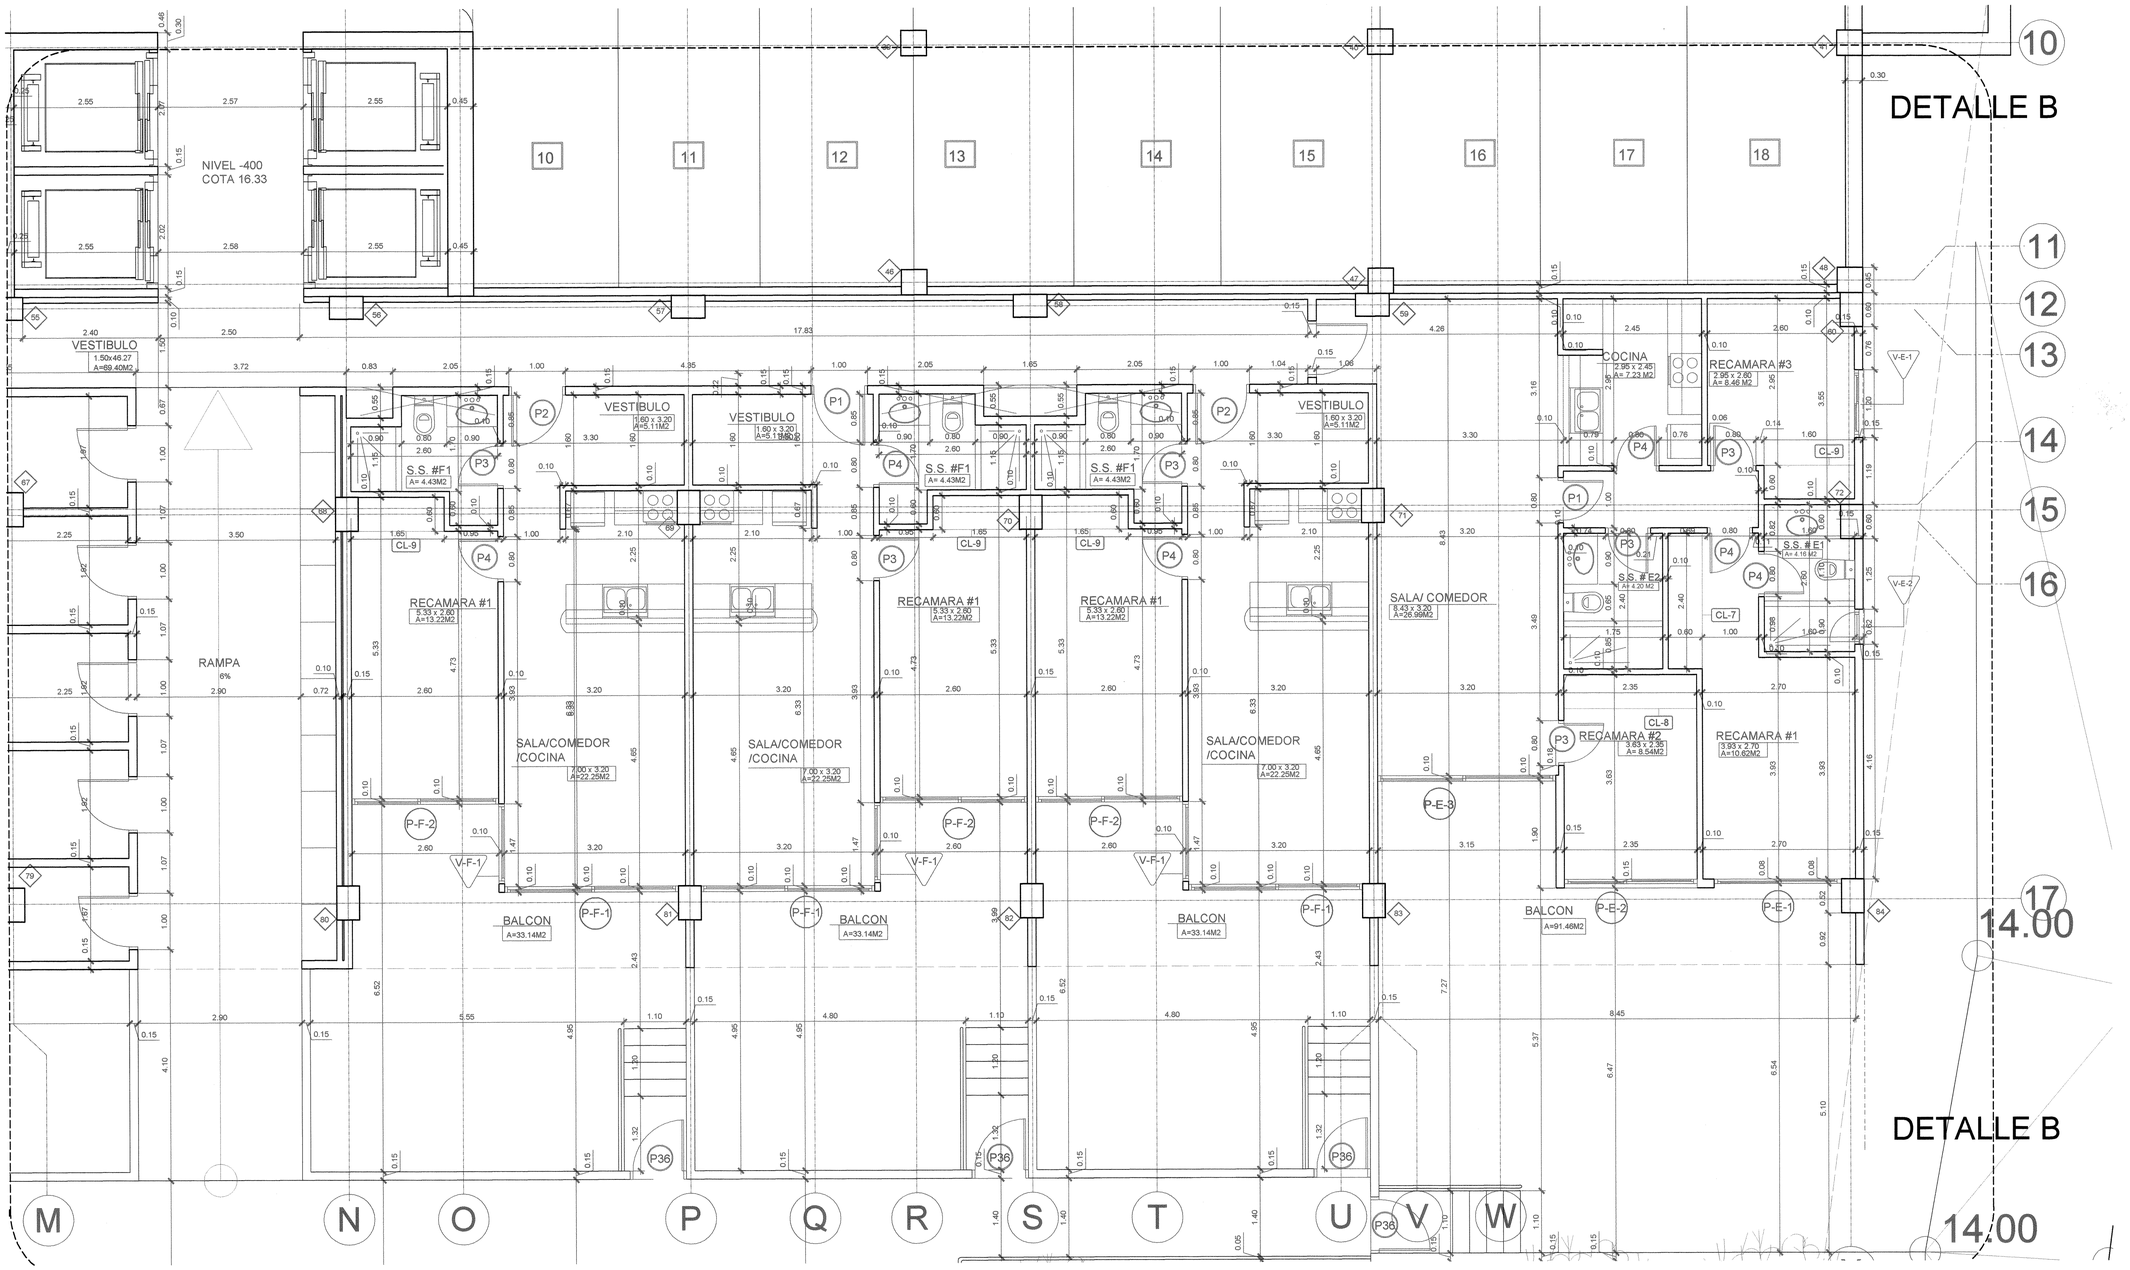

AR DETALLE B DE APARTAMENTOS TORRE C NIVEL - 400

ESCALA: 1:50

INGENIERIA MUNICIPAL
DISTRITO DE SAN CARLOS
APROBADO
INGENIERO MUNICIPAL
FECHA 22/8/11

Cuerpo de Bomberos
OFICINA DE SEGURIDAD
La Chorrera, 19 de Agosto de 2011
Resolución No. 0566 Plan No. 2011-0118
Se aprueba el respectivo Plan con las condiciones requeridas.
Jefe de la Oficina de Seguridad

FELIPE GONZALEZ LINCK
ARQUITECTO
EJECENCIA No. 97-1-168
LEY 15 DEL 26 DE ENERO DE 1959
JUNTA TECNICA DE INGENIERIA Y ARQUITECTURA

FELIFE GONZÁLEZ LINCK
ARQUITECTO
Tel. -- 66771610 -- Fax 392-2457 | 64035639

DISEÑO ARQUITECTÓNICO	Arq. Vicente Cortes Arq. Igor Cortes
DESARROLLO	Arq. Igor Cortes Arq. Ilem Segismond Arq. Nancy Urriola
PROYECTO ESTRUCTURAL	Ing. Ricauter Bowen
PROYECTO ELÉCTRICO	Ing. Edgar Naranjo
PROYECTO DE PLOMERÍA	Ing. Gilberto Ayala

PROYECTO

Residencial El Palmar

UBICACIÓN

COMUNIDAD DE 'EL PALMAR'
DTTO. DE SAN CARLOS - CORREGIMIENTO DE SAN CARLOS
PANAMÁ

SOCIEDAD PROMOTORA

Inversiones Decuria, S.A.

Representante legal: IGOR CORTES
Número de cédula o pasaporte: 8C054493

INGENIERÍA MUNICIPAL

PLANO

- DETALLE B DE APARTAMENTOS
TORRE C - NIVEL-400
ESCALA 1:50

ARCHIVO .DWG	NIVEL-400
FECHA	30/08/2010
FECHA MODIFICACIÓN	DD/MM/AAAA

ARQUITECTURA | HOJA: 6 | DE: 65

DETALLE A

DETALLE B

DETALLE A

DETALLE B

ESTACIONAMIENTOS Y PLANTA ARQUITECTONICA NIVEL -200@-300

AR

ESCALA: 1:100

INGENIERIA MUNICIPAL
DISTRITO DE SAN CARLOS
APROBADO
Nº 11.11
INGENIERO MUNICIPAL
FECHA 22/8/11

Cuerpo de Bomberos
OFICINA PREVENCIÓN DE RIESGOS
La Chorrera, 11 de agosto de 2011
Resolución No. 346 -DNPR-CBLCH
Se aprueba el registro de la presente obra, quedando por fijar las condiciones requeridas.
Jefe de la Oficina de Seguridad

FELIPE GONZALEZ LINCK
ARQUITECTO
IDONEIDAD No. 7771-89
LEY 15 DEL 26 DE ENERO DE 1959
JUNTA TECNICA DE INGENIERIA Y ARQUITECTURA

FELIFE GONZÁLEZ LINCK
ARQUITECTO
Tel. -- 66771610 -- Fax 392-2457 | 64035830

DISEÑO ARQUITECTÓNICO	Arq. Vicente Cortes Arq. Igor Cortes
DESARROLLO	Arq. Igor Cortes Arq. Ilem Segismond Arq. Nancy Urriola
PROYECTO ESTRUCTURAL	Ing. Ricauter Bowen
PROYECTO ELÉCTRICO	Ing. Edgar Naranjo
PROYECTO DE PLOMERÍA	Ing. Gilberto Ayala

PROYECTO

Residencial El Palmar

UBICACIÓN

COMUNIDAD DE 'EL PALMAR'
DTTO. DE SAN CARLOS - CORREGIMIENTO DE SAN CARLOS
PANAMÁ

SOCIEDAD PROMOTORA

Inversiones Decuria, S.A.

Representante legal: IGOR CORTES
Número de cédula o pasaporte: 8C054493

INGENIERÍA MUNICIPAL

PLANO

- PLANTA ARQUITECTONICA
NIVEL-200 @ -300
ESCALA 1:100

ARCHIVO .DWG	NIVEL-200@-300
FECHA	30/08/2010
FECHA MODIFICACIÓN	DD/MM/AAAA

ARQUITECTURA | HOJA: 7 | DE: 65

NIVEL - 150
COTA 23.09

NIVEL - 100
COTA 24.46

NIVEL - 100
COTA 24.59

RECAMARA #3
COCINA
VESTIBULO
S.S. #F1
S.S. #G1
S.S. # E1
S.S. # E2
RECAMARA #1
RECAMARA #2
SALA/ COMEDOR
BALCON

AR ESTACIONAMIENTO Y PLANTA ARQUITECTONICA NIVEL -100

ESCALA: 1:100

INGENIERIA MUNICIPAL
DISTRITO DE SAN CARLOS
APROBADO
INGENIERO MUNICIPAL
FECHA: 22/9/11

Cuerpo de Bomberos
OFICINA DE SEGURIDAD
La Chorrera, 11 de Agosto de 2011
Resolución No. 349 de 2011
Se aprueba el registro de este plano por llenar las condiciones requeridas.
Jefe de la Oficina de Seguridad

FELIPE GONZALEZ LINCK
ARQUITECTO
IDONEIDAD No. 7711-2000
LEY 15 DE 26 DE ENERO DE 1959
JUNTA TECNICA DE INGENIERIA Y ARQUITECTURA

FELIFE GONZÁLEZ LINCK
ARQUITECTO
Tel. – 66771610 – Fax 392-2457 | 64035839

DISEÑO ARQUITECTÓNICO	Arq. Vicente Cortes Arq. Igor Cortes
DESARROLLO	Arq. Igor Cortes Arq. Ilem Segismond Arq. Nancy Urriola
PROYECTO ESTRUCTURAL	Ing. Ricauter Bowen
PROYECTO ELÉCTRICO	Ing. Edgar Naranjo
PROYECTO DE PLOMERÍA	Ing. Gilberto Ayala

PROYECTO

Residencial El Palmar

UBICACIÓN

COMUNIDAD DE 'EL PALMAR'
DTTO. DE SAN CARLOS - CORREGIMIENTO DE SAN CARLOS
PANAMÁ

SOCIEDAD PROMOTORA

Inversiones Decuria, S.A.

Representante legal: IGOR CORTES
Número de cédula o pasaporte: 8-054-493

INGENIERÍA MUNICIPAL

PLANO

- PLANTA ARQUITECTONICA NIVEL-100
ESCALA 1:100

ARCHIVO .DWG	NIVEL-100
FECHA	30/08/2010
FECHA MODIFICACIÓN	DD/MM/AAAA

ARQUITECTURA | HOJA: 8 | DE: 65

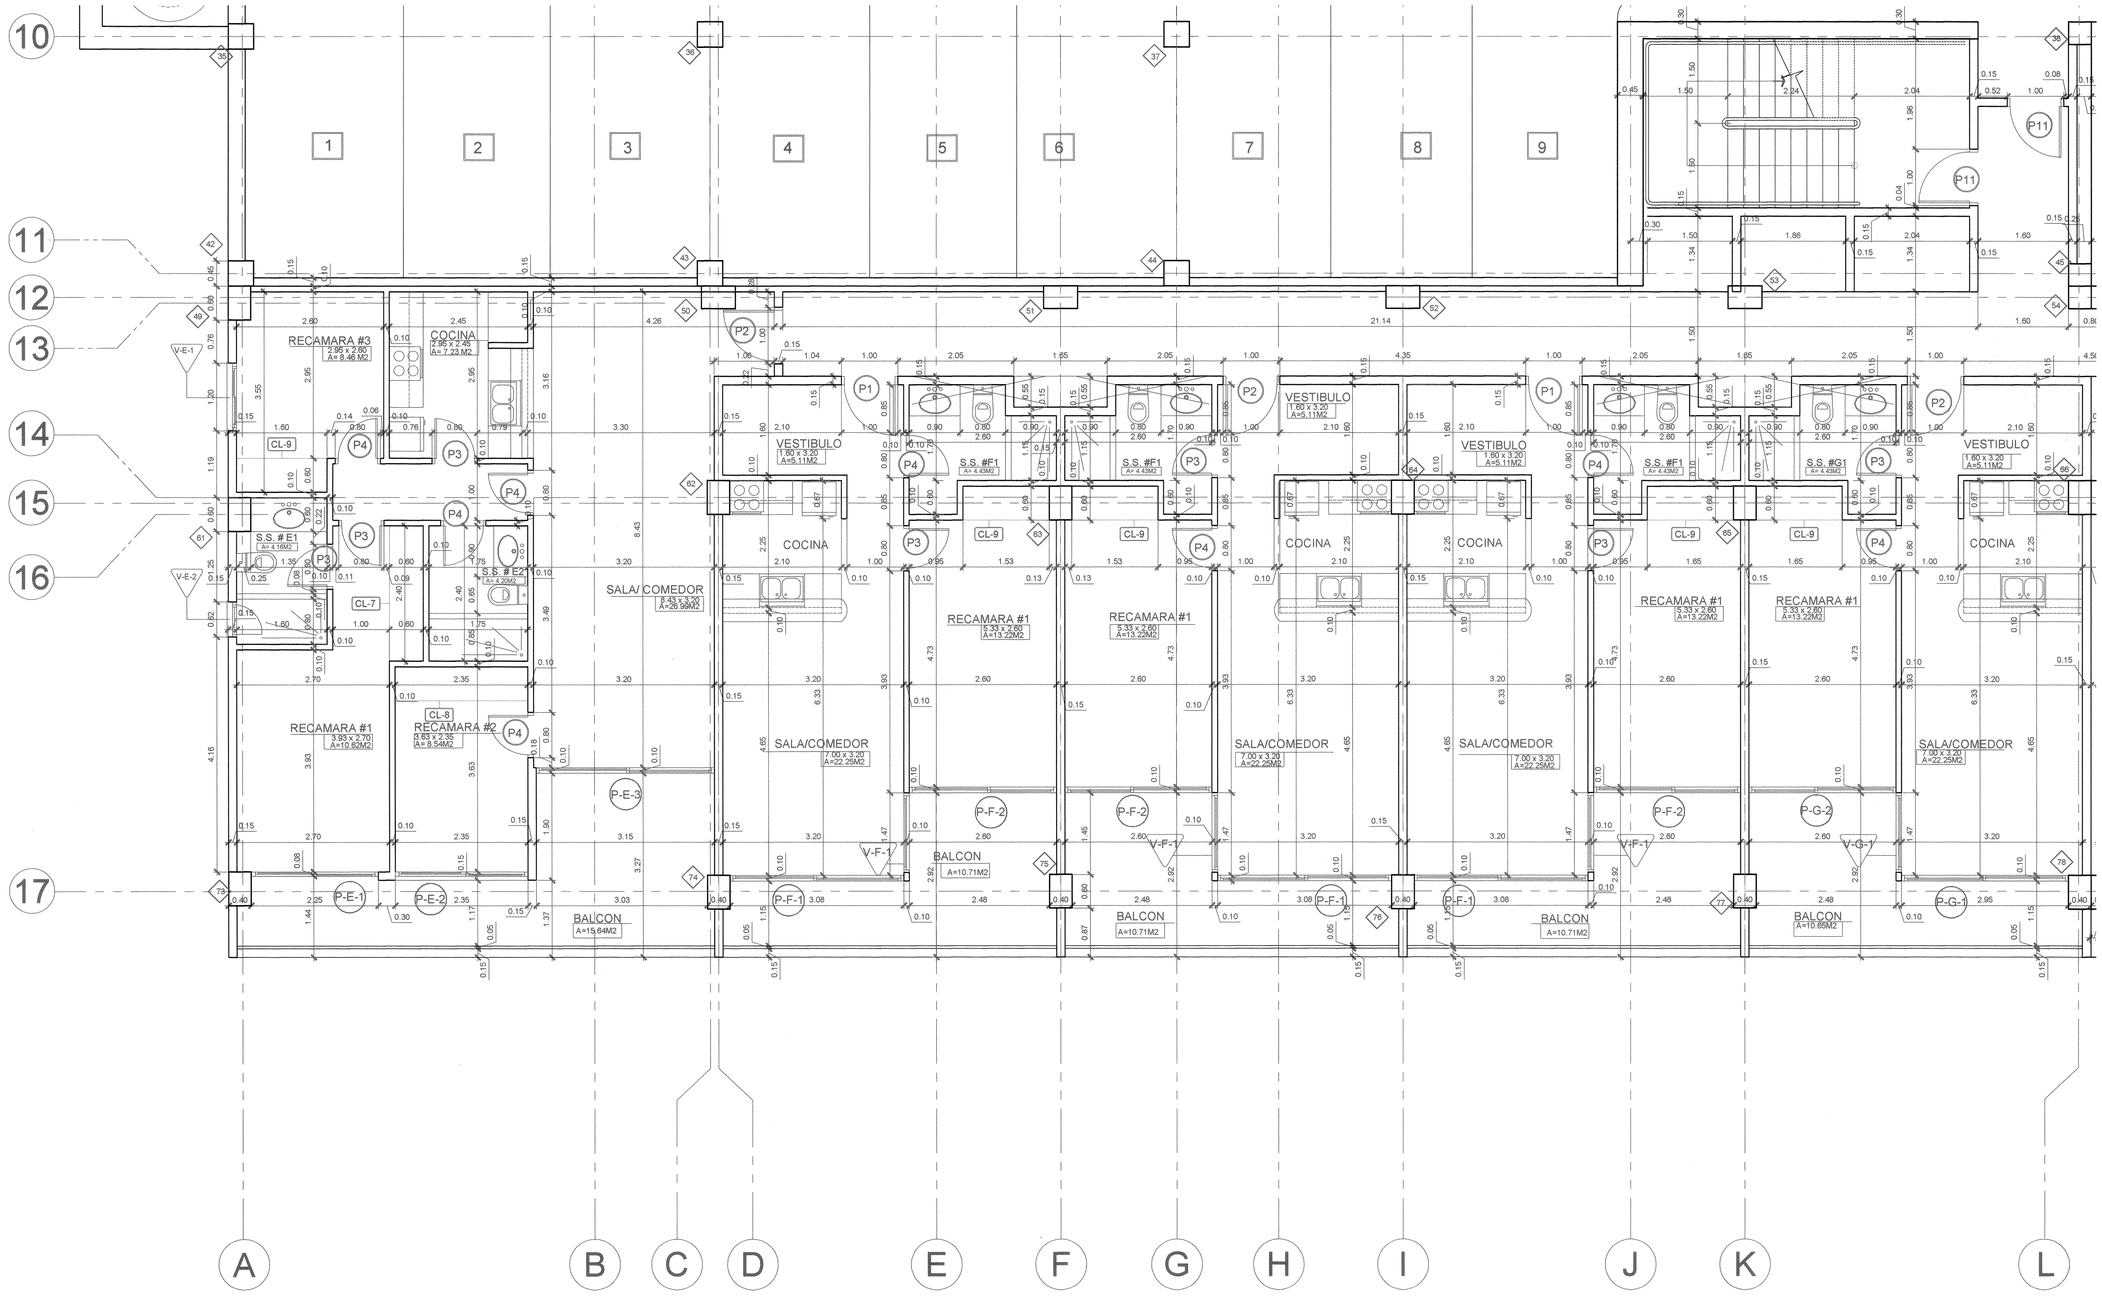

AR DETALLE A DE APARTAMENTOS TORRE C NIVELES -100@-300

ESCALA: 1:50

INGENIERIA MUNICIPAL
DISTRITO DE SAN CARLOS
APROBADO
FECHA 22/8/11
INGENIERO MUNICIPAL

Cuerpo de Bomberos
OFICINA DE SEGURIDAD
La Chorrera
Resolución No. ... de ... de 2011
Se aprueba el registro de ... para llenar las condiciones requeridas
Jefe de la Oficina de Seguridad

FELIPE GONZALEZ LINCK
ARQUITECTO
LICENCIA No. 87-1-143
LEY 15 DEL 26 DE ENERO DE 1959
JUNTA TECNICA DE INGENIERIA Y ARQUITECTURA

FELIFE GONZÁLEZ LINCK
ARQUITECTO
Tel. -- 66771610 -- Fax 392-2457 | 64035839

DISEÑO ARQUITECTÓNICO	Arq. Vicente Cortes Arq. Igor Cortes
DESARROLLO	Arq. Igor Cortes Arq. Ilem Segismond Arq. Nancy Urriola
PROYECTO ESTRUCTURAL	Ing. Ricauter Bowen
PROYECTO ELÉCTRICO	Ing. Edgar Naranjo
PROYECTO DE PLOMERÍA	Ing. Gilberto Ayala

PROYECTO

Residencial El Palmar

UBICACIÓN

COMUNIDAD DE "EL PALMAR"
DTTO. DE SAN CARLOS - CORREGIMIENTO DE SAN CARLOS
PANAMÁ

SOCIEDAD PROMOTORA

Inversiones Decuria, S.A.

Representante legal: IGOR CORTES
Número de cédula o pasaporte: 8CO54493

INGENIERÍA MUNICIPAL

PLANO

- DETALLE A DE APARTAMENTOS
TORRE C NIVEL-100@-300
ESCALA 1:50

ARCHIVO .DWG	NIVEL-200@-300
FECHA	30/08/2010
FECHA MODIFICACIÓN	DD/MM/AAAA

ARQUITECTURA	HOJA: 9	DE: 65

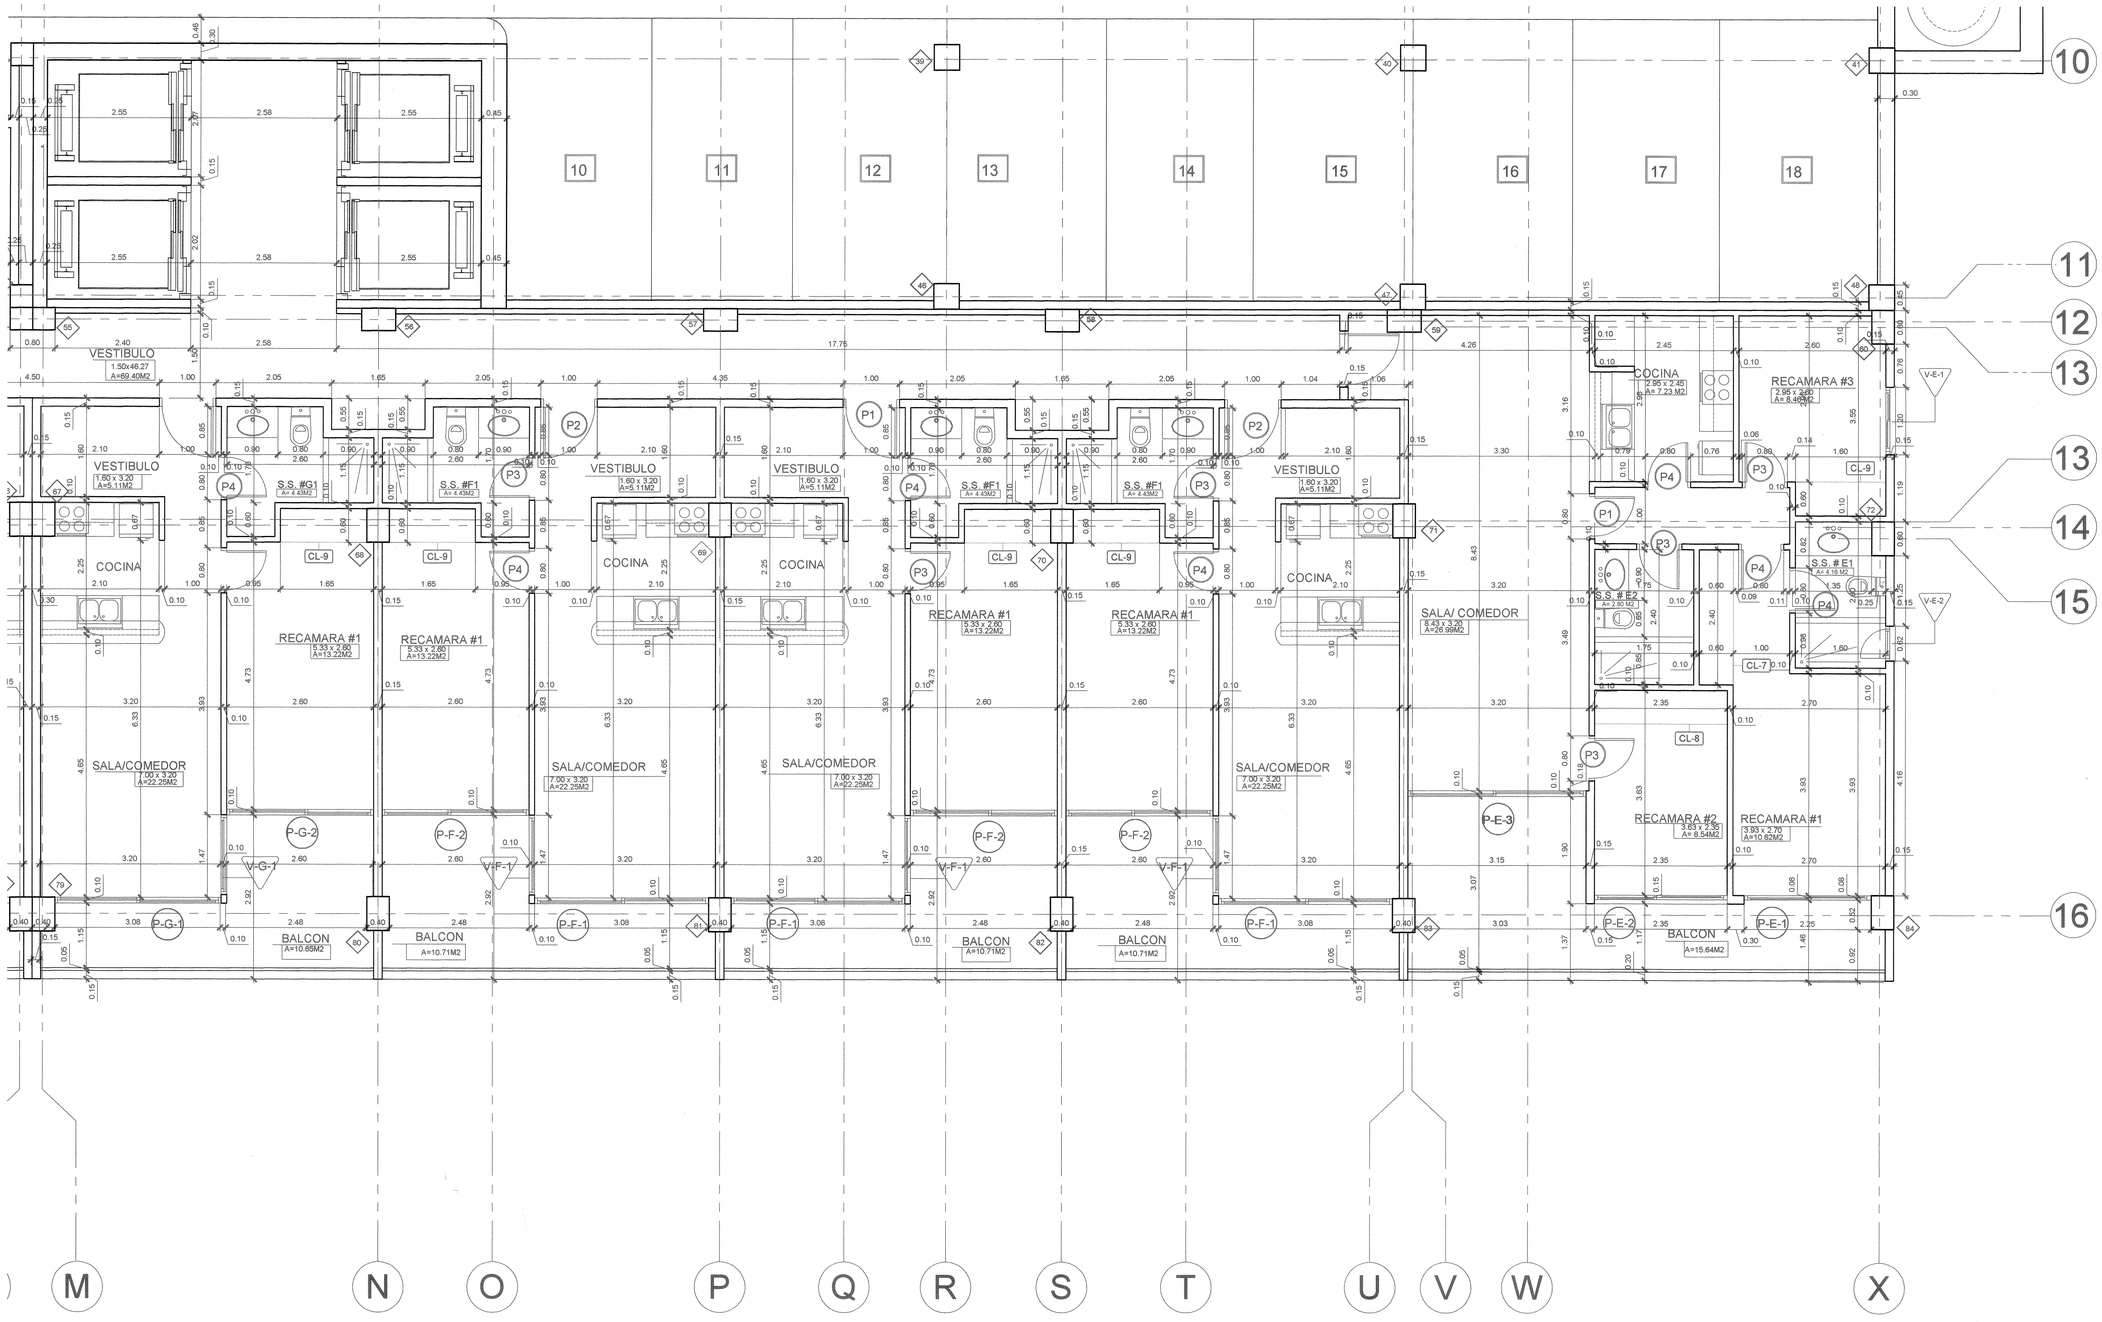

AR DETALLE B DE APARTAMENTOS TORRE C NIVELES -100@-300

ESCALA: 1:50

INGENIERIA MUNICIPAL
DISTRITO DE SAN CARLOS
APROBADO
FECHA 22/8/11
INGENIERO MUNICIPAL

Cuerpo de Bomberos
OFICINA DE SEGURIDAD
Fecha 22/8/11
Resolución No. 316
Se aprueba el reparo de este plano por llenar las condiciones requeridas.
Jefe de la Oficina de Seguridad

FELIPE GONZALEZ LINCK
ARQUITECTO
LICENCIA No. 7771-188
LEY 15 DEL 26 DE ENERO DE 1959
JUNTA TECNICA DE INGENIERIA Y ARQUITECTURA

FELIFE GONZÁLEZ LINCK
ARQUITECTO
Tel. -- 66771610 -- Fax 392-2457 | 64205839

DISEÑO ARQUITECTÓNICO	Arq. Vicente Cortes Arq. Igor Cortes
DESARROLLO	Arq. Igor Cortes Arq. Ilem Segismond Arq. Nancy Urriola
PROYECTO ESTRUCTURAL	Ing. Ricauter Bowen
PROYECTO ELÉCTRICO	Ing. Edgar Naranjo
PROYECTO DE PLOMERÍA	Ing. Gilberto Ayala

PROYECTO

Residencial El Palmar

UBICACIÓN

COMUNIDAD DE 'EL PALMAR'
DTTO. DE SAN CARLOS - CORREGIMIENTO DE SAN CARLOS
PANAMÁ

SOCIEDAD PROMOTORA

Inversiones Decuria, S.A.

Representante legal: IGOR CORTES
Número de cédula o pasaporte: 8C054493

INGENIERÍA MUNICIPAL

PLANO

- DETALLE B DE APARTAMENTOS
TORRE C NIVEL -100 @ -300
ESCALA 1:50

ARCHIVO .DWG	NIVEL-200@-300
FECHA	30/08/2010
FECHA MODIFICACIÓN	DD/MM/AAAA

ARQUITECTURA | HOJA: 10 | DE: 65

DETALLE A

DETALLE B

RETIRO 5m.

ESTACION DE MEDIDORES ELEC.

ESTACION DE TRANSFORMADORES

RAMPA INTERIOR DE ESTACIONAMIENTO

SALA DE FIESTAS
8.50 x 11.95
A=101.57M2

LOCAL COMERCIAL #1
5.70 x 8.08
A=34.63M2

DEPOSITO #1
3.25 x 1.90
A=6.11M2

NIVEL 000
COTA 27.34

LOBBY Y ACCESOS
A=246.07M2

S.S. # 4
2.30 X 2.25
A=10.35M2

DEPOSITO #5
2.60 x 2.75
A=14.77M2

S.S. # 3

DEPOSITO #2

AREA INFANTIL
7.03 x 8.10
A=42.69M2

AREA SOCIAL EXTERIOR

SALA DE AUDIOVISUALES
6.83 x 6.10
A=41.68M2

DEPOSITO #3
2.41 x 2.50
A=6.03M2

DEPOSITO #4
2.41 x 3.73
A=9.05M2

CANCHA DE SQUACH
11.45 x 6.40
A=73.24M2

S.S. # 5
2.30 x 5.25
A=10.99M2

BAÑOS SPA

AREA DE AGUAS-HOMBRES
10.74 x 6.16
A=66.18M2

AREA DE AGUAS-MUJERES
10.74 x 6.16
A=66.18M2

GIMNASIO
5.90 x 10.74
A=63.34M2

LOCAL COMERCIAL #2
6.23 x 5.81
A=36.18M2

S.S. # 2
A=4.57M2

RECAMARA#2
A=5.82M2

COCINA

S.S. # 1

SALA/ COMEDOR

RECAMARA #1

AREA SOCIAL EXTERIOR

AREA SOCIAL EXTERIOR

AREA SOCIAL EXTERIOR

AREA SOCIAL EXTERIOR

65.32

65.90

AR PLANTA ARQUITECTONICA NIVEL 000

ESCALA 1/100

INGENIERÍA MUNICIPAL
DISTRITO DE SAN CARLOS
APROBADO
INGENIERO MUNICIPAL
FECHA 22/8/11

Cuerpo de Bomberos
OFICINA DE SEGURIDAD
La Chorrera

La Chorrera, 11 de agosto de 2011
Resolución No. 276 Plano No. 16-45
Se aprueba el registro de este plano por llenar las condiciones requerida

Jefe de la Oficina de Seguridad

FELIPE GONZALEZ LINCK
ARQUITECTO
IDONEIDAD No. 1778-98
LEY 15 DEL 26 DE ENERO DE 1959
JUNTA TECNICA DE INGENIERIA Y ARQUITECTURA

FELIPE GONZÁLEZ LINCK
ARQUITECTO
Tel. – 66771610 – Fax 382-2457 | 64035839

DISEÑO ARQUITECTÓNICO	Arq. Vicente Cortes Arq. Igor Cortes
DESARROLLO	Arq. Igor Cortes Arq. Ilem Segismond Arq. Nancy Urriola
PROYECTO ESTRUCTURAL	Ing. Ricauter Bowen
PROYECTO ELÉCTRICO	Ing. Edgar Naranjo
PROYECTO DE PLOMERÍA	Ing. Gilberto Ayala

PROYECTO

Residencial El Palmar

UBICACIÓN

COMUNIDAD DE "EL PALMAR"
DTTO. DE SAN CARLOS - CORREGIMIENTO DE SAN CARLOS PANAMÁ

SOCIEDAD PROMOTORA

Inversiones Decuria, S.A.

Representante legal: IGOR CORTES
Número de cédula o pasaporte: 8C054493

INGENIERÍA MUNICIPAL

PLANO

- PLANTA ARQUITECTONICA NIVEL 00
ESCALA 1:100

ARCHIVO .DWG	NIVEL 000
FECHA	30/08/2010
FECHA MODIFICACIÓN	DD/MM/AAAA

ARQUITECTURA | HOJA: 12 | DE: 65

AR PLANTA ARQUITECTONICA COMPLETA NIVEL 000

ESCALA: 1:200

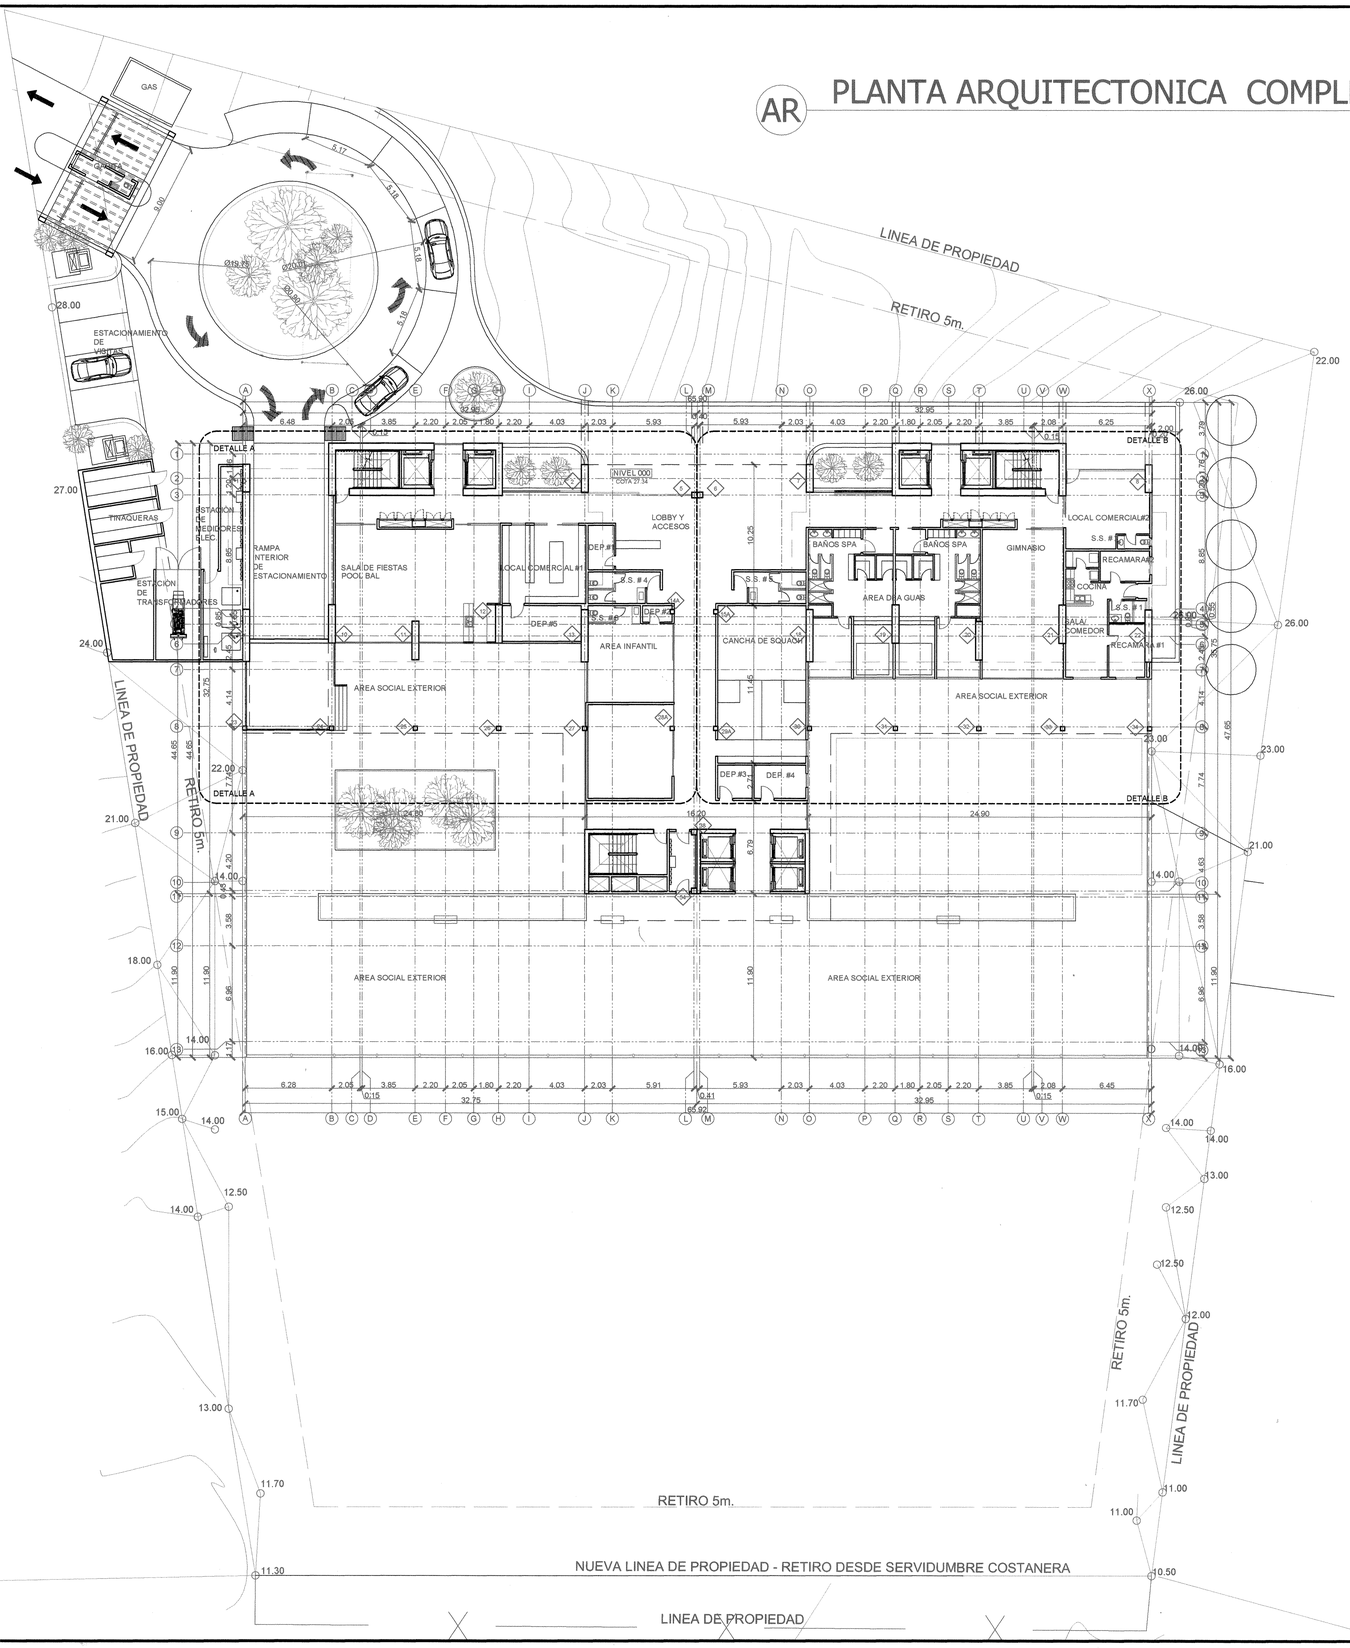

INGENIERIA MUNICIPAL
DISTRITO DE SAN CARLOS
APROBADO
Fecha 22/8/11
INGENIERO MUNICIPAL
FECHA 22/8/11

Cuerpo de Bomberos
OFICINA DE SEGURIDAD (NIVEL)
La Chorrera

La Chorrera, 11 de agosto de 2011
Resolución No. 216 Plano No. 11
Se aprueba el registro de este plano por llenar las condiciones requeridas.

Jefe de la Oficina de Seguridad

FELIPE GONZALEZ LINEK
ARQUITECTO
LICENCIA No. 77-1103
LEY 15 DEL 26 DE MAYO DE 1959
JUNTA TECNICA DE INGENIERIA Y ARQUITECTURA

FELIFE GONZÁLEZ LINCK
ARQUITECTO
Tel. – 66771610 – Fax 392-2457 | 64035839

DISEÑO ARQUITECTÓNICO	Arq. Vicente Cortes Arq. Igor Cortes
DESARROLLO	Arq. Igor Cortes Arq. Ilem Segismond Arq. Nancy Urriola
PROYECTO ESTRUCTURAL	Ing. Ricauter Bowen
PROYECTO ELÉCTRICO	Ing. Edgar Naranjo
PROYECTO DE PLOMERÍA	Ing. Gilberto Ayala

PROYECTO

Residencial El Palmar

UBICACIÓN

COMUNIDAD DE 'EL PALMAR'
DTTO. DE SAN CARLOS - CORREGIMIENTO DE SAN CARLOS
PANAMÁ

SOCIEDAD PROMOTORA

Inversiones Decuria, S.A.

Representante legal: IGOR CORTES
Número de cédula o pasaporte: BC054493

INGENIERÍA MUNICIPAL

PLANO

- PLANTA GENERAL NIVEL 000
ESCALA 1:200

ARCHIVO .DWG	NIVEL 000
FECHA	30/08/2010
FECHA MODIFICACIÓN	DD/MM/AAAA

ARQUITECTURA	HOJA: 11	DE: 65

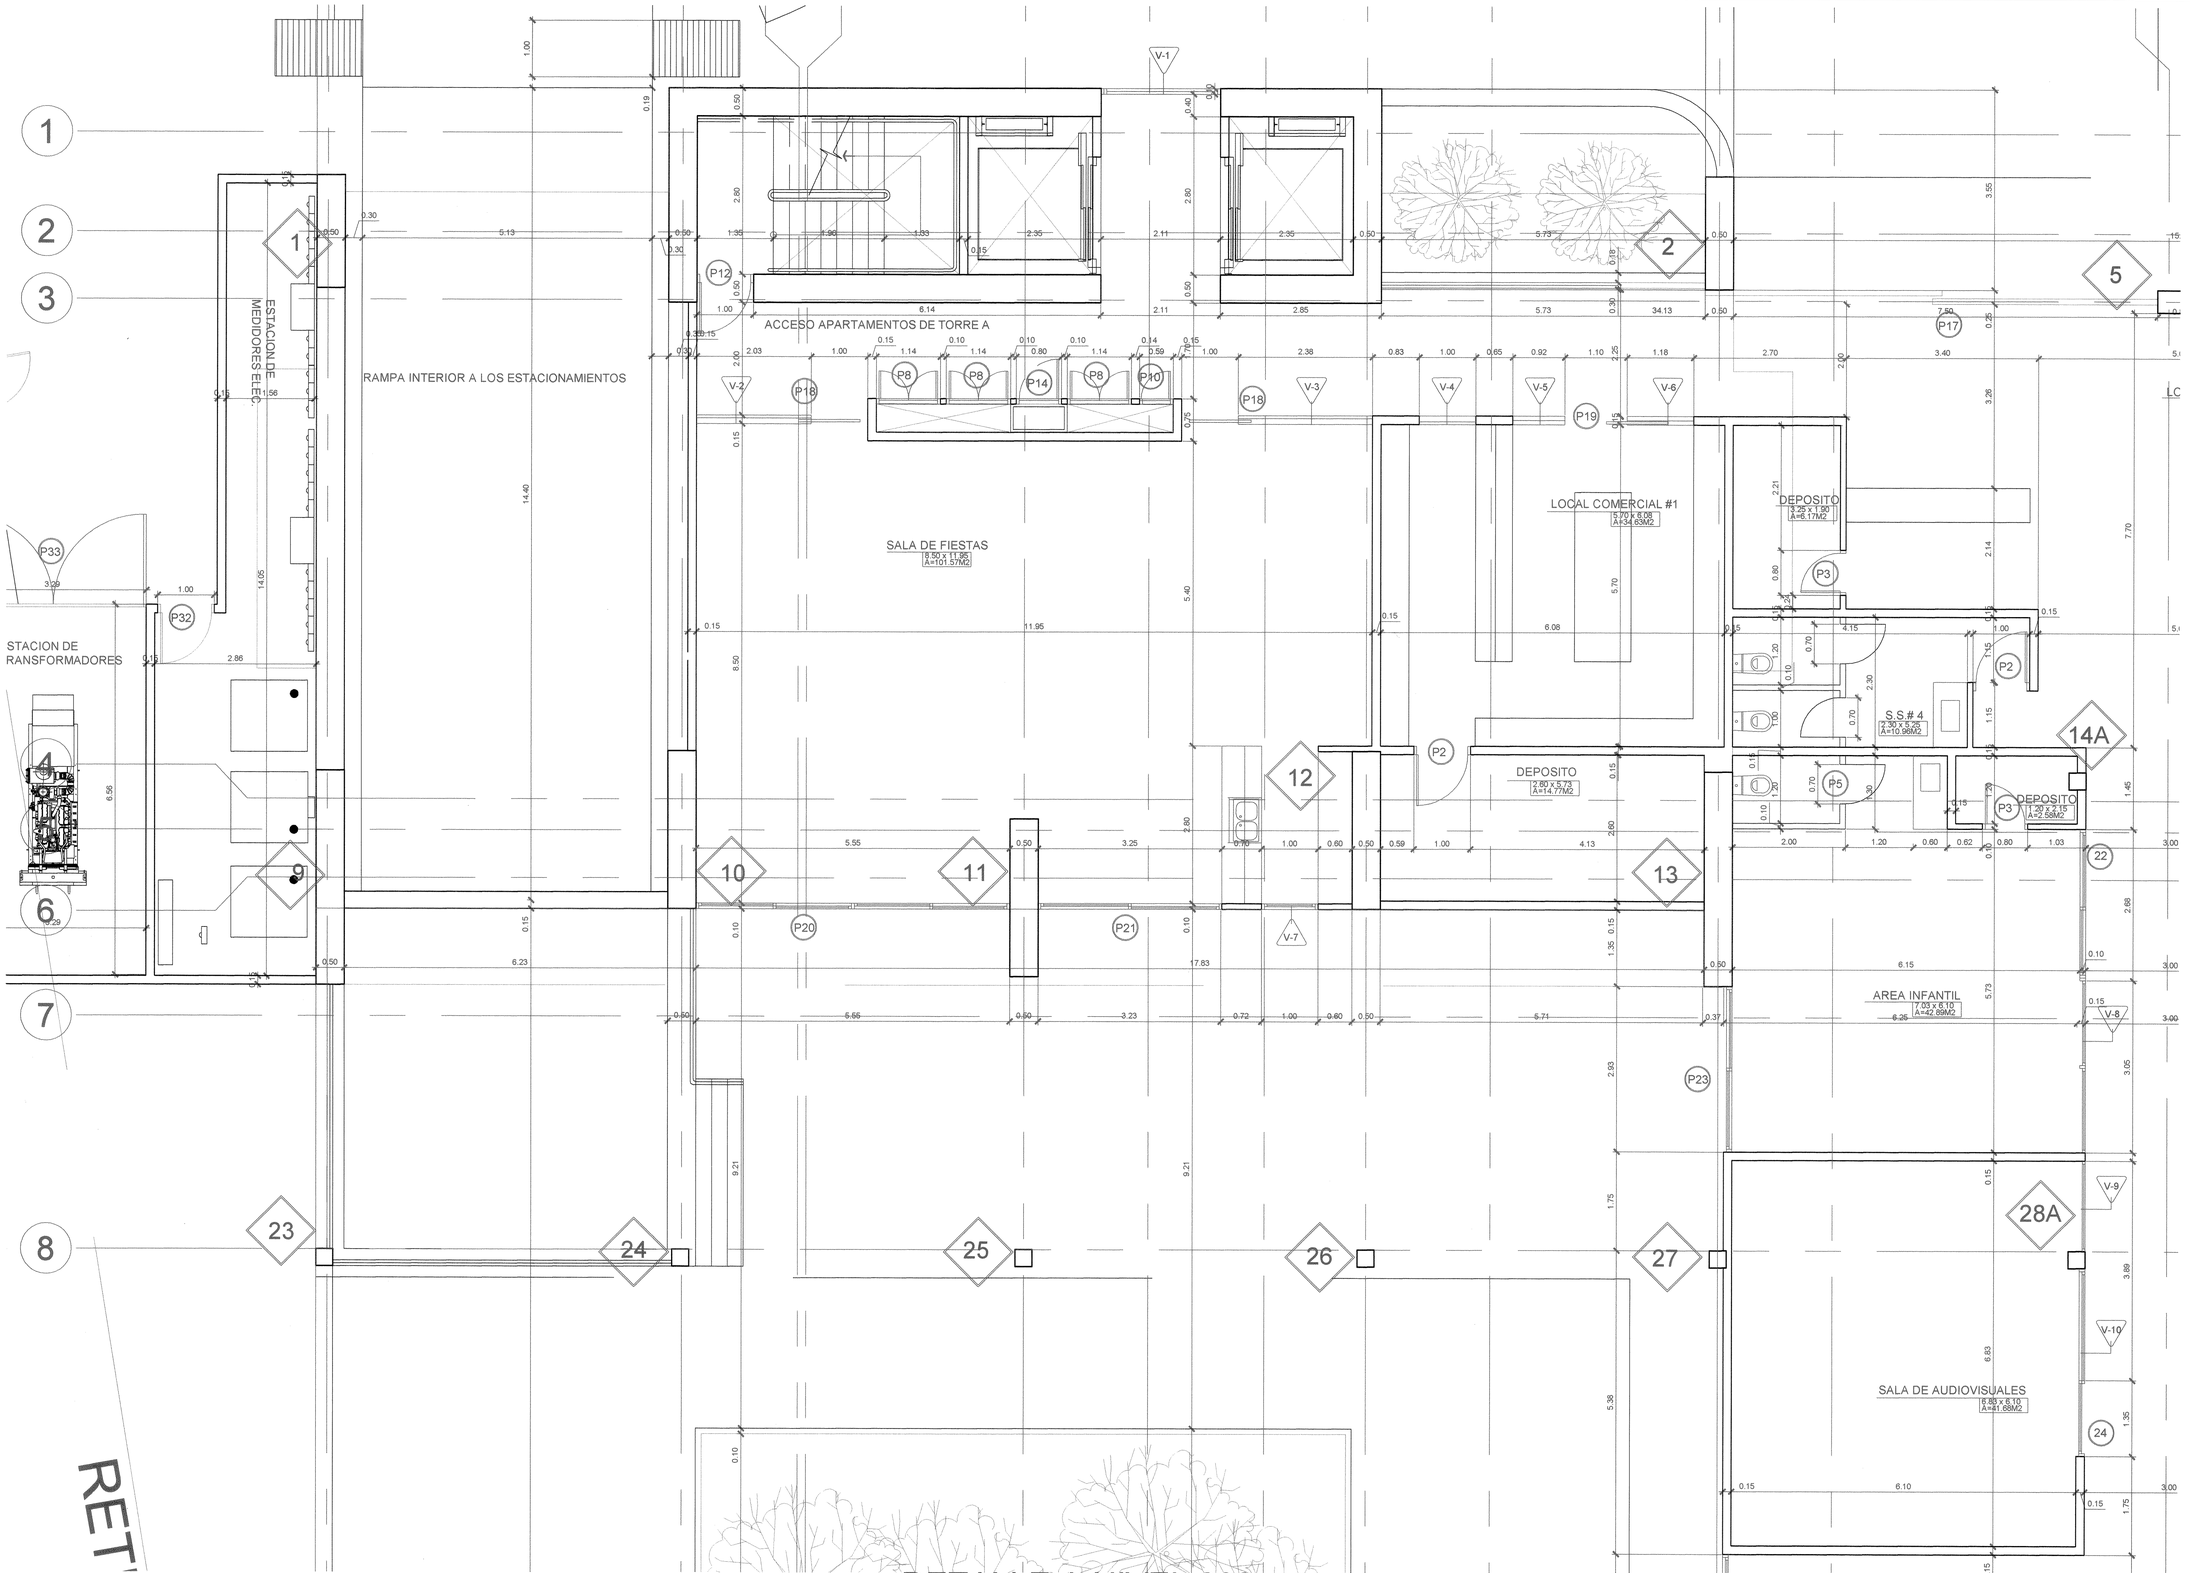

AR DETALLE A NIVEL 000

ESCALA 1/50

INGENIERIA MUNICIPAL
DISTRITO DE SAN CARLOS
APROBADO
INGENIERO MUNICIPAL
FECHA 22/8/11

Cuerpo de Bomberos
OFICINA DE SEGURIDAD(DAU)
La Chorrera

La Chorrera, 11 de agosto de 2011
Resolución No. 316-11 Planos No. 16-11
Se aprueba el registro de este plano por llenar las condiciones requeridas.

Jefe de la Oficina de Seguridad

FELIPE GONZALEZ LINCK
ARQUITECTO
IDONEIDAD No. 77-11198
LEY 15 DEL 26 DE ENERO DE 1959
JUNTA TECNICA DE INGENIERIA Y ARQUITECTURA

FELIFE GONZÁLEZ LINCK
ARQUITECTO
Tel. -- 66771610 -- Fax 392-2457 | 64035839

DISEÑO ARQUITECTÓNICO	Arq. Vicente Cortes Arq. Igor Cortes
DESARROLLO	Arq. Igor Cortes Arq. Ilem Segismond Arq. Nancy Urriola
PROYECTO ESTRUCTURAL	Ing. Ricauter Bowen
PROYECTO ELÉCTRICO	Ing. Edgar Naranjo
PROYECTO DE PLOMERÍA	Ing. Gilberto Ayala

PROYECTO

Residencial El Palmar

UBICACIÓN

COMUNIDAD DE 'EL PALMAR'
DTTO. DE SAN CARLOS - CORREGIMIENTO DE SAN CARLOS
PANAMÁ

SOCIEDAD PROMOTORA

Inversiones Decuria, S.A.

Representante legal: IGOR CORTES
Número de cédula o pasaporte: 8C054493

INGENIERÍA MUNICIPAL

PLANO

- DETALLE A NIVEL 00
ESCALARA 1:50

ARCHIVO .DWG	NIVEL 000
FECHA	30/08/2010
FECHA MODIFICACIÓN	DD/MM/AAAA

ARQUITECTURA | HOJA: 13 | DE: 65

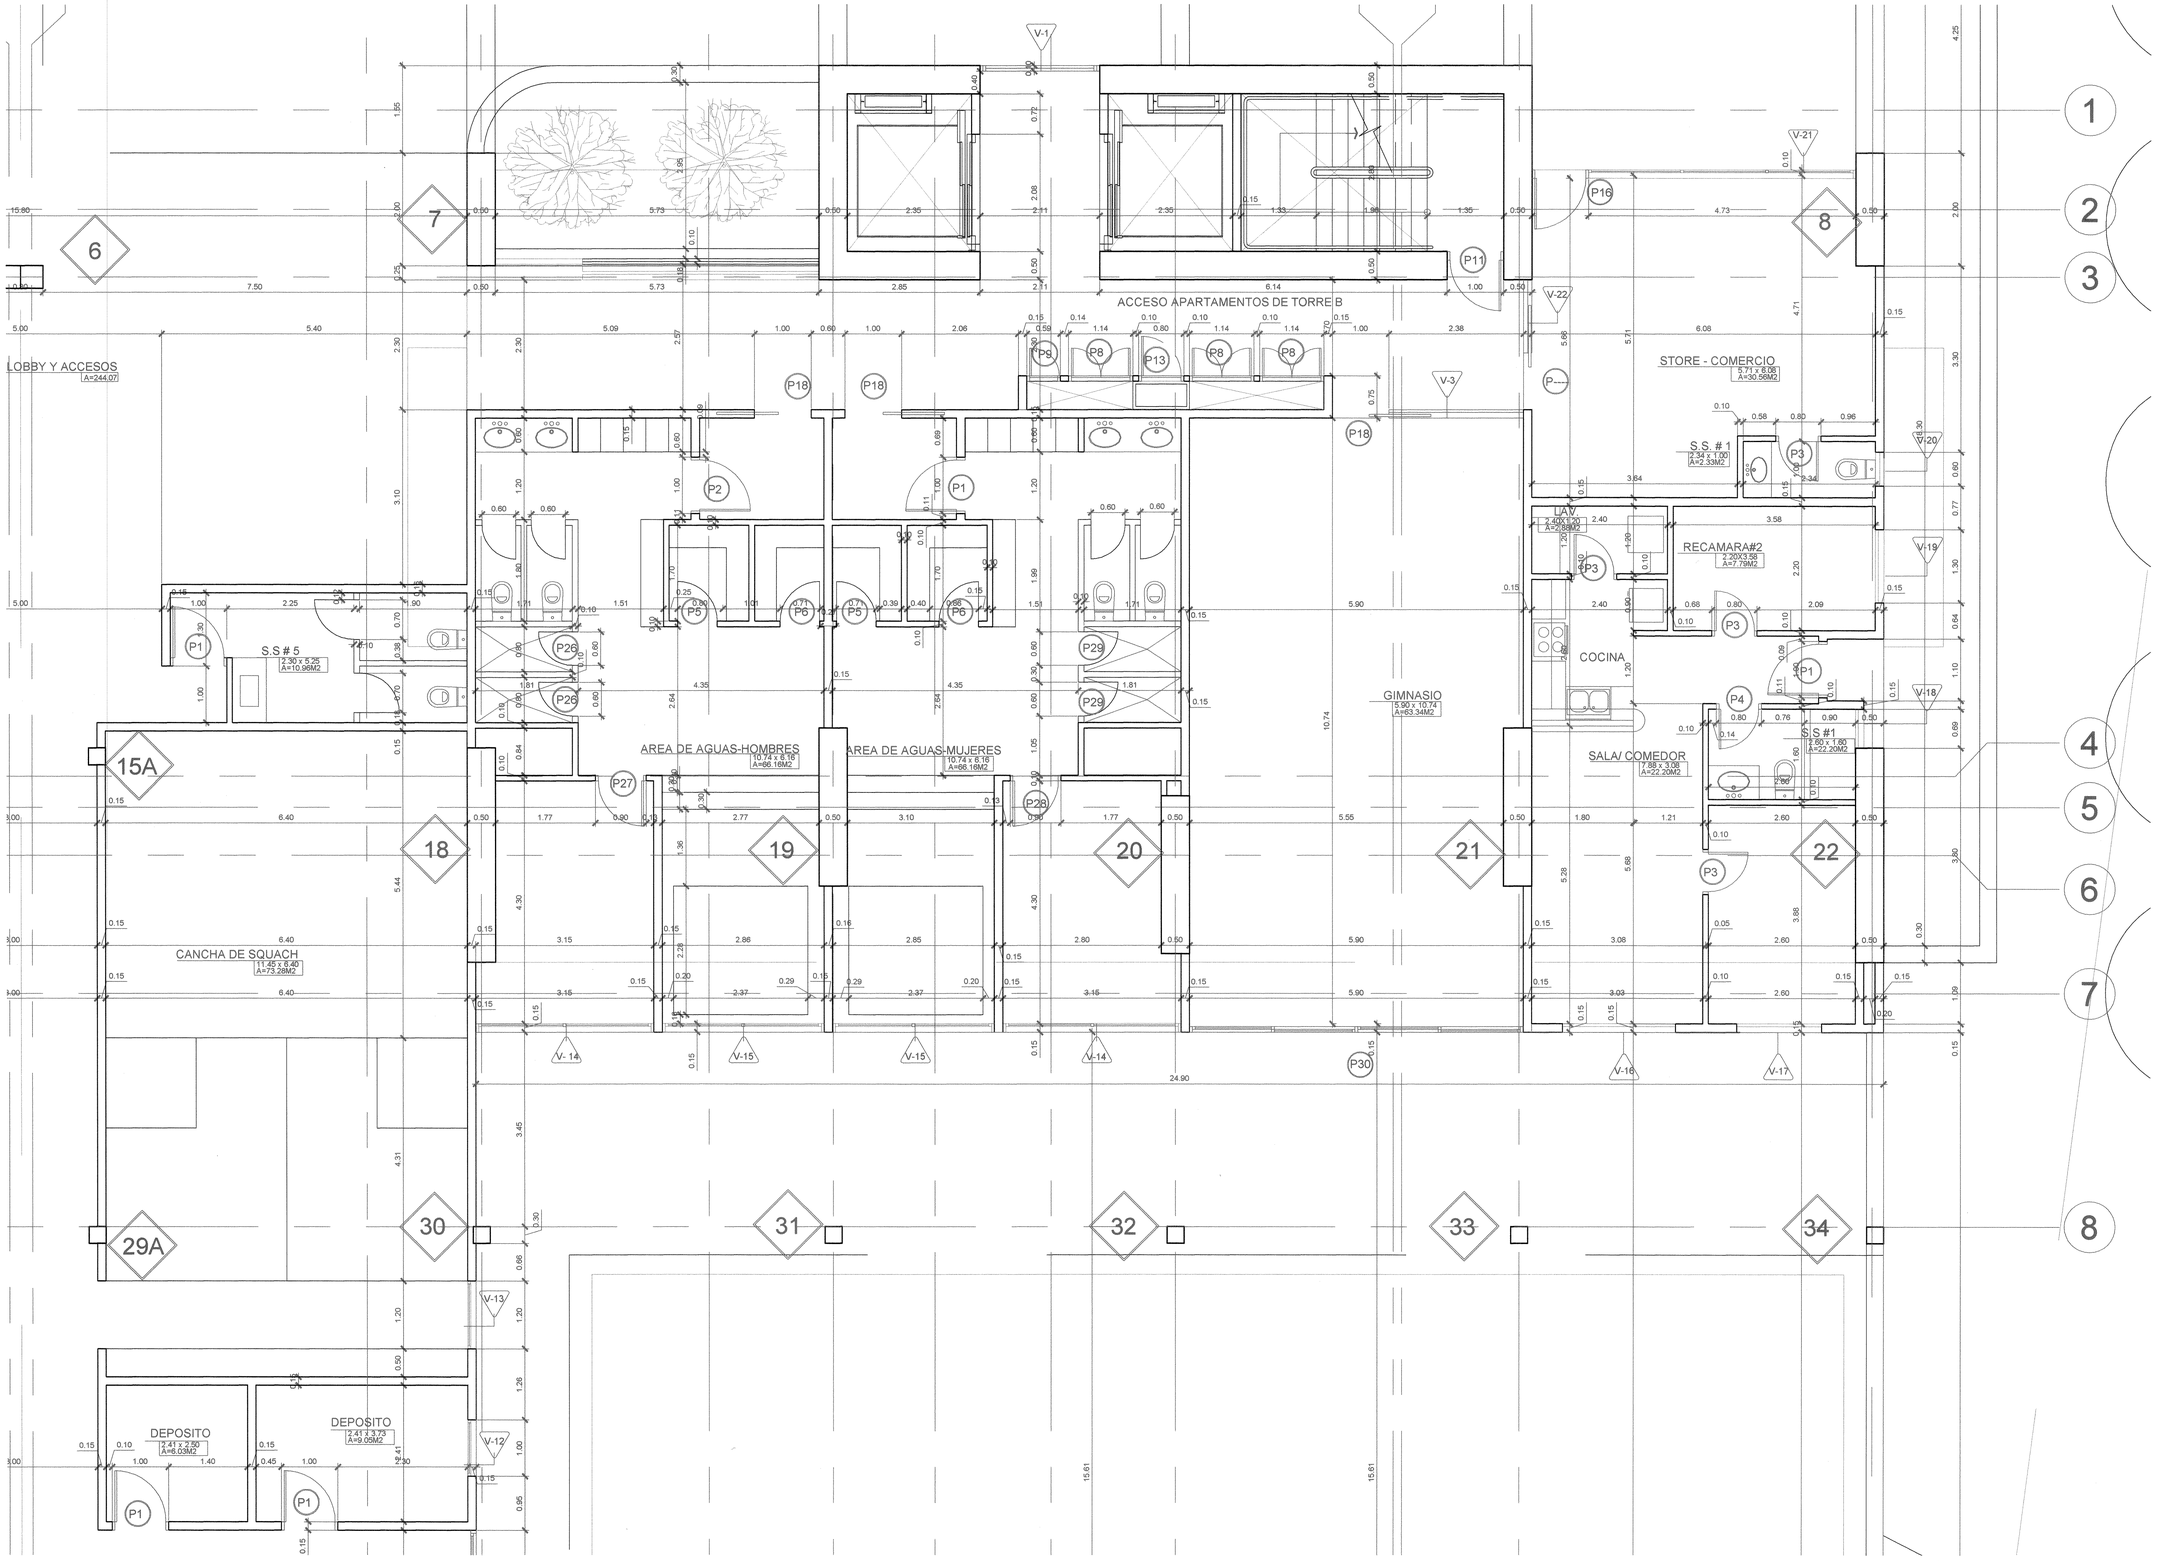

DETALLE B NIVEL 000

ESCALA 1/50

INGENIERIA MUNICIPAL
DISTRITO DE SAN CARLOS
APROBADO
INGENIERO MUNICIPAL
FECHA

Cuerpo de Bomberos
OFICINA DE SEGURIDAD
La Chorrera
La Chorrera, ... de 20..
Resolución No. .....
Se aprueba el registro de este plano por tener los condiciones requeridas
Jefe de la Oficina de Seguridad

FELIPE GONZALEZ LINCK
ARQUITECTO
IDONEIDAD No. 2001-105
LEY 15 DEL 26 DE ENERO DE 1959
JUNTA TECNICA DE INGENIERIA Y ARQUITECTURA

FELIFE GONZÁLEZ LINCK
ARQUITECTO
Tel. -- 66771610 – Fax 392-2457 | 64035839

DISEÑO ARQUITECTÓNICO	Arq. Vicente Cortes Arq. Igor Cortes
DESARROLLO	Arq. Igor Cortes Arq. Ilem Segismond Arq. Nancy Urriola
PROYECTO ESTRUCTURAL	Ing. Ricauter Bowen
PROYECTO ELÉCTRICO	Ing. Edgar Naranjo
PROYECTO DE PLOMERÍA	Ing. Gilberto Ayala

PROYECTO

Residencial El Palmar

UBICACIÓN

COMUNIDAD DE 'EL PALMAR'
DTTO. DE SAN CARLOS - CORREGIMIENTO DE SAN CARLOS
PANAMÁ

SOCIEDAD PROMOTORA

Inversiones Decuria, S.A.

Representante legal: IGOR CORTES
Número de cédula o pasaporte: 8C054493

INGENIERÍA MUNICIPAL

PLANO

- DETALLE B NIVEL 00
ESCALA 1:50

ARCHIVO .DWG	NIVEL 000
FECHA	30/08/2010
FECHA MODIFICACIÓN	DD/MM/AAAA

ARQUITECTURA | HOJA: 14 | DE: 65

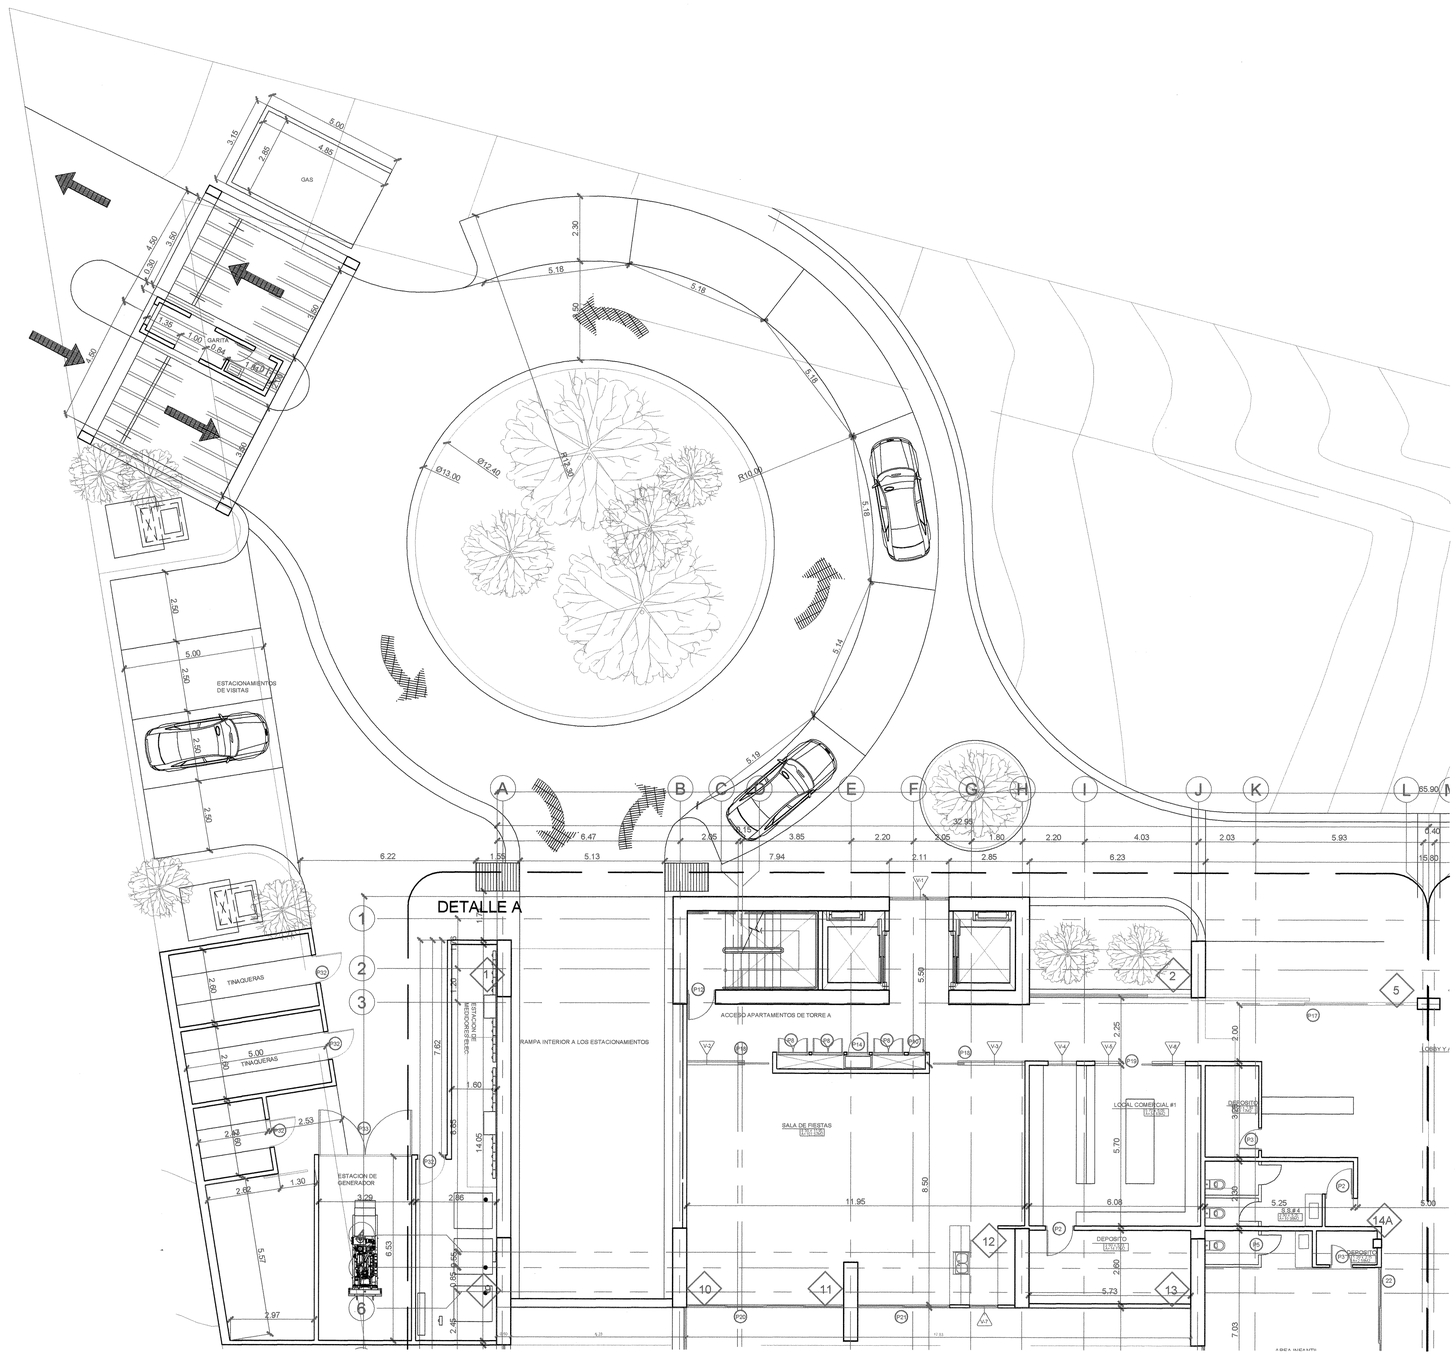

AR DETALLE C NIVEL 000

ESCALA 1/100

INGENIERIA MUNICIPAL
DISTRITO DE SAN CARLOS
APROBADO
INGENIERO MUNICIPAL
FECHA 22/8/11

Cuerpo de Bomb.
OFICINA DE SEGURIDAD
La Chorrera
La Chorrera, ... del 20...
Resolución No. ... Fecha No. ... de 20...
Se aprueba el presente plano, por llenar las condiciones requeridas.
Telf. de la Oficina de Seguridad

FELIPE GONZALEZ LINCK
ARQUITECTO
LICENCIA No. 87-1198
LEY 15 DEL 23 DE ENERO DE 1959
JUNTA TECNICA DE INGENIERIA Y ARQUITECTURA

FELIFE GONZÁLEZ LINCK
ARQUITECTO
Tel. -- 66771610 -- Fax 392-2457 | 64035839

DISEÑO ARQUITECTÓNICO	Arq. Vicente Cortes Arq. Igor Cortes
DESARROLLO	Arq. Igor Cortes Arq. Ilem Segismond Arq. Nancy Urriola
PROYECTO ESTRUCTURAL	Ing. Ricauter Bowen
PROYECTO ELÉCTRICO	Ing. Edgar Naranjo
PROYECTO DE PLOMERÍA	Ing. Gilberto Ayala

PROYECTO

Residencial El Palmar

UBICACIÓN

COMUNIDAD DE 'EL PALMAR'
DITTO. DE SAN CARLOS - CORREGIMIENTO DE SAN CARLOS
PANAMÁ

SOCIEDAD PROMOTORA

Inversiones Decuria, S.A.

Representante legal: IGOR CORTES
Número de cédula o pasaporte: 8C054493

INGENIERÍA MUNICIPAL

PLANO

- DETALLE C NIVEL 000
ESCALA 1:100

ARCHIVO .DWG	NIVEL 000
FECHA	30/08/2010
FECHA MODIFICACIÓN	DD/MM/AAAA

ARQUITECTURA | HOJA: 15 | DE: 65

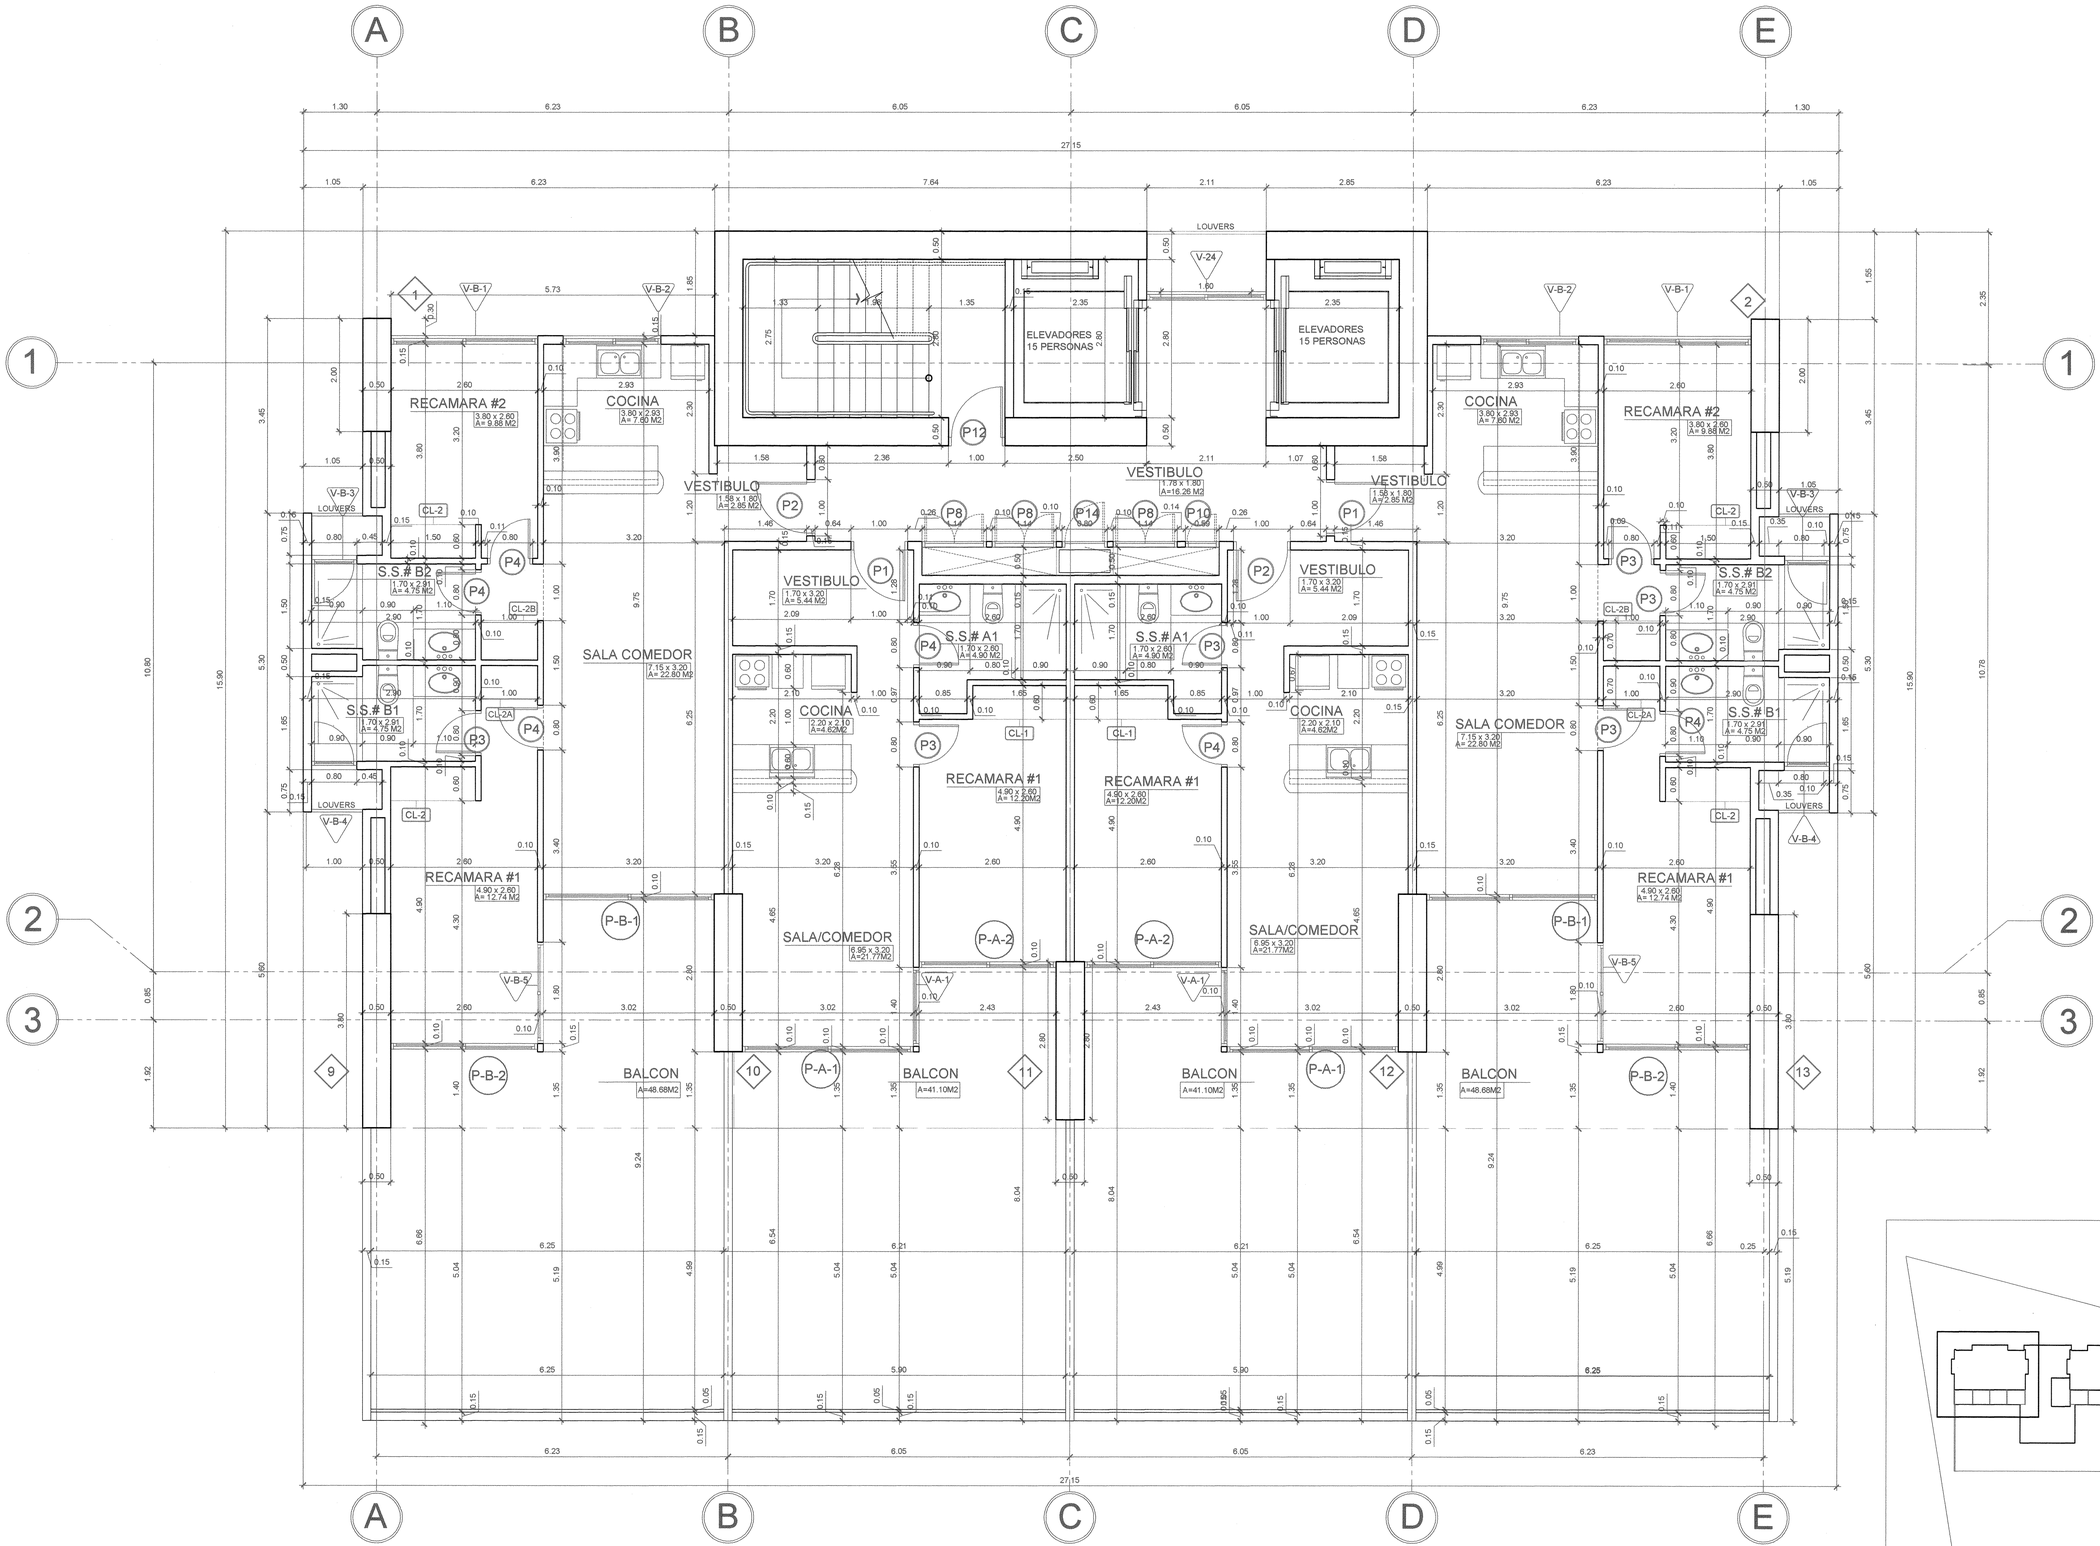

PLANTA ARQUITECTONICA TORRE A NIVEL + 100

AR

ESCALA: 1:50

INGENIERIA MUNICIPAL
DISTRITO DE SAN CARLOS
APROBADO
INGENIERO MUNICIPAL
FECHA 22/8/11

Cuerpo de Bomberos
OFICINA DE SEGURIDAD
La Chorrera, 11 de agosto de 2011
Resolución No. 23-11 Plano(s) aprobado(s) bajo las condiciones requeridas.

Jefe de la Oficina de Seguridad

FELIPE GONZALEZ LINCK
ARQUITECTO
LICENCIA No. 79-182
LEY 15 DEL 26 DE ENERO DE 1959
JUNTA TECNICA DE INGENIERIA Y ARQUITECTURA

FELIFE GONZÁLEZ LINCK
ARQUITECTO
Tel. -- 8677610 -- Fax 392-2457 | 64035839

DISEÑO ARQUITECTÓNICO	Arq. Vicente Cortes Arq. Igor Cortes
DESARROLLO	Arq. Igor Cortes Arq. Ilem Segismond Arq. Nancy Urriola
PROYECTO ESTRUCTURAL	Ing. Ricauter Bowen
PROYECTO ELÉCTRICO	Ing. Edgar Naranjo
PROYECTO DE PLOMERÍA	Ing. Gilberto Ayala

PROYECTO

Residencial El Palmar

UBICACIÓN

COMUNIDAD DE 'EL PALMAR'
DTTO. DE SAN CARLOS - CORREGIMIENTO DE SAN CARLOS
PANAMÁ

SOCIEDAD PROMOTORA

Inversiones Decuria, S.A.

Representante legal: IGOR CORTES
Número de cédula o pasaporte: BC054493

INGENIERÍA MUNICIPAL

PLANO

- PLANTA ARQUITECTONICA TORRE A
NIVEL 100
ESCALA 1:50

ARCHIVO .DWG	NIVEL+100
FECHA	30/08/2010
FECHA MODIFICACIÓN	DD/MM/AAAA

ARQUITECTURA | HOJA: 16 | DE: 65

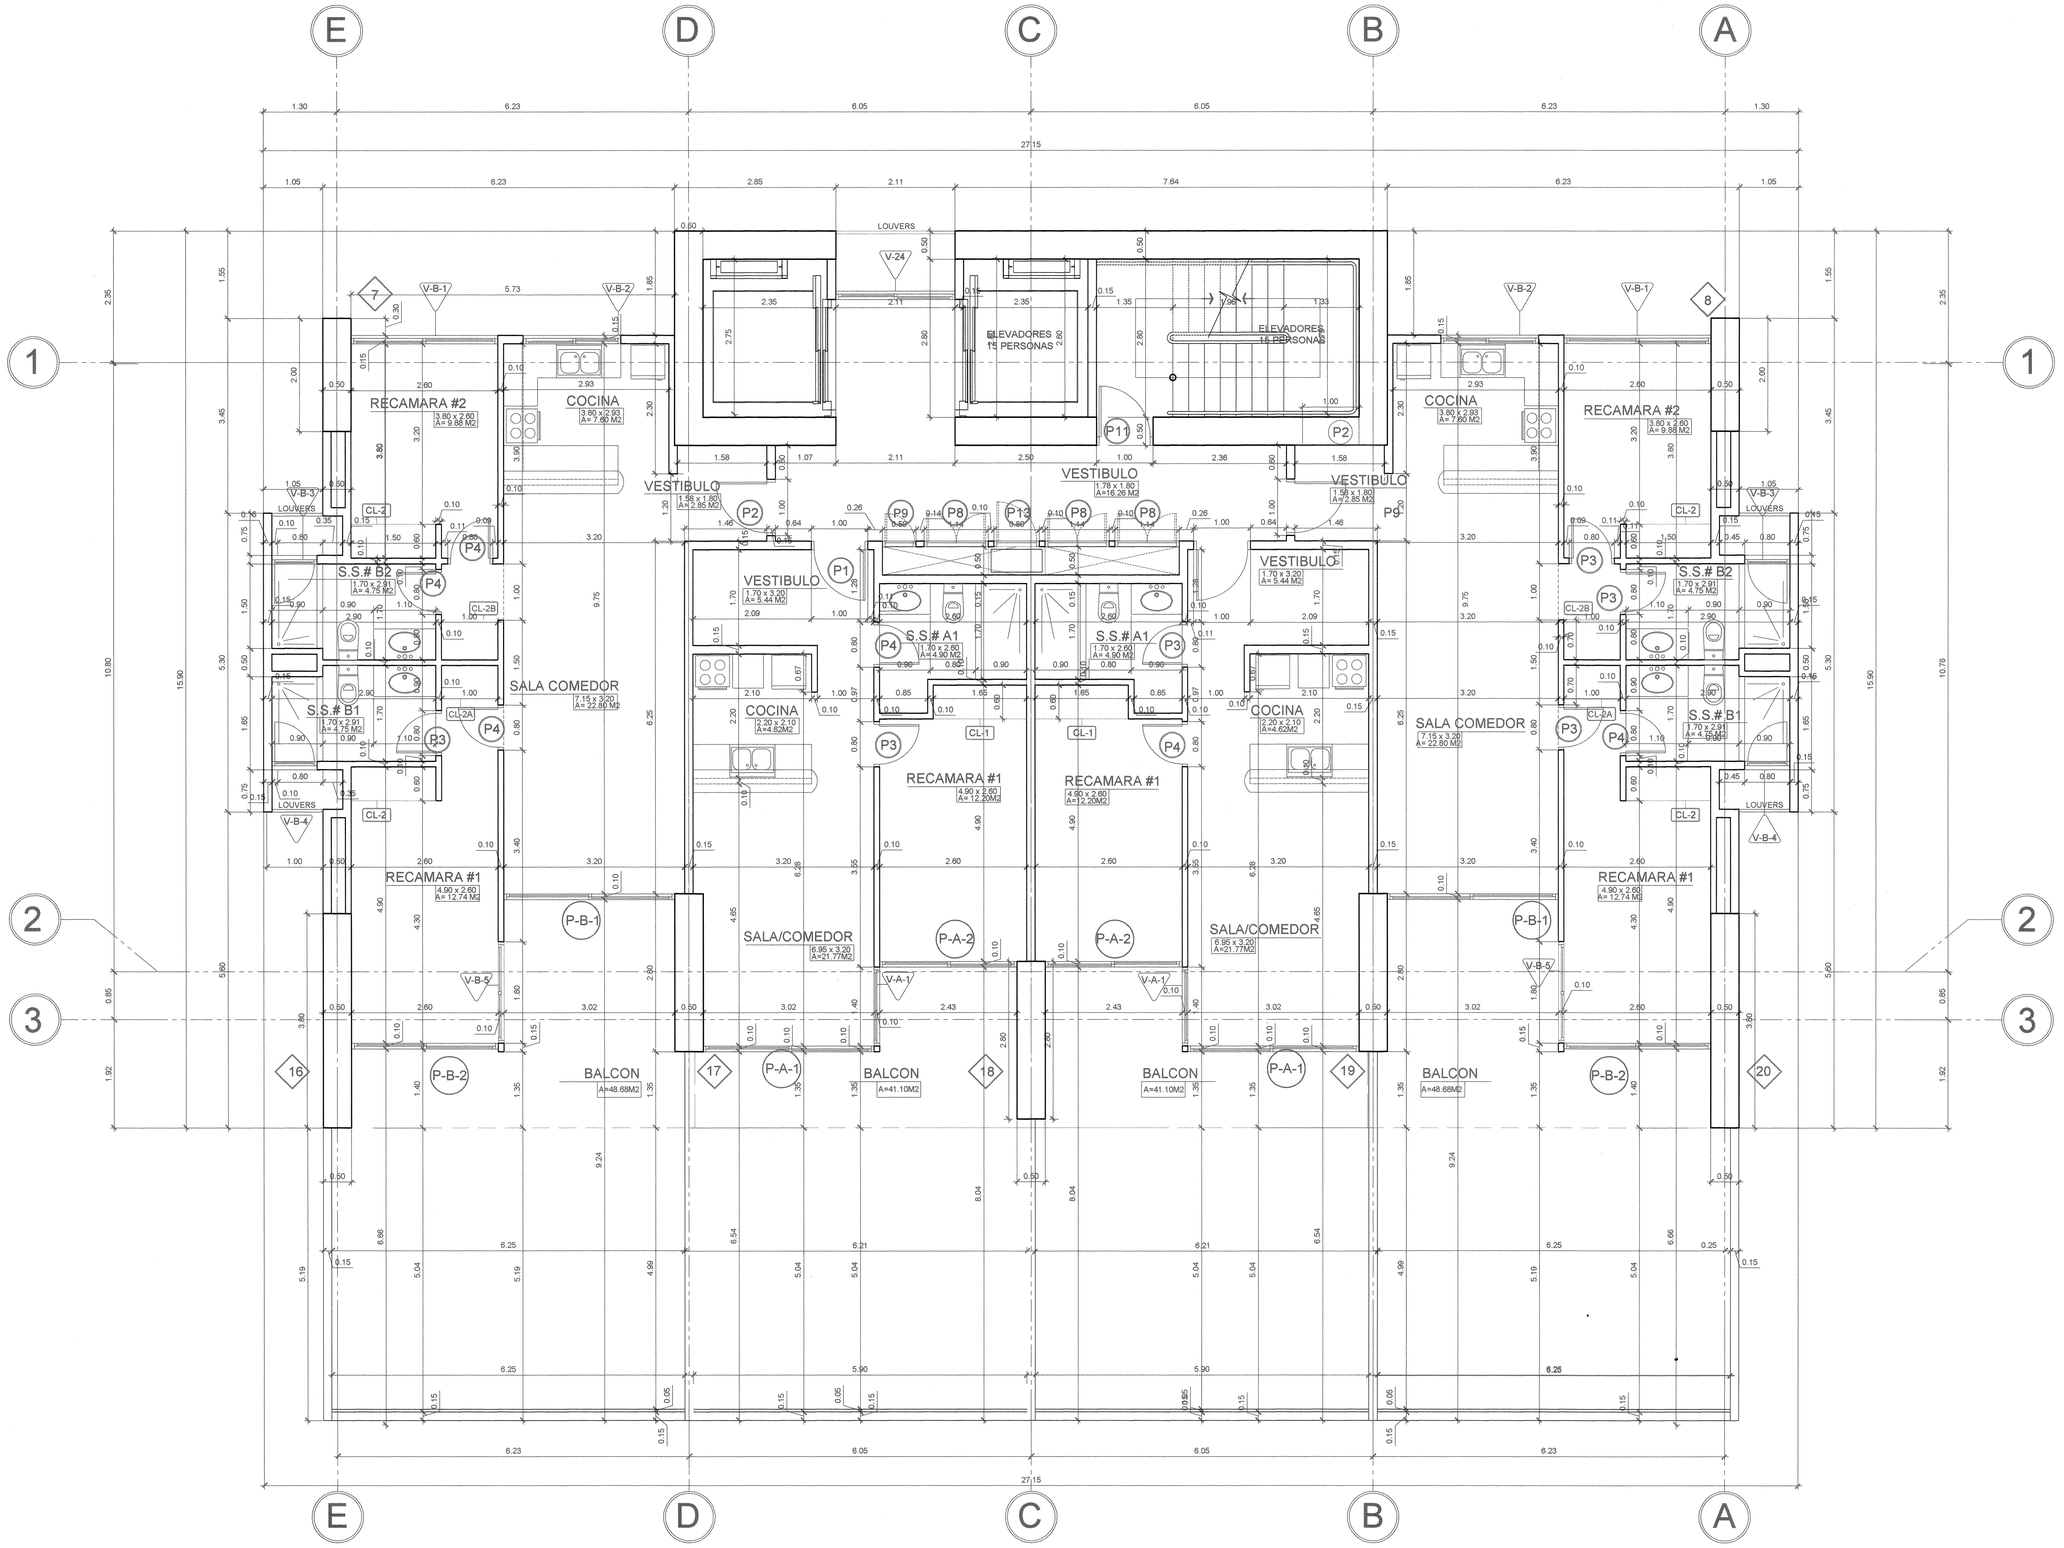

PLANTA ARQUITECTONICA TORRE B NIVEL + 100

AR

ESCALA: 1:50

INGENIERIA MUNICIPAL
DISTRITO DE SAN CARLOS
APROBADO
FECHA 22/8/11
INGENIERO MUNICIPAL

Cuerpo de Bomberos
OFICINA DE SEGURIDAD
La Chorrera, 1 de Agosto de 2011
Resolución No. 2-11 Plano No. 11-67
Se aprueba el registro de este plano por llenar las condiciones requeridas.
Jefe de la Oficina de Seguridad

FELIPE GONZALEZ LINCK
ARQUITECTO
LICENCIA No. 7771-102
LEY 15 DEL 26 DE ENERO DE 1959
JUNTA TECNICA DE INGENIERIA Y ARQUITECTURA

FELIFE GONZÁLEZ LINCK
ARQUITECTO
Tel. -- 6677 1610 -- Fax 392-2457 | 64205839

DISEÑO ARQUITECTÓNICO	Arq. Vicente Cortes Arq. Igor Cortes
DESARROLLO	Arq. Igor Cortes Arq. Ilem Segismond Arq. Nancy Urriola
PROYECTO ESTRUCTURAL	Ing. Ricauter Bowen
PROYECTO ELÉCTRICO	Ing. Edgar Naranjo
PROYECTO DE PLOMERÍA	Ing. Gilberto Ayala

PROYECTO

Residencial El Palmar

UBICACIÓN

COMUNIDAD DE 'EL PALMAR'
DTTO. DE SAN CARLOS - CORREGIMIENTO DE SAN CARLOS
PANAMÁ

SOCIEDAD PROMOTORA

Inversiones Decuria, S.A.

Representante legal: IGOR CORTES
Número de cédula o pasaporte: BC054493

INGENIERÍA MUNICIPAL

PLANO

-PLANTA ARQUITECTONICA TORRE B
NIVEL 100
ESCALA 1:50

ARCHIVO .DWG	NIVEL+100
FECHA	30/08/2010
FECHA MODIFICACIÓN	DD/MM/AAAA

ARQUITECTURA | HOJA: 17 | DE: 65

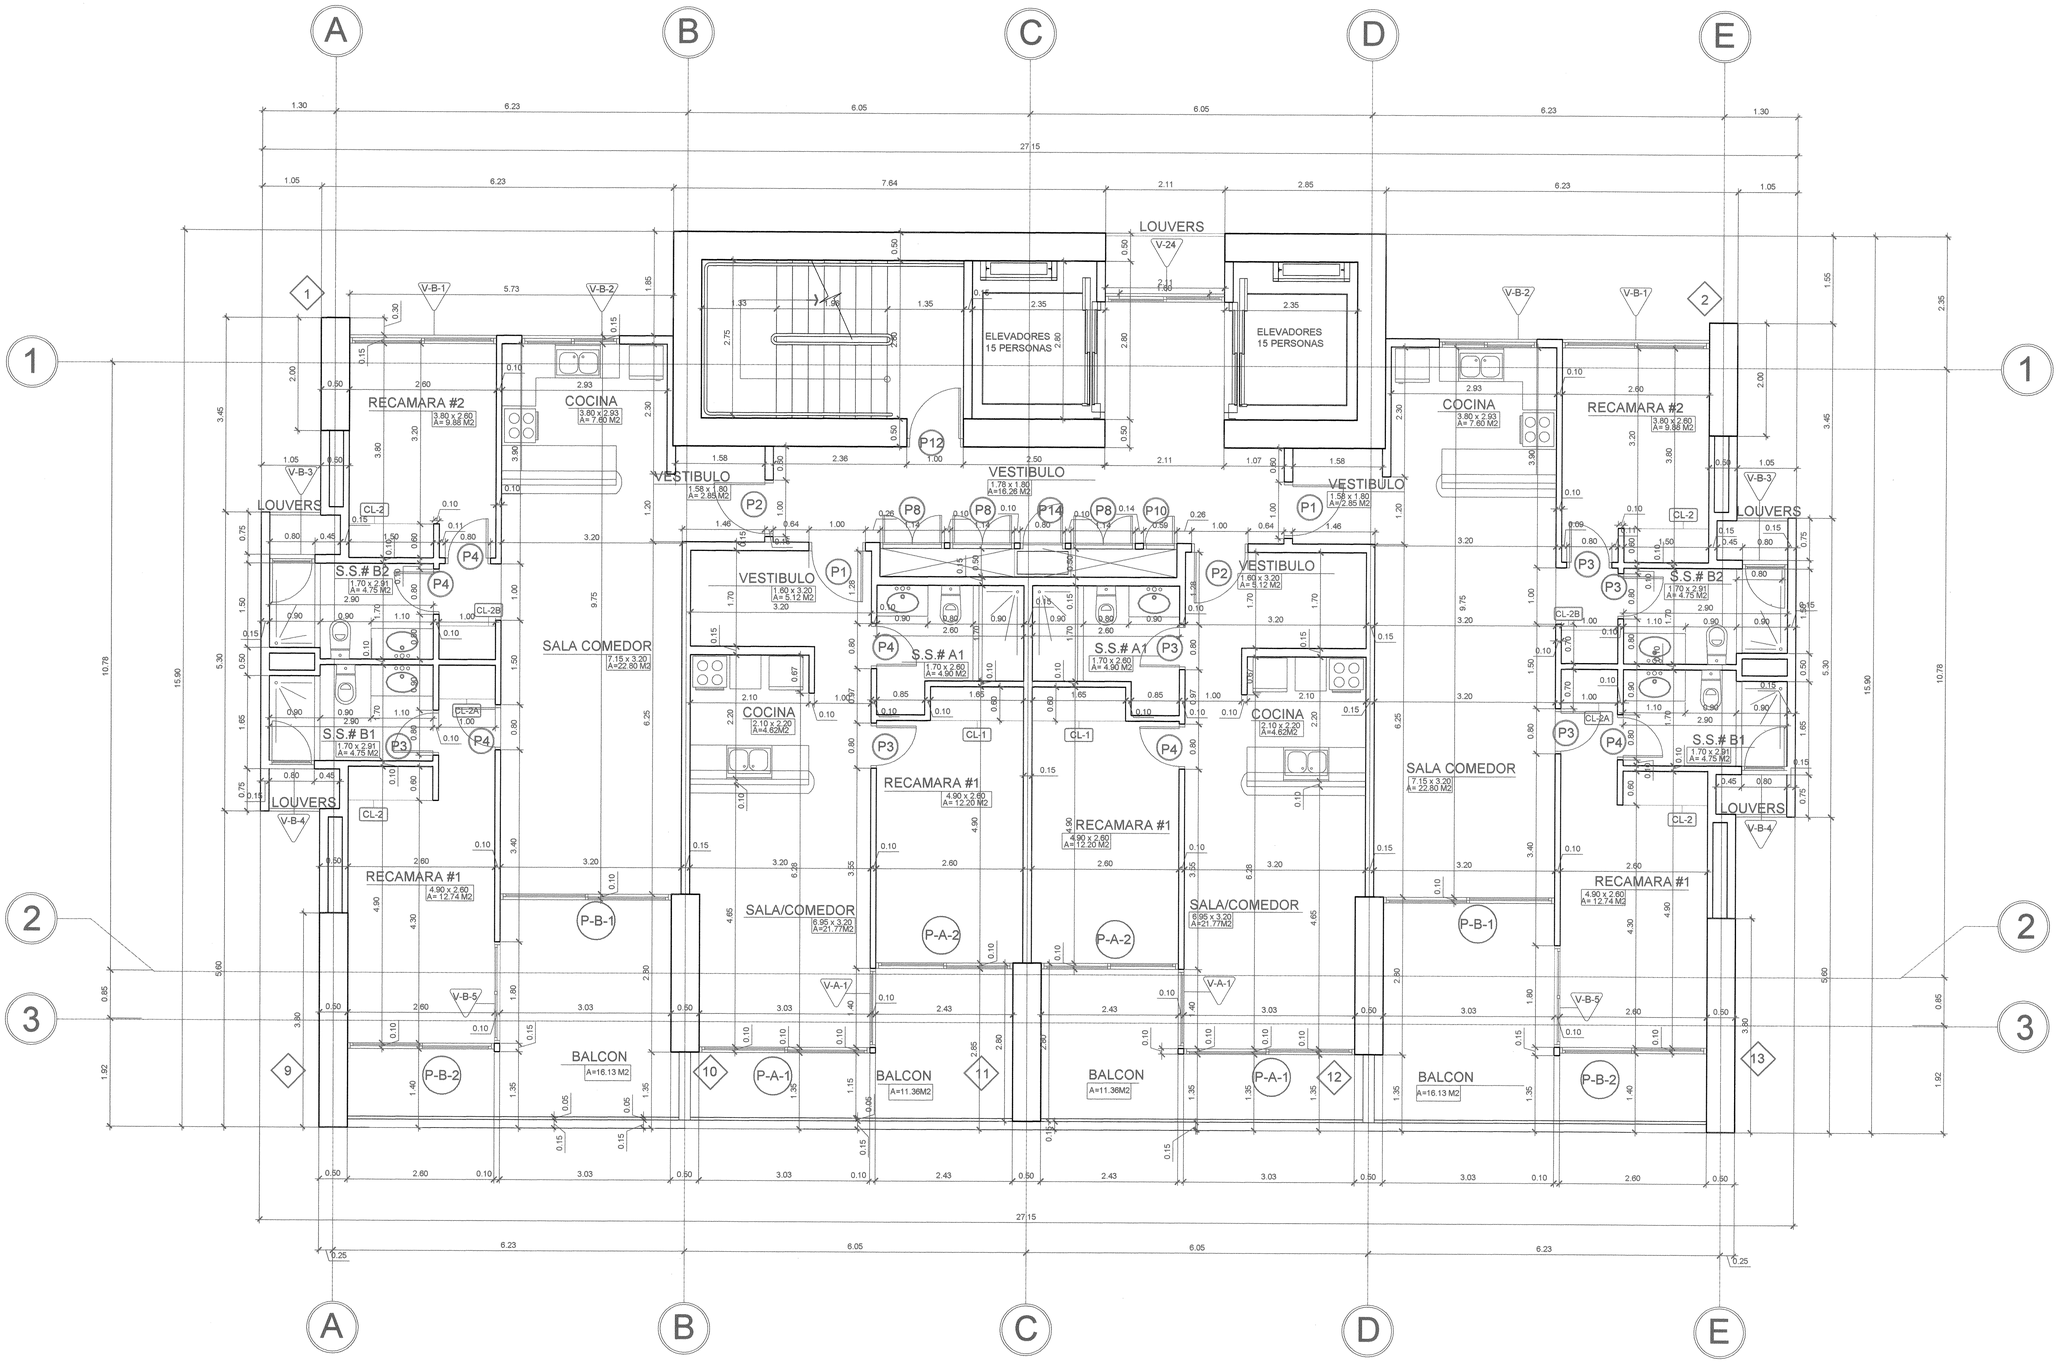

AR PLANTA ARQUITECTONICA TORRE A NIVEL + 200@500

ESCALA: 1:50

INGENIERIA MUNICIPAL
DISTRITO DE SAN CARLOS
APROBADO
INGENIERO MUNICIPAL
FECHA 22/8/11

Cuerpo de Bomberos
OFICINA DE SEGURIDAD
La Chorrera, 11 de Agosto de 2011
Resolución No. 314
Se aprueba el registro, sin plano por llenar las condiciones requeridas
Jefe de la Oficina de Seguridad

FELIPE GONZALEZ LINCK
ARQUITECTO
LICENCIA No. 7770-102
LEY 15 DEL 26 DE ENERO DE 1959
JUNTA TECNICA DE INGENIERIA Y ARQUITECTURA

FELIPE GONZÁLEZ LINCK
ARQUITECTO
Tel. -- 66771610 – Fax 392-2457 | 64035839

DISEÑO ARQUITECTÓNICO	Arq. Vicente Cortes Arq. Igor Cortes
DESARROLLO	Arq. Igor Cortes Arq. Ilem Segismond Arq. Nancy Urriola
PROYECTO ESTRUCTURAL	Ing. Ricauter Bowen
PROYECTO ELÉCTRICO	Ing. Edgar Naranjo
PROYECTO DE PLOMERÍA	Ing. Gilberto Ayala

PROYECTO

Residencial El Palmar

UBICACIÓN

COMUNIDAD DE 'EL PALMAR'
DTTO. DE SAN CARLOS - CORREGIMIENTO DE SAN CARLOS
PANAMÁ

SOCIEDAD PROMOTORA

Inversiones Decuria, S.A.

Representante legal: IGOR CORTES
Número de cédula o pasaporte: 8C054493

INGENIERÍA MUNICIPAL

PLANO

- PLANTA ARQUITECTONICA TORRE A NIVEL 200 @ 500
ESCALA 1:50

ARCHIVO .DWG	NIVEL+200@+500
FECHA	30/08/2010
FECHA MODIFICACIÓN	DD/MM/AAAA

ARQUITECTURA	HOJA:	DE:
	18	65

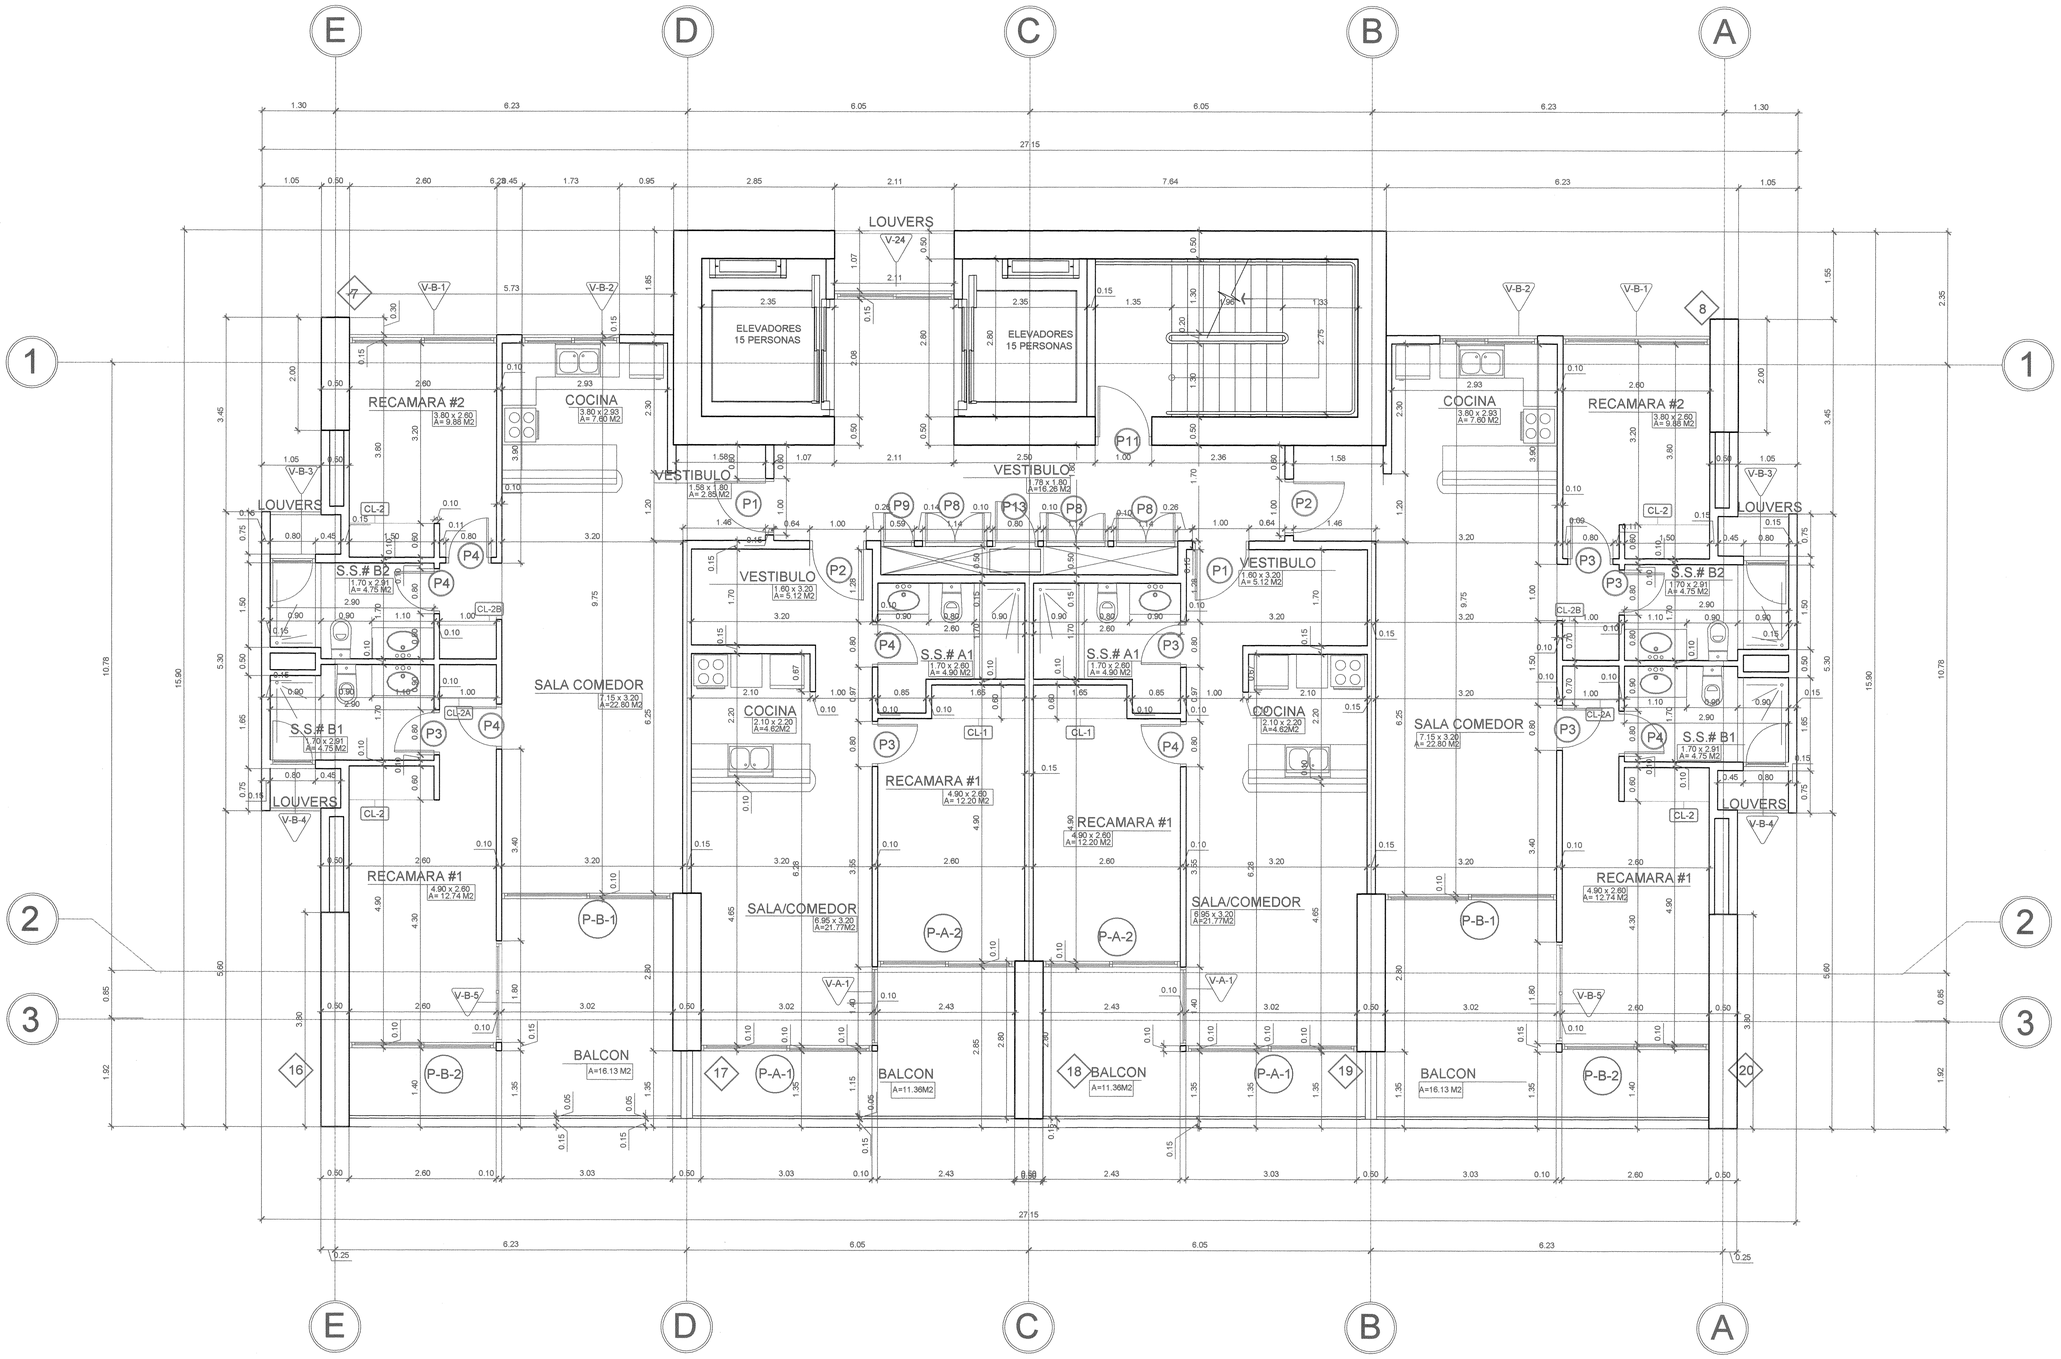

AR PLANTA ARQUITECTONICA TORRE B NIVEL + 200@500

ESCALA: 1:50

INGENIERIA MUNICIPAL
DISTRITO DE SAN CARLOS
APROBADO
INGENIERO MUNICIPAL
FECHA 22/8/11

Cuerpo de Bomberos
OFICINA DE SEGURIDAD
La Chorrera, 11 de Agosto de 2011
Resolución No. 214 Plano No. 116
Se aprueba el presente plano por llenar las condiciones requeridas
Jefe de la Oficina de Seguridad

FELIPE GONZALEZ LINCK
ARQUITECTO
LICENCIA No. 87-188
LEY 15 DEL 26 DE ENERO DE 1959
JUNTA TECNICA DE INGENIERIA Y ARQUITECTURA

FELIFE GONZÁLEZ LINCK
ARQUITECTO
Tel. – 66771610 – Fax 392-2457 | 64035839

DISEÑO ARQUITECTÓNICO	Arq. Vicente Cortes Arq. Igor Cortes
DESARROLLO	Arq. Igor Cortes Arq. Ilem Segismond Arq. Nancy Urriola
PROYECTO ESTRUCTURAL	Ing. Ricauter Bowen
PROYECTO ELÉCTRICO	Ing. Edgar Naranjo
PROYECTO DE PLOMERÍA	Ing. Gilberto Ayala

PROYECTO

Residencial El Palmar

UBICACIÓN

COMUNIDAD DE 'EL PALMAR'
DTTO. DE SAN CARLOS - CORREGIMIENTO DE SAN CARLOS
PANAMÁ

SOCIEDAD PROMOTORA

Inversiones Decuria, S.A.

Representante legal: IGOR CORTES
Número de cédula o pasaporte: 8C054493

INGENIERÍA MUNICIPAL

PLANO

- PLANTA ARQUITECTONICA TORRE B
NIVEL 200 @ 500
ESCALA 1:50

ARCHIVO .DWG	NIVEL+200@+500
FECHA	30/08/2010
FECHA MODIFICACIÓN	DD/MM/AAAA

ARQUITECTURA	HOJA: 19	DE: 65

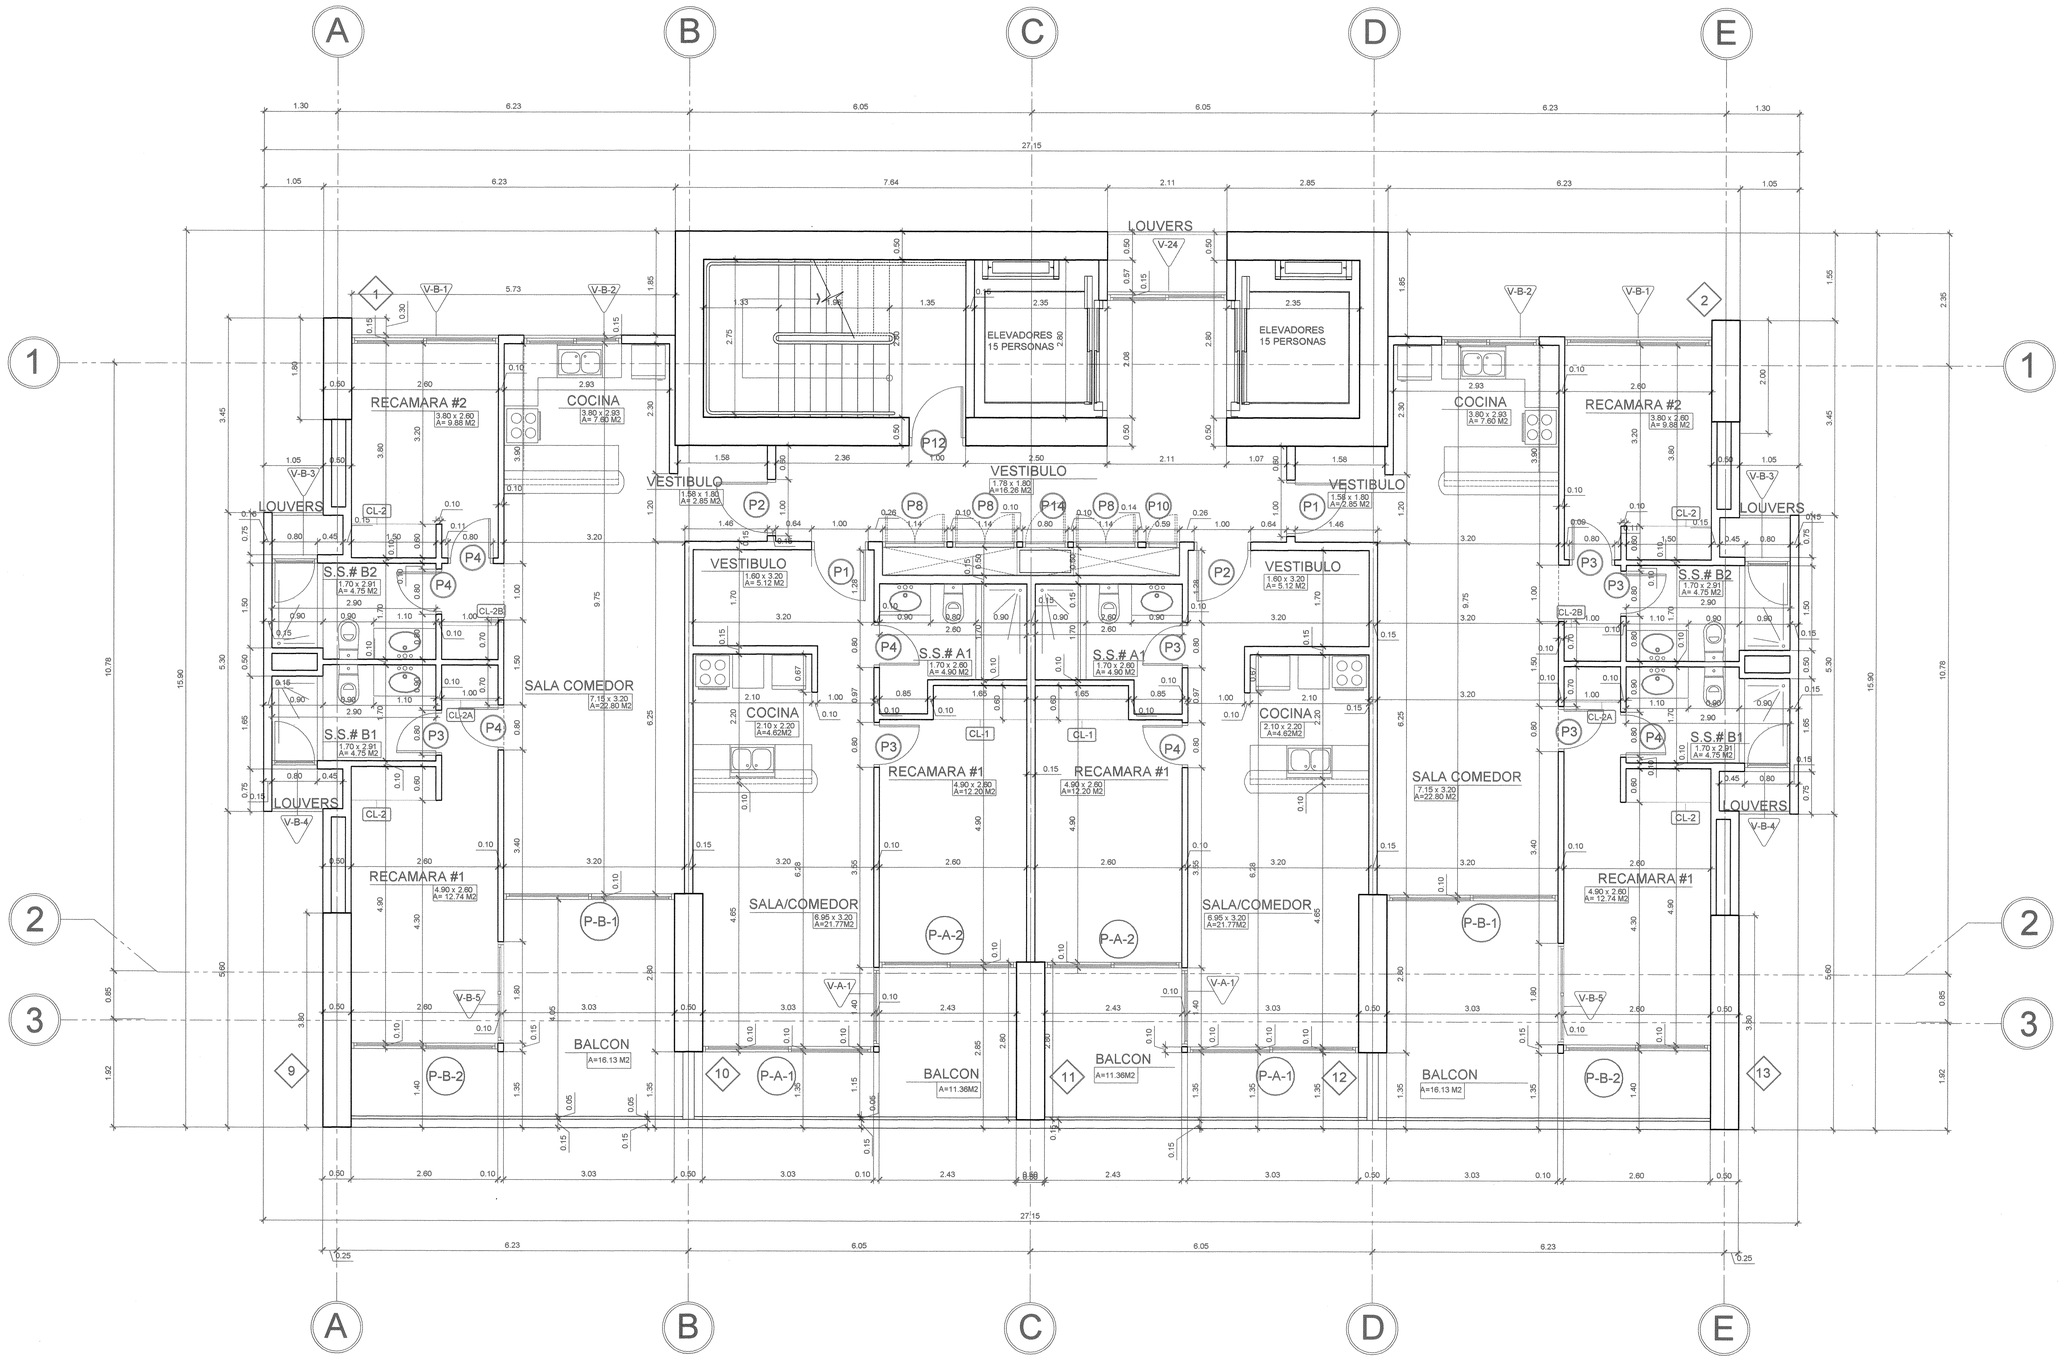

AR PLANTA ARQUITECTONICA TORRE A NIVEL +600@+2200

ESCALA: 1:50

INGENIERIA MUNICIPAL
DISTRITO DE SAN CARLOS
APROBADO
INGENIERO MUNICIPAL
FECHA 22/8/11

Cuerpo de Bomberos
OFICINA DE SEGURIDAD
La Chorrera
Resolución No. 3 de 18 de agosto de 2011
Se aprueba el registro de este plano por llenar las condiciones requeridas.
Jefe de la Oficina de Seguridad

FELIPE GONZALEZ LINCK
ARQUITECTO
LICENCIA No. 97-1108
LEY 15 DE 26 DE ENERO DE 1959
JUNTA TECNICA DE INGENIERIA Y ARQUITECTURA

FELIFE GONZÁLEZ LINCK
ARQUITECTO
Tel. – 66771610 – Fax 392-2457 | 64035839

DISEÑO ARQUITECTÓNICO	Arq. Vicente Cortes Arq. Igor Cortes
DESARROLLO	Arq. Igor Cortes Arq. Ilem Segismond Arq. Nancy Urriola
PROYECTO ESTRUCTURAL	Ing. Ricauter Bowen
PROYECTO ELÉCTRICO	Ing. Edgar Naranjo
PROYECTO DE PLOMERÍA	Ing. Gilberto Ayala

PROYECTO

Residencial El Palmar

UBICACIÓN

COMUNIDAD DE 'EL PALMAR'
DTTO. DE SAN CARLOS - CORREGIMIENTO DE SAN CARLOS
PANAMÁ

SOCIEDAD PROMOTORA

Inversiones Decuria, S.A.

Representante legal: IGOR CORTES
Número de cédula o pasaporte: 8C054493

INGENIERÍA MUNICIPAL

PLANO

- PLANTA ARQUITECTONICA TORRE A
NIVEL 600 @ 2200
ESCALA 1:50

ARCHIVO .DWG	NIVEL+600@+2200
FECHA	30/08/2010
FECHA MODIFICACIÓN	DD/MM/AAAA

ARQUITECTURA	HOJA: 20	DE: 65

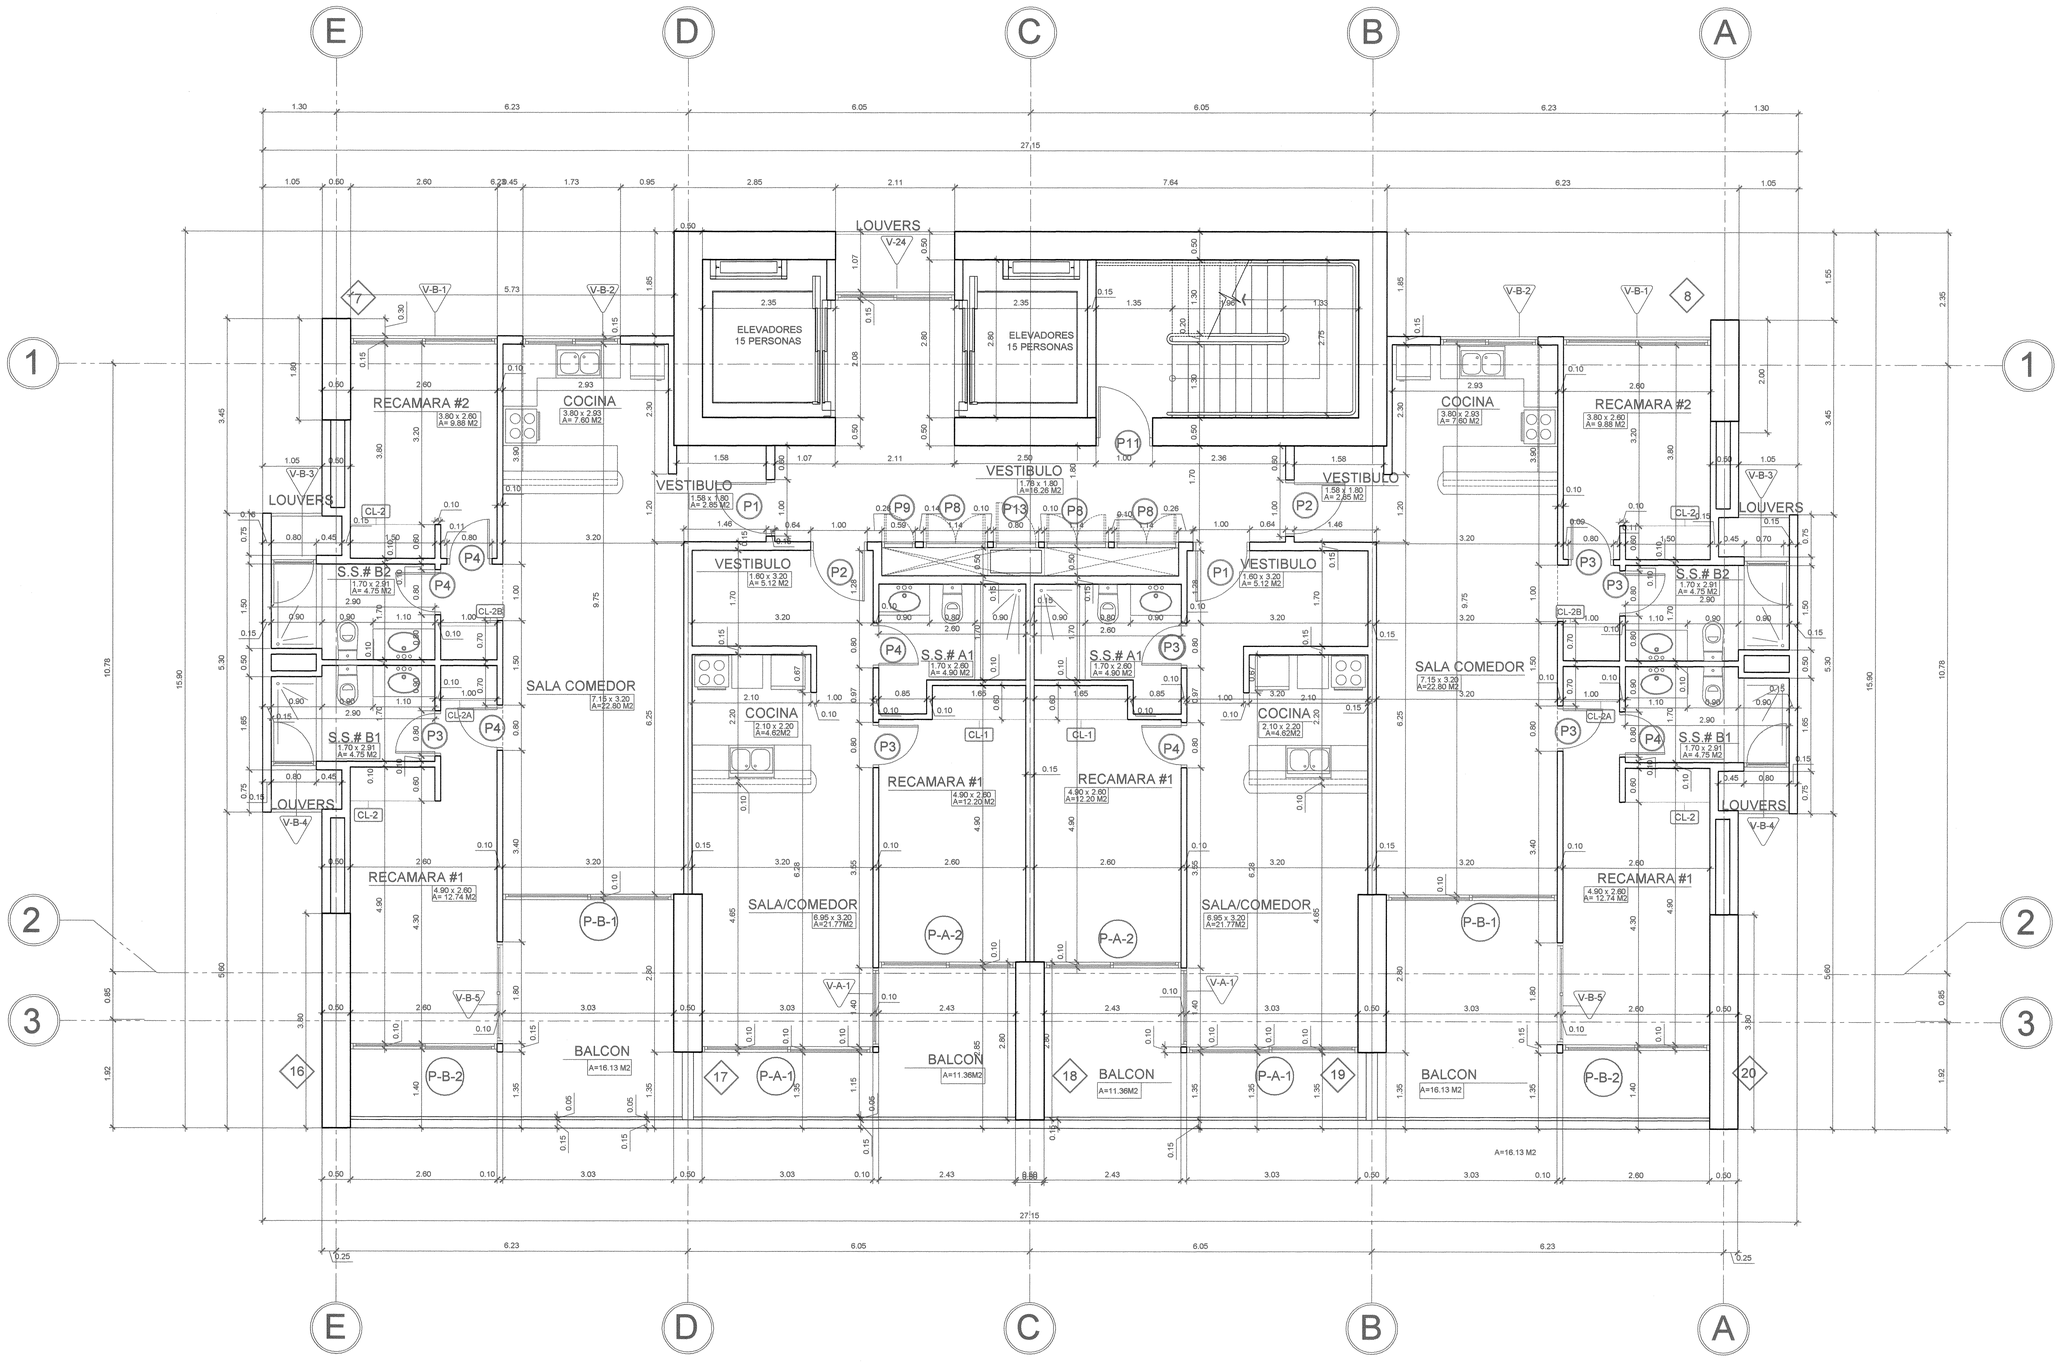

AR PLANTA ARQUITECTONICA TORRE B NIVEL +600@+2200

ESCALA: 1:50

INGENIERIA MUNICIPAL
DISTRITO DE SAN CARLOS
APROBADO
INGENIERO MUNICIPAL
FECHA 22/8/11

Cuerpo de Bomberos de La Chorrera
OFICINA DE SEGURIDAD
La Chorrera, 11 de agosto de 2011
Resolución No. 2011-0148
Se aprueba el registro de este plano, debe llenar las condiciones requeridas.
Jefe de la Oficina de Seguridad

FELIPE GONZALEZ LINCK
ARQUITECTO
IDONEIDAD No. 1008
LEY 15 DEL 26 DE ENERO DE 1959
JUNTA TECNICA DE INGENIERIA Y ARQUITECTURA

FELIFE GONZÁLEZ LINCK
ARQUITECTO
Tel. -- 66771810 -- Fax 302-2457 | 64035839

DISEÑO ARQUITECTÓNICO	Arq. Vicente Cortes Arq. Igor Cortes
DESARROLLO	Arq. Igor Cortes Arq. Ilem Segismond Arq. Nancy Urriola
PROYECTO ESTRUCTURAL	Ing. Ricauter Bowen
PROYECTO ELÉCTRICO	Ing. Edgar Naranjo
PROYECTO DE PLOMERÍA	Ing. Gilberto Ayala

PROYECTO

Residencial El Palmar

UBICACIÓN

COMUNIDAD DE 'EL PALMAR'
DTTO. DE SAN CARLOS - CORREGIMIENTO DE SAN CARLOS
PANAMÁ

SOCIEDAD PROMOTORA

Inversiones Decuria, S.A.

Representante legal: IGOR CORTES
Número de cédula o pasaporte: 8C054493

INGENIERÍA MUNICIPAL

PLANO

- PLANTA ARQUITECTONICA TORRE B
NIVEL 600 @ 2200
ESCALA 1:50

ARCHIVO .DWG	NIVEL+600@+2200
FECHA	30/08/2010
FECHA MODIFICACIÓN	DD/MM/AAAA

ARQUITECTURA | HOJA: 21 | DE: 65

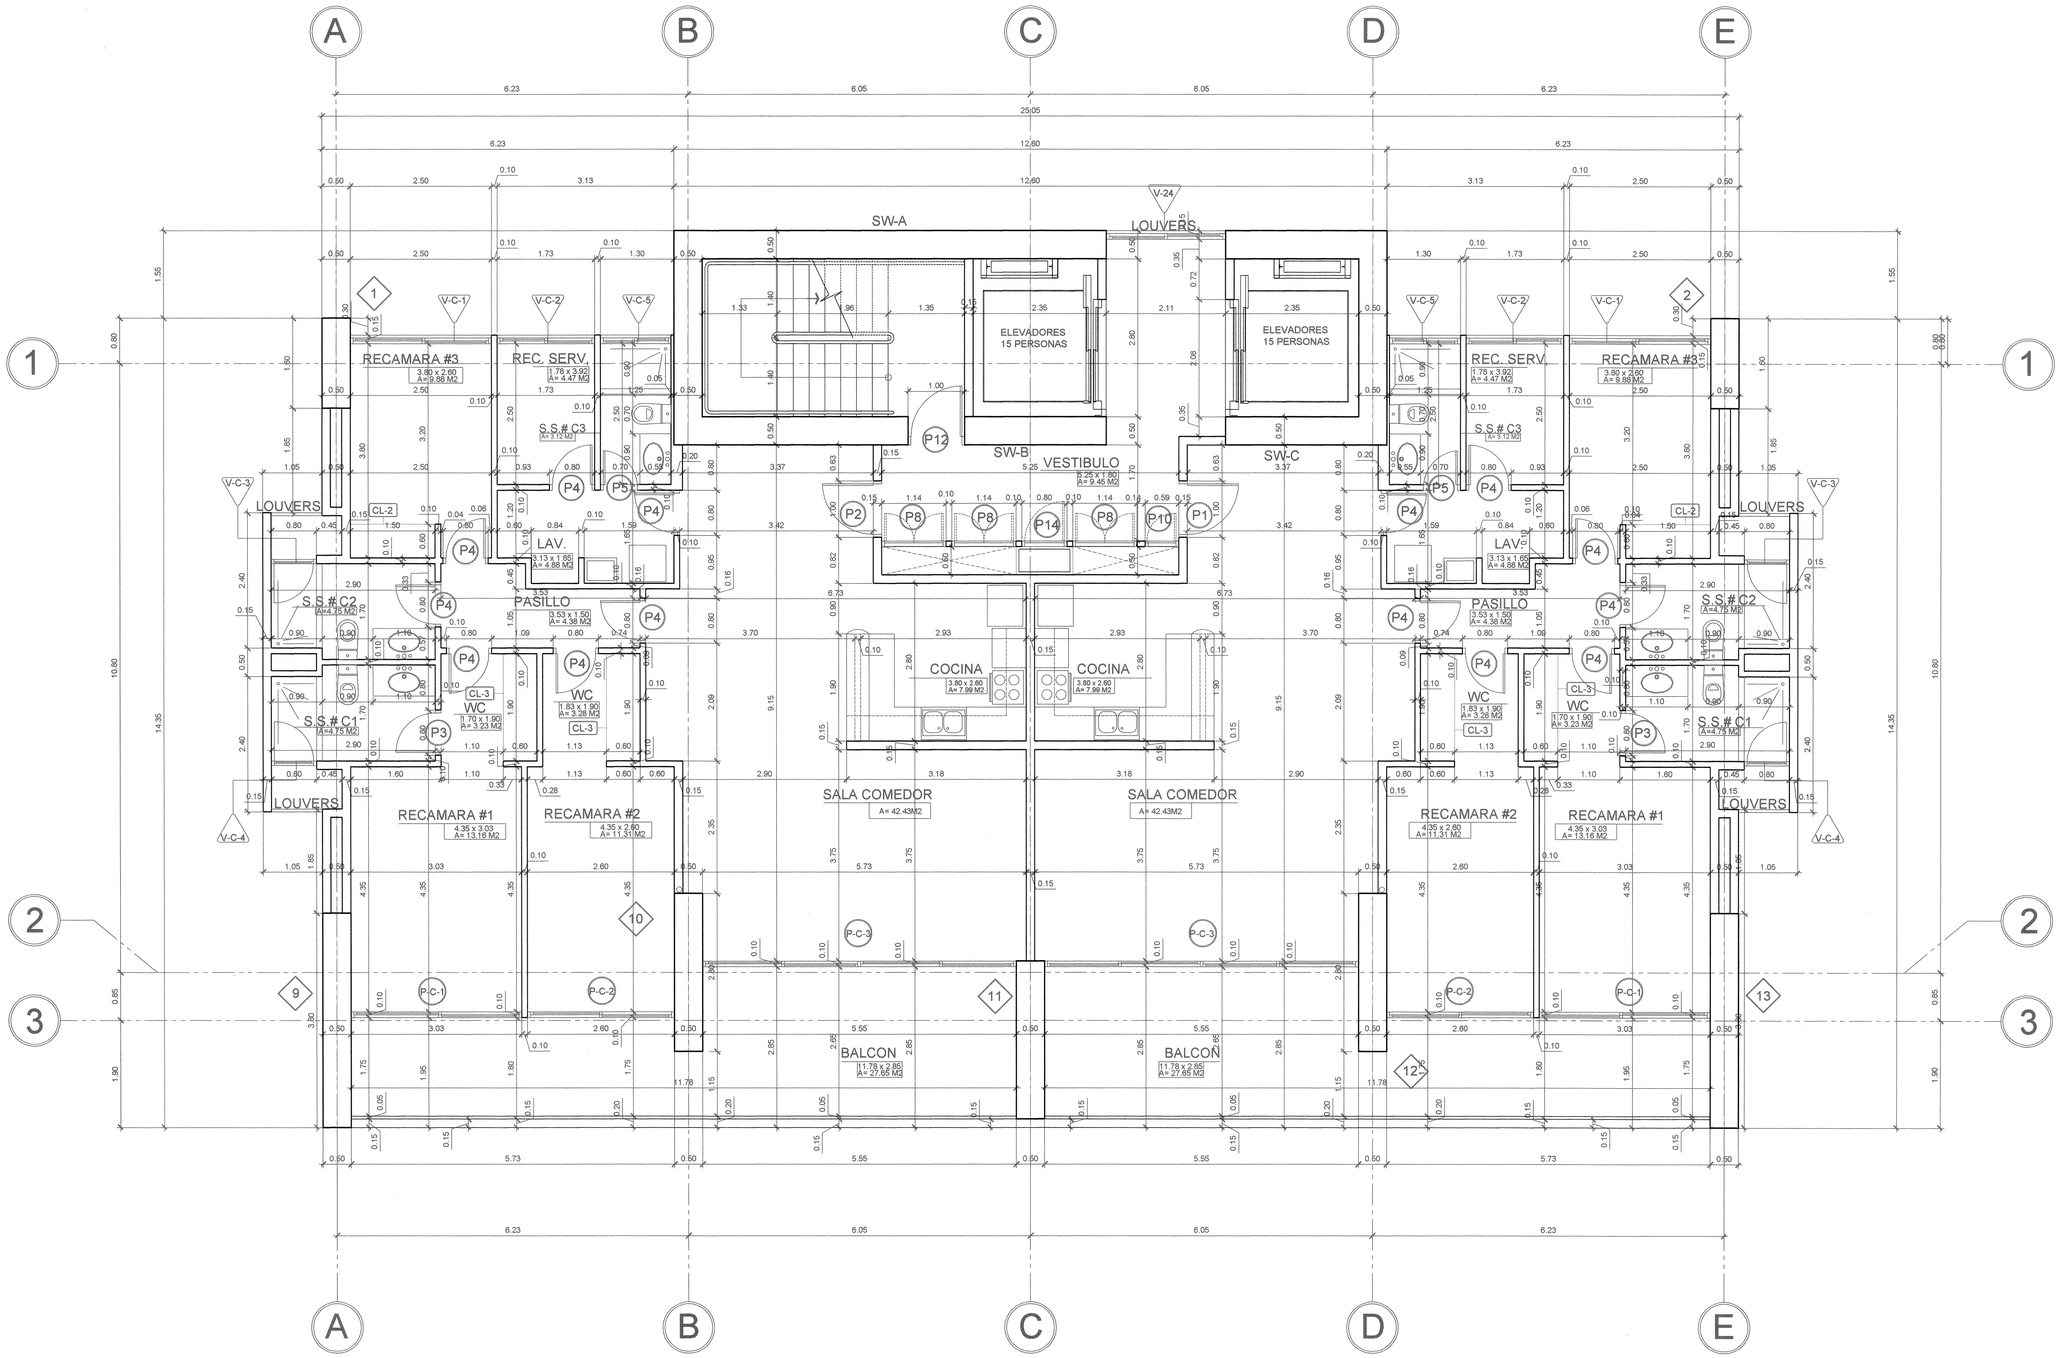

AR PLANTA ARQUITECTONICA TORRE A NIVEL + 2300@2500

ESCALA: 1:50

INGENIERIA MUNICIPAL
DISTRITO DE SAN CARLOS
APROBADO
INGENIERO MUNICIPAL
FECHA 22/8/10

Cuerpo de Bomberos
OFICINA DE SEGURIDAD
La Chorrera

La Chorrera, 11 de Agosto de 2010
Resolución No. 316 - 2010 D.P.C.
Se aprueba el registro de este plano por llenar las condiciones requeridas

Jefe de la Oficina de Seguridad

FELIPE GONZALEZ LINCK
ARQUITECTO
LICENCIA No. 1188
LEY 15 DEL 26 DE ENERO DE 1959
JUNTA TECNICA DE INGENIERIA Y ARQUITECTURA

FELIFE GONZÁLEZ LINCK
ARQUITECTO
Tel. -- 66771610 – Fax 302-2457 | 64035839

DISEÑO ARQUITECTÓNICO	Arq. Vicente Cortes Arq. Igor Cortes
DESARROLLO	Arq. Igor Cortes Arq. Ilem Segismond Arq. Nancy Urriola
PROYECTO ESTRUCTURAL	Ing. Ricauter Bowen
PROYECTO ELÉCTRICO	Ing. Edgar Naranjo
PROYECTO DE PLOMERÍA	Ing. Gilberto Ayala

PROYECTO

Residencial El Palmar

UBICACIÓN

COMUNIDAD DE 'EL PALMAR'
DITTO. DE SAN CARLOS - CORREGIMIENTO DE SAN CARLOS
PANAMÁ

SOCIEDAD PROMOTORA

Inversiones Decuria, S.A.

Representante legal: IGOR CORTES
Número de cédula o pasaporte: 8C054493

INGENIERÍA MUNICIPAL

PLANO

- PLANTA ARQUITECTONICA TORRE A
NIVEL 2300 @ 2500
ESCALA 1:50

ARCHIVO .DWG	NIVEL+2200@2500
FECHA	30/08/2010
FECHA MODIFICACIÓN	DD/MM/AAAA

ARQUITECTURA | HOJA: 22 | DE: 65

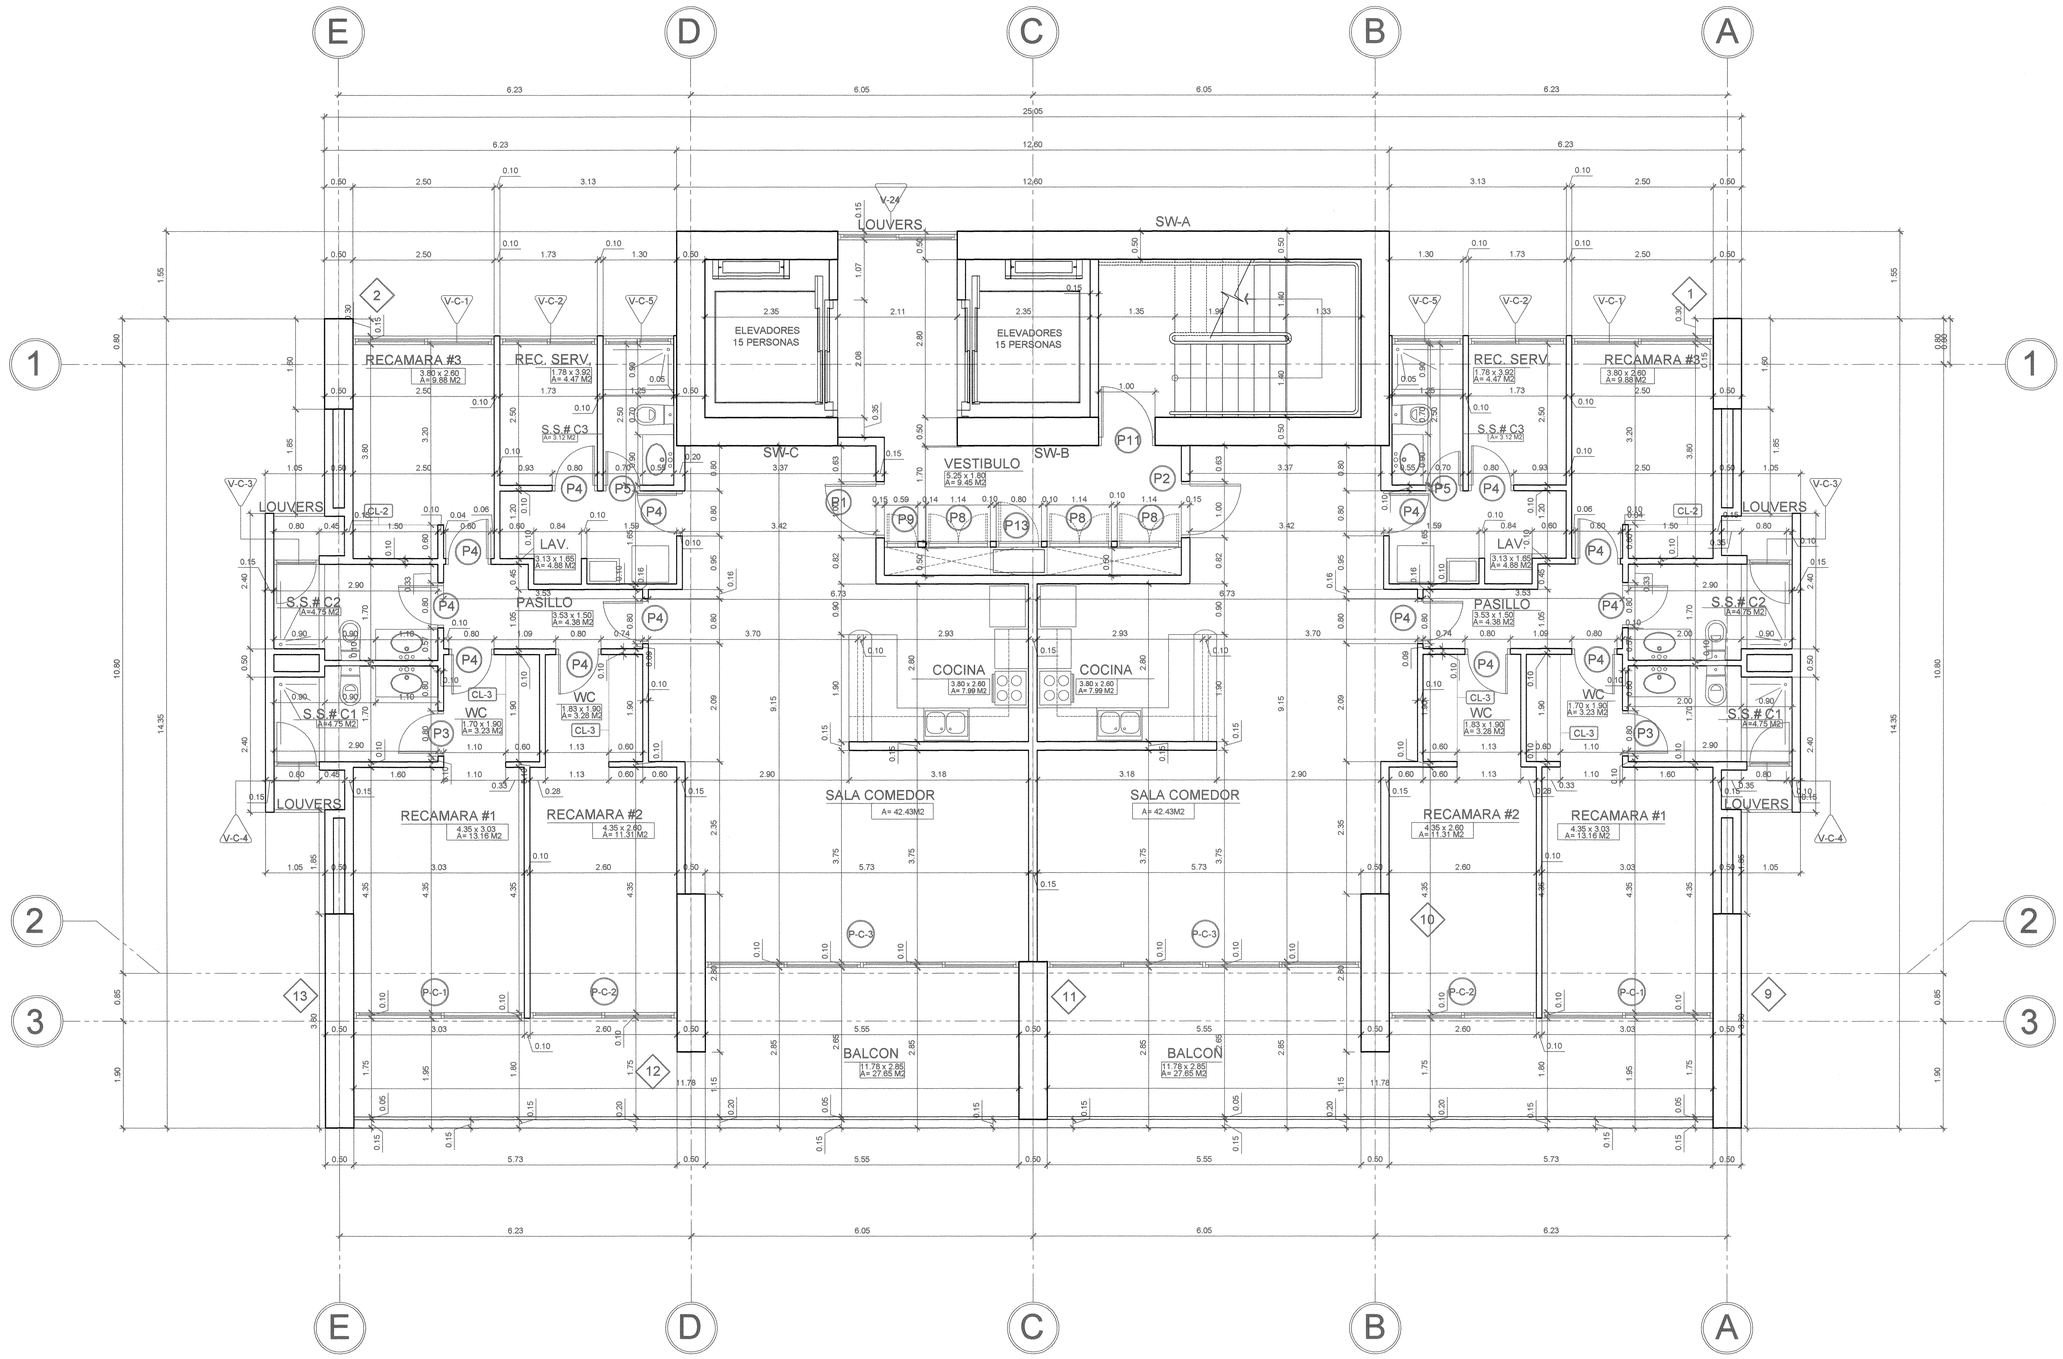

AR PLANTA ARQUITECTONICA TORRE B NIVEL + 2300@2500

ESCALA: 1:50

INGENIERIA MUNICIPAL
DISTRITO DE SAN CARLOS
APROBADO
INGENIERO MUNICIPAL
FECHA 22/8/11

Cuerpo de Bomberos
OFICINA DE SEGURIDAD
La Chorrera, 16/8/11
Resolución No. 316
Se aprueba el requisito de este plano por tener los dispositivos requeridos.
Jefe de la Oficina de Seguridad

FELIPE GONZALEZ LINCK
ARQUITECTO
LICENCIA No. 77-188
LEY 15 DEL 26 DE ENERO DE 1959
JUNTA TECNICA DE INGENIERIA Y ARQUITECTURA

FELIFE GONZÁLEZ LINCK
ARQUITECTO
Tel: -- 66771610 -- Fax 392-2457 | 64035839

DISEÑO ARQUITECTÓNICO	Arq. Vicente Cortes Arq. Igor Cortes
DESARROLLO	Arq. Igor Cortes Arq. Ilem Segismond Arq. Nancy Urriola
PROYECTO ESTRUCTURAL	Ing. Ricauter Bowen
PROYECTO ELÉCTRICO	Ing. Edgar Naranjo
PROYECTO DE PLOMERÍA	Ing. Gilberto Ayala

PROYECTO

Residencial El Palmar

UBICACIÓN

COMUNIDAD DE 'EL PALMAR'
DTTO. DE SAN CARLOS - CORREGIMIENTO DE SAN CARLOS
PANAMÁ

SOCIEDAD PROMOTORA

Inversiones Decuria, S.A.

Representante legal: IGOR CORTES
Número de cédula o pasaporte: 8C054493

INGENIERÍA MUNICIPAL

PLANO

- PLANTA ARQUITECTONICA TORRE B
NIVEL 2300 @ 2500
ESCALA 1:50

ARCHIVO .DWG	NIVEL+2200@2500
FECHA	30/08/2010
FECHA MODIFICACIÓN	DD/MM/AAAA

ARQUITECTURA	HOJA: 23	DE: 65

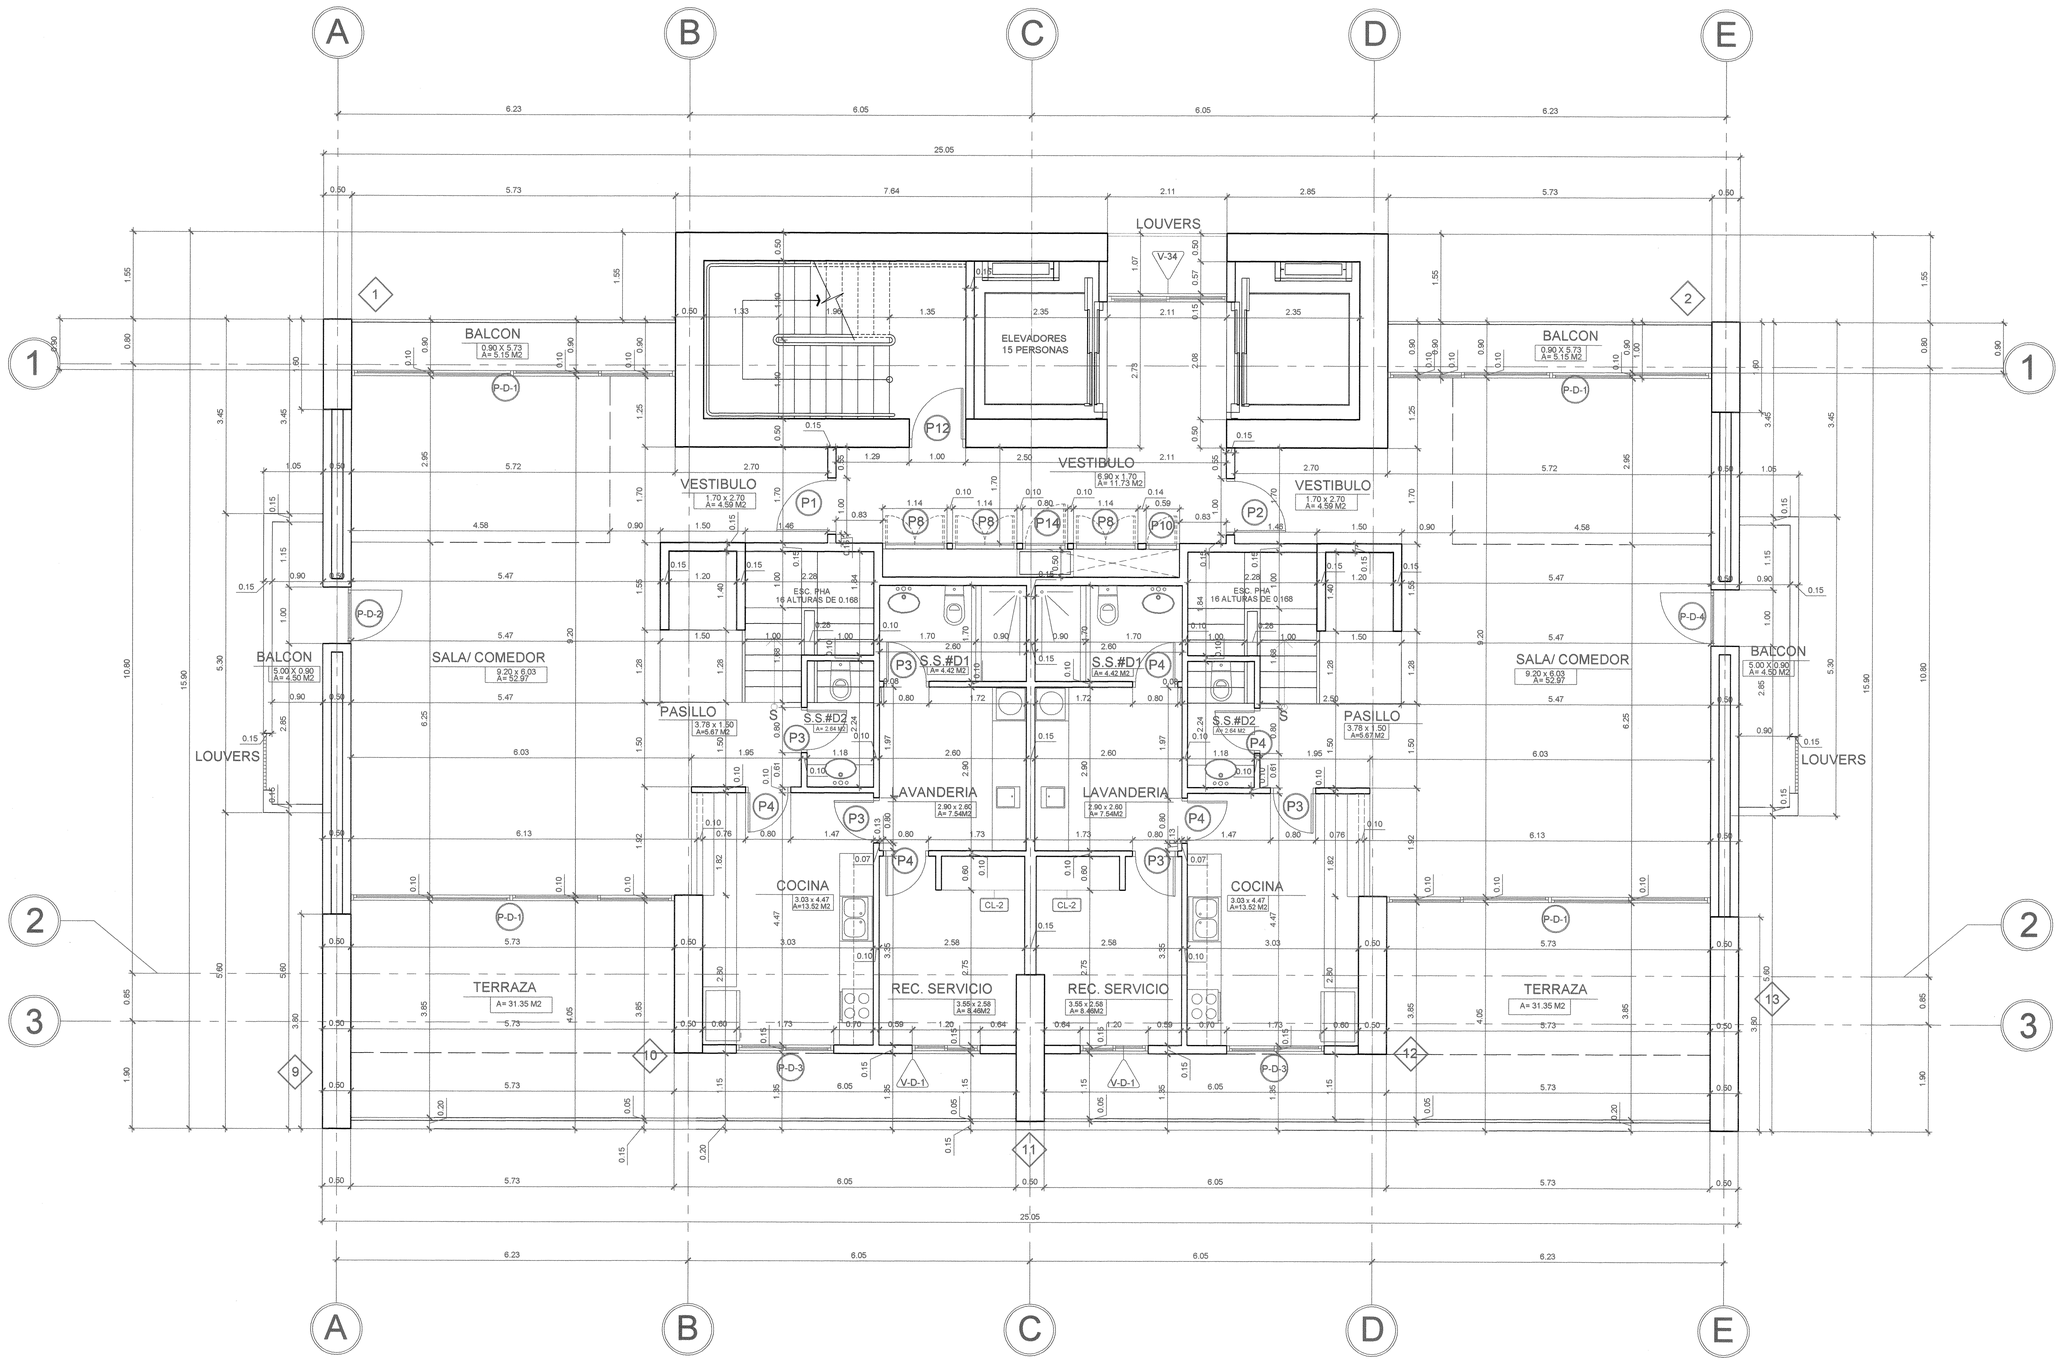

AR PLANTA ARQUITECTONICA TORRE A NIVEL + 2600

ESCALA: 1:50

INGENIERIA MUNICIPAL
DISTRITO DE SAN CARLOS
APROBADO
INGENIERO MUNICIPAL
FECHA 22/6/11

Cuerpo de Bomberos
OFICINA DE PREVENCION
La Chorrera, 11 de agosto de 2011
Resolución No. 3210
Se aprueba el registro de uso clase por llenar las condiciones requeridas.
Teniente de la Policía de Seguridad

FELIPE GONZALEZ LINCK
ARQUITECTO
IDONEIDAD No. 72-1-108
LEY 15 DEL 26 DE ENERO DE 1959
JUNTA TECNICA DE INGENIERIA Y ARQUITECTURA

FELIFE GONZÁLEZ LINCK
ARQUITECTO
Tel. -- 66771610 -- Fax 392-2457 | 64035839

DISEÑO ARQUITECTÓNICO	Arq. Vicente Cortes Arq. Igor Cortes
DESARROLLO	Arq. Igor Cortes Arq. Ilem Segismond Arq. Nancy Urriola
PROYECTO ESTRUCTURAL	Ing. Ricauter Bowen
PROYECTO ELÉCTRICO	Ing. Edgar Naranjo
PROYECTO DE PLOMERÍA	Ing. Gilberto Ayala

PROYECTO

Residencial El Palmar

UBICACIÓN

COMUNIDAD DE 'EL PALMAR'
DTTO. DE SAN CARLOS - CORREGIMIENTO DE SAN CARLOS
PANAMÁ

SOCIEDAD PROMOTORA

Inversiones Decuria, S.A.

Representante legal: IGOR CORTES
Número de cédula o pasaporte: 8-705-2054493

INGENIERÍA MUNICIPAL

PLANO

- PLANTA ARQUITECTONICA TORRE A NIVEL 2600
ESCALA 1:50

ARCHIVO .DWG	NIVEL+2600
FECHA	30/08/2010
FECHA MODIFICACIÓN	DD/MM/AAAA

ARQUITECTURA | HOJA: 24 | DE: 65

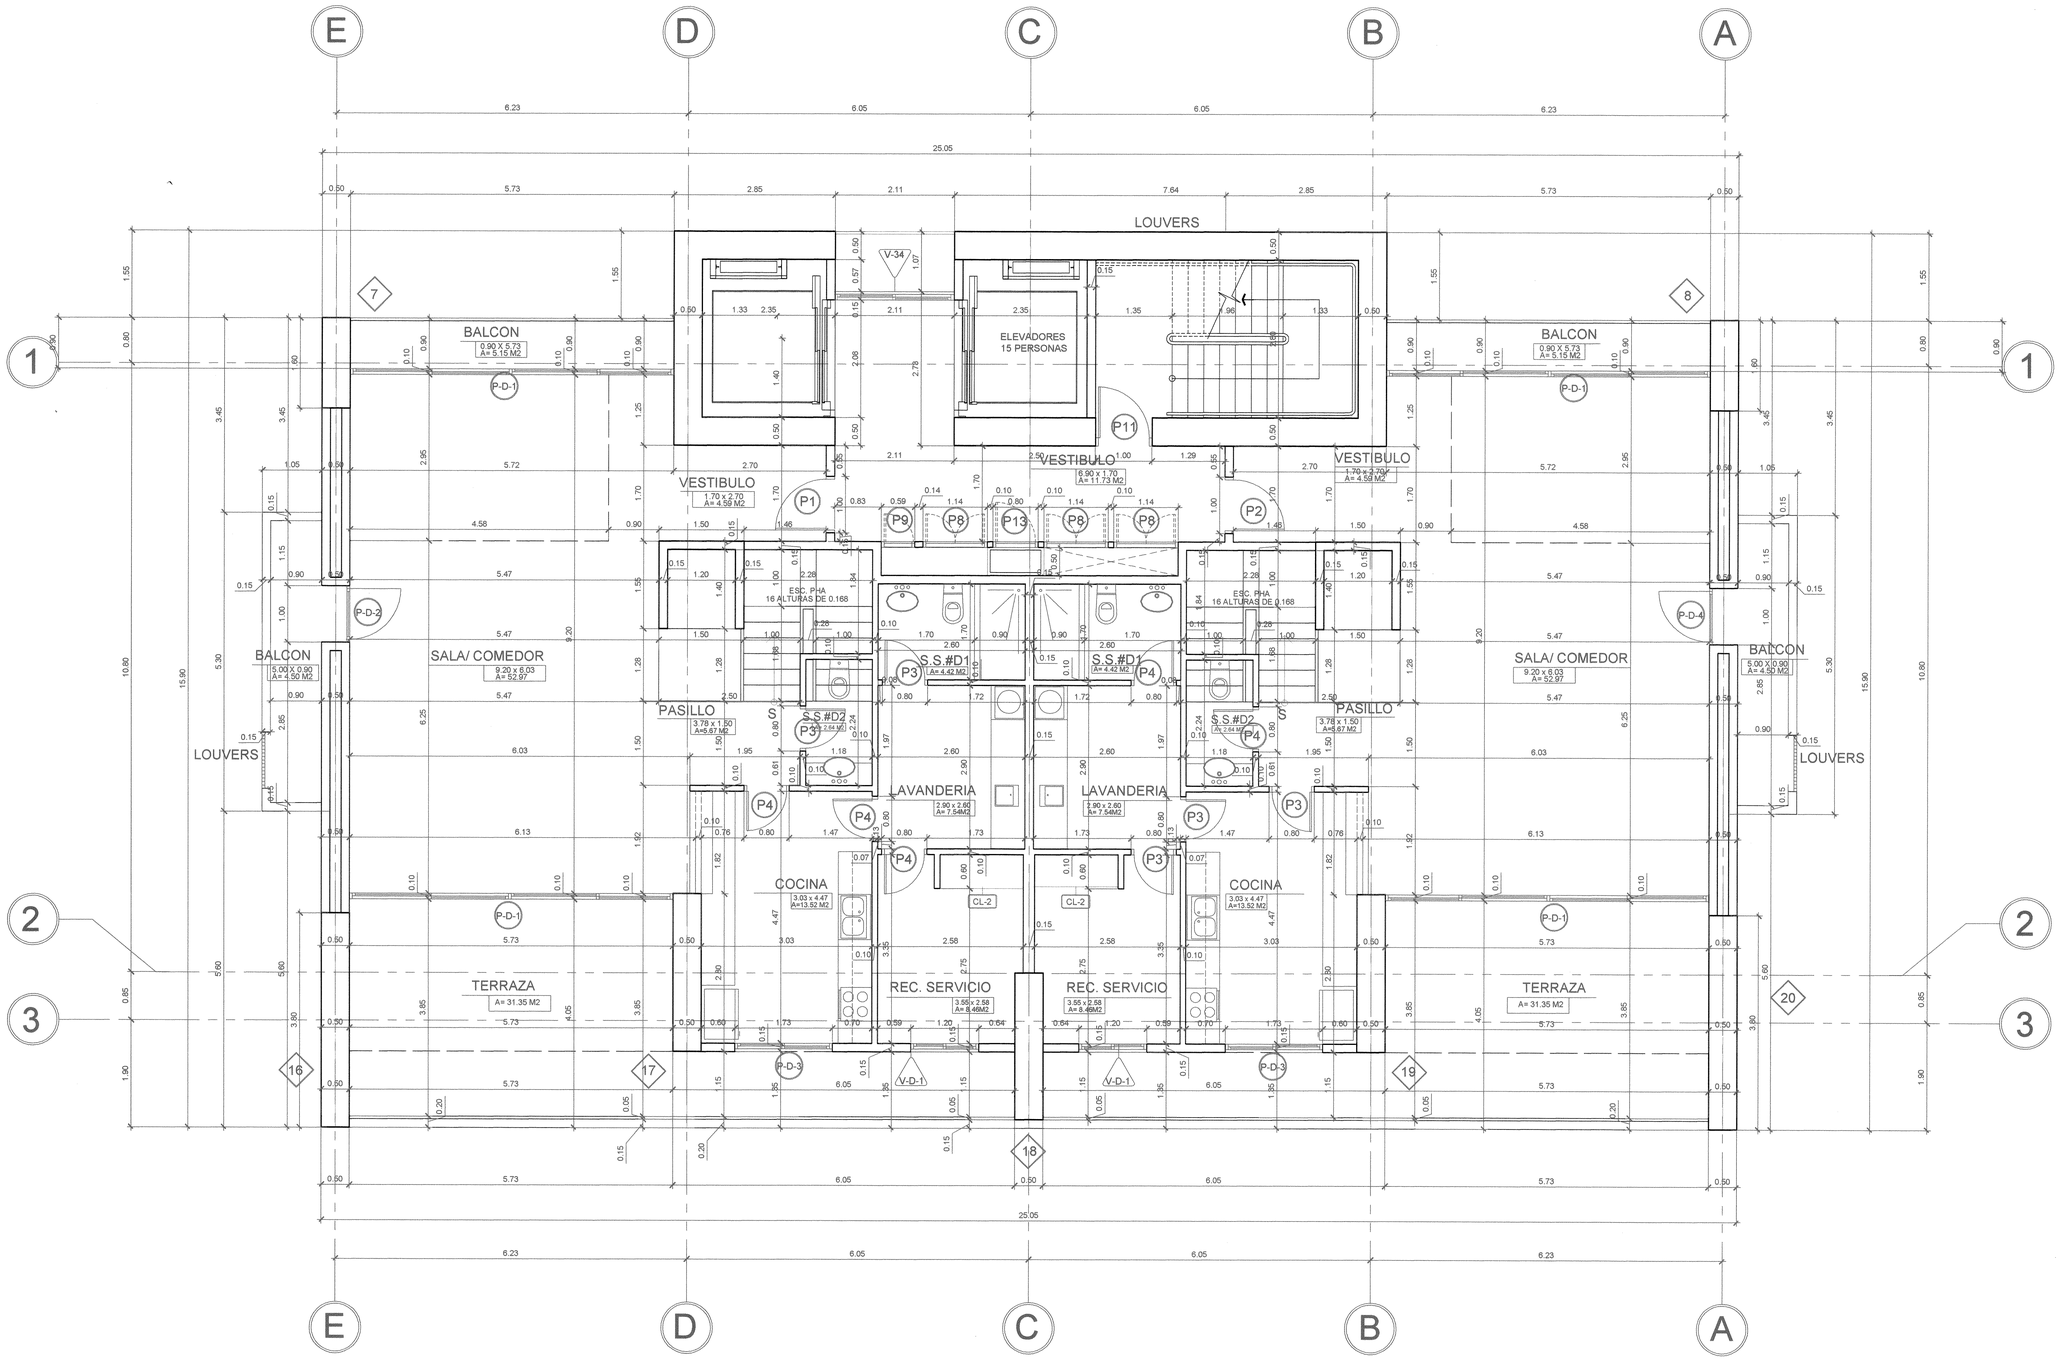

AR PLANTA ARQUITECTONICA TORRE B NIVEL + 2600

ESCALA: 1:50

INGENIERIA MUNICIPAL
DISTRITO DE SAN CARLOS
APROBADO
INGENIERO MUNICIPAL
FECHA 22/9/11

Cuerpo de Bomberos
OFICINA DE SEGURIDAD
La Chorrera
La Chorrera ... de 20...
Resolución No. ... Plano No. ...
Se aprueba el registro de este plano por cumplir las condiciones requeridas.
Jefe de la Oficina de Seguridad

FELIPE GONZALEZ LINCK
ARQUITECTO
LICENCIA No. 87-1-198
LEY 15 DEL 26 DE ENERO DE 1959
JUNTA TECNICA DE INGENIERIA Y ARQUITECTURA

FELIFE GONZÁLEZ LINCK
ARQUITECTO
Tel. -- 66771610 -- Fax 302-2457 | 64035839

DISEÑO ARQUITECTÓNICO	Arq. Vicente Cortes Arq. Igor Cortes
DESARROLLO	Arq. Igor Cortes Arq. Ilem Segismond Arq. Nancy Urriola
PROYECTO ESTRUCTURAL	Ing. Ricauter Bowen
PROYECTO ELÉCTRICO	Ing. Edgar Naranjo
PROYECTO DE PLOMERÍA	Ing. Gilberto Ayala

PROYECTO

Residencial El Palmar

UBICACIÓN

COMUNIDAD DE 'EL PALMAR'
DTTO. DE SAN CARLOS - CORREGIMIENTO DE SAN CARLOS
PANAMÁ

SOCIEDAD PROMOTORA

Inversiones Decuria, S.A.

Representante legal: IGOR CORTES
Número de cédula o pasaporte: 8CO54493

INGENIERÍA MUNICIPAL

PLANO

- PLANTA ARQUITECTONICA TORRE B
NIVEL 2600
ESCALA 1:50

ARCHIVO .DWG	NIVEL+2600
FECHA	30/08/2010
FECHA MODIFICACIÓN	DD/MM/AAAA

ARQUITECTURA | HOJA: 25 | DE: 65

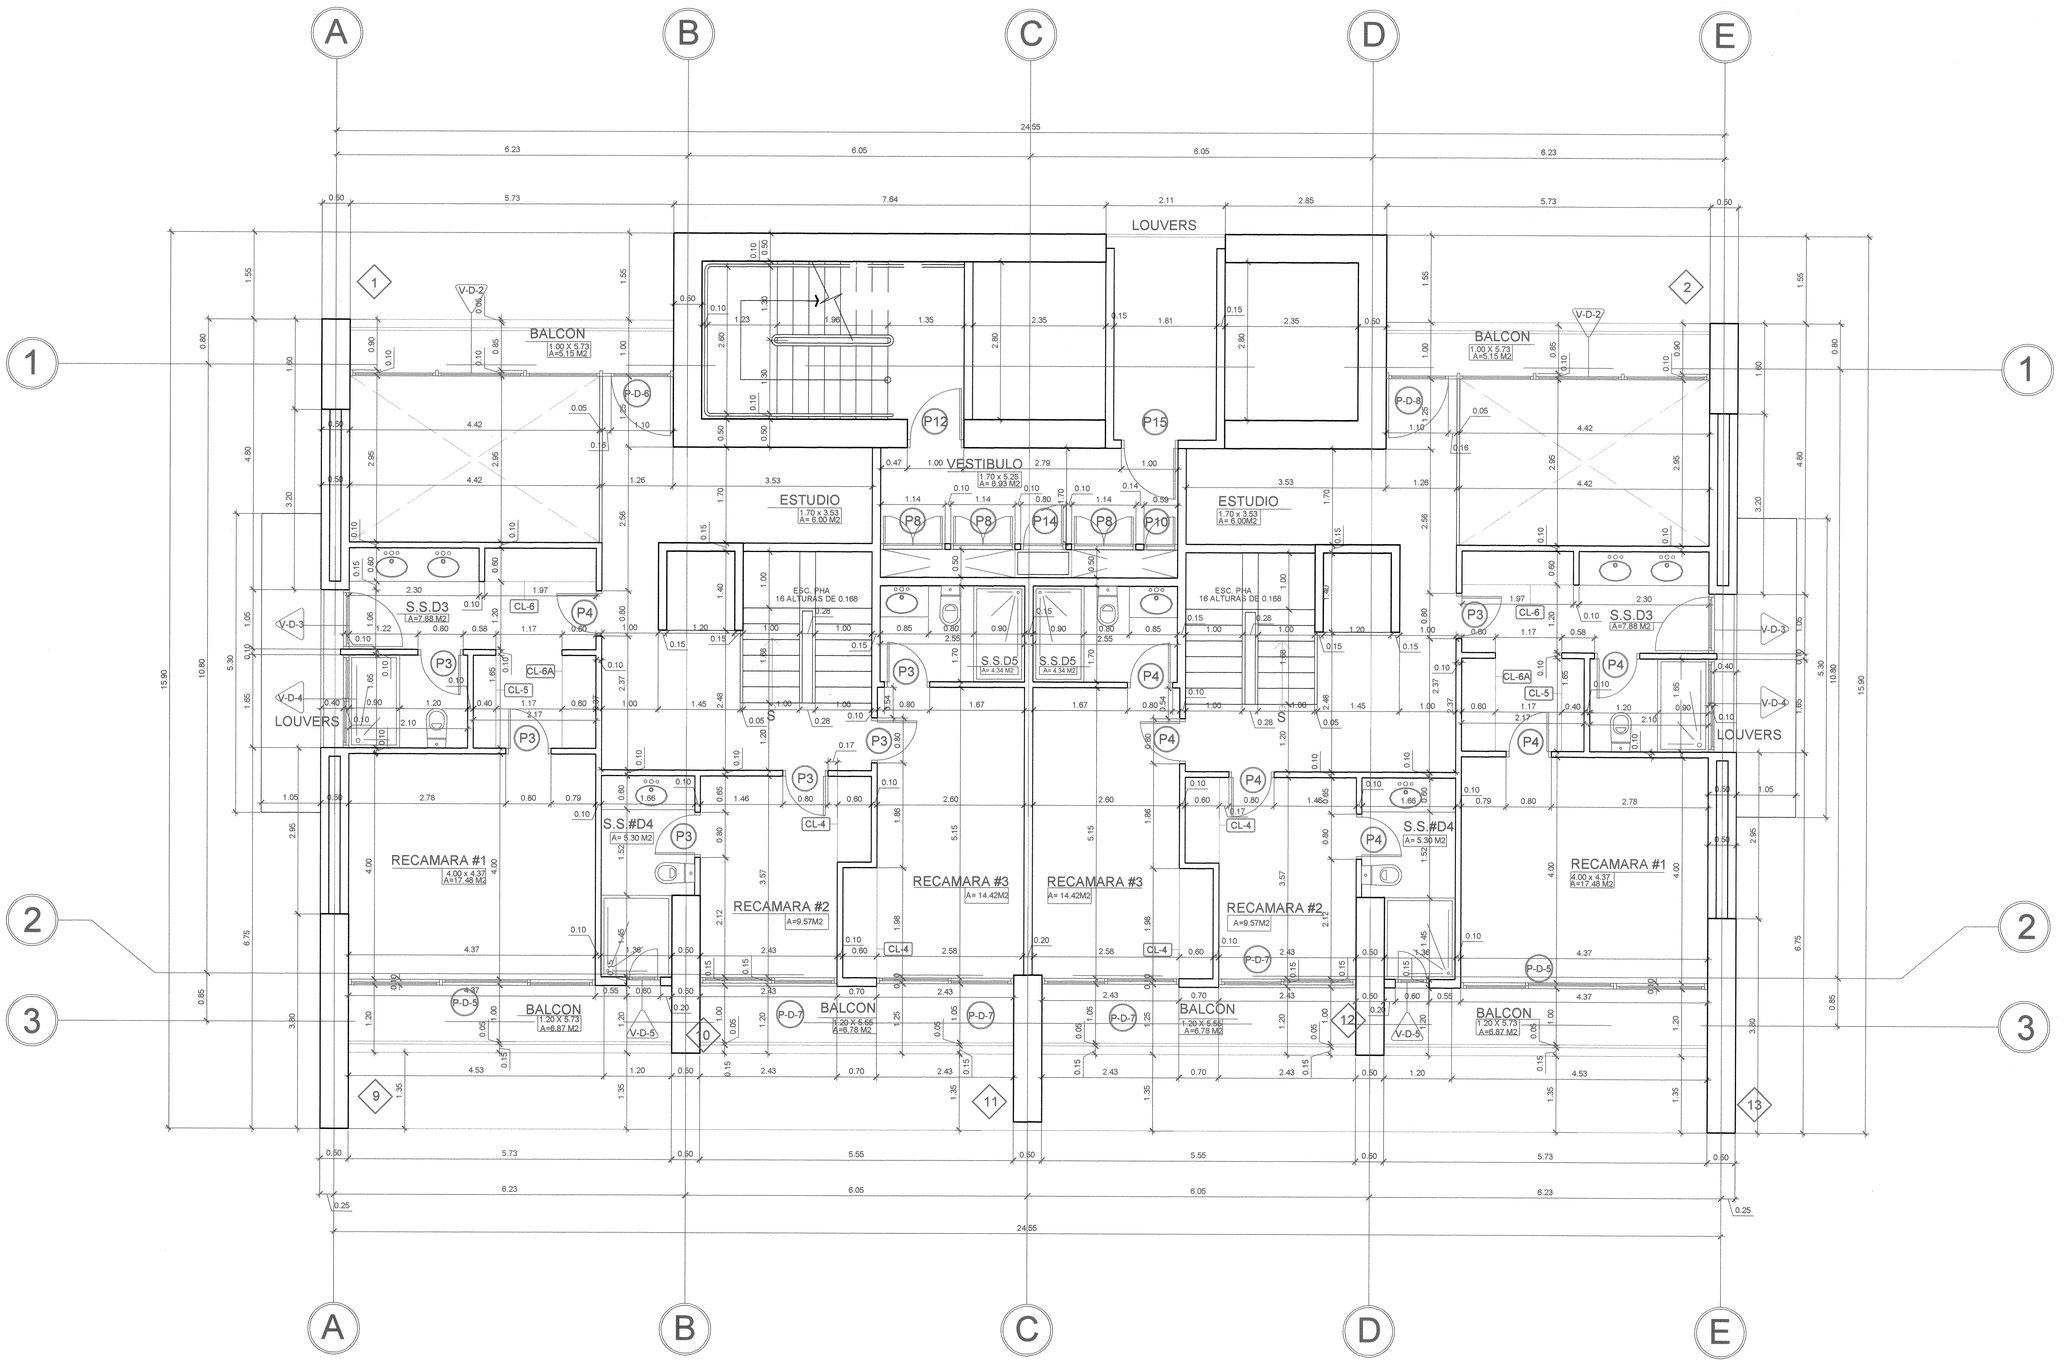

AR PLANTA ARQUITECTONICA TORRE A NIVEL +2700

ESCALA: 1:50

INGENIERIA MUNICIPAL
DISTRITO DE SAN CARLOS
APROBADO
INGENIERO MUNICIPAL
FECHA: 22/8/11

Cuerpo de Bomberos
OFICINA DE SEGURIDAD
La Chorrera

La Chorrera, 11 de Agosto de 2011
Resolución No. 2011 Placa No. 1a de 4...
Se aprueba el registro de este plano por llenar las condiciones requeridas.

Jefe de Seguridad

FELIPE GONZALEZ LINCK
ARQUITECTO
LICENCIA No. 77-108
LEY 15 DEL 23 DE ENERO DE 1959
JUNTA TECNICA DE INGENIERIA Y ARQUITECTURA

FELIPE GONZÁLEZ LINCK
ARQUITECTO
Tel. - 66771610 - Fax 392-2457 | 64035839

DISEÑO ARQUITECTÓNICO	Arq. Vicente Cortes Arq. Igor Cortes
DESARROLLO	Arq. Igor Cortes Arq. Ilem Segismond Arq. Nancy Urriola
PROYECTO ESTRUCTURAL	Ing. Ricauter Bowen
PROYECTO ELÉCTRICO	Ing. Edgar Naranjo
PROYECTO DE PLOMERÍA	Ing. Gilberto Ayala

PROYECTO

Residencial El Palmar

UBICACIÓN

COMUNIDAD DE "EL PALMAR"
DTTO. DE SAN CARLOS - CORREGIMIENTO DE SAN CARLOS
PANAMÁ

SOCIEDAD PROMOTORA

Inversiones Decuria, S.A.

Representante legal: IGOR CORTES
Número de cédula o pasaporte: 8C054493

INGENIERÍA MUNICIPAL

PLANO

- PLANTA ARQUITECTONICA TORRE A
NIVEL 2700
ESCALA 1:50

ARCHIVO .DWG	NIVEL+2700
FECHA	30/08/2010
FECHA MODIFICACIÓN	DD/MM/AAAA

ARQUITECTURA | HOJA: 26 | DE: 65

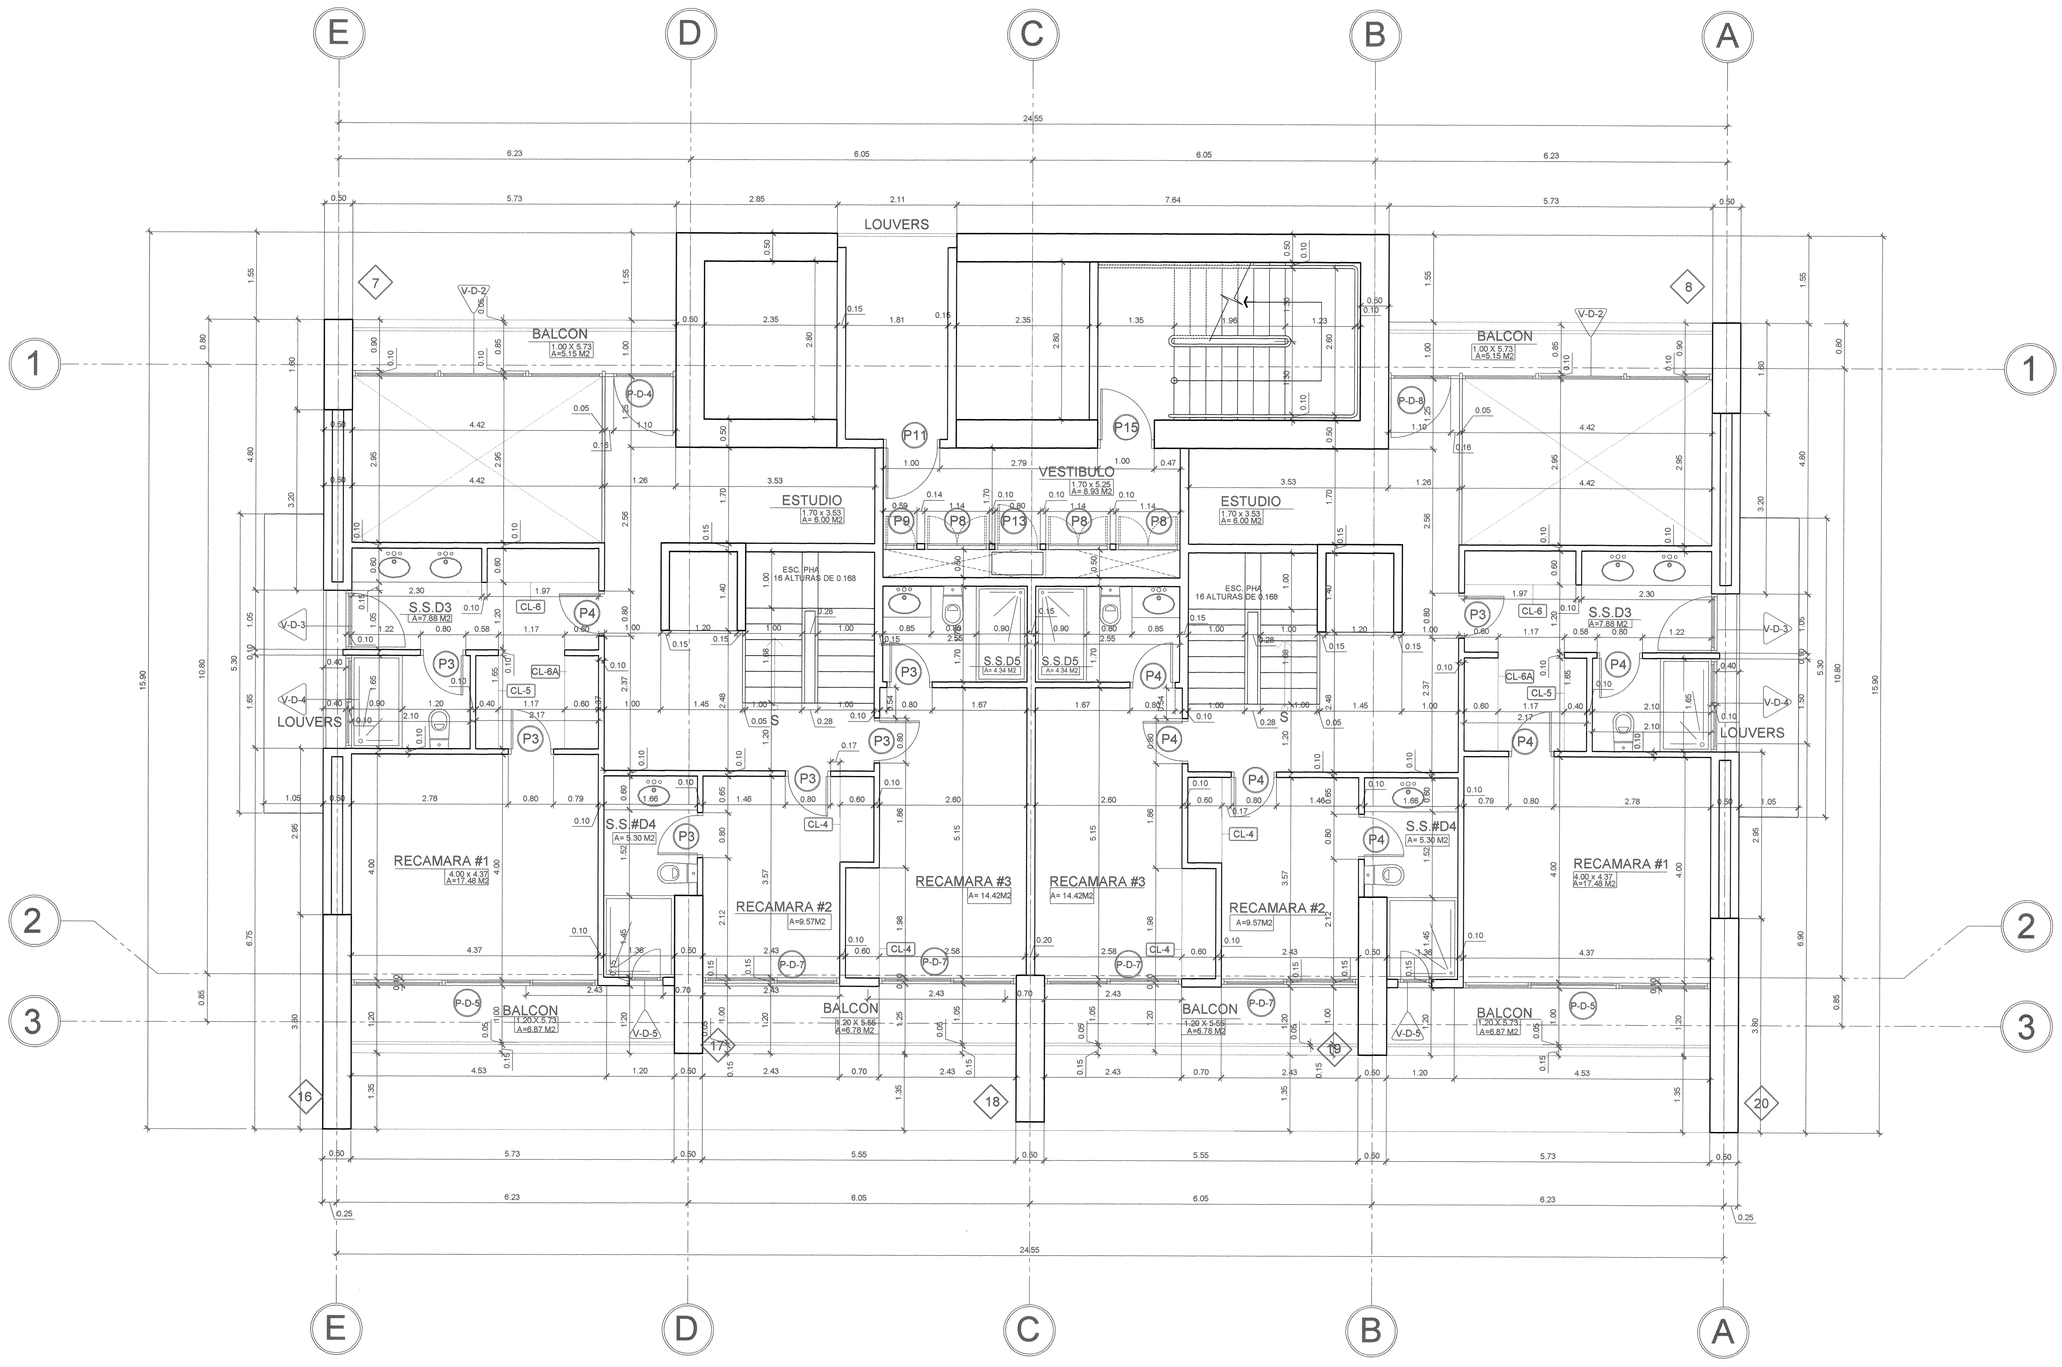

AR PLANTA ARQUITECTONICA TORRE B NIVEL +2700

ESCALA: 1:50

INGENIERIA MUNICIPAL
DISTRITO DE SAN CARLOS
APROBADO
INGENIERO MUNICIPAL
FECHA 22/8/11

Cuerpo de Bomberos
OFICINA DE SEGURIDAD
La Chorrera, 11 de agosto de 2011
Resolución No. 316 Plano No. 18-8
Se aprueba el registro de este plano por llenar las condiciones requeridas.
Jefe de la Oficina de Seguridad

FELIPE GONZALEZ LINCK
ARQUITECTO
LICENCIA No. 87-1488
LEY 15 DEL 26 DE ENERO DE 1959
JUNTA TECNICA DE INGENIERIA Y ARQUITECTURA

FELIPE GONZÁLEZ LINCK
ARQUITECTO
Tel: -- 66771610 – Fax 302-2457 | 64035839

DISEÑO ARQUITECTÓNICO	Arq. Vicente Cortes Arq. Igor Cortes
DESARROLLO	Arq. Igor Cortes Arq. Ilem Segismond Arq. Nancy Urriola
PROYECTO ESTRUCTURAL	Ing. Ricauter Bowen
PROYECTO ELÉCTRICO	Ing. Edgar Naranjo
PROYECTO DE PLOMERÍA	Ing. Gilberto Ayala

PROYECTO

Residencial El Palmar

UBICACIÓN

COMUNIDAD DE 'EL PALMAR'
DTTO. DE SAN CARLOS - CORREGIMIENTO DE SAN CARLOS
PANAMÁ

SOCIEDAD PROMOTORA

Inversiones Decuria, S.A.
Representante legal: IGOR CORTES
Número de cédula o pasaporte: BC054493

INGENIERÍA MUNICIPAL

PLANO

- PLANTA ARQUITECTONICA TORRE B
NIVEL 2700
ESCALA 1:50

ARCHIVO .DWG	NIVEL+2700
FECHA	DD/MM/AAAA
FECHA MODIFICACIÓN	DD/MM/AAAA

ARQUITECTURA	HOJA: 27	DE: 65

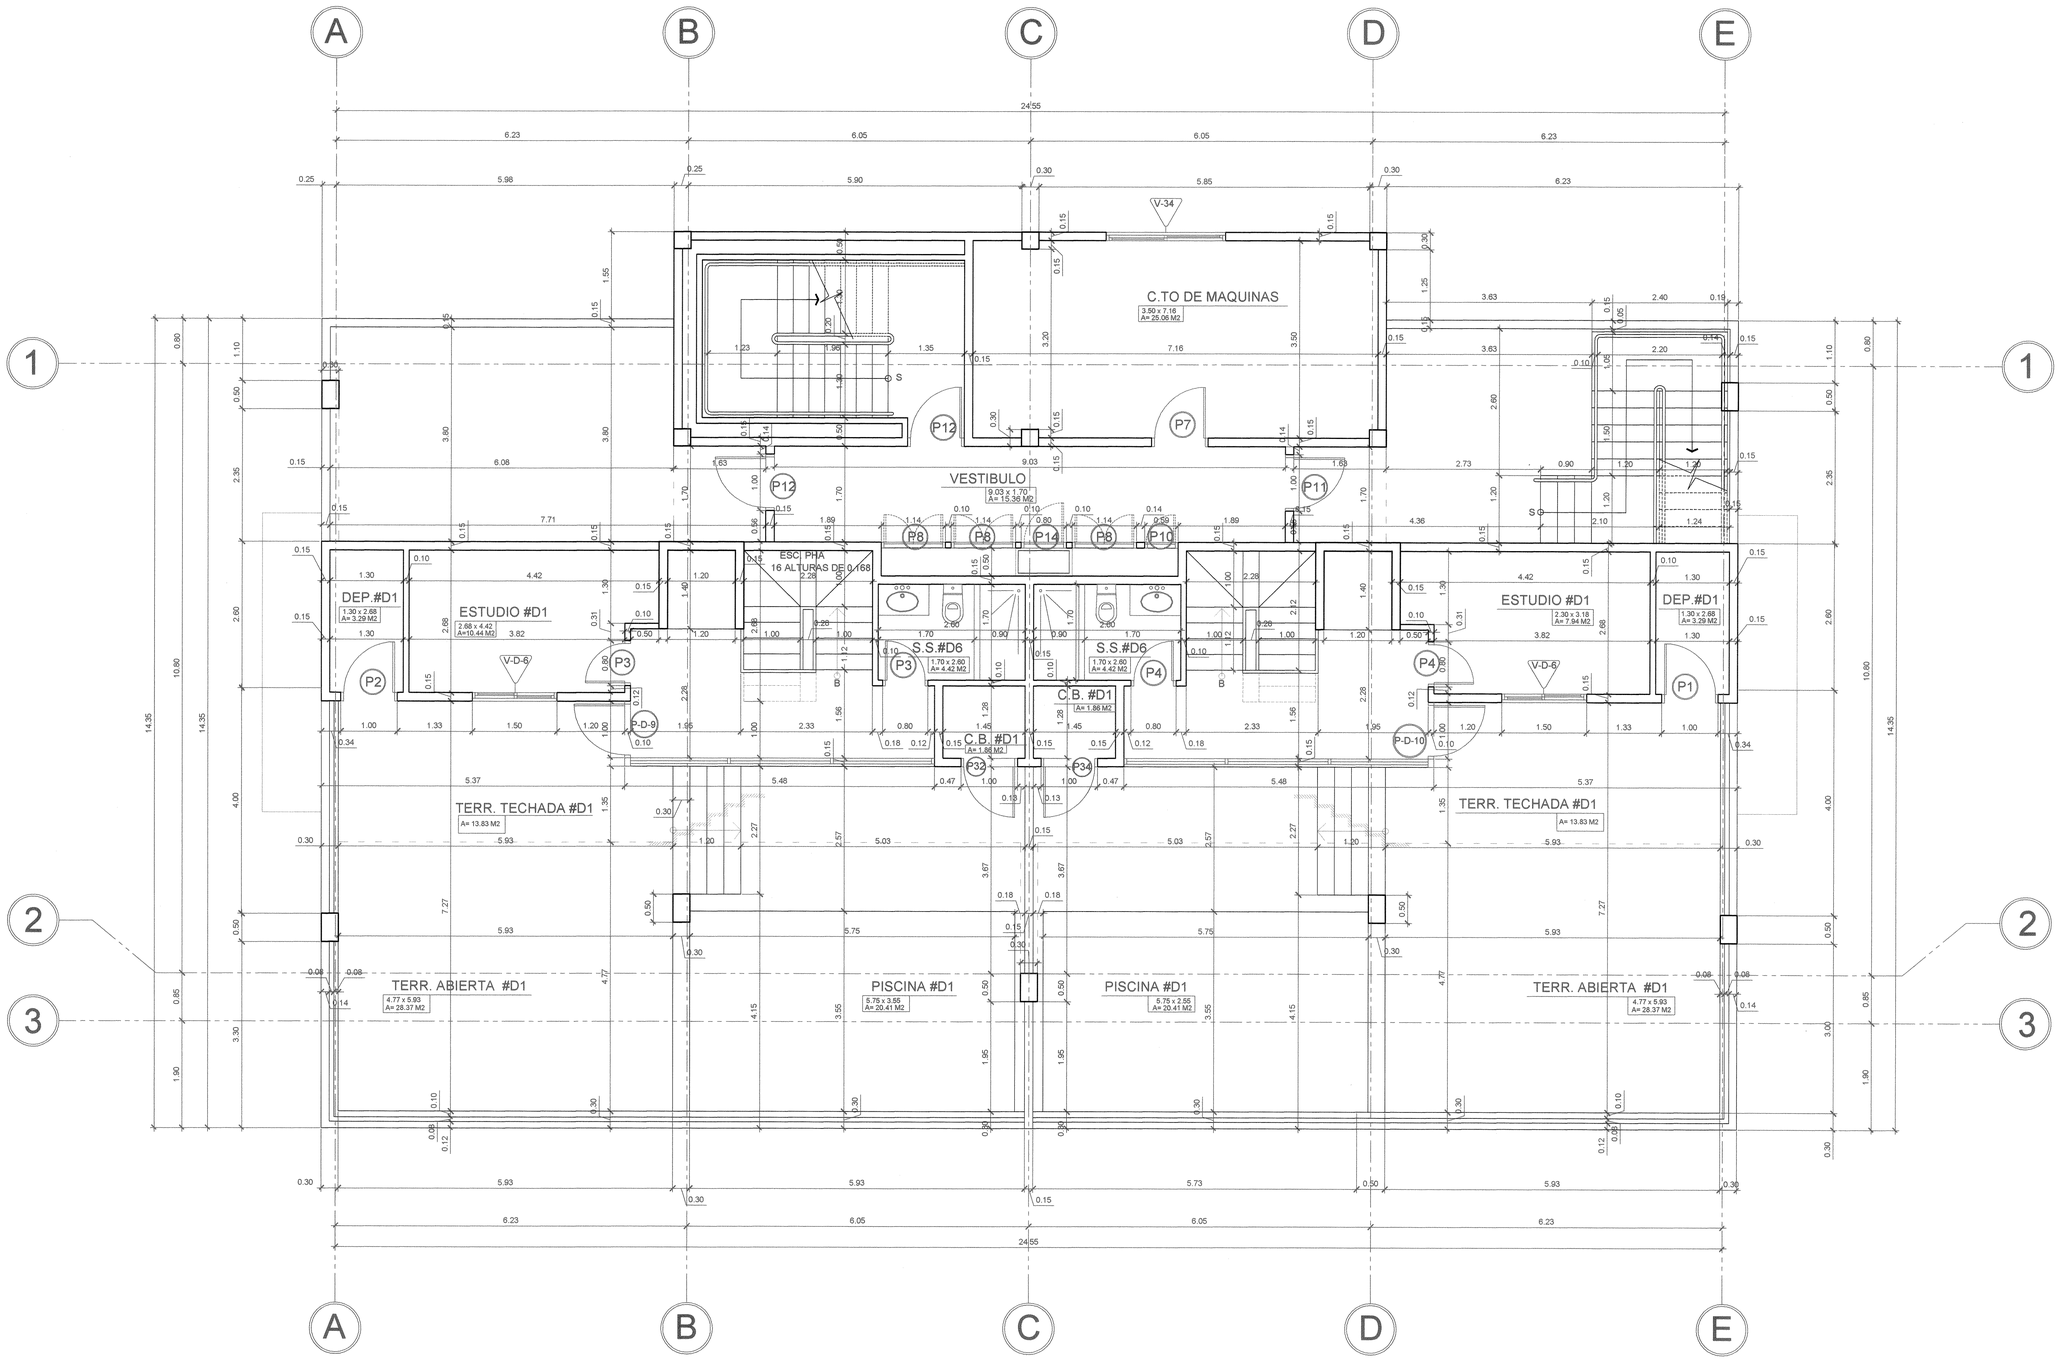

AR PLANTA ARQUITECTONICA TORRE A NIVEL +2800

ESCALA: 1:100

INGENIERIA MUNICIPAL
DISTRITO DE SAN CARLOS
APROBADO
FECHA 02/8/11
INGENIERO MUNICIPAL

Cuerpo de Bomberos
OFICINA DE SEGURIDAD
La Chorrera

La Chorrera, 11 de Agosto de 2011
Resolución No. 214-11 Plano No. 1678
Se aprueba el registro de este plano por llenar las condiciones requeridas.

Jefe de la Oficina de Seguridad

FELIPE GONZALEZ LINCK
ARQUITECTO
LICENCIA No. 87-01-182
LEY 15 DEL 26 DE ENERO DE 1959
JUNTA TECNICA DE INGENIERIA Y ARQUITECTURA

FELIFE GONZÁLEZ LINCK
ARQUITECTO
Tel: -- 66771610 -- Fax 392-2457 | 64035839

DISEÑO ARQUITECTÓNICO	Arq. Vicente Cortes Arq. Igor Cortes
DESARROLLO	Arq. Igor Cortes Arq. Ilem Segismond Arq. Nancy Urriola
PROYECTO ESTRUCTURAL	Ing. Ricauter Bowen
PROYECTO ELÉCTRICO	Ing. Edgar Naranjo
PROYECTO DE PLOMERÍA	Ing. Gilberto Ayala

PROYECTO

Residencial El Palmar

UBICACIÓN

COMUNIDAD DE "EL PALMAR"
DITTO. DE SAN CARLOS - CORREGIMIENTO DE SAN CARLOS
PANAMÁ

SOCIEDAD PROMOTORA

Inversiones Decuria, S.A.

Representante legal: IGOR CORTES
Número de cédula o pasaporte: BC054493

INGENIERÍA MUNICIPAL

PLANO

-PLANTA ARQUITECTONICA TORRE A
NIVEL 2800
ESCALA 1:50

ARCHIVO .DWG	NVIEL+2800
FECHA	30/08/2010
FECHA MODIFICACIÓN	DD/MM/AAAA

ARQUITECTURA | HOJA: 28 | DE: 65

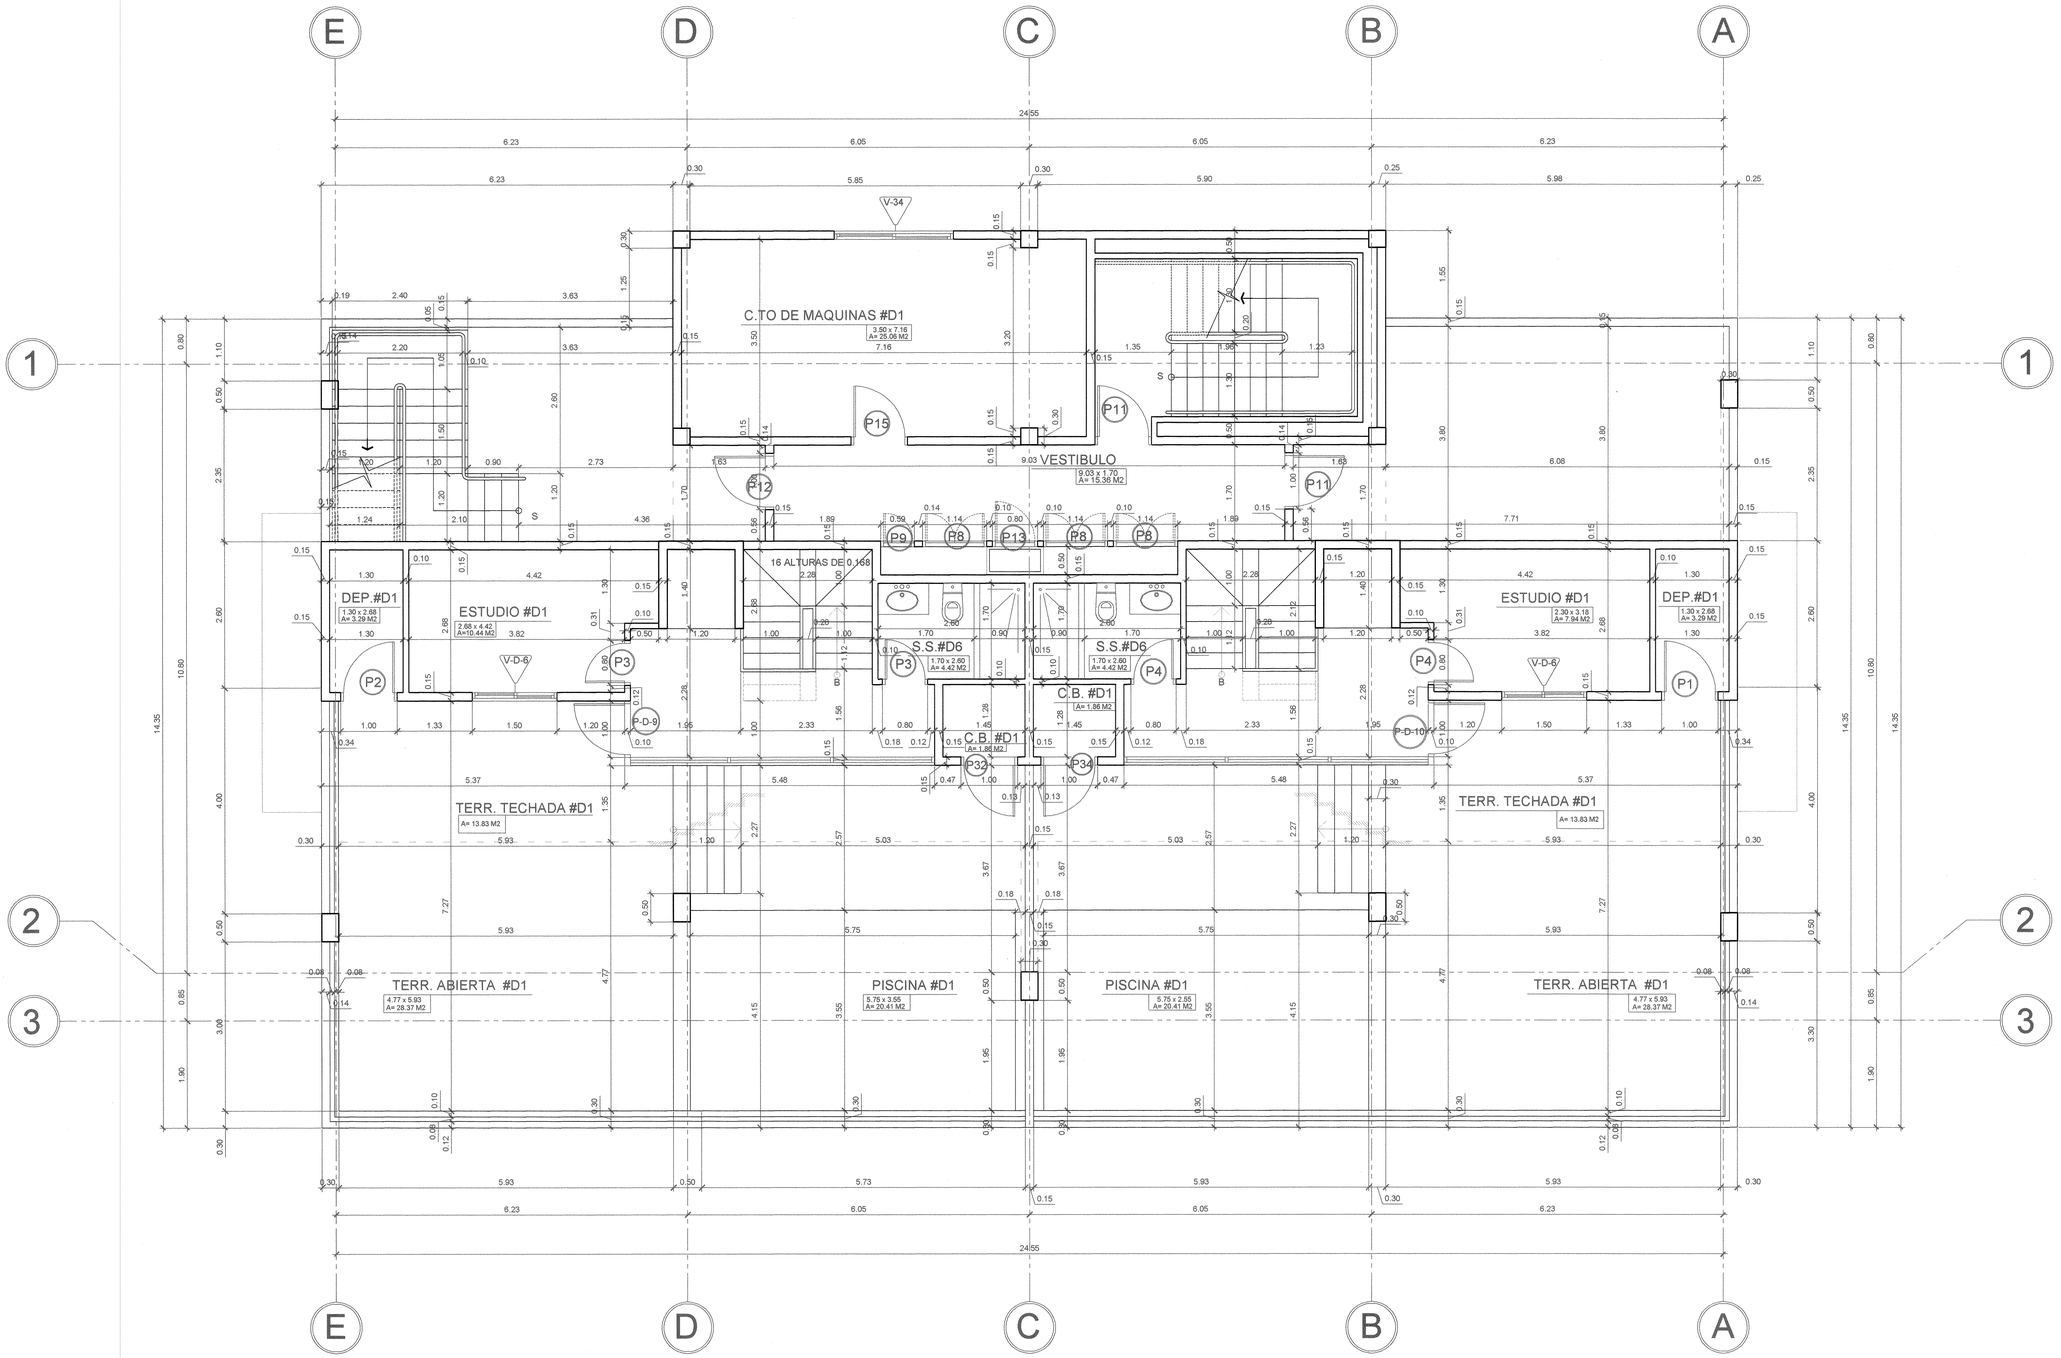

AR PLANTA ARQUITECTONICA TORRE B NIVEL +2800

ESCALA: 1:100

INGENIERIA MUNICIPAL
DISTRITO DE SAN CARLOS
APROBADO
INGENIERO MUNICIPAL
FECHA 22/8/11

Cuerpo de Bomberos
OFICINA DE SEGURIDAD
La Chorrera
La Chorrera, ... de 2011
Resolución No. ..... Plano No. .....
Se aprueba el registro de este plano por llenar las condiciones requeridas.

Jefe de la Oficina de Seguridad

FELIPE GONZALEZ LINCK
ARQUITECTO
LICENCIA No. 77-1-108
LEY 15 DEL 26 DE ENERO DE 1959
JUNTA TECNICA DE INGENIERIA Y ARQUITECTURA

FELIFE GONZÁLEZ LINCK
ARQUITECTO
Tel. -- 66771610 -- Fax 392-2457 | 64035839

DISEÑO ARQUITECTÓNICO	Arq. Vicente Cortes Arq. Igor Cortes
DESARROLLO	Arq. Igor Cortes Arq. Ilem Segismond Arq. Nancy Urriola
PROYECTO ESTRUCTURAL	Ing. Ricauter Bowen
PROYECTO ELÉCTRICO	Ing. Edgar Naranjo
PROYECTO DE PLOMERÍA	Ing. Gilberto Ayala

PROYECTO

Residencial El Palmar

UBICACIÓN

COMUNIDAD DE 'EL PALMAR'
DTTO. DE SAN CARLOS - CORREGIMIENTO DE SAN CARLOS
PANAMÁ

SOCIEDAD PROMOTORA

Inversiones Decuria, S.A.

Representante legal: IGOR CORTES
Número de cédula o pasaporte: 8C054493

INGENIERÍA MUNICIPAL

PLANO

-PLANTA ARQUITECTONICA TORRE B
NIVEL 2800
ESCALA 1:50

ARCHIVO .DWG	NVIEL+2800
FECHA	30/08/2010
FECHA MODIFICACIÓN	DD/MM/AAAA

ARQUITECTURA | HOJA: 29 | DE: 65

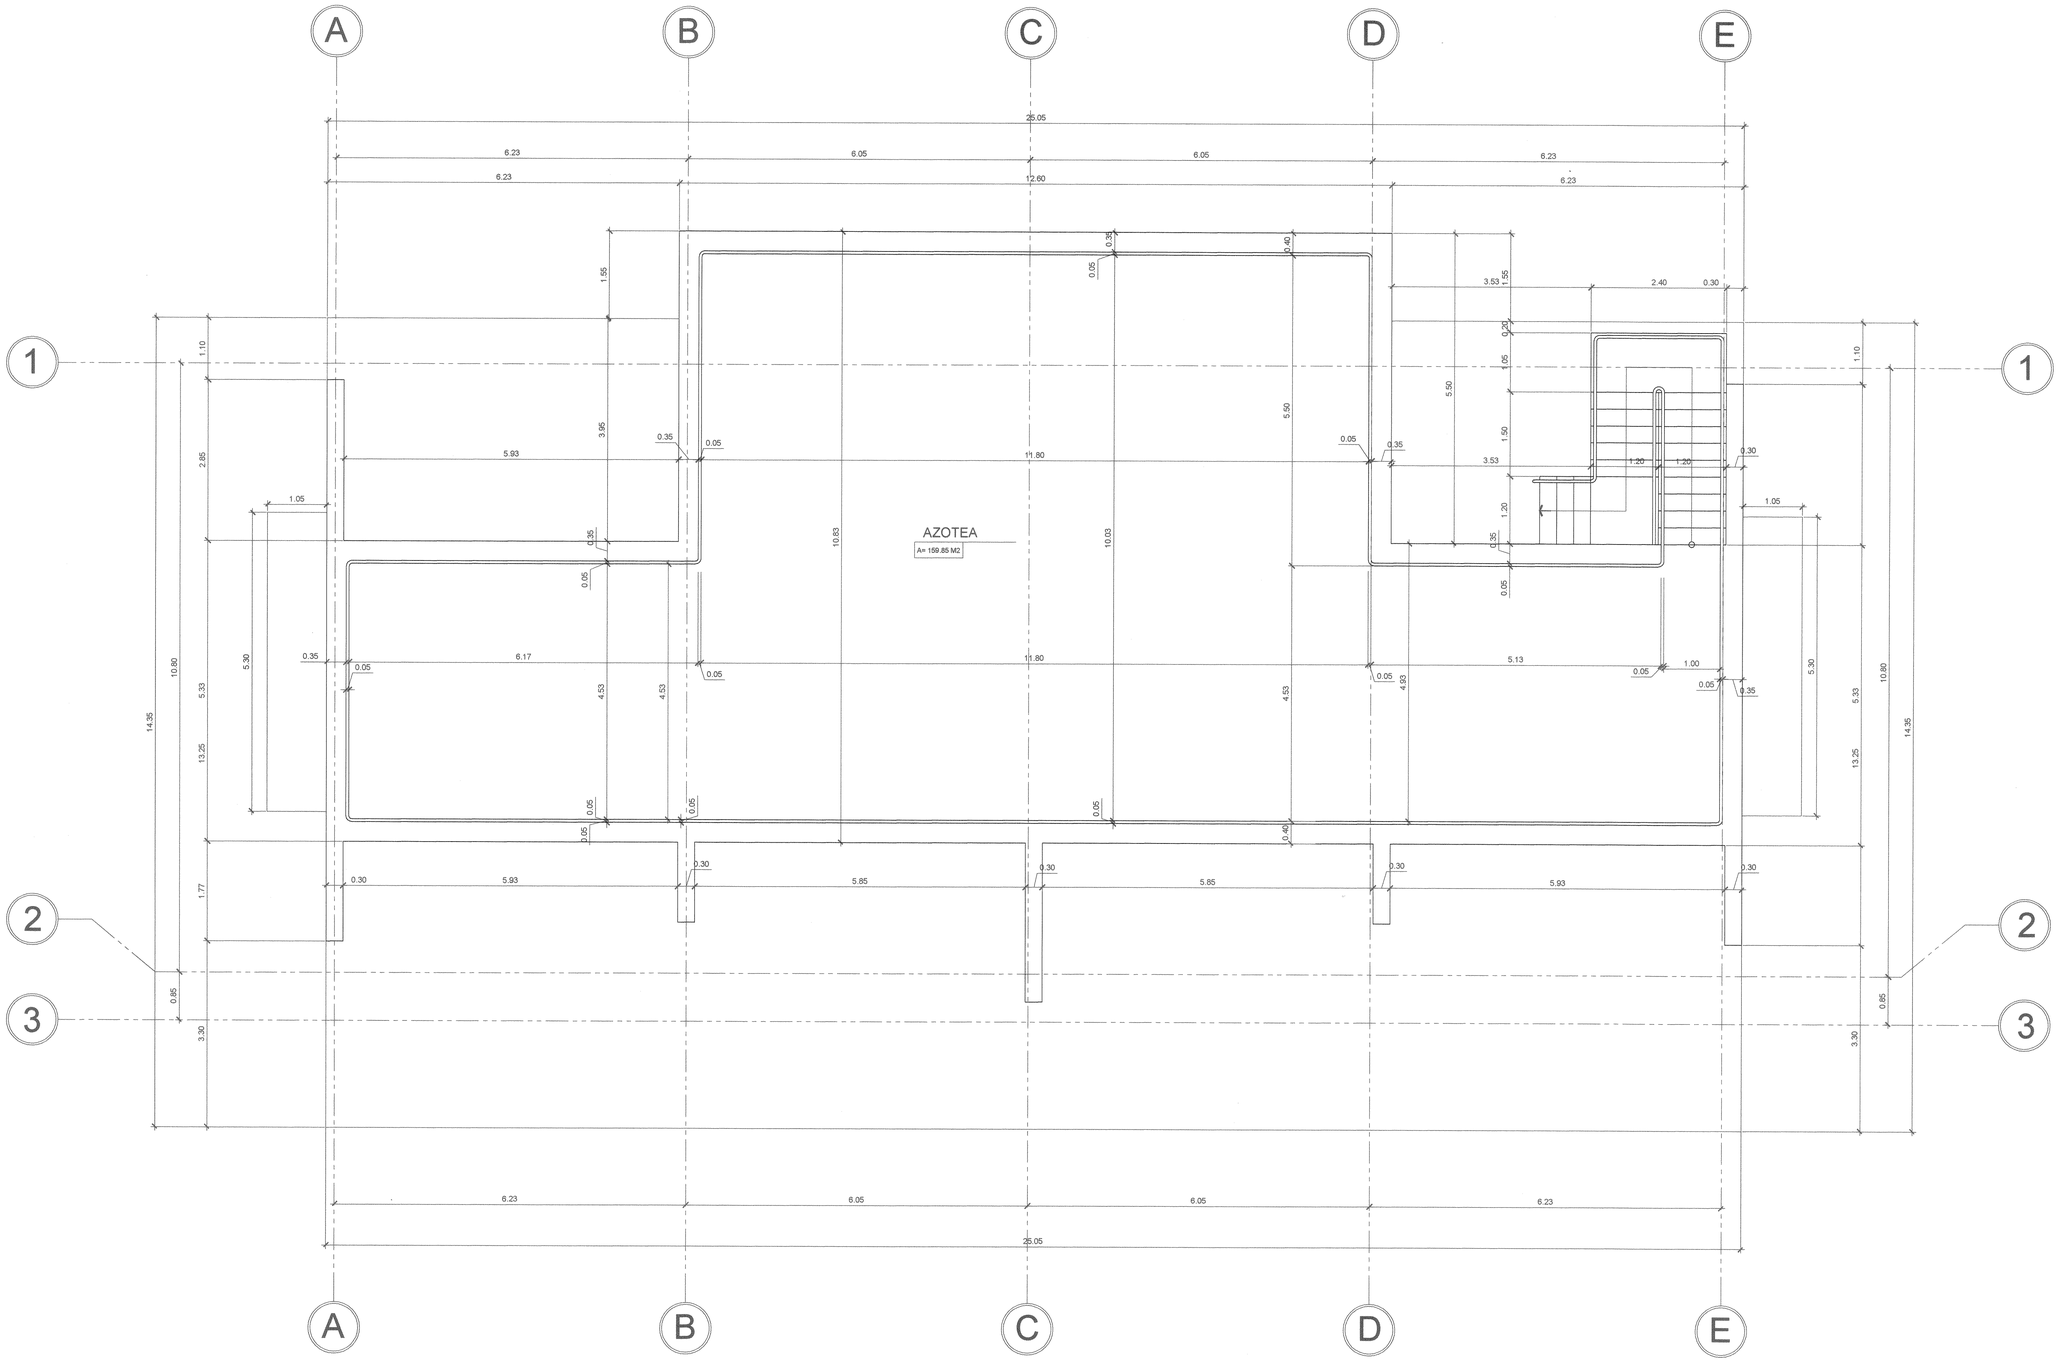

AR PLANTA ARQUITECTONICA TORRE A NIVEL + 2900

ESCALA: 1:50

INGENIERÍA MUNICIPAL
DISTRITO DE SAN CARLOS
APROBADO
INGENIERO MUNICIPAL
FECHA: 22/8/11

CUERPO DE BOMBEROS
OFICINA DE SEGURIDAD
La Chorrera
La Chorrera, 22 de Agosto de 2011
Resolución No. 376 (Planos No. 65)
Se aprueba el registro de este plano por llenar los condiciones requeridas.
Jefe de la Oficina de Seguridad

FELIPE GONZALEZ LINCK
ARQUITECTO
LICENCIA No. 771-198
LEY 15 DEL 26 DE ENERO DE 1959
JUNTA TECNICA DE INGENIERIA Y ARQUITECTURA

FELIFE GONZÁLEZ LINCK
ARQUITECTO
Tel. – 66771610 – Fax 392-2457 | 64035839

DISEÑO ARQUITECTÓNICO	Arq. Vicente Cortes Arq. Igor Cortes
DESARROLLO	Arq. Igor Cortes Arq. Ilem Segismond Arq. Nancy Urriola
PROYECTO ESTRUCTURAL	Ing. Ricauter Bowen
PROYECTO ELÉCTRICO	Ing. Edgar Naranjo
PROYECTO DE PLOMERÍA	Ing. Gilberto Ayala

PROYECTO

Residencial El Palmar

UBICACIÓN

COMUNIDAD DE 'EL PALMAR'
DTTO. DE SAN CARLOS - CORREGIMIENTO DE SAN CARLOS
PANAMÁ

SOCIEDAD PROMOTORA

Inversiones Decuria, S.A.

Representante legal: IGOR CORTES
Número de cédula o pasaporte: 8CD054493

INGENIERÍA MUNICIPAL

PLANO

- PLANTA ARQUITECTONICA TORRE A
NIVEL 2900
ESCALA 1:50

ARCHIVO .DWG	NIVEL+2900
FECHA	30/08/2010
FECHA MODIFICACIÓN	DD/MM/AAAA

ARQUITECTURA | HOJA: 30 | DE: 65

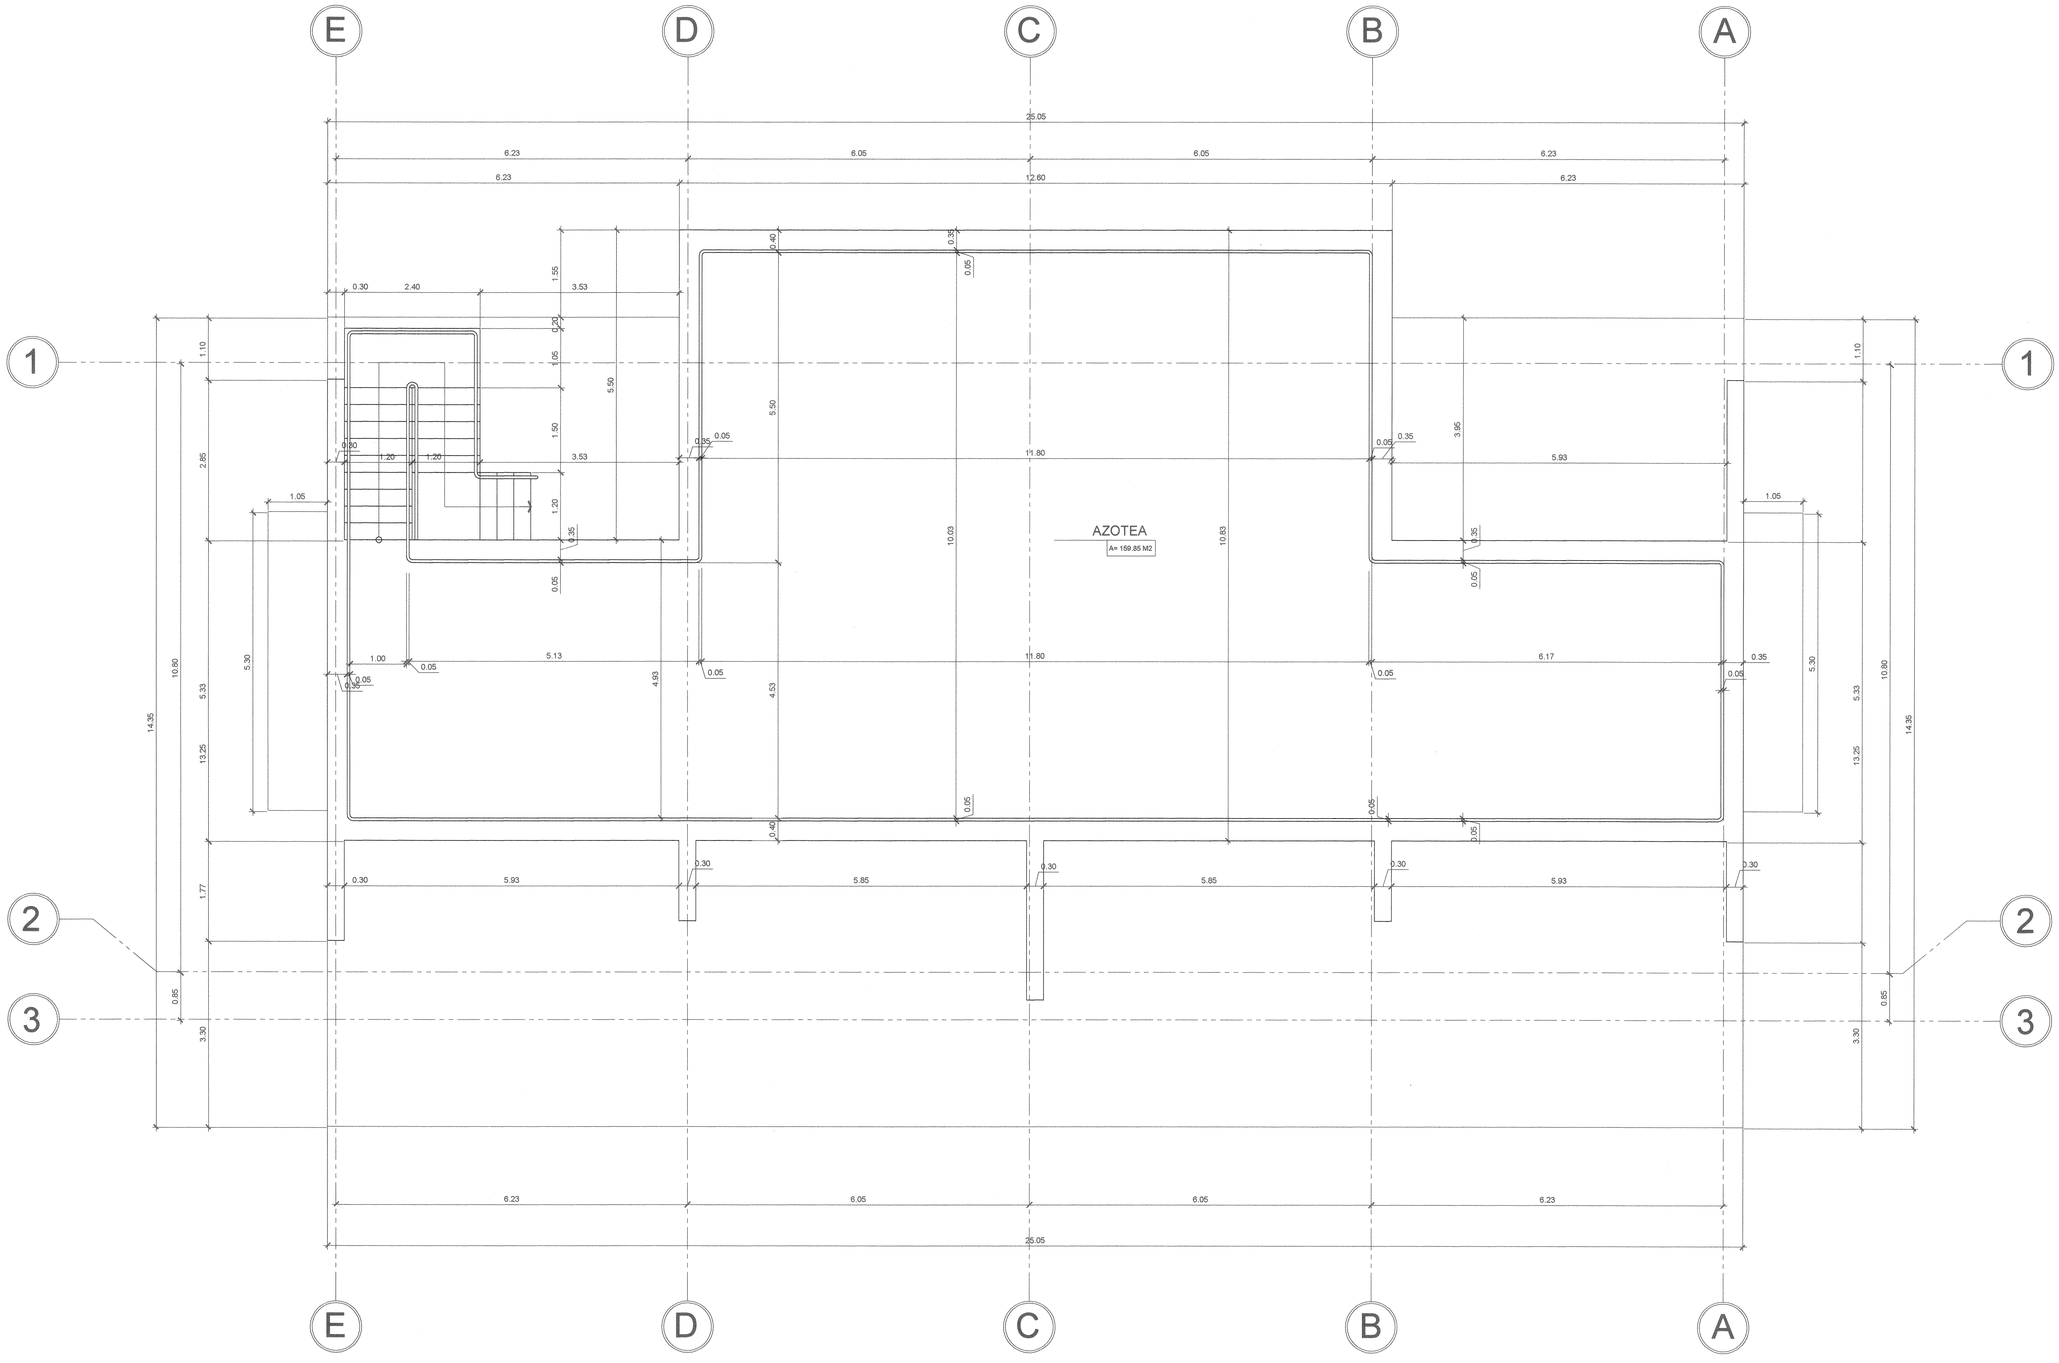

AR PLANTA ARQUITECTONICA TORRE B NIVEL + 2900

ESCALA: 1:50

INGENIERÍA MUNICIPAL
DISTRITO DE SAN CARLOS
APROBADO
24 de 11 11
INGENIERO MUNICIPAL
FECHA: 22/8/11

Cuerpo de Bomberos
OFICINA DE SEGURIDAD
La Chorrera
La Chorrera, ...11... de ...Agosto... de 2011
Resolución No. 346 (De 16-8-11)
Se aprueba el registro de conformidad con lo dispuesto por llenar las condiciones requerida.
Jefe de la Oficina de Seguridad

FELIPE GONZALEZ LINCK
ARQUITECTO
LICENCIA No. 87-1182
LEY 15 DEL 26 DE ENERO DE 1959
JUNTA TECNICA DE INGENIERIA Y ARQUITECTURA

FELIFE GONZÁLEZ LINCK
ARQUITECTO
Tel. -- 66771610 -- Fax 392-2457 | 64035839

DISEÑO ARQUITECTÓNICO	Arq. Vicente Cortes Arq. Igor Cortes
DESARROLLO	Arq. Igor Cortes Arq. Ilem Segismond Arq. Nancy Urriola
PROYECTO ESTRUCTURAL	Ing. Ricauter Bowen
PROYECTO ELÉCTRICO	Ing. Edgar Naranjo
PROYECTO DE PLOMERÍA	Ing. Gilberto Ayala

PROYECTO

Residencial El Palmar

UBICACIÓN

COMUNIDAD DE 'EL PALMAR'
DTTO. DE SAN CARLOS - CORREGIMIENTO DE SAN CARLOS
PANAMÁ

SOCIEDAD PROMOTORA

Inversiones Decuria, S.A.

Representante legal: IGOR CORTES
Número de cédula o pasaporte: 8C054493

INGENIERÍA MUNICIPAL

PLANO

- PLANTA ARQUITECTONICA TORRE B
NIVEL 2900
ESCALA 1:50

ARCHIVO .DWG	NIVEL+2900
FECHA	30/08/2010
FECHA MODIFICACIÓN	DD/MM/AAAA

ARQUITECTURA | HOJA: 31 | DE: 65

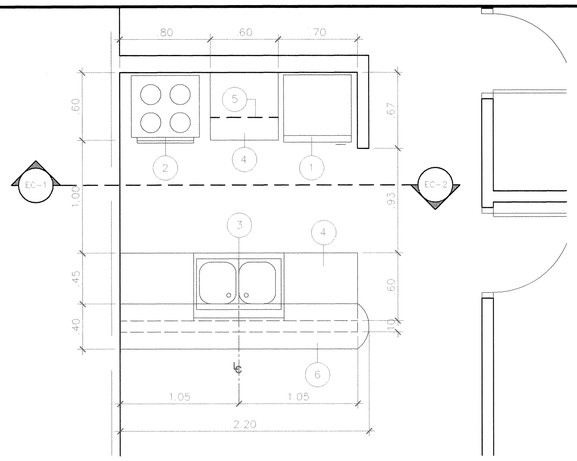

AMPL. COCINA A (N100 @ 2200)

ESCALA: 1:25

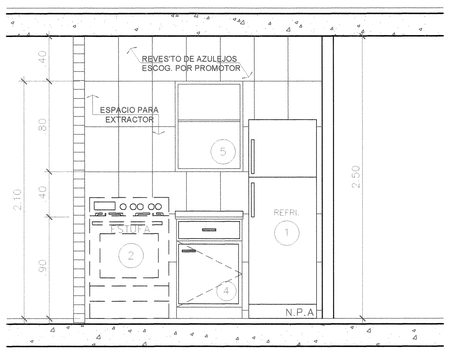

ELEVACION

COCINA A (N100 @ N2200) ESCALA: 1:25 EC-1

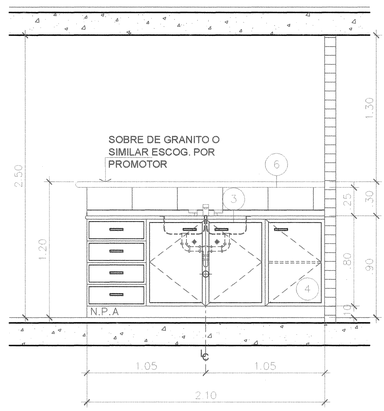

ELEVACION

COCINA A (N100 @ 2200) ESCALA: 1:25 EC-2

CUADRO DE CLAVES DE ACCESORIOS Y ARTEFACTOS DE COCINA

1	REFRIGERADORA
2	ESTUFA
3	FREGADOR DOBLE
3A	FREGADOR SENCILLO (TIPO BAR)
4	MUEBLE INFERIOR DE PUERTA Y GAVETAS DE MADERA
5	MUEBLE SUPERIOR DE PUERTAS Y TABILLA INTERIOR EN MADERA
6	MUEBLE DESAYUNADOR / MOSTRADOR
7	TINA DE LAVAR

NOTAS IMPORTANTE DE COCINA

EL DISEÑO O MODULACION FINAL DE LOS MUEBLES DE COCINA, SERA ESCOGIDO POR EL PROMOTOR DEL PROYECTO

ESTA ES UNA PROPUESTA DE MODULACION QUE PODRA SER CAMBIADA PREVIA APROBACION DEL PROMOTOR

INGENIERIA MUNICIPAL
DISTRITO DE SAN CARLOS
APROBADO
21 de 11 de 11
INGENIERO MUNICIPAL
FECHA 22/8/11

Cuerpo de Bomberos
OFICINA DE SEGURIDAD
La Chorrera
La Chorrera, 11 de Agosto de 2011
Resolución No. 3-11 Plano No. 11-48
Se aprueba el registro de este plano por llenar las condiciones requeridas

Dirección de la Oficina de Seguridad

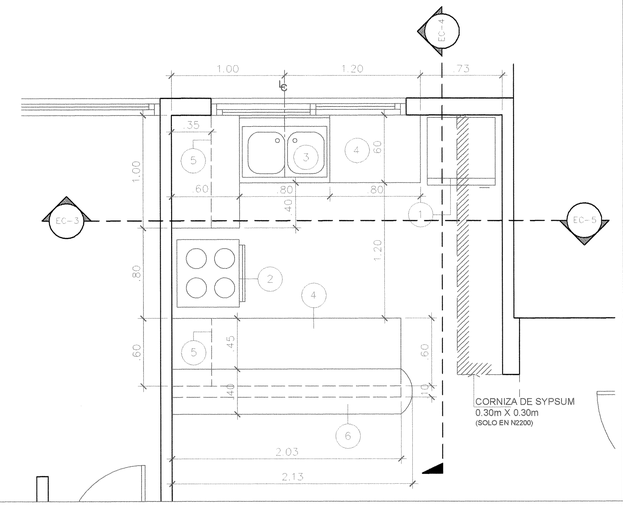

AMPL. COCINA B (N100 @ 2200)

ESCALA: 1:25

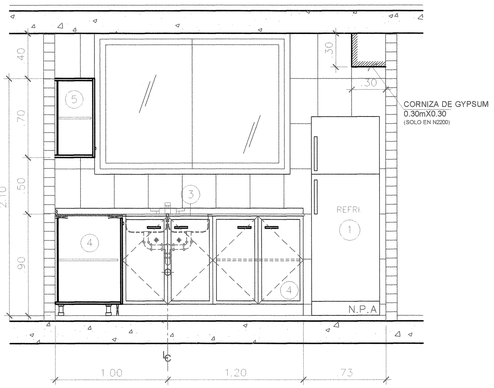

ELEVACION

COCINA B (N100 @ N2200) ESCALA: 1:25 EC-3

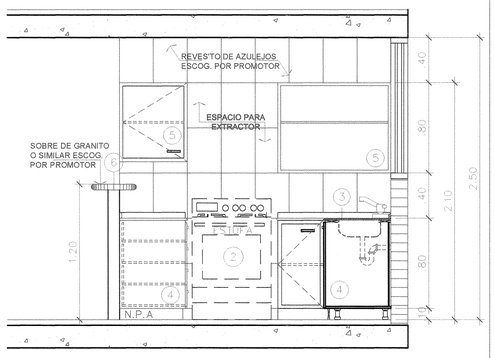

ELEVACION

COCINA B (N100 @ N2200) ESCALA: 1:25 EC-4

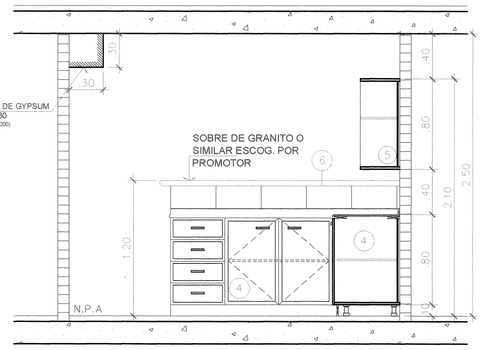

ELEVACION

COCINA B (N100 @ N2200) ESCALA: 1:25 EC-5

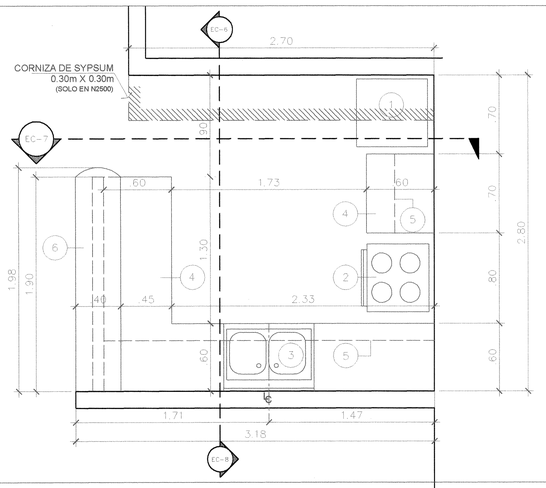

AMPL. COCINA C (N2300 @ 2500)

ESCALA: 1:25

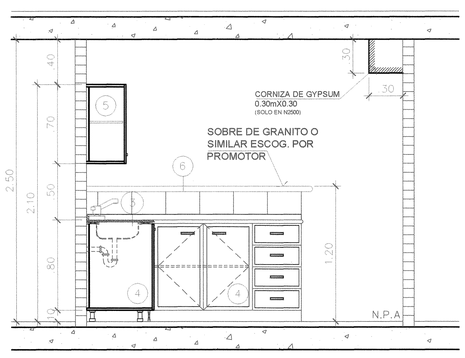

ELEVACION

COCINA C (N2300 @ N2500) ESCALA: 1:25 EC-6

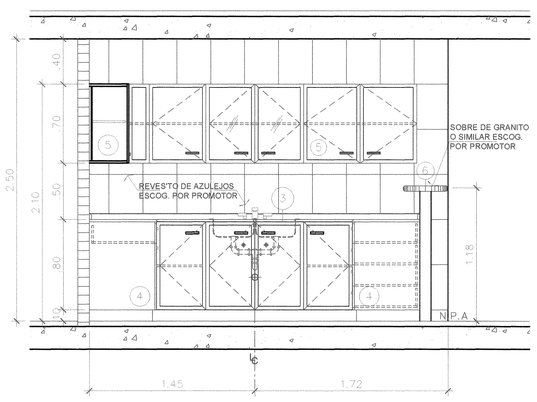

ELEVACION

COCINA C (N2300 @ N2500) ESCALA: 1:25 EC-7

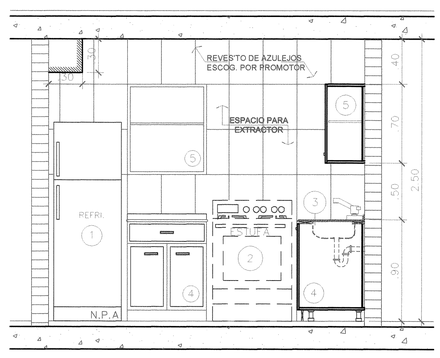

ELEVACION

COCINA C (N2300 @ N2500) ESCALA: 1:25 EC-8

FELIFE GONZALEZ LINCK
ARQUITECTO
LICENCIA No. 87-11108
LEY 15 DEL 26 DE ENERO DE 1959
JUNTA TECNICA DE INGENIERIA Y ARQUITECTURA

FELIFE GONZÁLEZ LINCK
ARQUITECTO
Tel. -- 66771610 -- Fax 392-2457 | 64035859

DISEÑO ARQUITECTÓNICO	Arq. Vicente Cortes Arq. Igor Cortes
DESARROLLO	Arq. Igor Cortes Arq. Ilem Segismond Arq. Nancy Urriola
PROYECTO ESTRUCTURAL	Ing. Ricauter Bowen
PROYECTO ELÉCTRICO	Ing. Edgar Naranjo
PROYECTO DE PLOMERÍA	Ing. Gilberto Ayala

PROYECTO

Residencial El Palmar

UBICACIÓN

COMUNIDAD DE "EL PALMAR"
DTTO. DE SAN CARLOS - CORREGIMIENTO DE SAN CARLOS
PANAMÁ

SOCIEDAD PROMOTORA

Inversiones Decuria, S.A.

Representante legal: IGOR CORTES
Número de cédula o pasaporte: BC054493

INGENIERÍA MUNICIPAL

PLANO

- DETALLE DE COCINAS A, B, C
NIVEL 100 @ 2500
ESCALA 1:25

ARCHIVO .DWG	COCINAS
FECHA	30/08/2010
FECHA MODIFICACIÓN	DD/MM/AAAA

ARQUITECTURA | HOJA: 32 | DE: 65

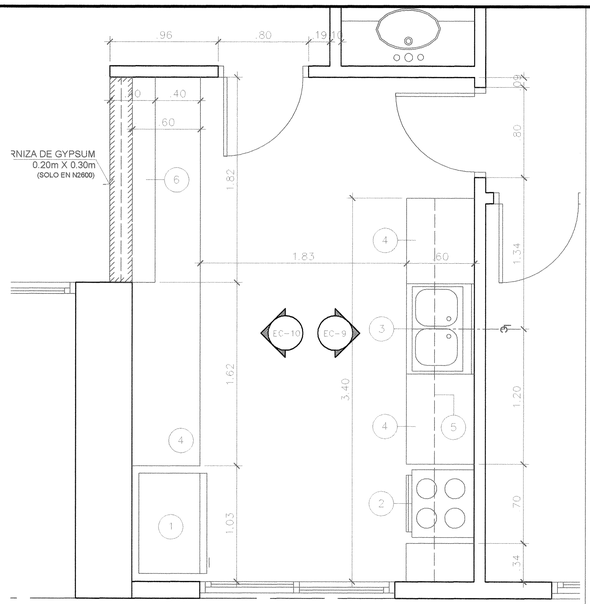

AMPL. COCINA D (N2600)

ESCALA: 1:25

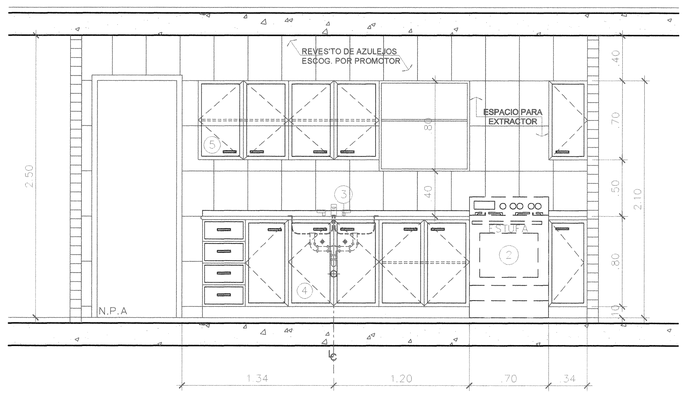

ELEVACION

COCINA D (N2600) ESCALA: 1:25 EC-9

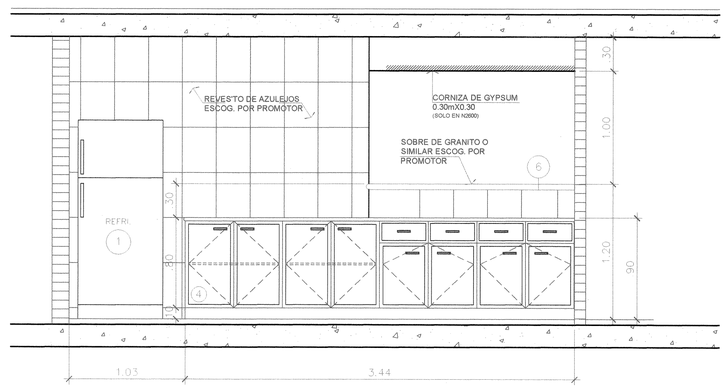

ELEVACION

COCINA D (N2600) ESCALA: 1:25 EC-10

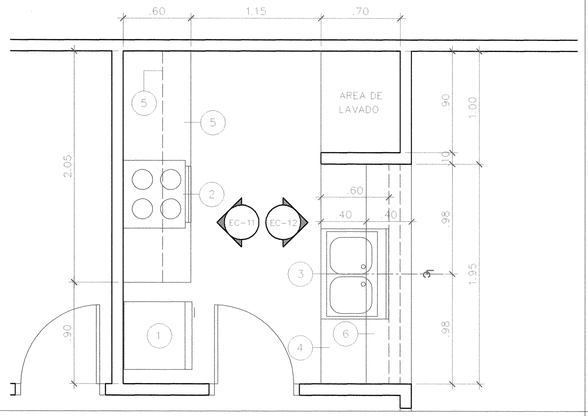

AMPL. COCINA E (N-100@-400)

ESCALA: 1:25

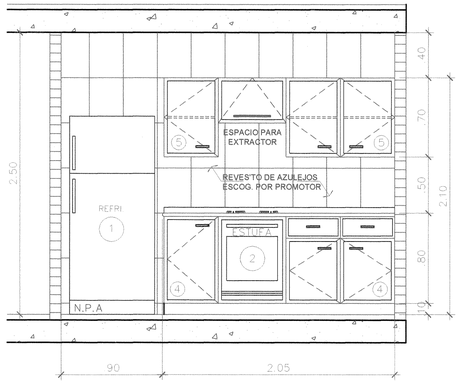

ELEVACION

COCINA E (N-100@-400) ESCALA: 1:25 EC-11

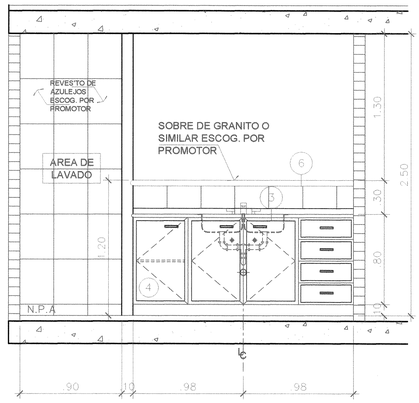

ELEVACION

COCINA D (N-100@-400) ESCALA: 1:25 EC-12

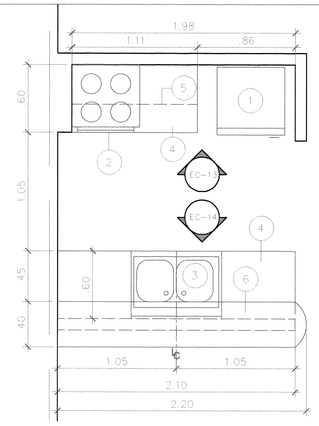

AMPL. COCINA F (N-100 @ -400)

ESCALA: 1:25

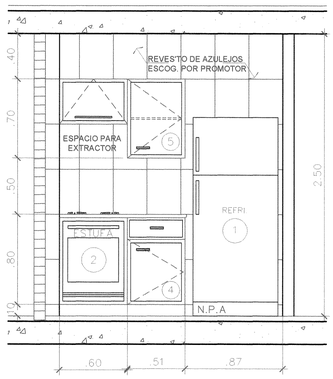

ELEVACION

COCINA F (N-100 @ -400) ESCALA: 1:25 EC-13

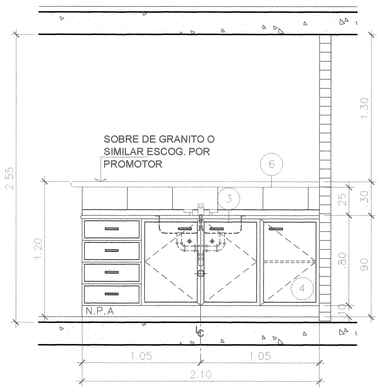

ELEVACION

COCINA F (N-100 @ -400) ESCALA: 1:25 EC-14

CUADRO DE CLAVES DE ACCESORIOS Y ARTEFACTOS DE COCINA

1	REFRIGERADORA
2	ESTUFA
3	FREGADOR DOBLE
3A	FREGADOR SENCILLO (TIPO BAR)
4	MUEBLE INFERIOR DE PUERTA Y GAVETAS DE MADERA
5	MUEBLE SUPERIOR DE PUERTAS Y TABLILLA INTERIOR EN MADERA
6	MUEBLE DESAYUNADOR / MOSTRADOR
7	PILA DE LAVAR

NOTAS IMPORTANTE DE COCINA

EL DISEÑO O MODULACION FINAL DE LOS MUEBLES DE COCINA, SERA ESCOGIDO POR EL PROMOTOR DEL PROYECTO.

ESTA ES UNA PROPUESTA DE MODULACION QUE PODRA SER CAMBIADA PREVIA APROBACION DEL PROMOTOR

INGENIERIA MUNICIPAL
DISTRITO DE SAN CARLOS
APROBADO
INGENIERO MUNICIPAL
FECHA 22/8/11

Cuerpo de Bomberos
OFICINA DE SEGURIDAD
La Chorrera

La Chorrera, 11 de agosto de 2011
Se aprueba No. 346 Placa No. 1665
Siempre y cuando el registro de este plano cumpla con las condiciones requeridas.

Jefe de la Ofic. de Seguridad

FELIPE GONZALEZ LINCK
ARQUITECTO
LICENCIA No. 87-1188
LEY 15 DEL 26 DE ENERO DE 1959
JUNTA TECNICA DE INGENIERIA Y ARQUITECTURA

FELIFE GONZÁLEZ LINCK
ARQUITECTO
Tel. – 66771610 – Fax 392-2457 | 64035839

DISEÑO ARQUITECTÓNICO	Arq. Vicente Cortes Arq. Igor Cortes
DESARROLLO	Arq. Igor Cortes Arq. Ilem Segismond Arq. Nancy Urriola
PROYECTO ESTRUCTURAL	Ing. Ricauter Bowen
PROYECTO ELÉCTRICO	Ing. Edgar Naranjo
PROYECTO DE PLOMERÍA	Ing. Gilberto Ayala

PROYECTO

Residencial El Palmar

UBICACIÓN

COMUNIDAD DE 'EL PALMAR'
DTTO. DE SAN CARLOS - CORREGIMIENTO DE SAN CARLOS
PANAMÁ

SOCIEDAD PROMOTORA

Inversiones Decuria, S.A.

Representante legal: IGOR CORTES
Número de cédula o pasaporte: 8C054493

INGENIERÍA MUNICIPAL

PLANO

- DETALLE DE COCINAS D, E, F
NIVEL 2600 Y NIVEL -100 @ -400
ESCALA 1:25

ARCHIVO .DWG	COCINAS
FECHA	30/08/2010
FECHA MODIFICACIÓN	DD/MM/AAAA

ARQUITECTURA | HOJA: 33 | DE: 65

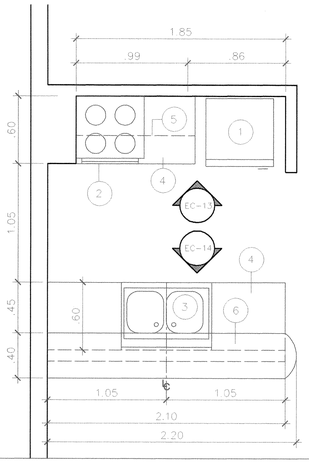

AMPL. COCINA G (N-100 @ -400)

TORRE A ESCALA: 1:25

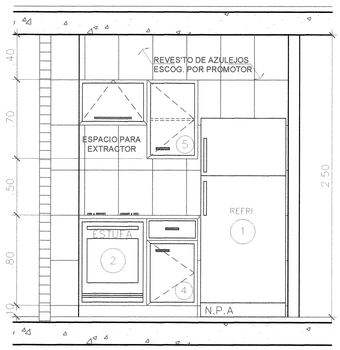

ELEVACION

COCINA G (N-100 @ -400) ESCALA: 1:25 EC-13

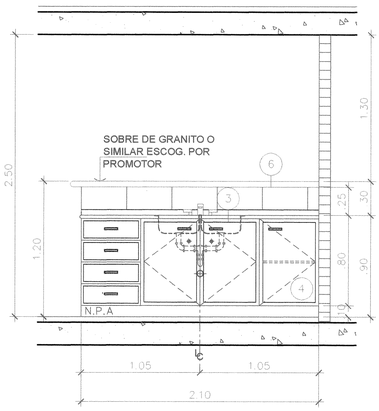

ELEVACION

COCINA G (N-100 @ -400) ESCALA: 1:25 EC-14

CUADRO DE CLAVES DE ACCESORIOS Y ARTEFACTOS DE COCINA

1	REFRIGERADORA
2	ESTUFA
3	FREGADOR DOBLE
3A	FREGADOR SENCILLO (TIPO BAR)
4	MUEBLE INFERIOR DE PUERTA Y GAVETAS DE MADERA
5	MUEBLE SUPERIOR DE PUERTAS Y TABILLA INTERIOR EN MADERA
6	MUEBLE DESAYUNADOR / MOSTRADOR
7	TINA DE LAVAR

NOTAS IMPORTANTE DE COCINA

EL DISEÑO O MODULACION FINAL DE LOS MUEBLES DE COCINA, SERA ESCOGIDO POR EL PROMOTOR DEL PROYECTO.

ESTA ES UNA PROPUESTA DE MODULACION QUE PODRA SER CAMBIADA PREVIA APROBACION DEL PROMOTOR.

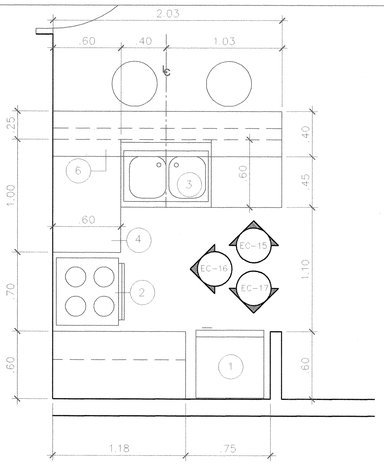

AMPL. COCINA #1 (N000)

TORRE A ESCALA: 1:25

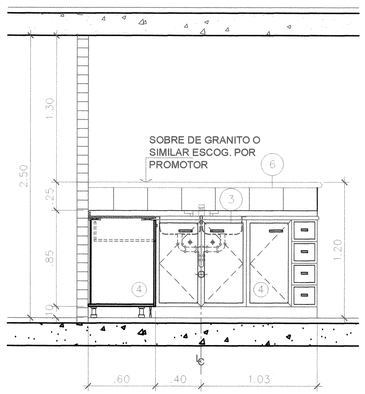

ELEVACION

COCINA #1 (N000) ESCALA: 1:25 EC-18

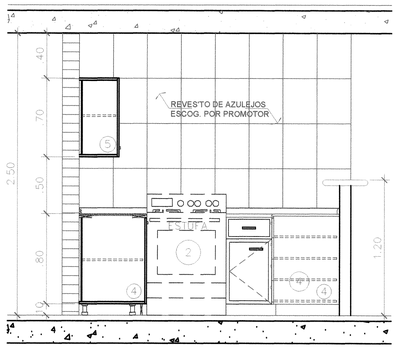

ELEVACION

COCINA #1 (N000) ESCALA: 1:25 EC-19

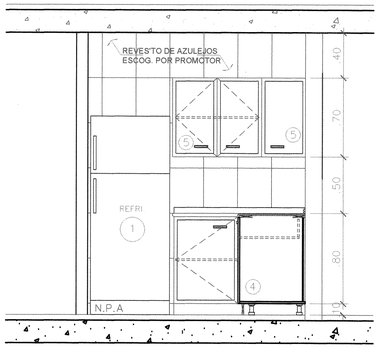

ELEVACION

COCINA #1 (N000) ESCALA: 1:25 EC-20

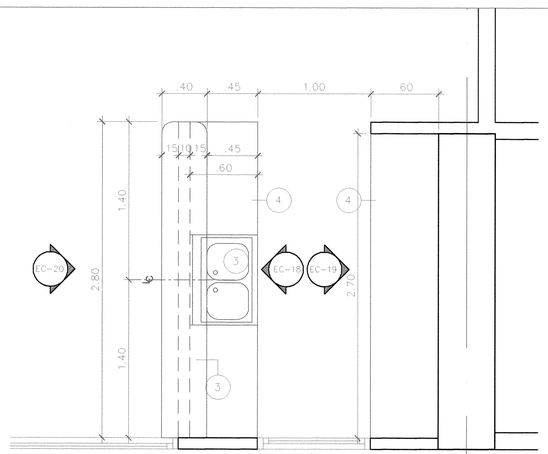

AMPL. COCINA - SALON DE FIESTAS (N000)

TORRE A ESCALA: 1:25

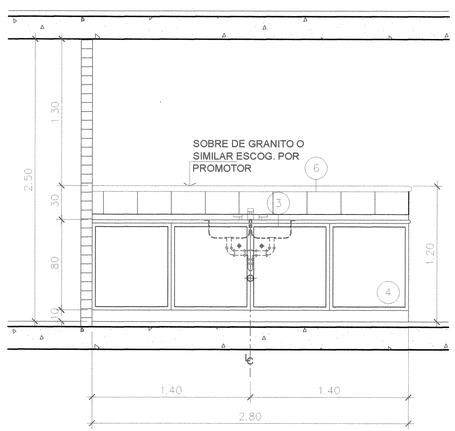

ELEVACION

COCINA-SALON DE FIESTAS (N000) ESCALA: 1:25 EC-18

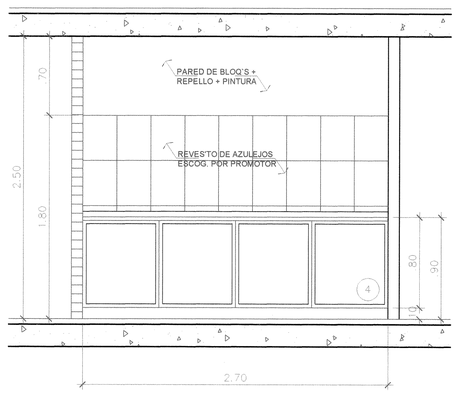

ELEVACION

COCINA-SALON DE FIESTAS (N000) ESCALA: 1:25 EC-19

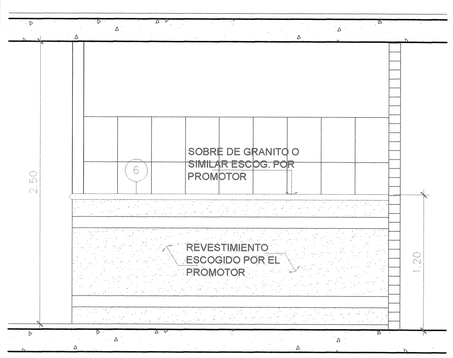

ELEVACION

COCINA-SALON DE FIESTAS (N000) ESCALA: 1:25 EC-20

INGENIERIA MUNICIPAL
DISTRITO DE SAN CARLOS
APROBADO
INGENIERO MUNICIPAL
FECHA 22/8/11

Cuerpo de Bomberos
OFICINA DE SEGURIDAD
La Chorrera
La Chorrera, ... de ... de 20...
Resolución No. ...
Se aprueba el registro de ese plano por llenar las condiciones requeridas.
Jefe de la Oficina de Seguridad

FELIPE GONZALEZ LINCK
ARQUITECTO
LICENCIA No. 77-1-113
LEY 15 DEL 26 DE ENERO DE 1959
JUNTA TECNICA DE INGENIERIA Y ARQUITECTURA

FELIFE GONZÁLEZ LINCK
ARQUITECTO
Tel. – 66771610 – Fax 392-2457 | 64035839

DISEÑO ARQUITECTÓNICO	Arq. Vicente Cortes Arq. Igor Cortes
DESARROLLO	Arq. Igor Cortes Arq. Ilem Segismond Arq. Nancy Urriola
PROYECTO ESTRUCTURAL	Ing. Ricauter Bowen
PROYECTO ELÉCTRICO	Ing. Edgar Naranjo
PROYECTO DE PLOMERÍA	Ing. Gilberto Ayala

PROYECTO

Residencial El Palmar

UBICACIÓN

COMUNIDAD DE 'EL PALMAR'
DITO. DE SAN CARLOS - CORREGIMIENTO DE SAN CARLOS
PANAMÁ

SOCIEDAD PROMOTORA

Inversiones Decuria, S.A.
Representante legal: IGOR CORTES
Número de cédula o pasaporte: 8C054493

INGENIERÍA MUNICIPAL

PLANO

- DETALLE DE COCINAS G Y P.B
NIVEL 00 @ -400
ESCALA 1:25

ARCHIVO .DWG	COCINAS
FECHA	30/08/2010
FECHA MODIFICACIÓN	DD/MM/AAAA

ARQUITECTURA HOJA: 34 DE: 65

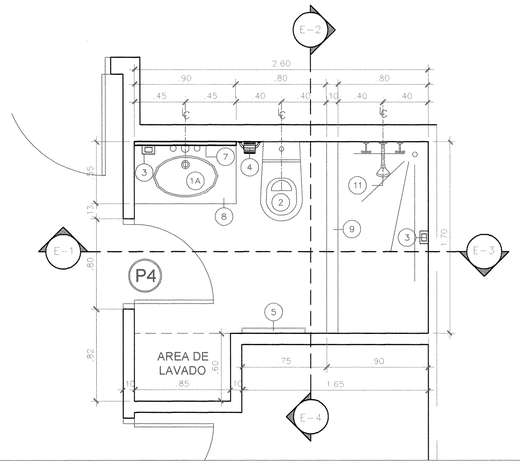

AMPL. SERV. SANITARIOS A1 - NIVEL 100 @ 2200

ESCALA: 1:25

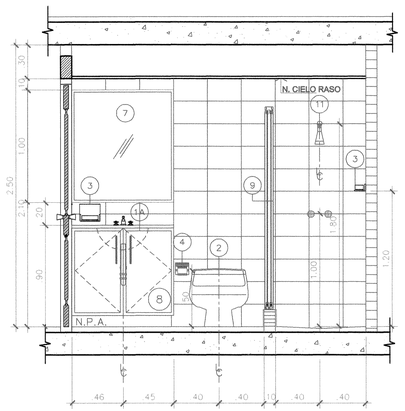

ELEVACION

SERV. SANT. A1 (N100 @ 2200) ESCALA: 1:25 E-1

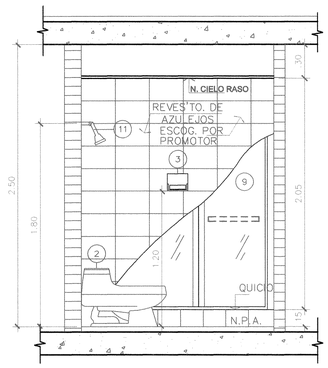

ELEVACION

SERV. SANT. A1 (N100 @ 2200) ESCALA: 1:25 E-2

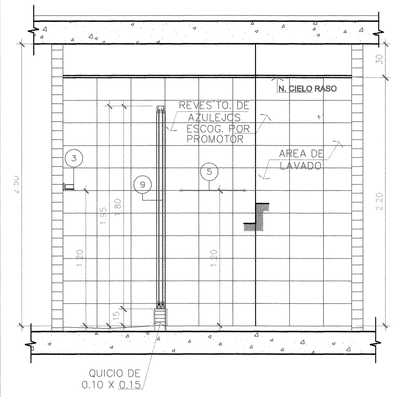

ELEVACION

SERV. SANT. A1 (N100 @ 2200) ESCALA: 1:25 E-3

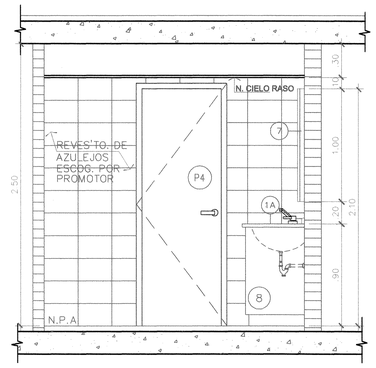

ELEVACION

SERV. SANT. A1 (N100 @ 2200) ESCALA: 1:25 E-4

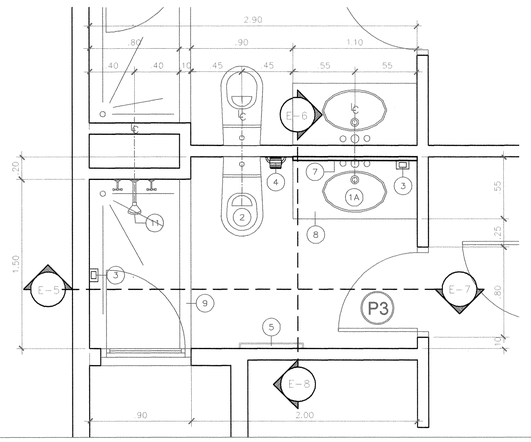

AMPL. SERV. SANITARIOS B1, C1 - NIVEL 100 @ 2500

ESCALA: 1:25

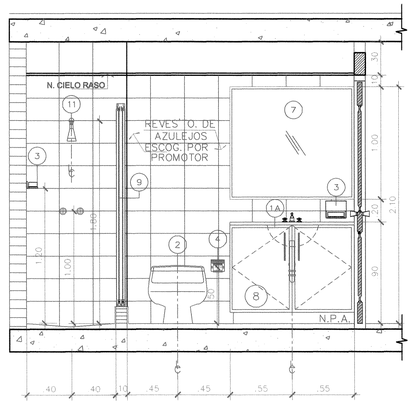

ELEVACION

SERV. SANT. B1, C1 (N100 @ 2500) ESCALA: 1:25 E-5

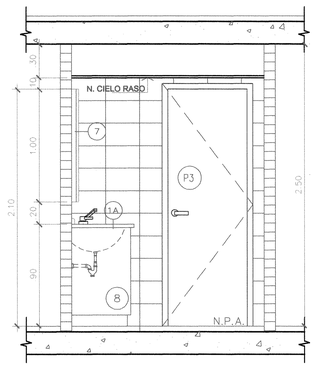

ELEVACION

SERV. SANT. B1, C1 (N100 @ 2500) ESCALA: 1:25 E-6

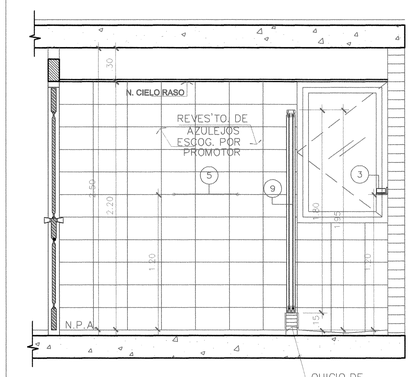

ELEVACION

SERV. SANT. B1, C1 (N100 @ 2500) ESCALA: 1:25 E-7

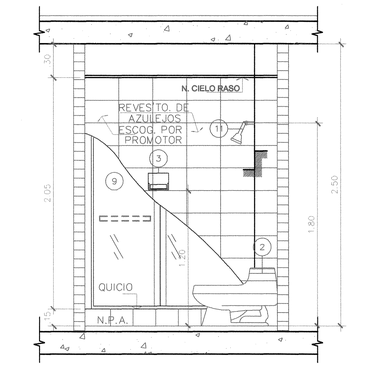

ELEVACION

SERV. SANT. B1, C1 (N100 @ 2500) ESCALA: 1:25 E-8

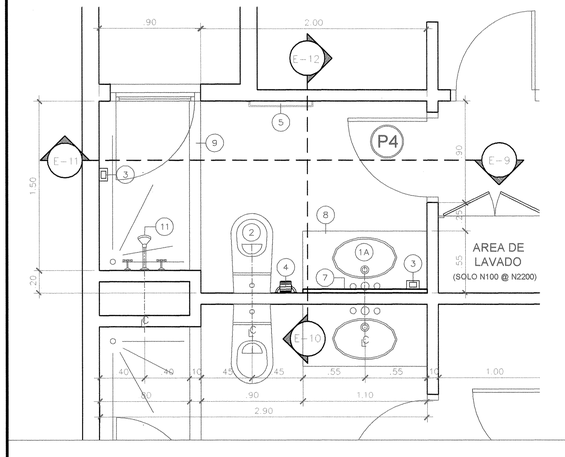

AMPL. SERV. SANITARIOS B2, C2 - NIVEL 100 @ 2500

ESCALA: 1:25

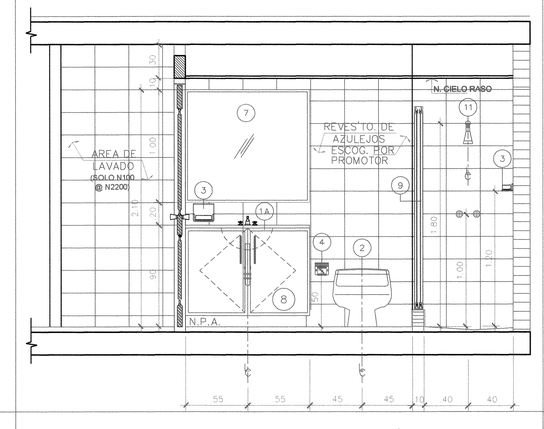

ELEVACION

SERV. SANT. B2, C2 (N100 @ 2500) ESCALA: 1:25 E-9

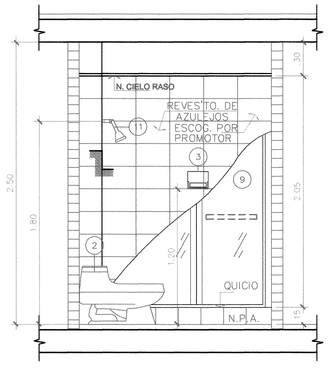

ELEVACION

SERV. SANT. B2, C2 (N100 @ 2500)

ESCALA: 1:25 E-10

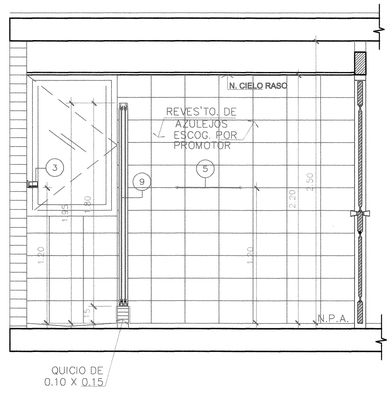

ELEVACION

SERV. SANT. B2, C2 (N100 @ 2500) ESCALA: 1:25 E-11

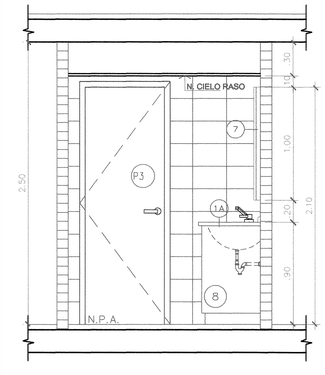

ELEVACION

SERV. SANT. B2,C2 (N100 @ 2500) ESCALA: 1:25 E-12

INGENIERIA MUNICIPAL
DISTRITO DE SAN CARLOS
APROBADO
22/11/11
INGENIERO MUNICIPAL
FECHA 22/8/11

Cuerpo de Bomberos
OFICINA DE SEGURIDAD
La Chorrera
La Chorrera, 11 de Agosto de 2011
Resolución No. 348 (Plano No. 10-48)
Se aprueba el registro de este plano con las siguientes condiciones requeridas
Jefe de la Oficina de Seguridad

FELIPE GONZALEZ LINCK
ARQUITECTO
LICENCIA No. 7271-188
LEY 15 DEL 26 DE ENERO DE 1959
JUNTA TECNICA DE INGENIERIA Y ARQUITECTURA

FELIPE GONZÁLEZ LINCK
ARQUITECTO
Tel. – 06771610 – Fax 392-2457 | 64035839

DISEÑO ARQUITECTÓNICO	Arq. Vicente Cortes Arq. Igor Cortes
DESARROLLO	Arq. Igor Cortes Arq. Ilem Segismond Arq. Nancy Urriola
PROYECTO ESTRUCTURAL	Ing. Ricauter Bowen
PROYECTO ELÉCTRICO	Ing. Edgar Naranjo
PROYECTO DE PLOMERÍA	Ing. Gilberto Ayala

PROYECTO

Residencial El Palmar

UBICACIÓN

COMUNIDAD DE 'EL PALMAR'
DTTO. DE SAN CARLOS - CORREGIMIENTO DE SAN CARLOS
PANAMÁ

SOCIEDAD PROMOTORA

Inversiones Decuria, S.A.
Representante legal: IGOR CORTES
Número de cédula o pasaporte: 8-054-493

INGENIERÍA MUNICIPAL

PLANO

- DETALLE DE SERVICIOS SANITARIOS APTOS A, B, C - NIVEL 100 @ 2500
ESCALA 1:25

ARCHIVO .DWG	BAÑOS A,B,C
FECHA	30/08/2010
FECHA MODIFICACIÓN	DD/MM/AAAA

ARQUITECTURA | HOJA: 35 | DE: 65

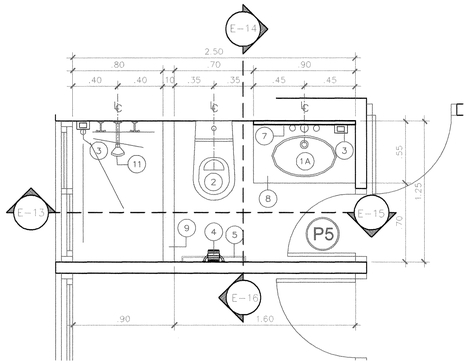

AMPL. SERV. SANITARIOS C3 - NIV.2300@2500

ESCALA: 1:25

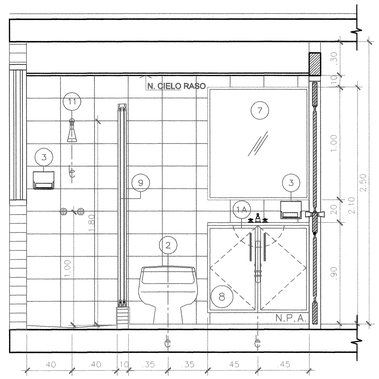

ELEVACION

SERV. SANT. C3 (N2300@2500) ESCALA: 1:25 E-13

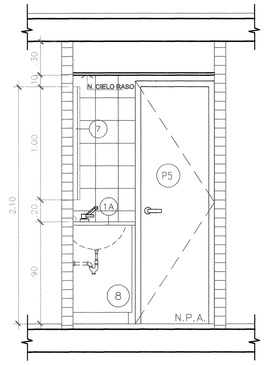

ELEVACION

SERV. SANT. C3 (N2300@2500) ESCALA: 1:25 E-14

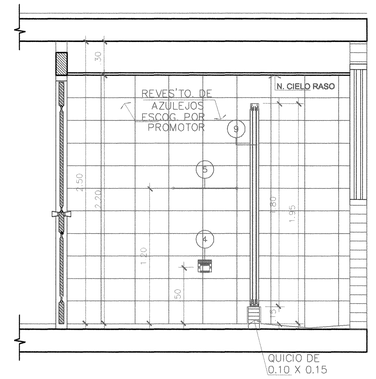

ELEVACION

SERV. SANT. C3 (N2300@2500) ESCALA: 1:25 E-15

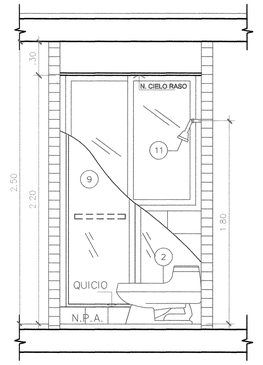

ELEVACION

SERV. SANT. C3 (N2300@2500) ESCALA: 1:25 E-16

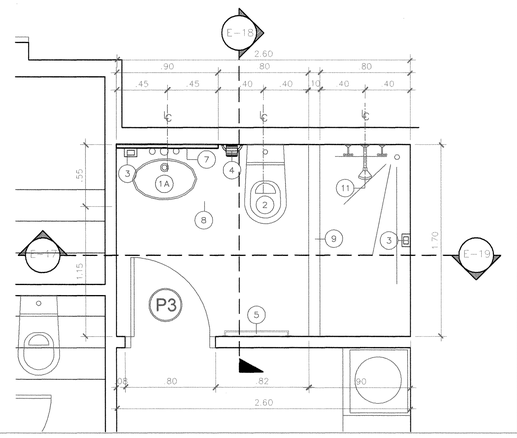

AMPL. SERV. SANITARIOS D1, D6 - N 2600 / N2800

ESCALA: 1:25

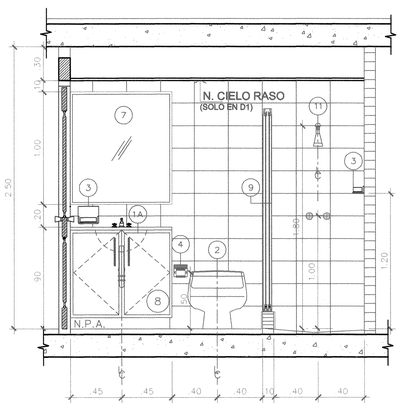

ELEVACION

SERV. SANT. D1, D6 (N2600/N2800) ESCALA: 1:25 E-17

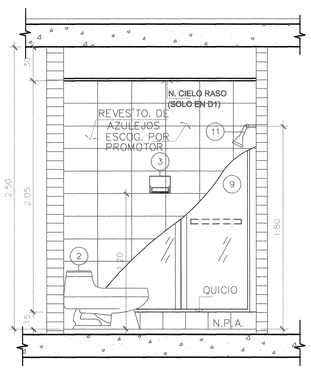

ELEVACION

SERV. SANT. D1,D6 (N2600/N2800) ESCALA: 1:25 E-18

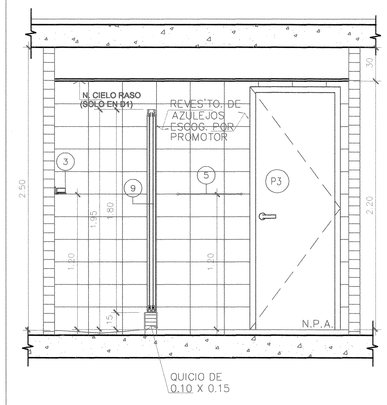

ELEVACION

SERV. SANT. D1, D6 (N2600/N2800) ESCALA: 1:25 E-19

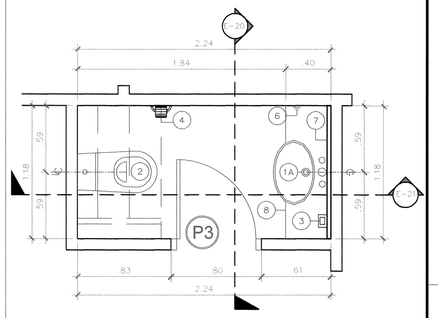

AMPL. SERV. SANITARIOS D2 - NIV 2600

ESCALA: 1:25

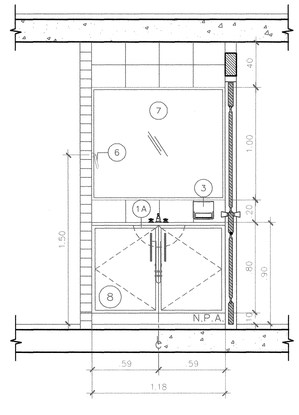

ELEVACION

SERV. SANT. D2 (N2600) ESCALA: 1:25 E-20

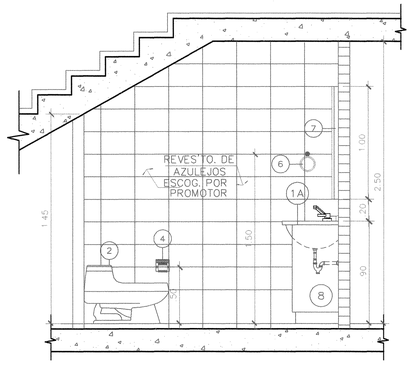

ELEVACION

SERV. SANT. D2 (N2600) ESCALA: 1:25 E-21

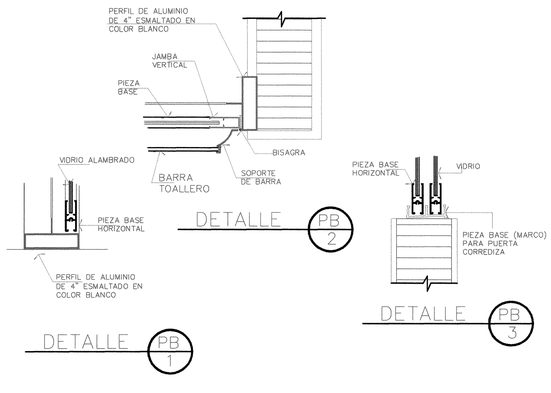

DETALLES DE PUERTAS DE BAÑO

ESCALA 1:5

CUADRO DE ARTEFACTOS SANITARIOS Y ACCESORIOS

1A	LAVAMANOS INCESA STANDARD O SIMILAR EMBUTIDO EN MUEBLE EN COLOR BLANCO O COLORES NEUTRALES
1B	LAVAMANOS DE PEDESTAL MARCA INCESA STANDARD O SIMILAR EN COLOR BLANCO O COLORES NEUTRALES
1C	LAVAMANOS DE PARED MARCA INCESA STANDARD O SIMILAR EN COLOR BLANCO O COLORES NEUTRALES
2	INODORO DE UNA PIEZA MARCA INCESA STANDARD O SIMILAR EN COLOR BLANCO O COLORES NEUTRALES
2A	INODORO FLUXOMETRO EN COLOR BLANCO O COLORES NEUTRALES
3	JABONERA / CEPILLERA TIPO SUPERFICIAL, SEGUN COLOR DE ARTEFACTOS
4	PAPELERA STANDARD
5	TUBO TOALLERO DE 24" CROMADO SUPERFICIAL
6	ARO TOALLERO (PARA TOALLA DE MANOS) JUNTO AL LAVAMANOS, VER UBICACION EN PLANTA Y ELEVACIONES
7	ESPEJO
8	MUEBLE SEGUN DISEÑO Y MATERIAL ESCOGIDO POR EL ARQ.
9	PUERTAS DE BAÑO CORREDIZA CON MARCOS DE ALUMINIO ESMALTADO BLANCO Y VIDRIO
10	PUERTAS DE BAÑO ABATIBLE CON MARCOS DE ALUMINIO ESMALTADO BLANCO Y VIDRIO
11	DUCHA
12	DISPENSADOR DE PAPEL TOALLA
13	DISPENSADOR DE PAPEL HIGIENICO
14	DISPENSADOR DE JABON DE MANOS
15	BARRA PARA MINUSVALIDOS

NOTAS IMPORTANTES DE BAÑOS

EL REVESTIMIENTO DE AZULEJOS SERAN IMPORTADOS EN COLOR Y DISEÑO ESCOGIDO POR EL PROMOTOR SEGUN ALTURAS INDICADAS EN LOS DETALLES

SERA DECISION DEL DUEÑO EL SUMINISTRO E INSTALACION DE LOS ACCESORIOS SANITARIOS, TALES COMO JABONERAS, CEPILLERAS, PAPELERA, AROS TOALLEROS, ESPEJOS Y SIMILARES.

LA GRIFERIA DEBERA SER ESCOGIDA POR EL DUEÑO DEL PROYECTO E INSTALADA POR EL CONTRATISTA.

INGENIERIA MUNICIPAL
DISTRITO DE SAN CARLOS
APROBADO
INGENIERO MUNICIPAL
FECHA 22/8/11

Cuerpo de Bomberos
OFICINA DE SEGURIDAD
La Chorrera, ... de ... de 2011
Resolución No. ... Fecha No. ...
Se autoriza el presente plano por llenar las condiciones requerida

Jefe de la Oficina de Seguridad

FELIPE GONZALEZ LINCK
ARQUITECTO
LICENCIA No. 1-182
LEY 15 DEL 26 DE ENERO DE 1959
JUNTA TECNICA DE INGENIERIA Y ARQUITECTURA

FELIFE GONZÁLEZ LINCK
ARQUITECTO
Tel. – 65771610 – Fax 392-2457 | 64035839

DISEÑO ARQUITECTÓNICO	Arq. Vicente Cortes Arq. Igor Cortes
DESARROLLO	Arq. Igor Cortes Arq. Ilem Segismond Arq. Nancy Urriola
PROYECTO ESTRUCTURAL	Ing. Ricauter Bowen
PROYECTO ELÉCTRICO	Ing. Edgar Naranjo
PROYECTO DE PLOMERÍA	Ing. Gilberto Ayala

PROYECTO

Residencial El Palmar

UBICACIÓN

COMUNIDAD DE 'EL PALMAR'
DTTO. DE SAN CARLOS - CORREGIMIENTO DE SAN CARLOS
PANAMÁ

SOCIEDAD PROMOTORA

Inversiones Decuria, S.A.

Representante legal: IGOR CORTES
Número de cédula o pasaporte: 8-705-1493

INGENIERÍA MUNICIPAL

PLANO

- DETALLE DE SERVICIOS SANITARIOS
APTOS C - NIVEL 2300@2500
APTOS D - NIVEL 2600@2800
ESCALA 1:25

ARCHIVO .DWG	BAÑOS D,E,F
FECHA	30/08/2010
FECHA MODIFICACIÓN	DD/MM/AAAA

ARQUITECTURA | HOJA: 36 | DE: 65

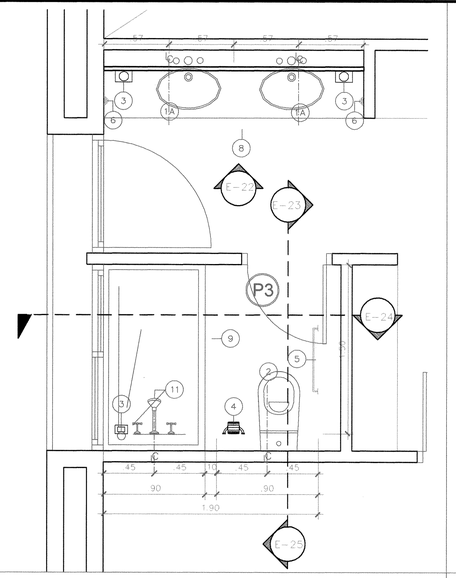

AMPL. SERV. SANITARIOS D3 - NIVEL 2700

ESCALA: 1:25

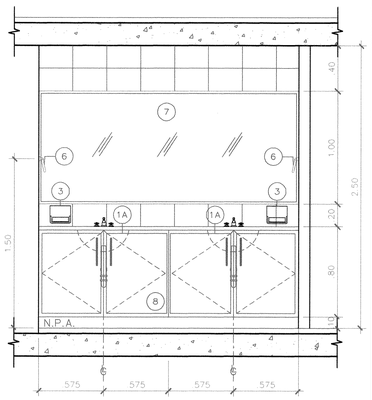

ELEVACION

SERV. SANT. D3 (N2700) ESCALA: 1:25 E-22

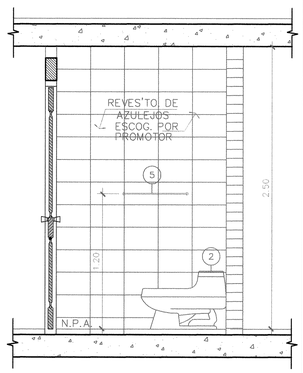

ELEVACION

SERV. SANT. D3 (N2700) ESCALA: 1:25 E-23

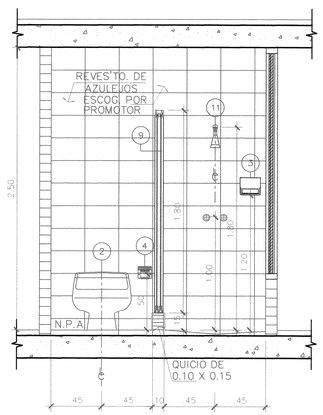

ELEVACION

SERV. SANT. D3 (N2700) ESCALA: 1:25 E-24

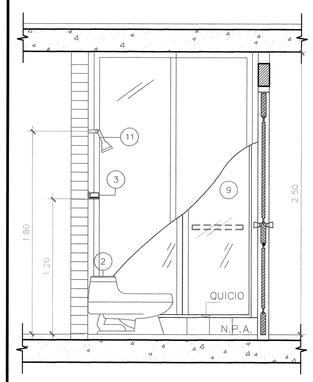

ELEVACION

SERV. SANT. D3 (N2700) ESCALA: 1:25 E-25

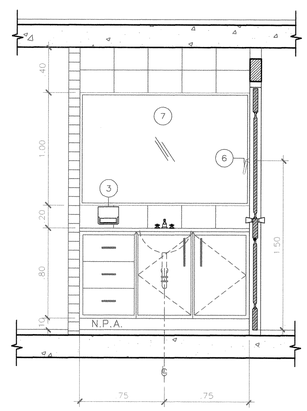

ELEVACION

SERV. SANT. D4 (N2700) ESCALA: 1:25 E-26

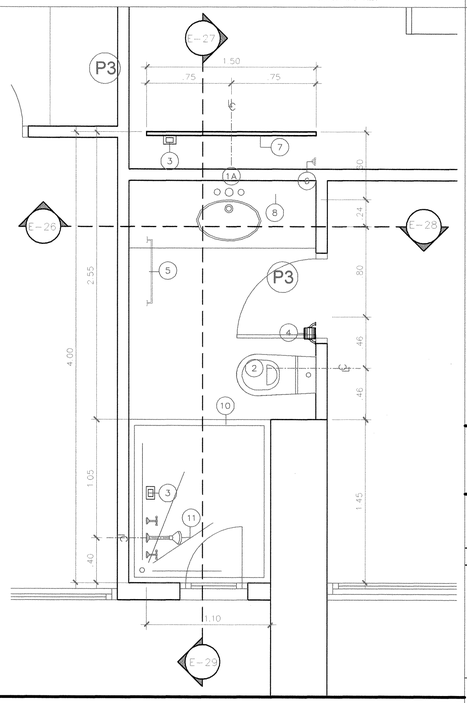

AMPL. SERV. SANITARIOS D4 - NIVEL 2700

ESCALA: 1:25

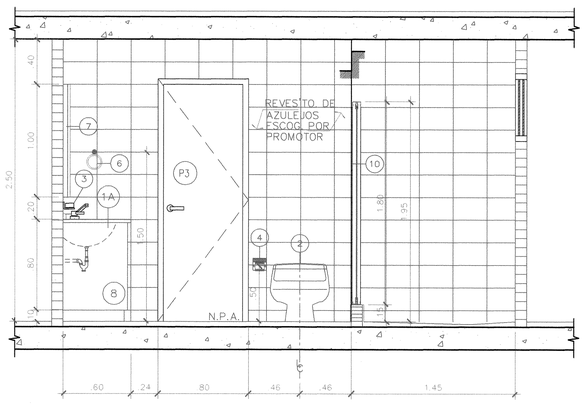

ELEVACION

SERV. SANT. D4 (N2700) ESCALA: 1:25 E-27

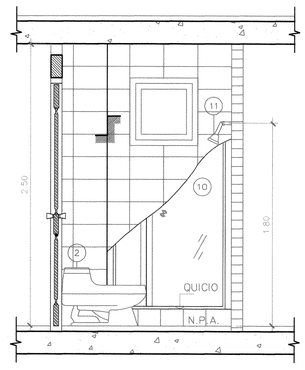

ELEVACION

SERV. SANT. D4 (N2700) ESCALA: 1:25 E-28

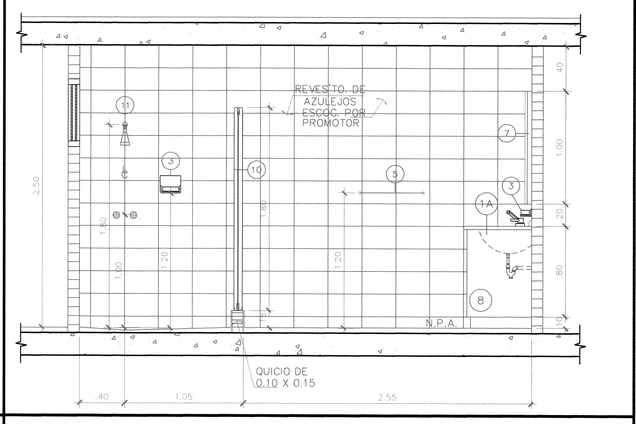

ELEVACION

SERV. SANT. D4 (N2700) ESCALA: 1:25 E-29

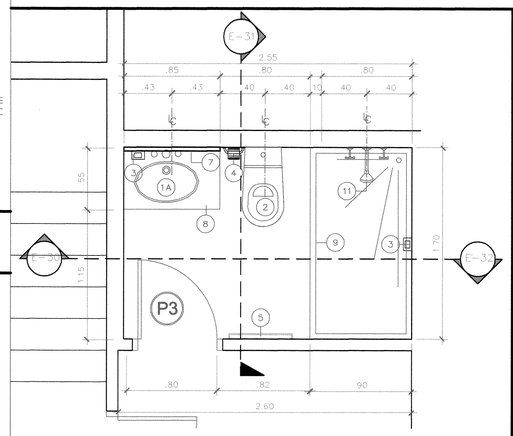

AMPL. SERV. SANITARIOS D5 - NIVEL 2700

ESCALA: 1:25

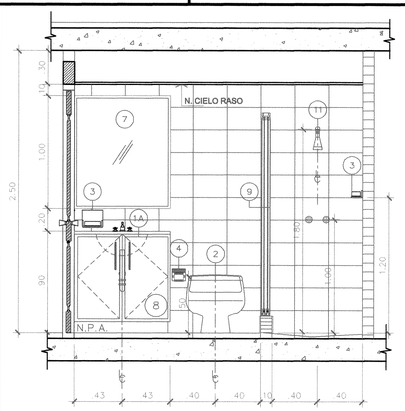

ELEVACION

SERV. SANT. D5 (N2700) ESCALA: 1:25 E-30

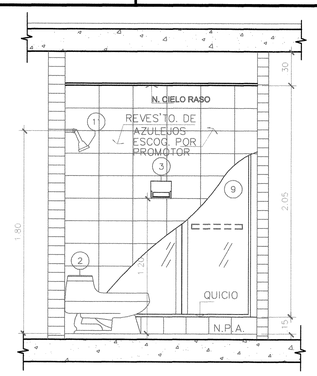

ELEVACION

SERV. SANT. D5(N2700) ESCALA: 1:25 E-31

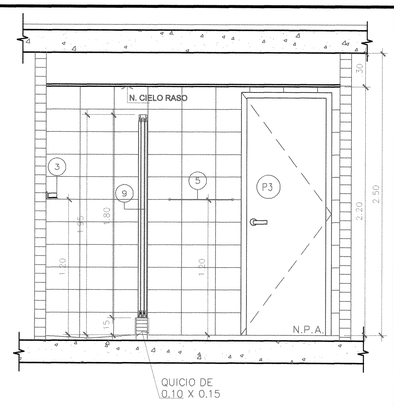

ELEVACION

SERV. SANT. D5 (N2700) ESCALA: 1:25 E-32

INGENIERIA MUNICIPAL
DISTRITO DE SAN CARLOS
APROBADO
INGENIERO MUNICIPAL
FECHA 20 /6/ 11

Cuerpo de Bomb...
OFICINA DE SEGURIDAD
La Chorrera
La Chorrera, ... de ... de 20...
Resolución No. ... Plano No. ...
Se aprueba el registro de este plano por llenar las condiciones requeridas.
Jefe de la Oficina de Seguridad

FELIPE GONZALEZ LINCK
ARQUITECTO
LICENCIA No. 77-103
LEY 15 DEL 26 DE ENERO DE 1959
JUNTA TECNICA DE INGENIERIA Y ARQUITECTURA

FELIFE GONZÁLEZ LINCK
ARQUITECTO
Tel. -- 66771610 -- Fax 392-2457 | 64036839

DISEÑO ARQUITECTÓNICO	Arq. Vicente Cortes Arq. Igor Cortes
DESARROLLO	Arq. Igor Cortes Arq. Ilem Segismond Arq. Nancy Urriola
PROYECTO ESTRUCTURAL	Ing. Ricauter Bowen
PROYECTO ELÉCTRICO	Ing. Edgar Naranjo
PROYECTO DE PLOMERÍA	Ing. Gilberto Ayala

PROYECTO

Residencial El Palmar

UBICACIÓN

COMUNIDAD DE 'EL PALMAR'
DTTO. DE SAN CARLOS - CORREGIMIENTO DE SAN CARLOS
PANAMÁ

SOCIEDAD PROMOTORA

Inversiones Decuria, S.A.

Representante legal: IGOR CORTES
Número de cédula o pasaporte: 8C054493

INGENIERÍA MUNICIPAL

PLANO

- DETALLE DE SERVICIOS SANITARIOS APTOS D - NIVEL2600 @ 2800
ESCALA 1:25

ARCHIVO .DWG	BAÑOS D,E,F
FECHA	30/08/2010
FECHA MODIFICACIÓN	DD/MM/AAAA

ARQUITECTURA	HOJA: 37	DE: 65

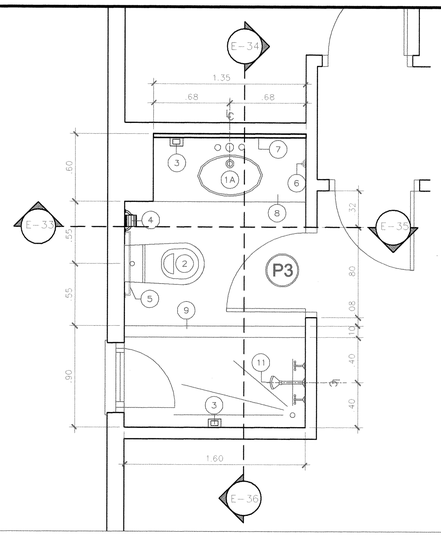

AMPL. SERV. SANITARIOS E1 - N-100@-400

ESCALA: 1:25

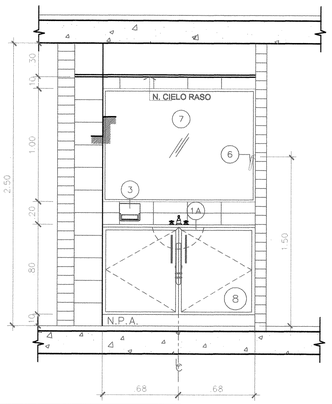

NOTA:
COLOCAR CIELO RASO EN BAÑO
A EXCEPCION DEL N-100

ELEVACION
SERV. SANT. E1 (N-100@-400) ESCALA: 1:25 E-33

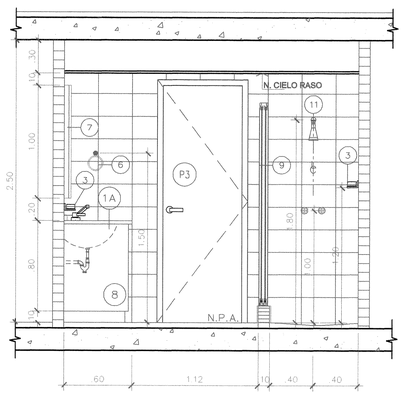

ELEVACION
SERV. SANT. E1 (N-100@-400) ESCALA: 1:25 E-34

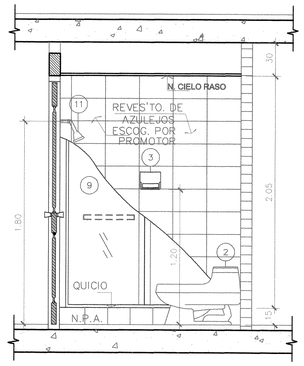

ELEVACION
SERV. SANT. E1(N-100@-400) ESCALA: 1:25 E-35

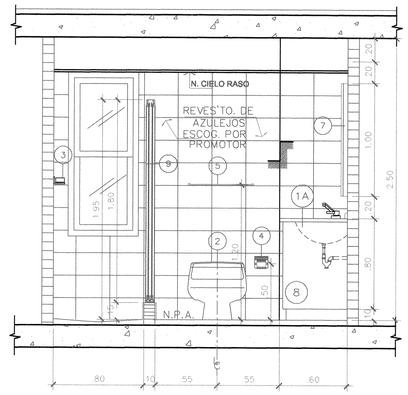

ELEVACION
SERV. SANT. E1 (N-100@-400) ESCALA: 1:25 E-36

AMPL. SERV. SANITARIOS E2 - N-100@-400

ESCALA: 1:25

NOTA:
COLOCAR CIELO RASO EN BAÑO
A EXCEPCION DEL N-100

ELEVACION
SERV. SANT. E2 (N-100@-400) ESCALA: 1:25 E-37

ELEVACION
SERV. SANT. E2 (N-100@-400) ESCALA: 1:25 E-38

ELEVACION
SERV. SANT. E2(N-100@-400) ESCALA: 1:25 E-39

ELEVACION
SERV. SANT. E2 (N-100@-400) ESCALA: 1:25 E-40

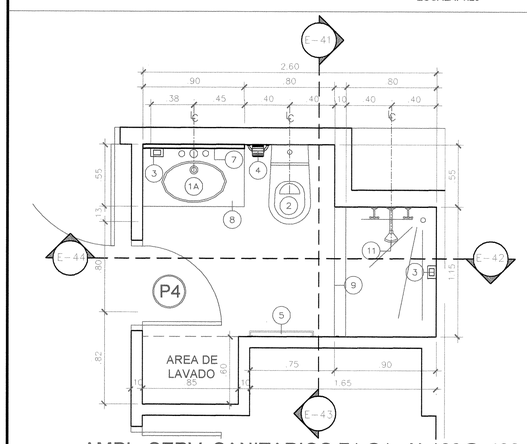

AMPL. SERV. SANITARIOS F1,G1 - N-100@-400

ESCALA: 1:25

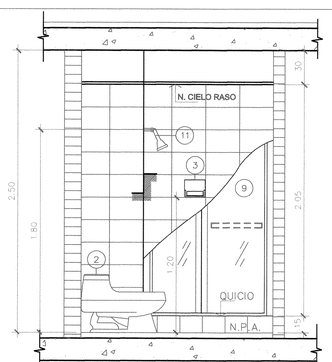

NOTA:
COLOCAR CIELO RASO EN BAÑO
A EXCEPCION DEL N-100

ELEVACION
SERV. SANT. F1,G1 (N-100@-400) ESCALA: 1:25 E-41

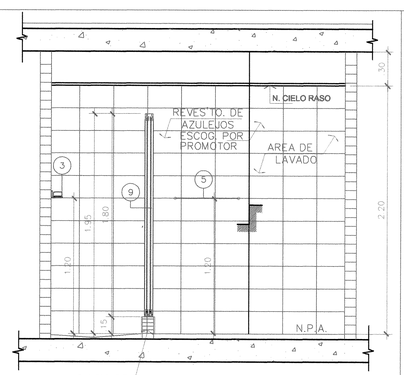

ELEVACION
SERV. SANT. F1,G1 (N-100@-400) ESCALA: 1:25 E-42

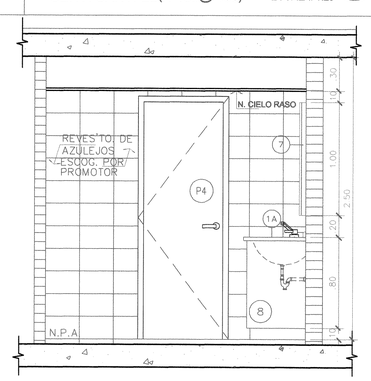

ELEVACION
SERV. SANT. F1,G1(N-100@-400) ESCALA: 1:25 E-43

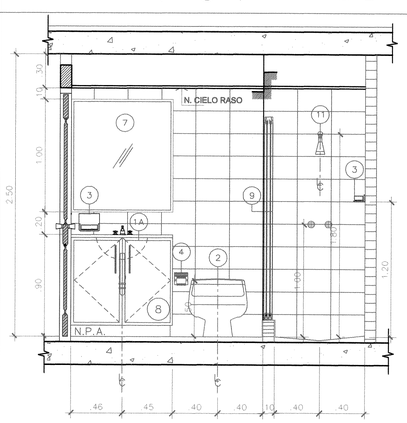

ELEVACION
SERV. SANT. F1,G1 (N-100@-400) ESCALA: 1:25 E-44

INGENIERIA MUNICIPAL
DISTRITO DE SAN CARLOS
APROBADO
INGENIERO MUNICIPAL
FECHA: 12/8/11

Cuerpo de Bomberos
La Chorrera
OFICINA DE SEGURIDAD
La Chorrera, ... de ... de 20...
Resolución No. ... Fiscal No. ...
Se aprueba el registro de este plano por llenar los condiciones requeridas.
Jefe de la Oficina de Seguridad

FELIPE GONZALEZ LINCK
ARQUITECTO
LICENCIA No. 87-1-102
LEY 15 DEL 26 DE ENERO DE 1959
JUNTA TECNICA DE INGENIERIA Y ARQUITECTURA

FELIPE GONZÁLEZ LINCK
ARQUITECTO
Tel. - 66771610 - Fax 302-2457 | 64035830

DISEÑO ARQUITECTÓNICO	Arq. Vicente Cortes Arq. Igor Cortes
DESARROLLO	Arq. Igor Cortes Arq. Ilem Segismond Arq. Nancy Urriola
PROYECTO ESTRUCTURAL	Ing. Ricauter Bowen
PROYECTO ELÉCTRICO	Ing. Edgar Naranjo
PROYECTO DE PLOMERÍA	Ing. Gilberto Ayala

PROYECTO

Residencial El Palmar

UBICACIÓN
COMUNIDAD DE 'EL PALMAR'
DITTO. DE SAN CARLOS - CORREGIMIENTO DE SAN CARLOS
PANAMÁ

SOCIEDAD PROMOTORA
Inversiones Decuria, S.A.
Representante legal: IGOR CORTES
Número de cédula o pasaporte: 8C054493

INGENIERÍA MUNICIPAL

PLANO
- DETALLE DE SERVICIOS SANITARIOS APTOS E, F, G - NIVEL -100 @ -400
ESCALA 1:25

ARCHIVO .DWG	BAÑOS D,F,E
FECHA	30/08/2010
FECHA MODIFICACIÓN	DD/MM/AAAA

ARQUITECTURA | HOJA: 38 | DE: 65

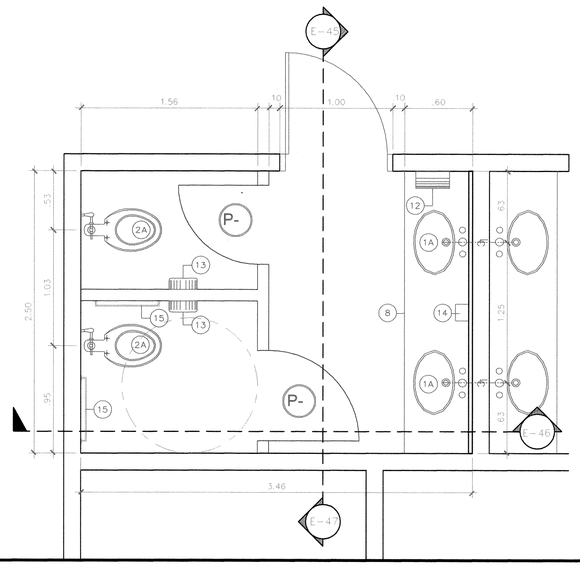

AMPL. SERV. SANITARIOS PUBLICOS AREA SOCIAL (N-400)

ESCALA: 1:25

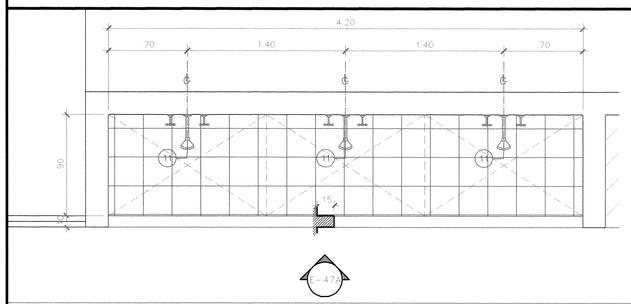

AMPL. DE DUCHAS - AREA SOCIAL (N-400)

ESCALA: 1:25

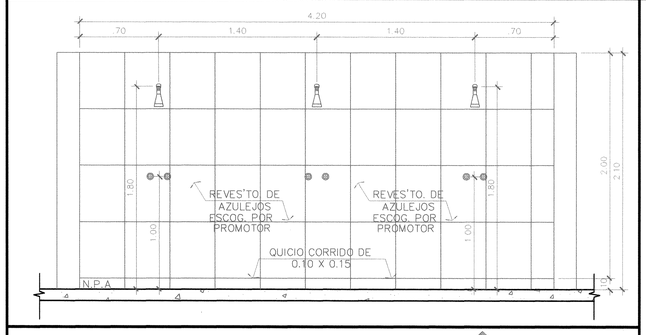

ELEVACION

DUCHAS - AREA SOCIAL (N-400) ESCALA: 1:25 (E-47A)

NOTAS IMPORTANTES DE BAÑOS

EL REVESTIMIENTO DE AZULEJOS SERAN IMPORTADOS EN COLOR Y DISEÑO ESCOGIDO POR EL PROMOTOR SEGUN ALTURAS INDICADAS EN LOS DETALLES

SERA DECISION DEL DUEÑO EL SUMINISTRO E INSTALACION DE LOS ACCESORIOS SANITARIOS, TALES COMO JABONERAS, CEPILLERAS, PAPELERA, AROS TOALLEROS, ESPEJOS Y SIMILARES.

LA GRIFERIA DEBERA SER ESCOGIDA POR EL DUEÑO DEL PROYECTO E INSTALADA POR EL CONTRATISTA.

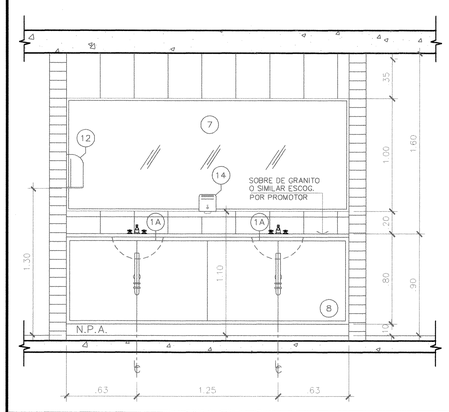

ELEVACION

SERV. SANIT. AREA SOCIAL (N-400) ESCALA: 1:25 (E-45)

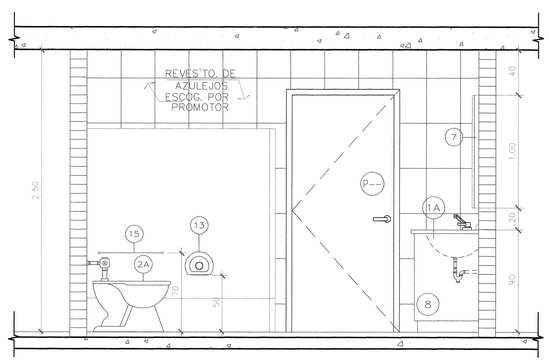

ELEVACION

SERV. SANIT. AREA SOCIAL (N-400) ESCALA: 1:25 (E-46)

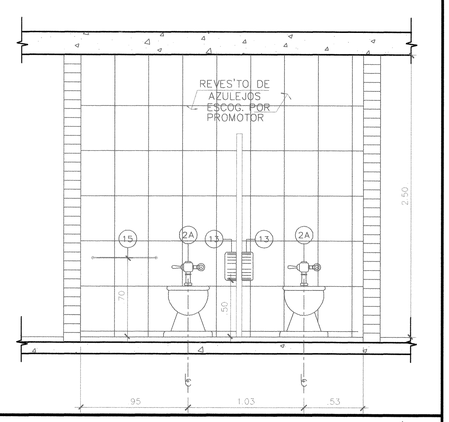

ELEVACION

SERV. SANIT. AREA SOCIAL (N-400) ESCALA: 1:25 (E-47)

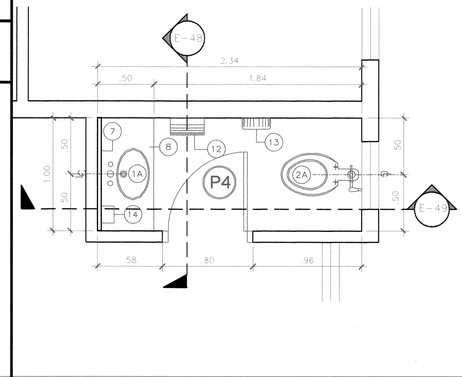

AMPL. SERV. SANITARIOS #1 (N000)

ESCALA: 1:25

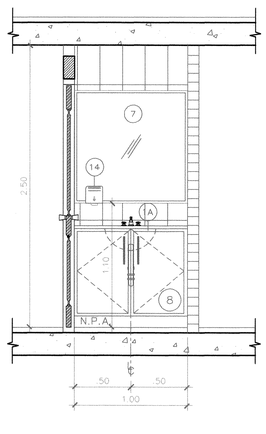

ELEVACION

SERV. SANT. #1 (N000) ESCALA: 1:25 (E-48)

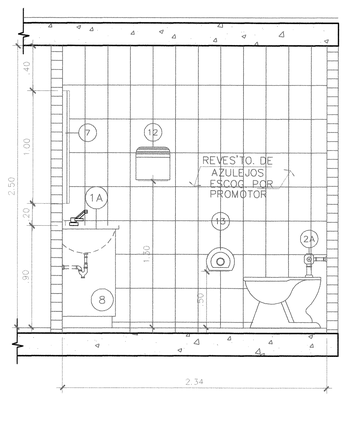

ELEVACION

SERV. SANT. #1 (N000) ESCALA: 1:25 (E-49)

CUADRO DE ARTEFACTOS SANITARIOS Y ACCESORIOS

1A	LAVAMANOS INCESA STANDARD O SIMILAR EMBUTIDO EN MUEBLE EN COLOR BLANCO O COLORES NEUTRALES
1B	LAVAMANOS DE PEDESTAL MARCA INCESA STANDARD O SIMILAR EN COLOR BLANCO O COLORES NEUTRALES
1C	LAVAMANOS DE PARED MARCA INCESA STANDARD O SIMILAR EN COLOR BLANCO O COLORES NEUTRALES
2	INODORO DE UNA PIEZA MARCA INCESA STANDARD O SIMILAR EN COLOR BLANCO O COLORES NEUTRALES
2A	INODORO FLUXOMETRO EN COLOR BLANCO O COLORES NEUTRALES
3	JABONERA / CEPILLERA TIPO SUPERFICIAL, SEGUN COLOR DE ARTEFACTOS
4	PAPELERA STANDARD
5	TUBO TOALLERO DE 24" CROMADO SUPERFICIAL
6	ARO TOALLERO (PARA TOALLA DE MANOS) JUNTO AL LAVAMANOS, VER UBICACION EN PLANTA Y ELEVACIONES
7	ESPEJO
8	MUEBLE SEGUN DISEÑO Y MATERIAL ESCOGIDO POR EL ARQ.
9	PUERTAS DE BAÑO CORREDIZA CON MARCOS DE ALUMINIO ESMALTADO BLANCO Y VIDRIO
10	PUERTAS DE BAÑO ABATIBLE CON MARCOS DE ALUMINIO ESMALTADO BLANCO Y VIDRIO
11	DUCHA
12	DISPENSADOR DE PAPEL TOALLA
13	DISPENSADOR DE PAPEL HIGIENICO
14	DISPENSADOR DE JABON DE MANOS
15	BARRA PARA MINUSVALIDOS

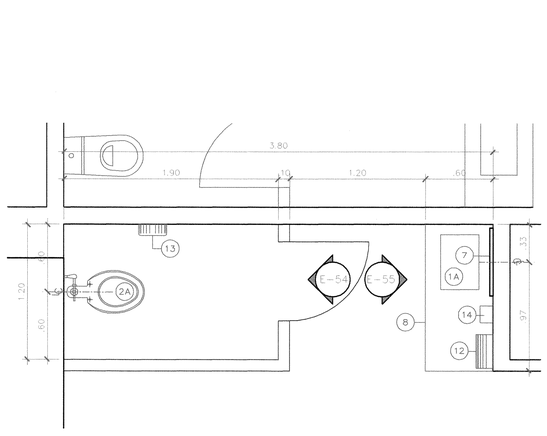

AMPL. SERV. SANITARIOS #3 (N+000)

ESCALA: 1:25

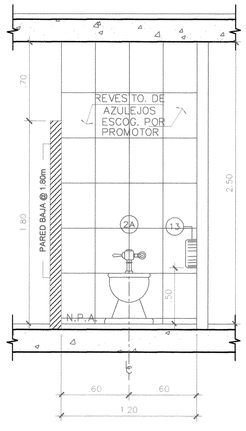

ELEVACION

SERV. SANT. #3 (N000) ESCALA: 1:25 (E-54)

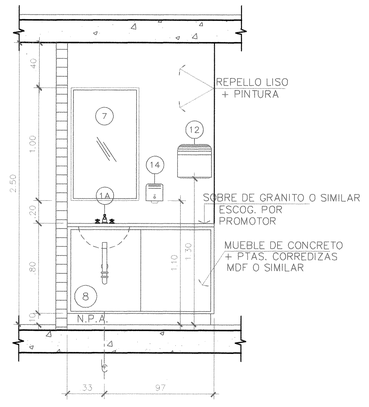

ELEVACION

SERV. SANT. #3 (N000) ESCALA: 1:25 (E-55)

INGENIERIA MUNICIPAL
DISTRITO DE SAN CARLOS
APROBADO
INGENIERO MUNICIPAL
FECHA: 22/8/11

Cuerpo de Bomberos
OFICINA DE INSPECCIONES
La Chorrera, 11 de Agosto 2011
Revisado: Planos de Obra
Se aprueba el presente plano con las siguientes condiciones especiales:
Jefe de la Sección de Seguridad

FELIPE GONZALEZ LINCK
ARQUITECTO
LICENCIA No. 7111-188
FIRMA
LEY 15 DEL 26 DE ENERO DE 1959
JUNTA TECNICA DE INGENIERIA Y ARQUITECTURA

FELIFE GONZÁLEZ LINCK
ARQUITECTO
Tel. – 66771610 – Fax 392-2457 | 64035839

DISEÑO ARQUITECTÓNICO	Arq. Vicente Cortes Arq. Igor Cortes
DESARROLLO	Arq. Igor Cortes Arq. Ilem Segismond Arq. Nancy Urriola
PROYECTO ESTRUCTURAL	Ing. Ricauter Bowen
PROYECTO ELÉCTRICO	Ing. Edgar Naranjo
PROYECTO DE PLOMERÍA	Ing. Gilberto Ayala

PROYECTO

Residencial El Palmar

UBICACIÓN

COMUNIDAD DE 'EL PALMAR'
DTTO. DE SAN CARLOS - CORREGIMIENTO DE SAN CARLOS
PANAMÁ

SOCIEDAD PROMOTORA

Inversiones Decuria, S.A.

Representante legal: IGOR CORTES
Número de cédula o pasaporte: 8C054493

INGENIERÍA MUNICIPAL

PLANO

- DETALLE DE SERVICIOS SANITARIOS
  AREA SOCIAL - NIVEL -400
  PLANTA BAJA - NIVEL 00
  ESCALA 1:25

ARCHIVO .DWG	BAÑOS N+000
FECHA	30/08/2010
FECHA MODIFICACIÓN	DD/MM/AAAA

ARQUITECTURA | HOJA: 39 | DE: 65

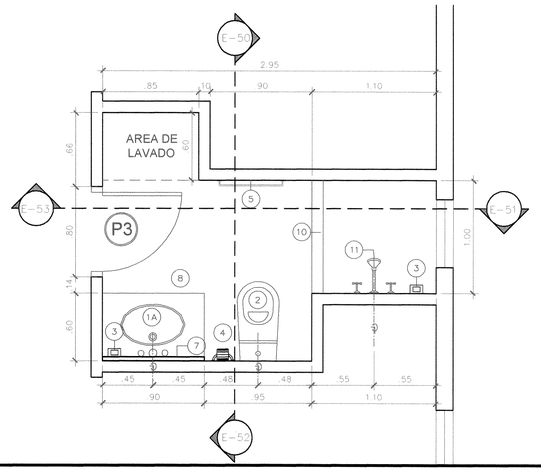

AMPL. SERV. SANITARIOS #2 (N000)

ESCALA: 1:25

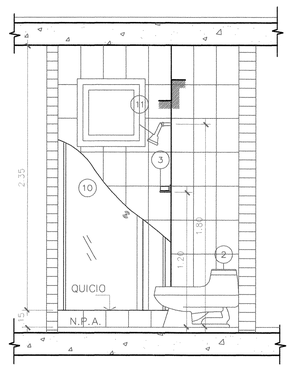

ELEVACION

SERV. SANT. #2 (N000) ESCALA: 1:25 (E-50)

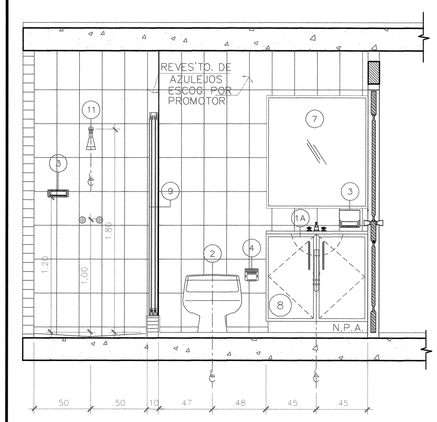

ELEVACION

SERV. SANT. #2 (N000) ESCALA: 1:25 (E-51)

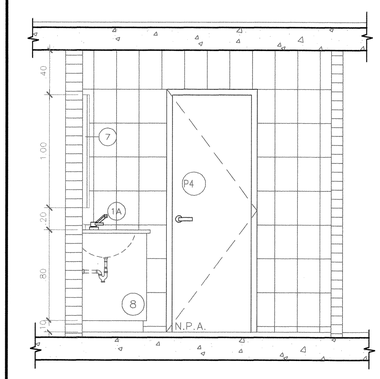

ELEVACION

SERV. SANT. #2 (N000) ESCALA: 1:25 (E-52)

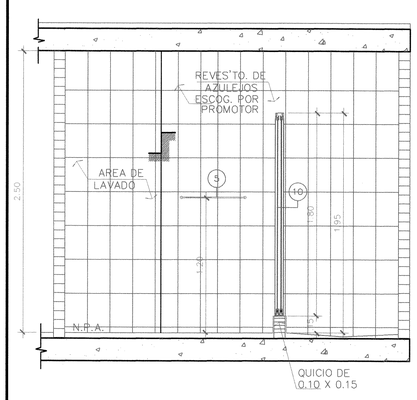

ELEVACION

SERV. SANT. #2 (N000) ESCALA: 1:25 (E-53)

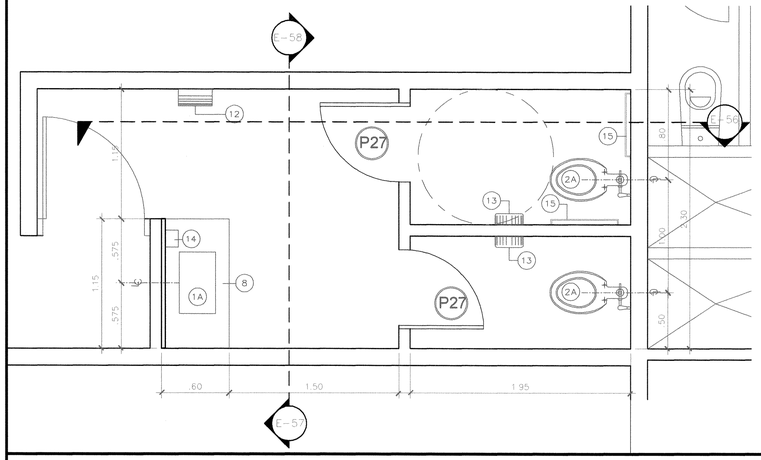

AMPL. SERV. SANITARIOS #4, #5 (N000)

ESCALA: 1:25

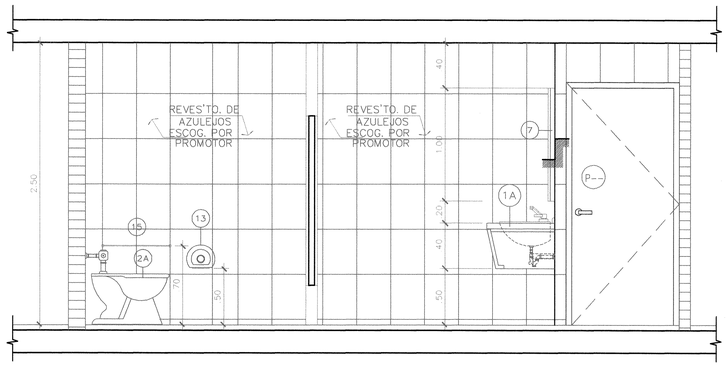

ELEVACION

SERV. SANT. #4, #5 (N000) ESCALA: 1:25 (E-56)

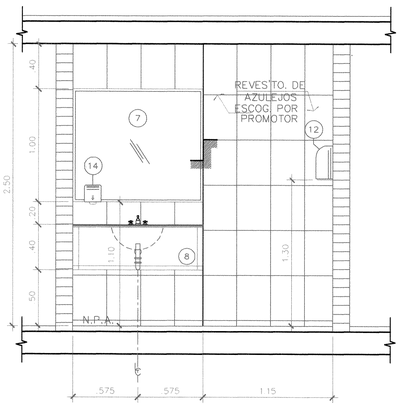

ELEVACION

SERV. SANT. #4, #5 (N000) ESCALA: 1:25 (E-57)

CUADRO DE ARTEFACTOS SANITARIOS Y ACCESORIOS

1A	LAVAMANOS INCESA STANDARD O SIMILAR EMBUTIDO EN MUEBLE EN COLOR BLANCO O COLORES NEUTRALES
1B	LAVAMANOS DE PEDESTAL MARCA INCESA STANDARD O SIMILAR EN COLOR BLANCO O COLORES NEUTRALES
1C	LAVAMANOS DE PARED MARCA INCESA STANDARD O SIMILAR EN COLOR BLANCO O COLORES NEUTRALES
2	INODORO DE UNA PIEZA MARCA INCESA STANDARD O SIMILAR EN COLOR BLANCO O COLORES NEUTRALES
2A	INODORO FLUXOMETRO EN COLOR BLANCO O COLORES NEUTRALES
3	JABONERA / CEPILLERA TIPO SUPERFICIAL, SEGUN COLOR DE ARTEFACTOS
4	PAPELERA STANDARD
5	TUBO TOALLERO DE 24" CROMADO SUPERFICIAL
6	ARO TOALLERO (PARA TOALLA DE MANOS) JUNTO AL LAVAMANOS, VER UBICACION EN PLANTA Y ELEVACIONES
7	ESPEJO
8	MUEBLE SEGUN DISEÑO Y MATERIAL ESCOGIDO POR EL APO.
9	PUERTAS DE BAÑO CORREDIZA CON MARCOS DE ALUMINIO ESMALTADO BLANCO Y VIDRIO
10	PUERTAS DE BAÑO ABATIBLE CON MARCOS DE ALUMINIO ESMALTADO BLANCO Y VIDRIO
11	DUCHA
12	DISPENSADOR DE PAPEL TOALLA
13	DISPENSADOR DE PAPEL HIGIENICO
14	DISPENSADOR DE JABON DE MANOS
15	BARRA PARA MINUSVALIDOS

NOTAS IMPORTANTES DE BAÑOS

EL REVESTIMIENTO DE AZULEJOS SERAN IMPORTADOS EN COLOR Y DISEÑO ESCOGIDO POR EL PROMOTOR SEGUN ALTURAS INDICADAS EN LOS DETALLES

SERA DECISION DEL DUEÑO EL SUMINISTRO E INSTALACION DE LOS ACCESORIOS SANITARIOS, TALES COMO JABONERAS, CEPILLERAS, PAPELERA, AROS TOALLEROS, ESPEJOS Y SIMILARES.

LA GRIFERIA DEBERA SER ESCOGIDA POR EL DUEÑO DEL PROYECTO E INSTALADA POR EL CONTRATISTA.

INGENIERIA MUNICIPAL
DISTRITO DE SAN CARLOS
APROBADO
INGENIERO MUNICIPAL
FECHA: 22/9/11

Cuerpo de Bomberos
OFICINA DE SEGURIDAD
La Chorrera
La Chorrera, 11 de Agosto de 2011
Resolución No. 346 (Plano No. 16-8)
Se aprueba el registro de estos planos por llenar las condiciones requeridas.
Jefe de la Oficina de Seguridad

FELIPE GONZÁLEZ LINCK
ARQUITECTO
LICENCIA No. 7711-108
LEY 15 DEL 26 DE ENERO DE 1959
JUNTA TECNICA DE INGENIERIA Y ARQUITECTURA

FELIFE GONZÁLEZ LINCK
ARQUITECTO
Tel. – 66771610 – Fax 392-2457 | 64035839

DISEÑO ARQUITECTÓNICO	Arq. Vicente Cortes Arq. Igor Cortes
DESARROLLO	Arq. Igor Cortes Arq. Ilem Segismond Arq. Nancy Urriola
PROYECTO ESTRUCTURAL	Ing. Ricauter Bowen
PROYECTO ELÉCTRICO	Ing. Edgar Naranjo
PROYECTO DE PLOMERÍA	Ing. Gilberto Ayala

PROYECTO

Residencial El Palmar

UBICACIÓN

COMUNIDAD DE 'EL PALMAR'
DTTO. DE SAN CARLOS - CORREGIMIENTO DE SAN CARLOS
PANAMÁ

SOCIEDAD PROMOTORA

Inversiones Decuria, S.A.
Representante legal: IGOR CORTES
Número de cédula o pasaporte: 8C054493

INGENIERÍA MUNICIPAL

PLANO

- DETALLE DE SERVICIOS SANITARIOS
PLANTA BAJA - NIVEL 00
ESCALA 1:25

ARCHIVO .DWG	BAÑOS N+000
FECHA	30/08/2010
FECHA MODIFICACIÓN	DD/MM/AAAA

ARQUITECTURA | HOJA: 40 | DE: 65

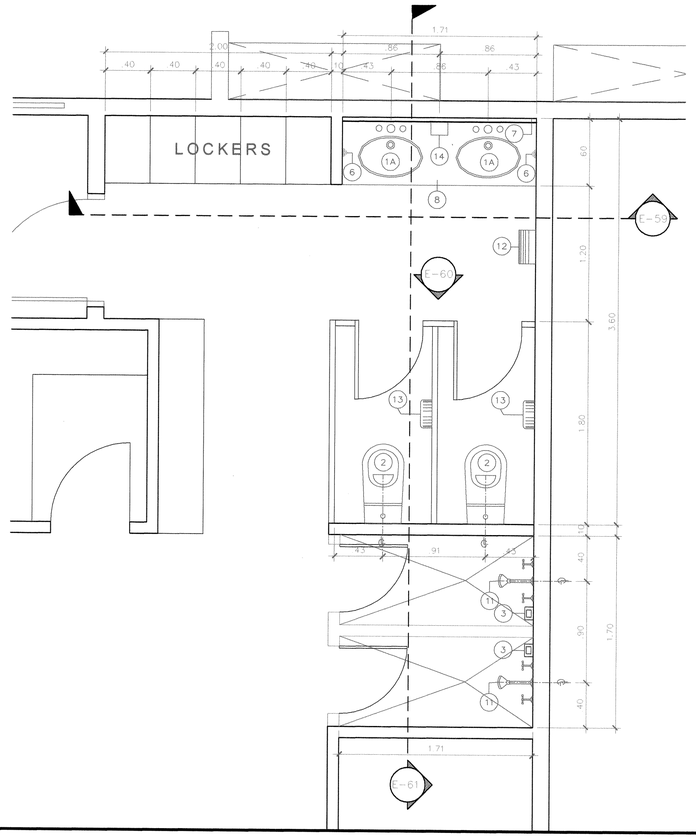

AMPL. SERV. SANITARIOS SPA (N+000)

ESCALA: 1:25

CUADRO DE ARTEFACTOS SANITARIOS Y ACCESORIOS	
1A	LAVAMANOS INCESA STANDARD O SIMILAR EMBUTIDO EN MUEBLE EN COLOR BLANCO O COLORES NEUTRALES
1B	LAVAMANOS DE PEDESTAL MARCA INCESA STANDARD O SIMILAR EN COLOR BLANCO O COLORES NEUTRALES
1C	LAVAMANOS DE PARED MARCA INCESA STANDARD O SIMILAR EN COLOR BLANCO O COLORES NEUTRALES
2	INODORO DE UNA PIEZA MARCA INCESA STANDARDO SIMILAR EN COLOR BLANCO O COLORES NEUTRALES
2A	INODORO FLUXOMETRO EN COLOR BLANCO O COLORES NEUTRALES
3	JABONERA / CEPILLERA TIPO SUPERFICIAL, SEGUN COLOR DE ARTEFACTOS
4	PAPELERA STANDARD
5	TUBO TOALLERO DE 24" CROMADO SUPERFICIAL
6	ARO TOALLERO (PARA TOALLA DE MANOS) JUNTO AL LAVAMANOS, VER UBICACION EN PLANTA Y ELEVACIONES
7	ESPEJO
8	MUEBLE SEGUN DISEÑO Y MATERIAL ESCOGIDO POR EL ARQ.
9	PUERTAS DE BAÑO CORREDIZA CON MARCOS DE ALUMINIO ESMALTADO BLANCO Y VIDRIO
10	PUERTAS DE BAÑO ABATIBLE CON MARCOS DE ALUMINIO ESMALTADO BLANCO Y VIDRIO
11	DUCHA
12	DISPENSADOR DE PAPEL TOALLA
13	DISPENSADOR DE PAPEL HIGIENICO
14	DISPENSADOR DE JABON DE MANOS
15	BARRA PARA MINUSVALIDOS

NOTAS IMPORTANTES DE BAÑOS

EL REVESTIMIENTO DE AZULEJOS SERAN IMPORTADOS EN COLOR Y DISEÑO ESCOGIDO POR EL PROMOTOR SEGUN ALTURAS INDICADAS EN LOS DETALLES

SERA DECISION DEL DUEÑO EL SUMINISTRO E INSTALACION DE LOS ACCESORIOS SANITARIOS, TALES COMO JABONERAS, CEPILLERAS, PAPELERA, AROS TOALLEROS, ESPEJOS Y SIMILARES.

LA GRIFERIA DEBERA SER ESCOGIDA POR EL DUEÑO DEL PROYECTO E INSTALADA POR EL CONTRATISTA.

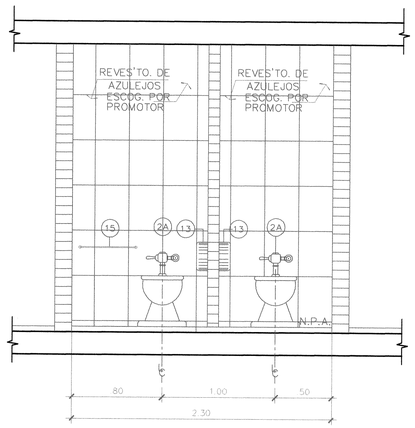

ELEVACION
SERV. SANT. #4, #5 (N000)
E-58
ESCALA: 1:25

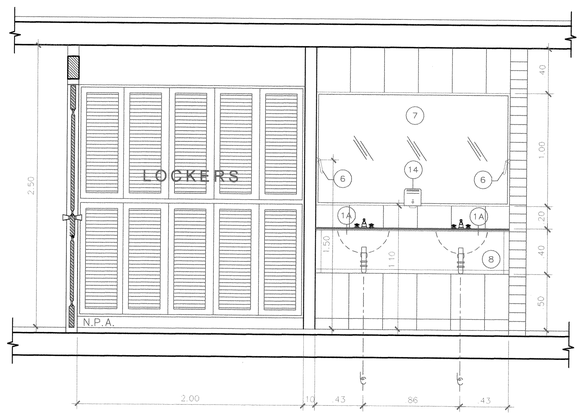

ELEVACION
SERV. SANT. SPA (N000)
E-59
ESCALA: 1:25

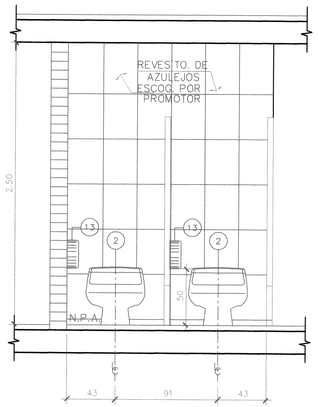

ELEVACION
SERV. SANT. SPA (N000)
E-60
ESCALA: 1:25

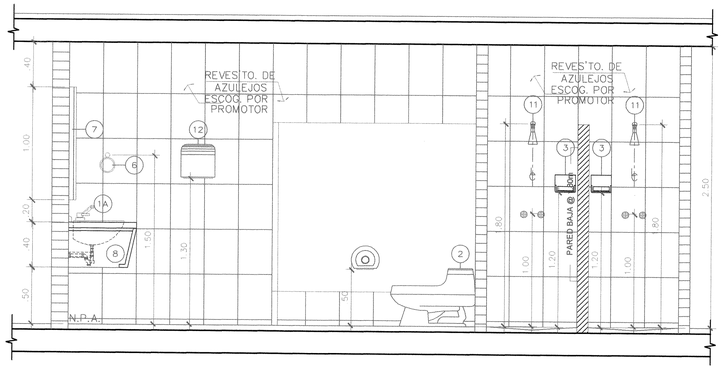

ELEVACION
SERV. SANT. SPA (N000)
E-61
ESCALA: 1:25

INGENIERIA MUNICIPAL
DISTRITO DE SAN CARLOS
APROBADO
INGENIERO MUNICIPAL
FECHA

Cuerpo de Bomberos
OFICINA DE SEGURIDAD
La Chorrera
La Chorrera, ... de ... de 20...
Resolución No. ... Plano No. ...
Se aprueba el registro de este plano por llenar las condiciones requeridas

Jefe de la Oficina de Seguridad

FELIPE GONZALEZ LINCK
ARQUITECTO
LICENCIA No. 7781-188
LEY 15 DEL 26 DE ENERO DE 1959
JUNTA TECNICA DE INGENIERIA Y ARQUITECTURA

FELIFE GONZÁLEZ LINCK
ARQUITECTO
Tel. -- 66771610 -- Fax 392-2457 | 64035839

DISEÑO ARQUITECTÓNICO	Arq. Vicente Cortes Arq. Igor Cortes
DESARROLLO	Arq. Igor Cortes Arq. Ilem Segismond Arq. Nancy Urriola
PROYECTO ESTRUCTURAL	Ing. Ricauter Bowen
PROYECTO ELÉCTRICO	Ing. Edgar Naranjo
PROYECTO DE PLOMERÍA	Ing. Gilberto Ayala

PROYECTO
Residencial El Palmar

UBICACIÓN
COMUNIDAD DE 'EL PALMAR'
DTTO. DE SAN CARLOS - CORREGIMIENTO DE SAN CARLOS
PANAMÁ

SOCIEDAD PROMOTORA
Inversiones Decuria, S.A.
Representante legal: IGOR CORTES
Número de cédula o pasaporte: 8C054493

INGENIERÍA MUNICIPAL

PLANO
- DETALLE DE SERVICIOS SANITARIOS
PLANTA BAJA - NIVEL 00
ESCALA 1:25

ARCHIVO .DWG	BAÑOS N+000
FECHA	30/08/2010
FECHA MODIFICACIÓN	DD/MM/AAAA

ARQUITECTURA | HOJA: 41 | DE: 65

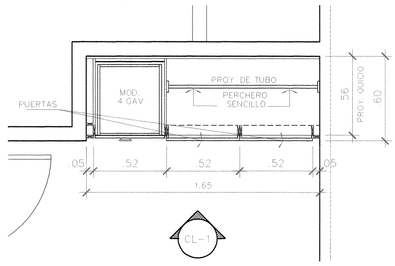

AMPL. CLOSET CL-1

ESCALA: 1:20

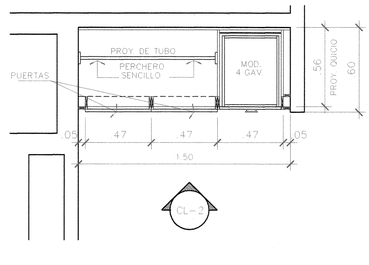

AMPL. CLOSET CL-2

ESCALA: 1:20

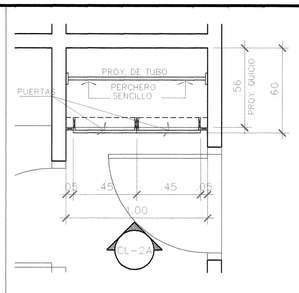

AMPL. CLOSET CL-2A

ESCALA: 1:20

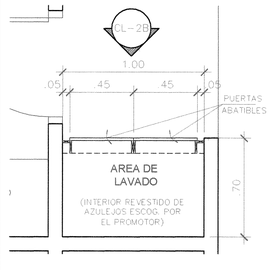

AMPL. CLOSET CL-2B

ESCALA: 1:20

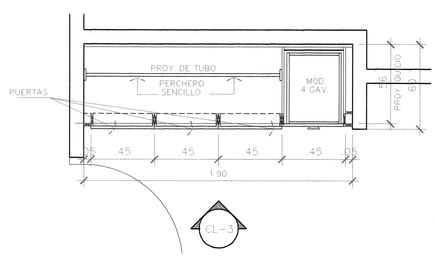

AMPL. CLOSET CL-3

ESCALA: 1:20

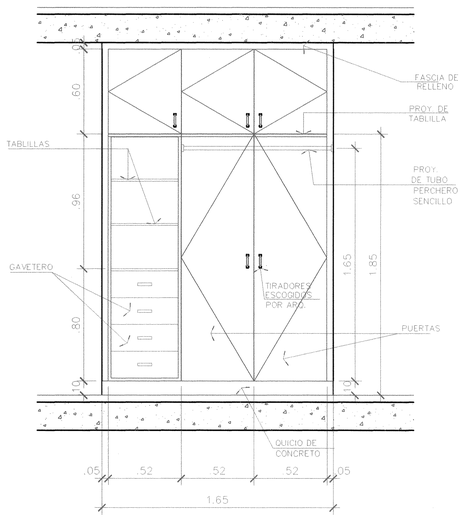

ELEVACION

APTO A (N100 @ N2200)

ESCALA: 1:20 CL-1

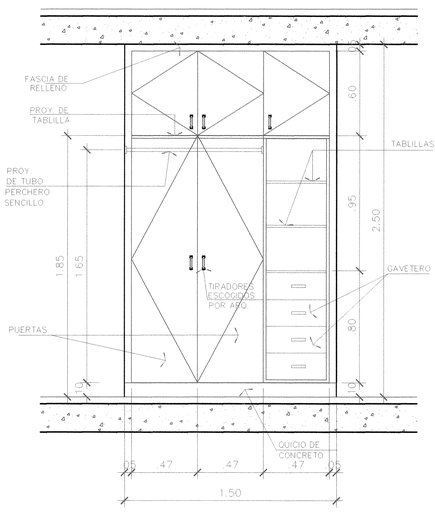

ELEVACION

APTO B (N100 @ N2200)
APTO C (N2300 @ N2500)
APTO D (N2600)

ESCALA: 1:20 CL-2

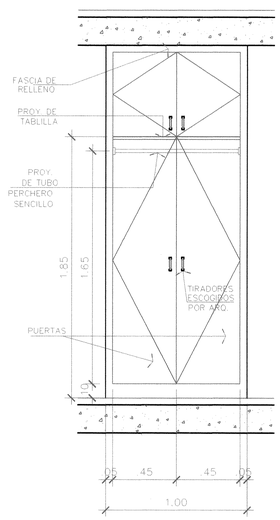

ELEVACION

APTO B (N100 @ N2200)
APTO P.B (N000)

ESCALA 1:20 CL-2A

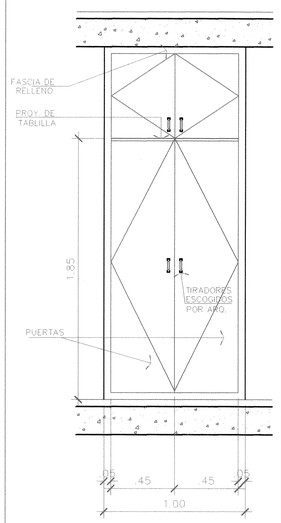

ELEVACION

APTO B (N100 @ N2200)

ESCALA 1:20 CL-2B

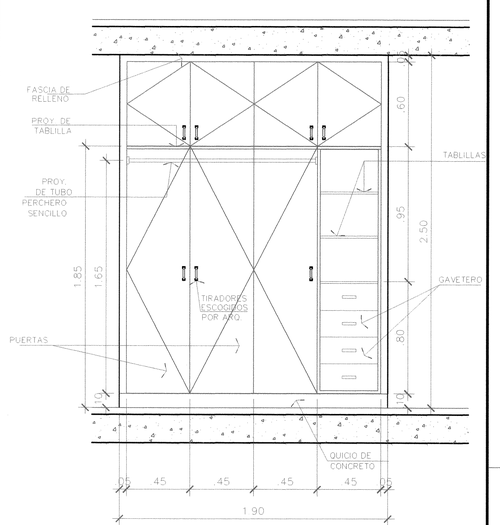

ELEVACION

APTO C (N2300 @ N2500)

ESCALA: 1:20 CL-3

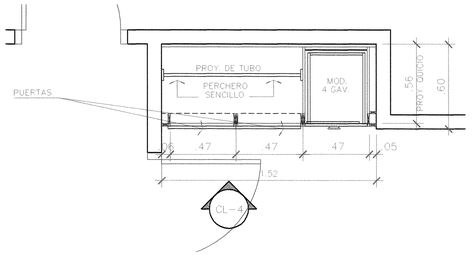

AMPL. CLOSET CL-4

ESCALA: 1:20

NOTAS IMPORTANTE DE CLOSET

EL DISEÑO O MODULACION FINAL DE LOS MUEBLES DE CLOSET, SERA ESCOGIDO POR EL PROMOTOR DEL PROYECTO.

ESTA ES UNA PROPUESTA DE MODULACION QUE PODRA SER CAMBIADA PREVIA APROBACION DEL PROMOTOR.

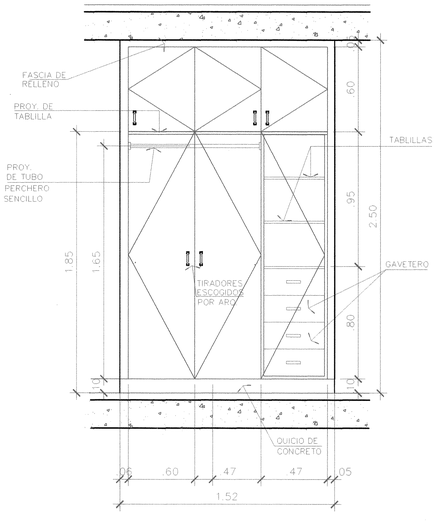

ELEVACION

APTO D (N2700)

ESCALA: 1:20 CL-4

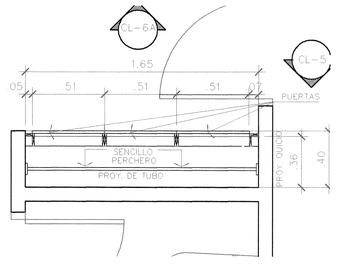

AMPL. CLOSET CL-5

ESCALA: 1:20

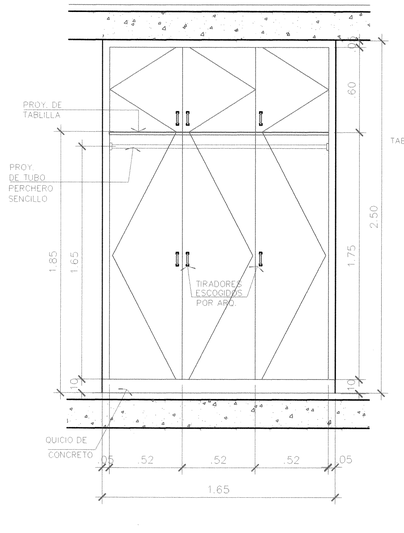

ELEVACION

APTO D (N2700)

ESCALA: 1:20 CL-5

INGENIERIA MUNICIPAL
DISTRITO DE SAN CARLOS
APROBADO
INGENIERO MUNICIPAL
FECHA 22/8/11

Cuerpo de Bomberos
OFICINA DE SEGURIDAD
La Chorrera, 22 de agosto de 2011
Resolución No. 2011 Plano No. 10452
Se aprueba el registro de este plano para construir las condiciones requeridas

Firma de Seguridad

FELIPE GONZALEZ LINCK
ARQUITECTO
LICENCIA No. 87-188
LEY 15 DEL 26 DE ENERO DE 1959
JUNTA TECNICA DE INGENIERIA Y ARQUITECTURA

FELIPE GONZÁLEZ LINCK
ARQUITECTO
Tel. – 66771610 – Fax 392-2457 | 64035839

DISEÑO ARQUITECTÓNICO	Arq. Vicente Cortes Arq. Igor Cortes
DESARROLLO	Arq. Igor Cortes Arq. Ilem Segismond Arq. Nancy Urriola
PROYECTO ESTRUCTURAL	Ing. Ricauter Bowen
PROYECTO ELÉCTRICO	Ing. Edgar Naranjo
PROYECTO DE PLOMERÍA	Ing. Gilberto Ayala

PROYECTO

Residencial El Palmar

UBICACIÓN

COMUNIDAD DE 'EL PALMAR'
DTTO. DE SAN CARLOS - CORREGIMIENTO DE SAN CARLOS
PANAMÁ

SOCIEDAD PROMOTORA

Inversiones Decuria, S.A.

Representante legal: IGOR CORTES
Número de cédula o pasaporte: 8CD54493

INGENIERÍA MUNICIPAL

PLANO

- DETALLE DE CLOSETS, APTOS A,B,C,D
NIVEL 100 @ 2700
ESCALA 1:20

ARCHIVO .DWG	CLOSETS
FECHA	30/08/2010
FECHA MODIFICACIÓN	DD/MM/AAAA

ARQUITECTURA | HOJA: 42 | DE: 65

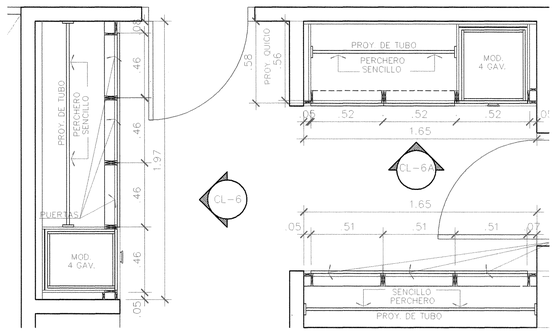

AMPL. CLOSET CL 6 Y CL-6A

ESCALA: 1:20

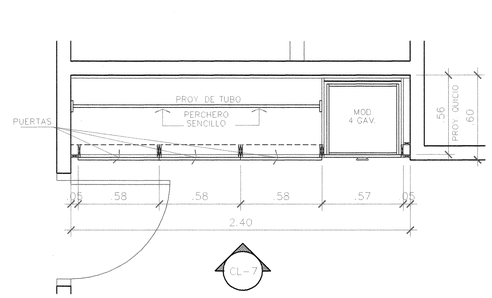

AMPL. CLOSET CL-7

ESCALA: 1:20

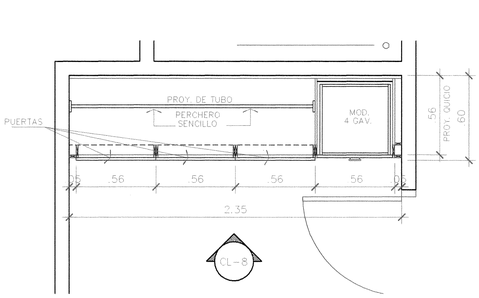

AMPL. CLOSET CL-8

ESCALA: 1:20

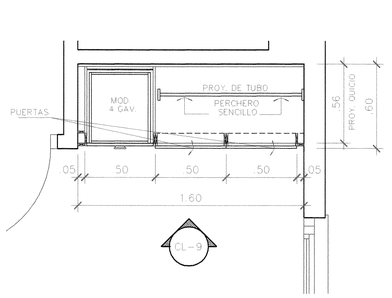

AMPL. CLOSET CL-9

ESCALA: 1:20

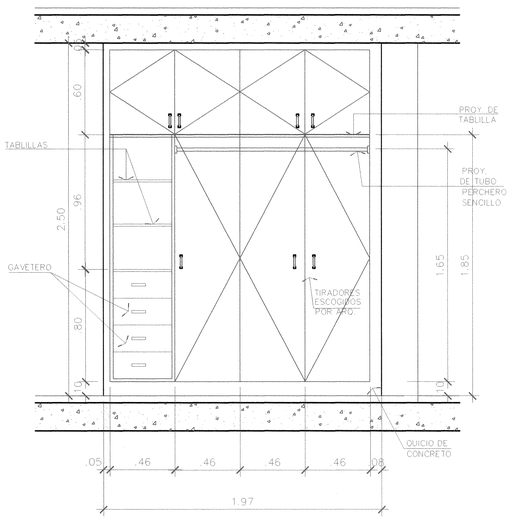

ELEVACION

APTO D (N2700)

CL-6

ESCALA: 1:20

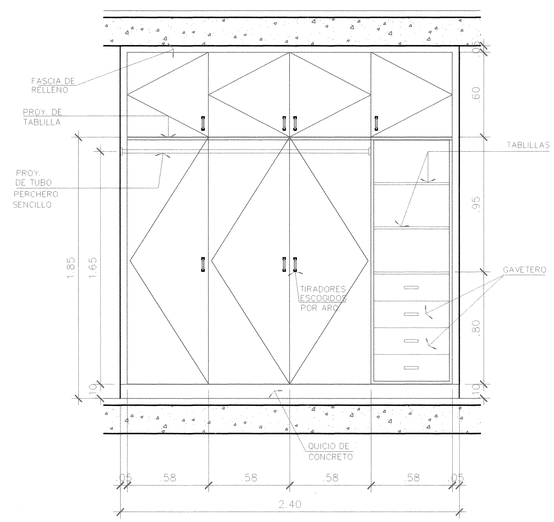

ELEVACION

APTO E (N-100 @ N-400)

CL-7

ESCALA: 1:20

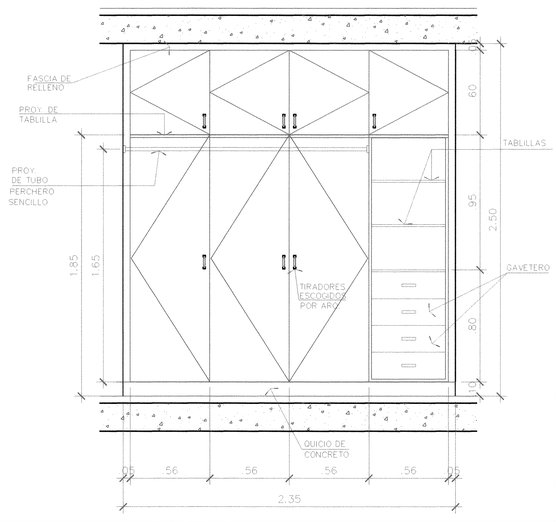

ELEVACION

APTO E (N-100 @ N-400)

CL-8

ESCALA: 1:20

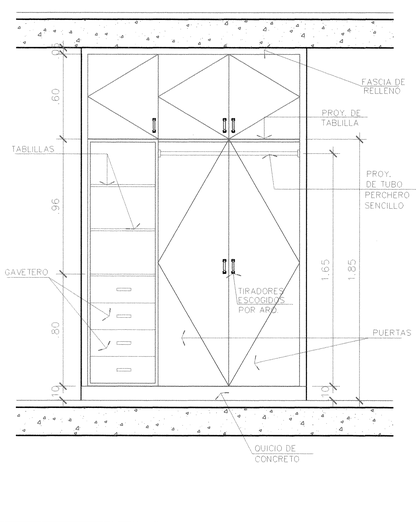

ELEVACION

APTO E (N-100 @ N-400)

CL-9

ESCALA: 1:20

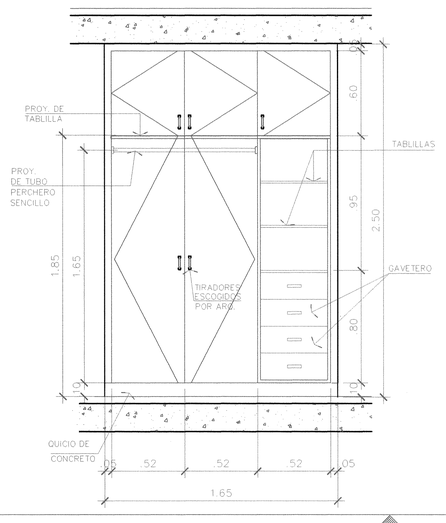

ELEVACION

APTO D (N2700)

CL-6A

ESCALA: 1:20

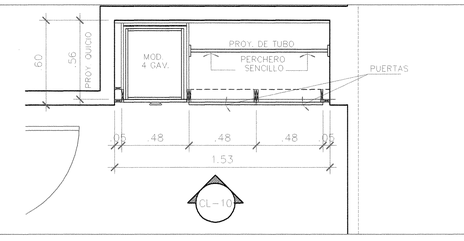

AMPL. CLOSET CL-10

ESCALA: 1:20

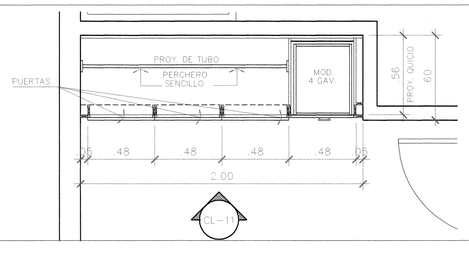

AMPL. CLOSET CL-11

ESCALA: 1:20

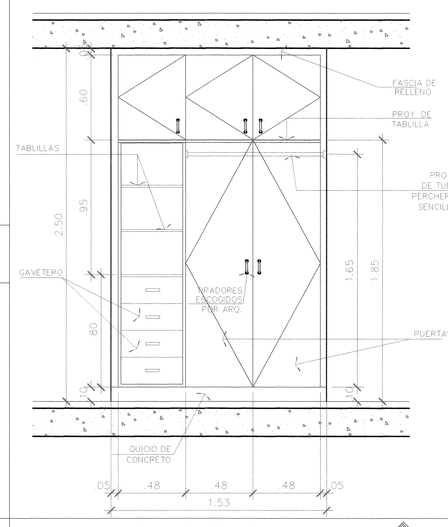

ELEVACION

APTO G, F (N-100 @ N-400)

CL-10

ESCALA: 1:20

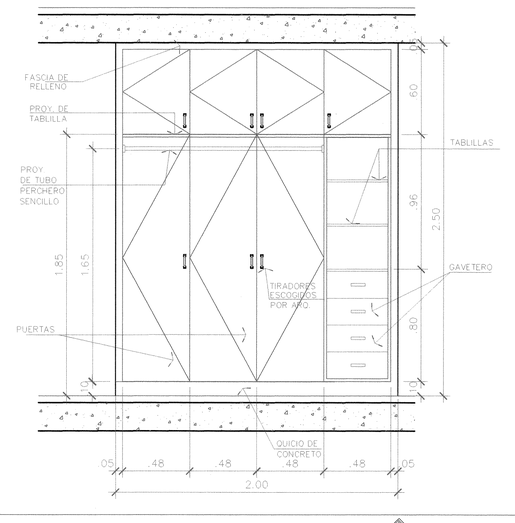

ELEVACION

APTO P.B (N000)

CL-11

ESCALA: 1:20

INGENIERIA MUNICIPAL
DISTRITO DE SAN CARLOS
APROBADO
INGENIERO MUNICIPAL
FECHA 22/8/11

La Chorrera, 11 de agosto de 20 11
Resolución No. 316-11 Plano No. 14-18
Se aprueba lo registrado en este plano con tener las condiciones requeridas
Ing. Municipal de La Chorrera

Cuerpo de Bomberos
OFICINA DE SEGURIDAD
La Chorrera
Dirección de Seguridad

FELIPE GONZÁLEZ LINCK
ARQUITECTO
LICENCIA No. 7171-88
FIRMA
LEY 15 DEL 26 DE ENERO DE 1959
JUNTA TÉCNICA DE INGENIERÍA Y ARQUITECTURA

FELIFE GONZÁLEZ LINCK
ARQUITECTO
Tel. -- 66771610 -- Fax 302-2457 | 64036839

DISEÑO ARQUITECTÓNICO	Arq. Vicente Cortes Arq. Igor Cortes
DESARROLLO	Arq. Igor Cortes Arq. Ilem Segismond Arq. Nancy Urriola
PROYECTO ESTRUCTURAL	Ing. Ricauter Bowen
PROYECTO ELÉCTRICO	Ing. Edgar Naranjo
PROYECTO DE PLOMERÍA	Ing. Gilberto Ayala

PROYECTO

Residencial El Palmar

UBICACIÓN

COMUNIDAD DE 'EL PALMAR'
DTTO. DE SAN CARLOS - CORREGIMIENTO DE SAN CARLOS
PANAMÁ.

SOCIEDAD PROMOTORA

Inversiones Decuria, S.A.

Representante legal: IGOR CORTES
Número de cédula o pasaporte: 8C054493

INGENIERÍA MUNICIPAL

PLANO

- DETALLES DE CLOSETS APTOS D, E, F, G y PLANTA BAJA
NIVEL +2700
NIVEL 00 @ -400
ESCALA 1:20

ARCHIVO .DWG	CLOSETS
FECHA	30/08/2010
FECHA MODIFICACIÓN	DD/MM/AAAA

ARQUITECTURA | HOJA: 43 | DE: 65

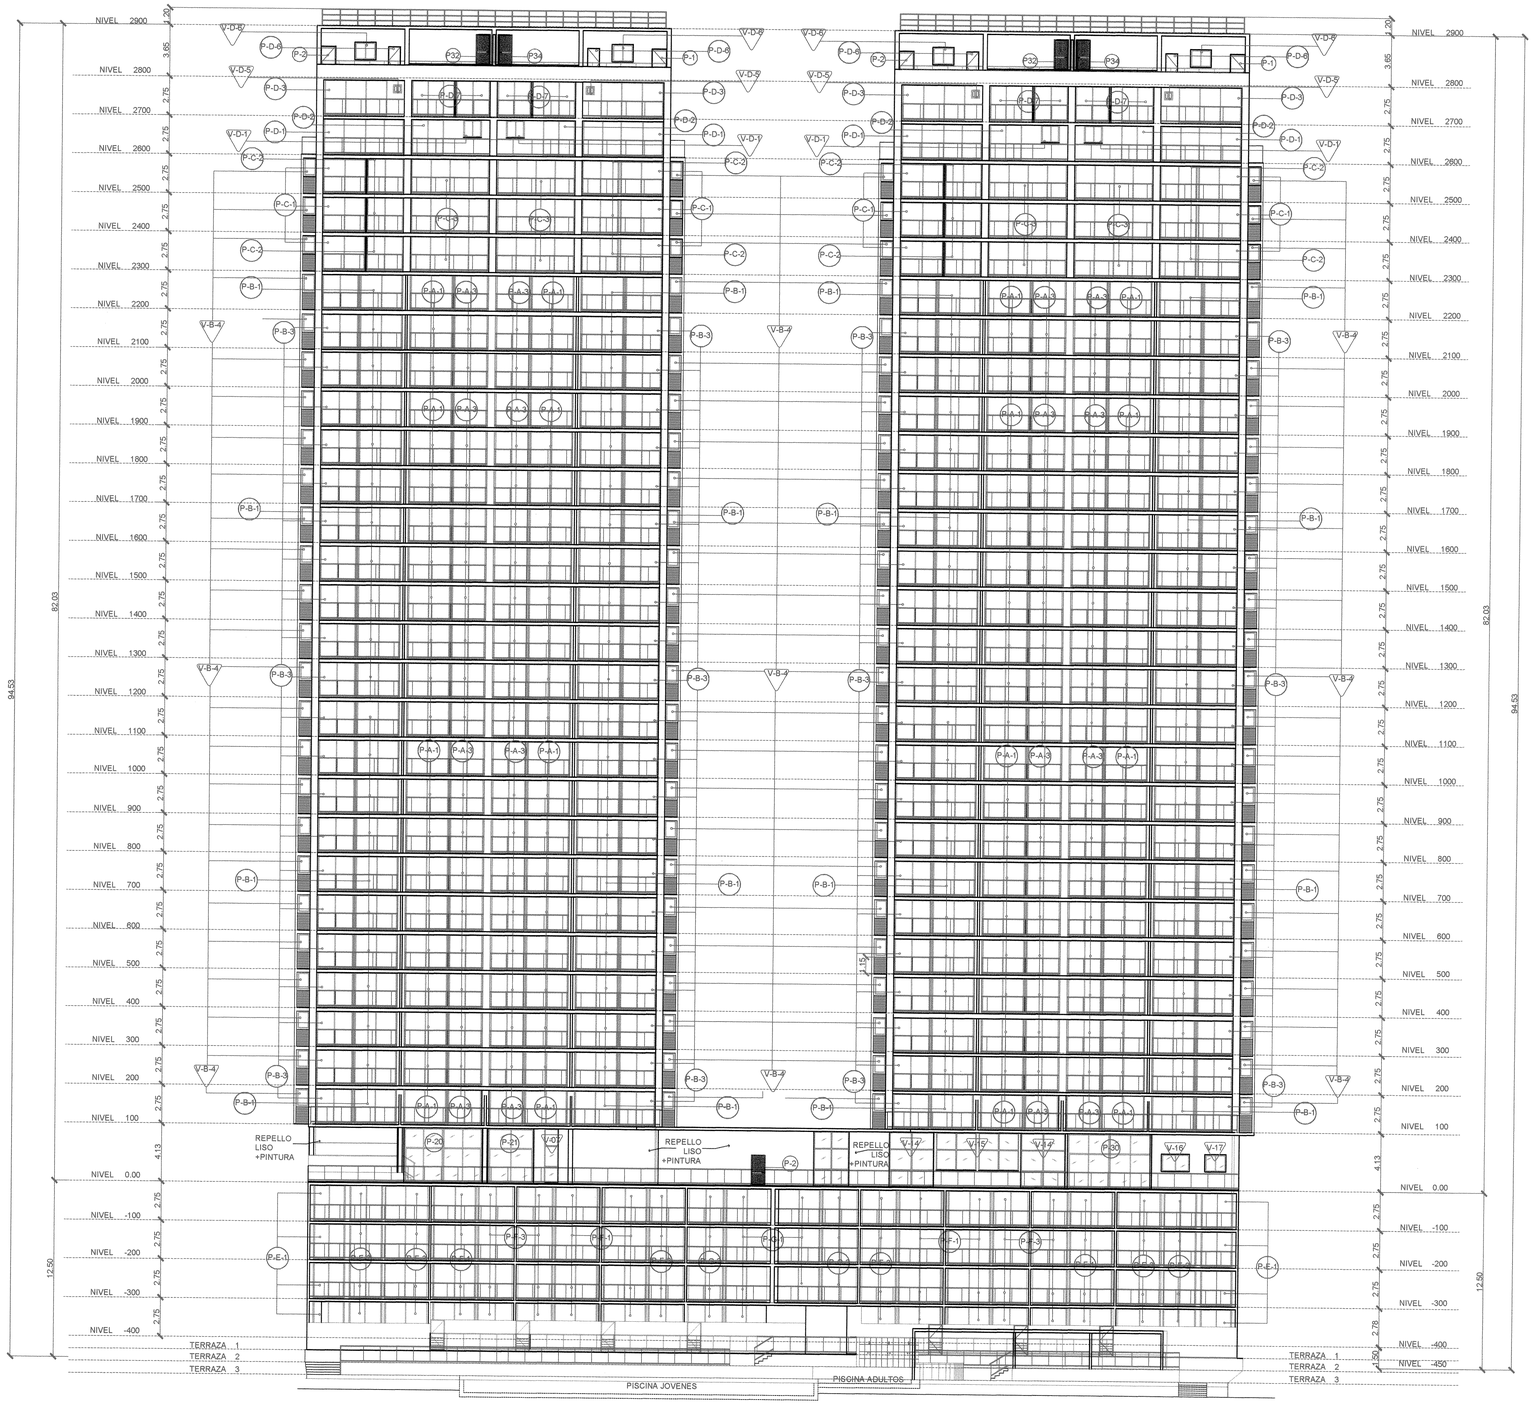

AR ELEVACION FRONTAL

ESCALA: 1:200

INGENIERIA MUNICIPAL
DISTRITO DE SAN CARLOS
APROBADO
INGENIERO MUNICIPAL
FECHA 12/9/11

Cuerpo de Bomberos
OFICINA DE SEGURIDAD
La Chorrera
Se aprueba Diseño No. 316 Agosto 2011
Recibo No. 16482
Se aprueba bajo el cumplimiento de los puntos por llenar las condiciones requeridas
Jefe de Seguridad

FELIPE GONZALEZ LINCK
ARQUITECTO
LICENCIA No. 97-188
FIRMA
LEY 15 DEL 26 DE ENERO DE 1959
JUNTA TECNICA DE INGENIERIA Y ARQUITECTURA

FELIFE GONZÁLEZ LINCK
ARQUITECTO
Tel. – 86771610 – Fax 392-2457 | 64035839

DISEÑO ARQUITECTÓNICO	Arq. Vicente Cortes Arq. Igor Cortes
DESARROLLO	Arq. Igor Cortes Arq. Ilem Segismond Arq. Nancy Urriola
PROYECTO ESTRUCTURAL	Ing. Ricauter Bowen
PROYECTO ELÉCTRICO	Ing. Edgar Naranjo
PROYECTO DE PLOMERÍA	Ing. Gilberto Ayala

PROYECTO

Residencial El Palmar

UBICACIÓN

COMUNIDAD DE 'EL PALMAR'
DTTO. DE SAN CARLOS - CORREGIMIENTO DE SAN CARLOS
PANAMÁ

SOCIEDAD PROMOTORA

Inversiones Decuria, S.A.

Representante legal: IGOR CORTES
Número de cédula o pasaporte: BC054493

INGENIERÍA MUNICIPAL

PLANO

- ELEVACION FRONTAL
ESCALA 1:200

ARCHIVO .DWG	ELEVACION FRONTAL
FECHA	30/08/2010
FECHA MODIFICACIÓN	DD/MM/AAAA

ARQUITECTURA	HOJA: 44	DE: 65

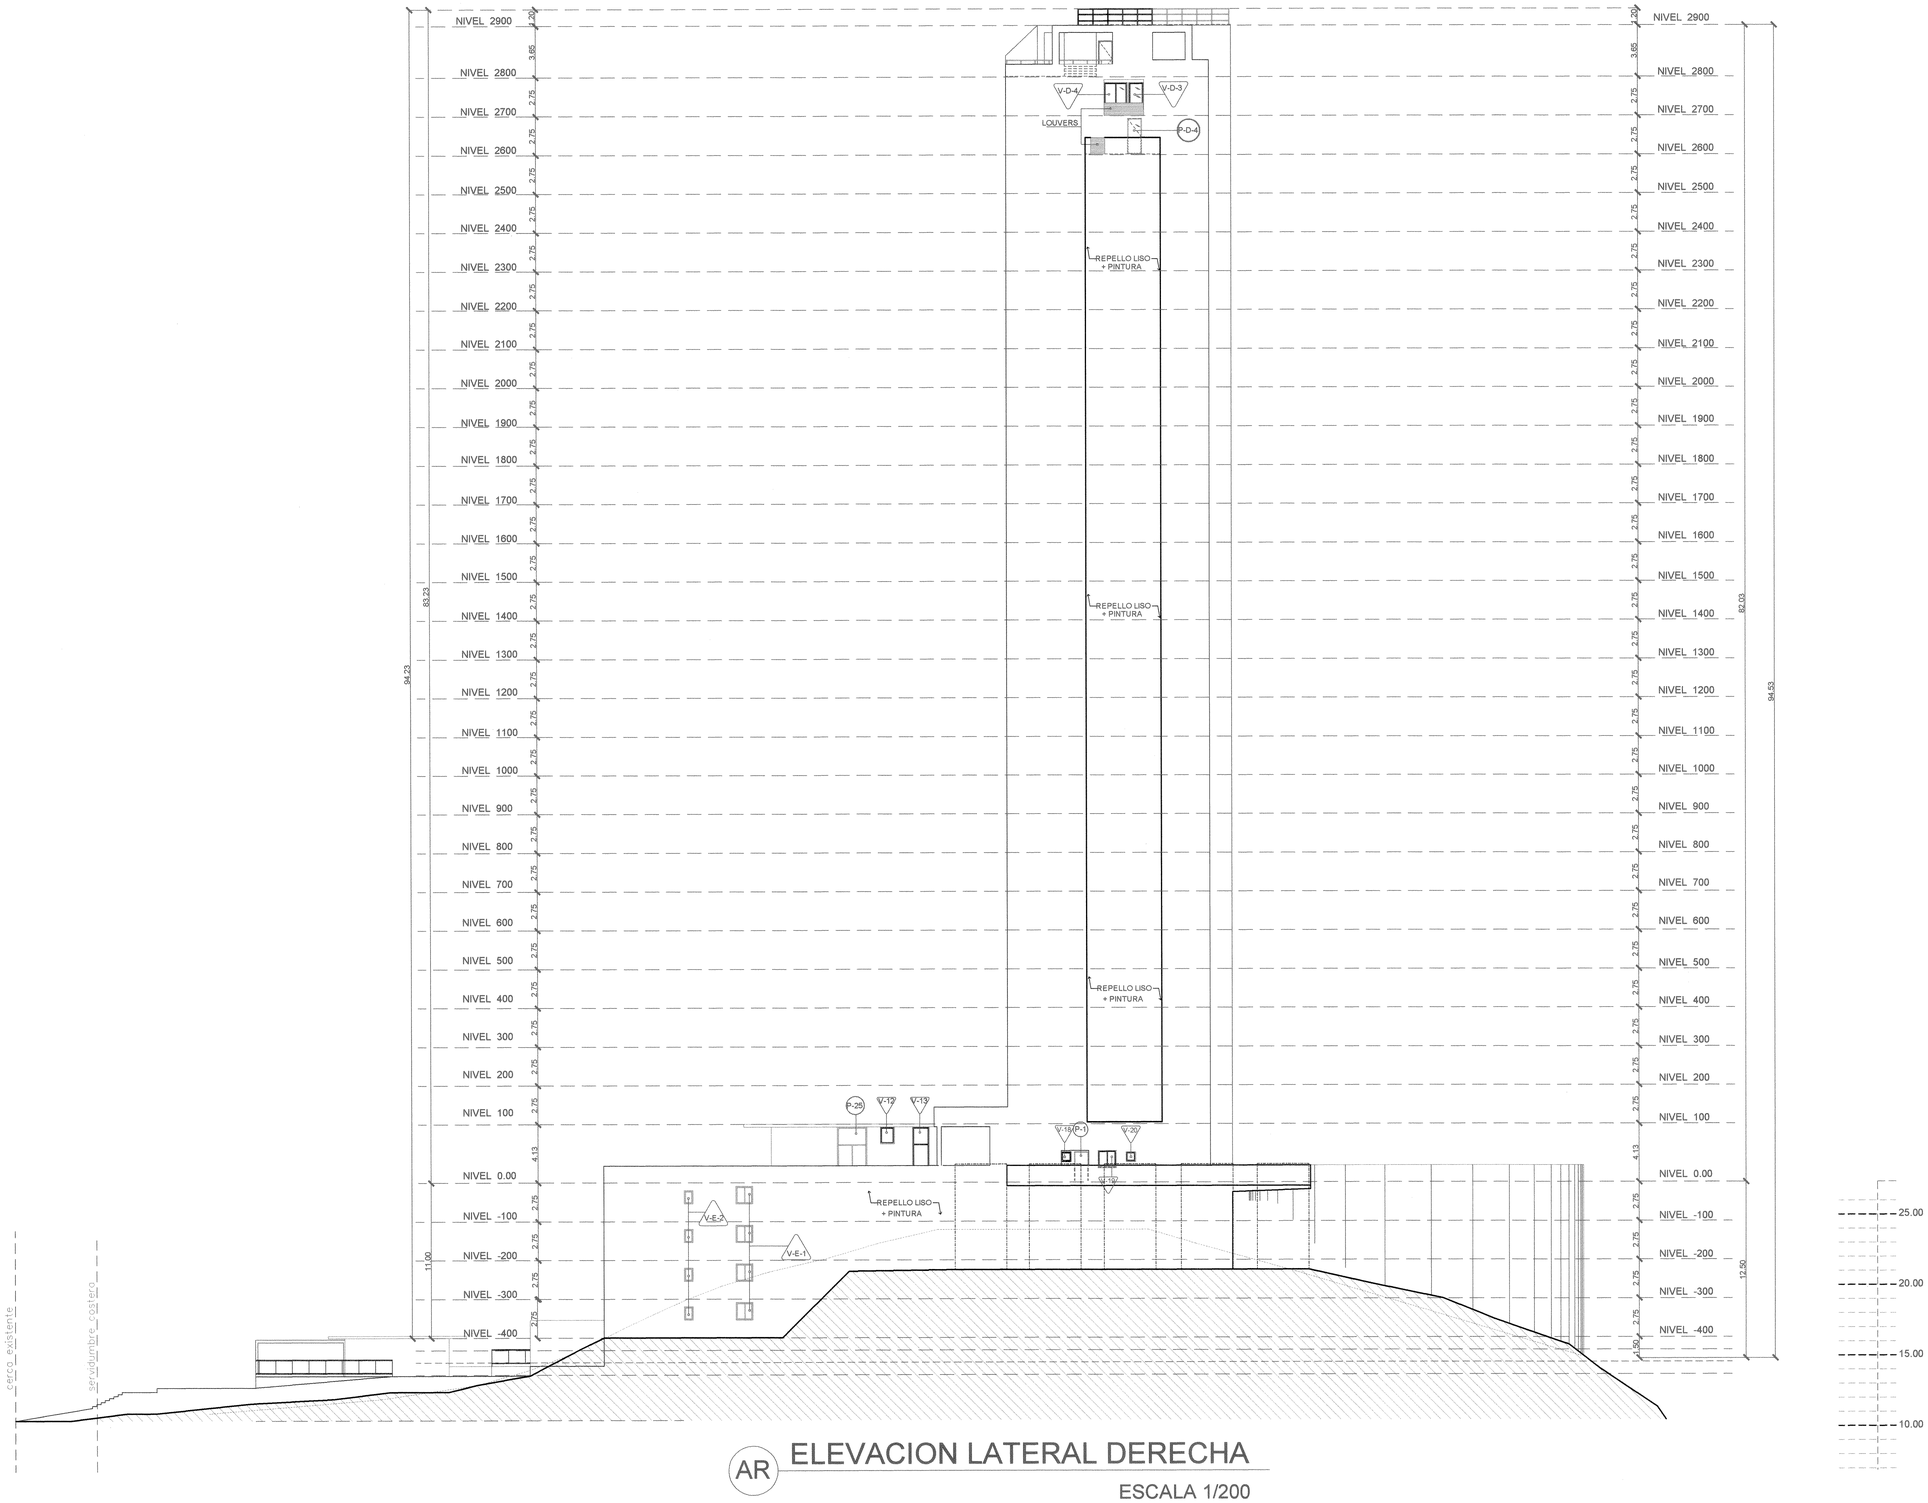

AR ELEVACION LATERAL DERECHA

ESCALA 1/200

INGENIERIA MUNICIPAL
DISTRITO DE SAN CARLOS
APROBADO
INGENIERO MUNICIPAL
FECHA: 22/8/11

Cuerpo de Bomberos
OFICINA DE SEGURIDAD
La Chorrera
La Chorrera, 11 de agosto de 2011
Resolución No. 211 Plano No. 16-159
Se aprueba el registro de este plano por llenar las condiciones requeridas
Oficina de Seguridad

FELIPE GONZALEZ LINCK
ARQUITECTO
IDONEIDAD No. 77-188
LEY 15 DEL 26 DE ENERO DE 1959
JUNTA TECNICA DE INGENIERIA Y ARQUITECTURA

FELIFE GONZÁLEZ LINCK
ARQUITECTO
Tel. – 66771610 – Fax 392-2457 | 64035839

DISEÑO ARQUITECTÓNICO	Arq. Vicente Cortes Arq. Igor Cortes
DESARROLLO	Arq. Igor Cortes Arq. Ilem Segismond Arq. Nancy Urriola
PROYECTO ESTRUCTURAL	Ing. Ricauter Bowen
PROYECTO ELÉCTRICO	Ing. Edgar Naranjo
PROYECTO DE PLOMERÍA	Ing. Gilberto Ayala

PROYECTO

Residencial El Palmar

UBICACIÓN

COMUNIDAD DE 'EL PALMAR'
DTTO. DE SAN CARLOS - CORREGIMIENTO DE SAN CARLOS
PANAMÁ

SOCIEDAD PROMOTORA

Inversiones Decuria, S.A.

Representante legal: IGOR CORTES
Número de cédula o pasaporte: 8C054493

INGENIERÍA MUNICIPAL

PLANO

- ELEVACION LAT. DERECHA
ESCALA 1:200

ARCHIVO .DWG	ELEVACION LATERAL DERECHA
FECHA	30/08/2010
FECHA MODIFICACIÓN	DD/MM/AAAA

ARQUITECTURA | HOJA: 45 | DE: 65

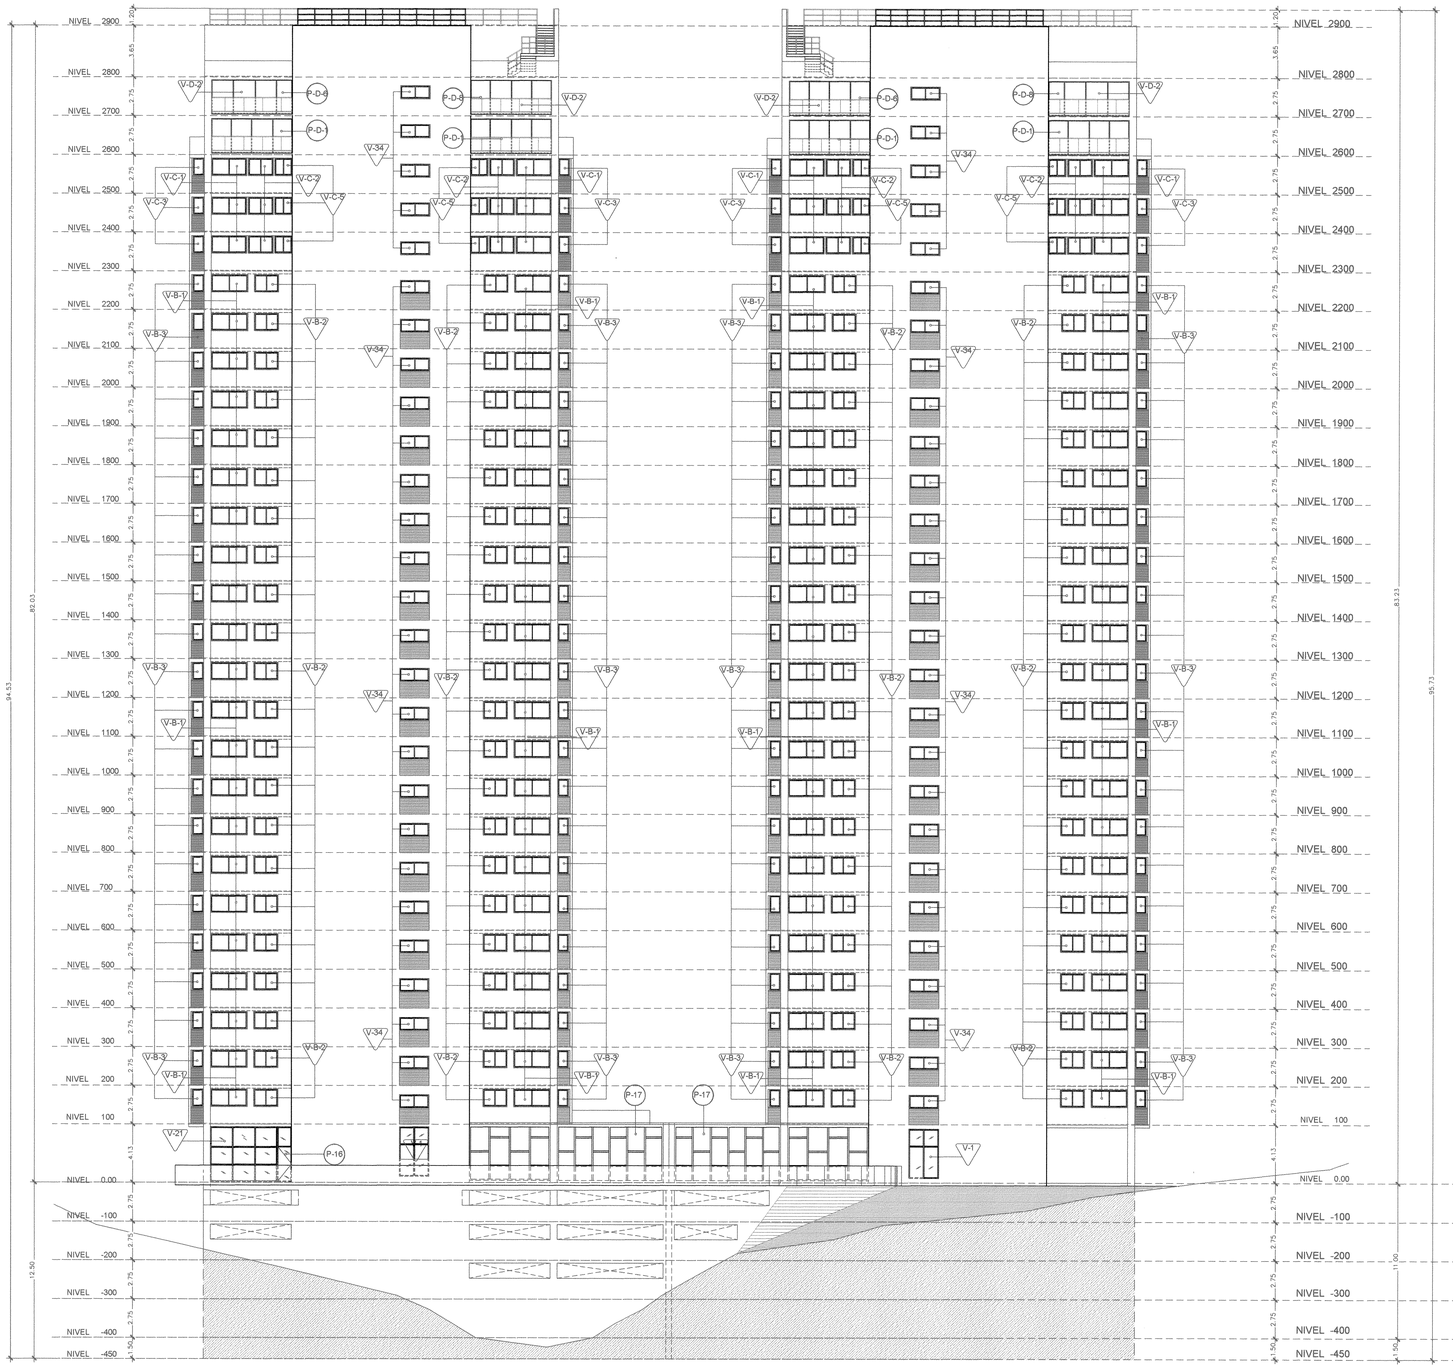

AR ELEVACION POSTERIOR
ESCALA 1:200

INGENIERIA MUNICIPAL
DISTRITO DE SAN CARLOS
APROBADO
INGENIERO MUNICIPAL
FECHA 22/8/11

Cuerpo de Bomberos
OFICINA No. 5-2 (Sede)
La Chorrera
La Chorrera, 11 de Agosto de 2011
Revisión No. 2 Plano No. 46
Se sanciona el registro de este plano por llenar las condiciones requeridas.
Jefe de la Oficina de Seguridad

FELIFE GONZALEZ LINCK
ARQUITECTO
IDONEIDAD No. 77-1188
LEY 15 DE 26 DE ENERO DE 1959
JUNTA TECNICA DE INGENIERIA Y ARQUITECTURA

FELIFE GONZÁLEZ LINCK
ARQUITECTO
Tel. – 66771610 – Fax 392-2457 | 64035839

DISEÑO ARQUITECTÓNICO	Arq. Vicente Cortes Arq. Igor Cortes
DESARROLLO	Arq. Igor Cortes Arq. Ilem Segismond Arq. Nancy Urriola
PROYECTO ESTRUCTURAL	Ing. Ricauter Bowen
PROYECTO ELÉCTRICO	Ing. Edgar Naranjo
PROYECTO DE PLOMERÍA	Ing. Gilberto Ayala

PROYECTO
Residencial El Palmar

UBICACIÓN
COMUNIDAD DE 'EL PALMAR'
DTTO. DE SAN CARLOS - CORREGIMIENTO DE SAN CARLOS
PANAMÁ.

SOCIEDAD PROMOTORA
Inversiones Decuria, S.A.
Representante legal: IGOR CORTES
Número de cédula o pasaporte: BC054493

INGENIERÍA MUNICIPAL

PLANO
- ELEVACION POSTERIOR
ESCALA 1:200

ARCHIVO .DWG	ELEVACION POSTERIOR
FECHA	30/08/2010
FECHA MODIFICACIÓN	DD/MM/AAAA

ARQUITECTURA | HOJA: 46 | DE: 65

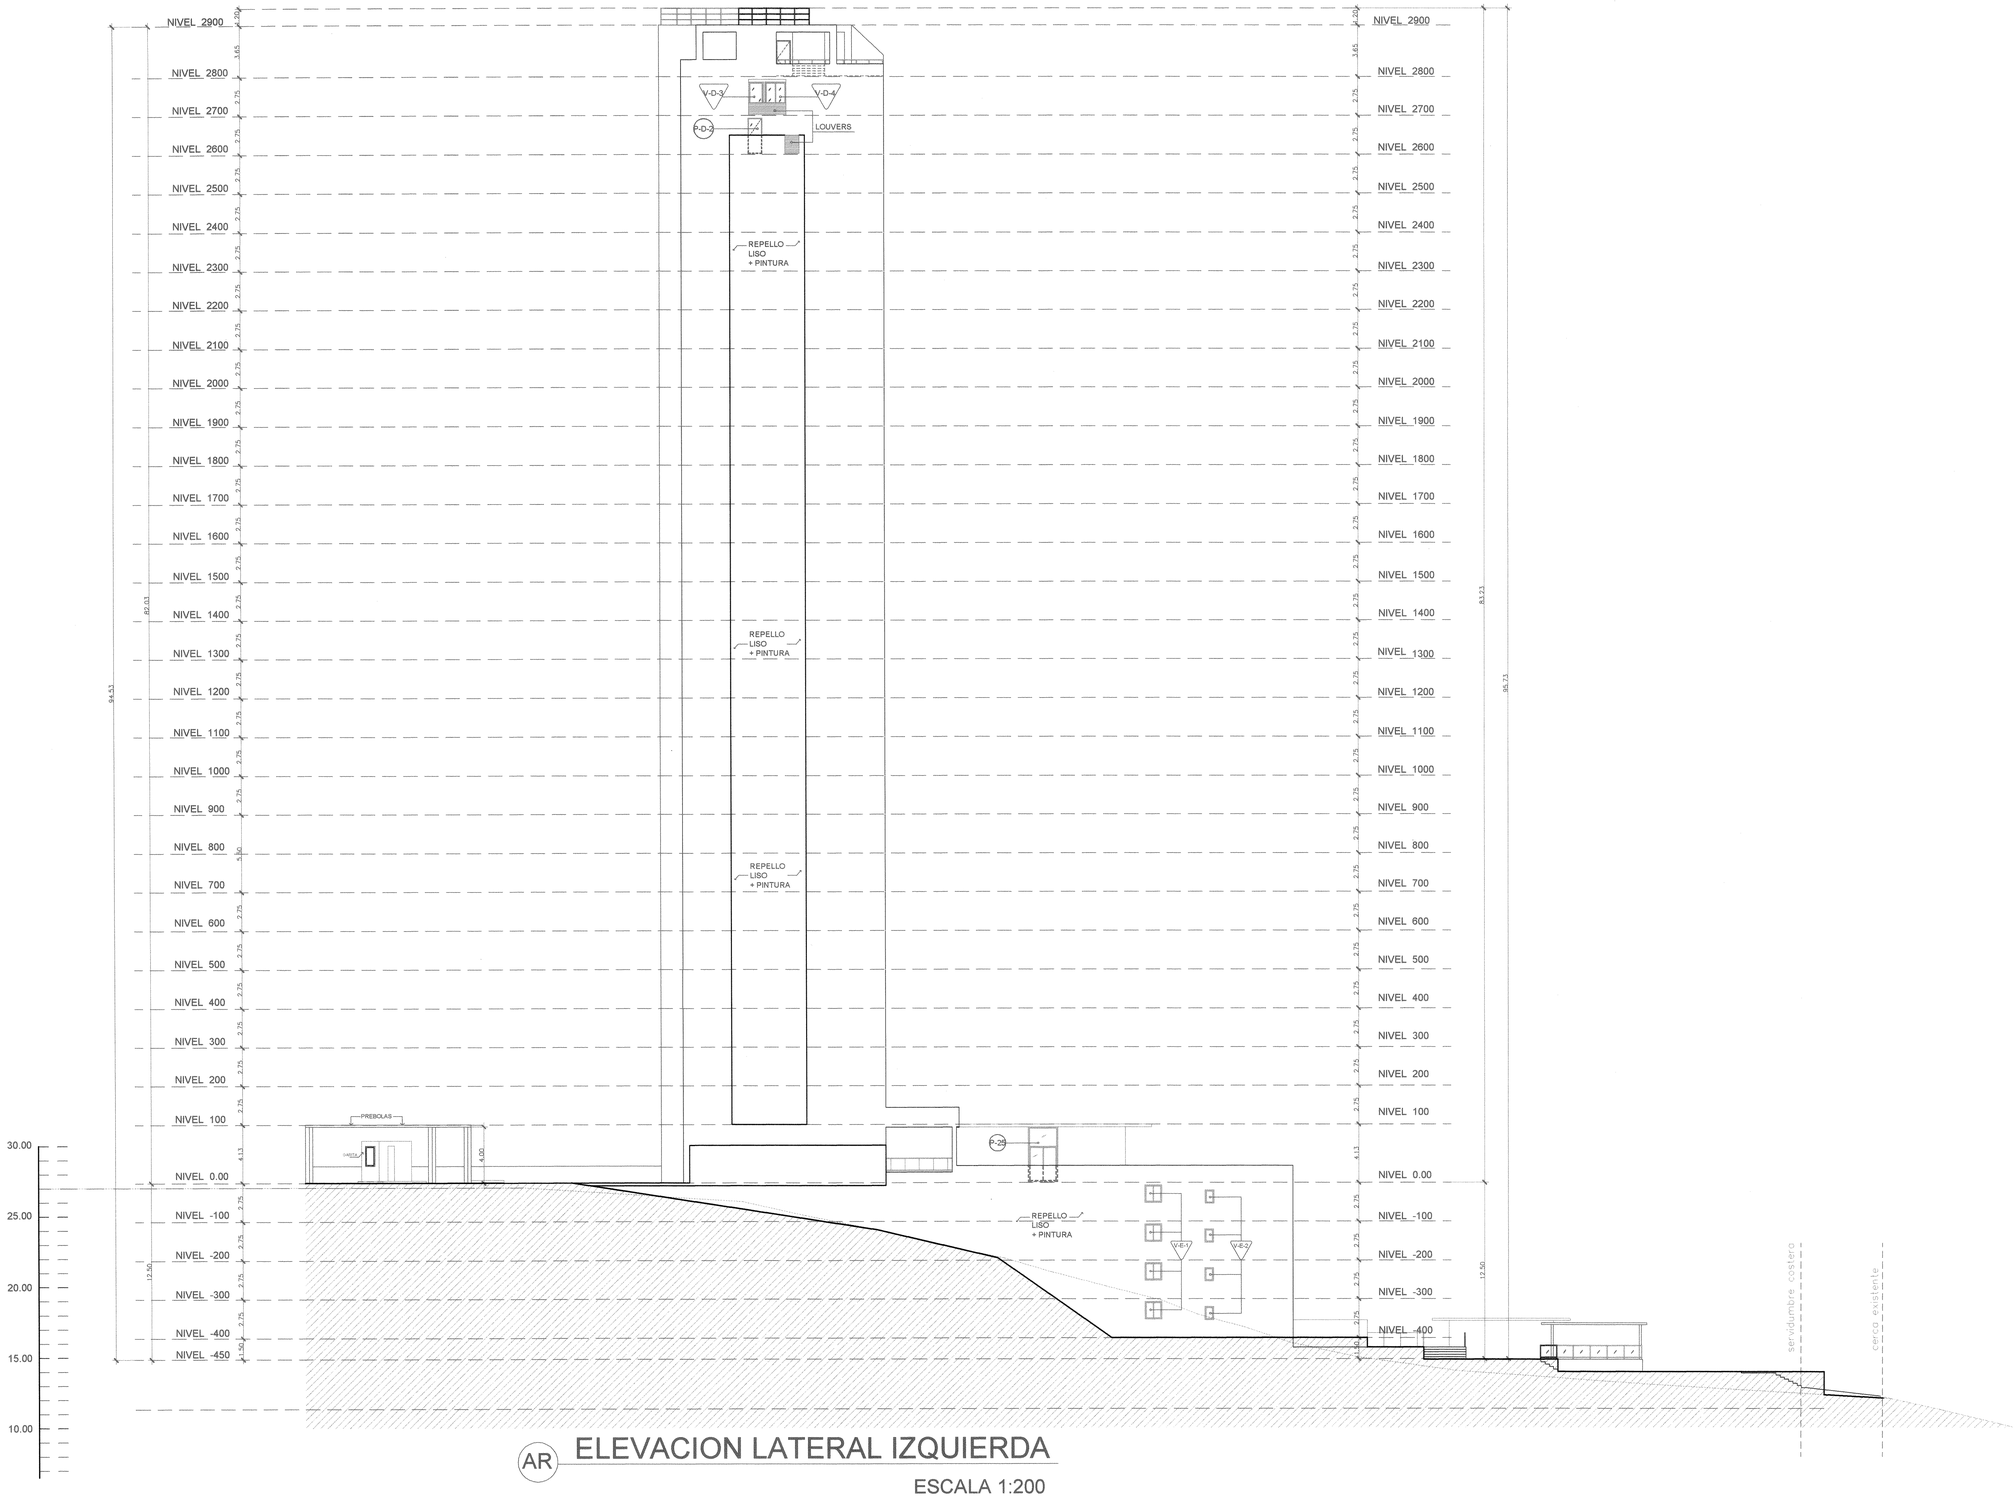

AR ELEVACION LATERAL IZQUIERDA

ESCALA 1:200

INGENIERIA MUNICIPAL
DISTRITO DE SAN CARLOS
APROBADO
INGENIERO MUNICIPAL
FECHA 22/8/11

Cuerpo de Bomberos
OFICINA DE SEGURIDAD
La Chorrera
La Chorrera, 11 de Agosto de 2011
Resolución No. 314 Plano No. 16-48
Se aprueba el registro de este plano por llenar las condiciones requeridas.
Jefe de la Oficina de Seguridad

FELIPE GONZALEZ LINCK
ARQUITECTO
IDONEIDAD No. 7771-188
LEY 15 DEL 26 DE ENERO DE 1959
JUNTA TECNICA DE INGENIERIA Y ARQUITECTURA

FELIFE GONZÁLEZ LINCK
ARQUITECTO
Tel. -- 66771610 -- Fax 392-2457 | 64035839

DISEÑO ARQUITECTÓNICO	Arq. Vicente Cortes Arq. Igor Cortes
DESARROLLO	Arq. Igor Cortes Arq. Ilem Segismond Arq. Nancy Urriola
PROYECTO ESTRUCTURAL	Ing. Ricauter Bowen
PROYECTO ELÉCTRICO	Ing. Edgar Naranjo
PROYECTO DE PLOMERÍA	Ing. Gilberto Ayala

PROYECTO

Residencial El Palmar

UBICACIÓN

COMUNIDAD DE "EL PALMAR"
DTTO. DE SAN CARLOS - CORREGIMIENTO DE SAN CARLOS
PANAMÁ

SOCIEDAD PROMOTORA

Inversiones Decuria, S.A.
Representante legal: IGOR CORTES
Número de cédula o pasaporte: BC054493

INGENIERÍA MUNICIPAL

PLANO

- ELEVACION LATERAL IZQUIERDA

ARCHIVO .DWG	ELEVACION LATERAL IZQUIERDA
FECHA	30/08/2010
FECHA MODIFICACIÓN	DD/MM/AAAA

ARQUITECTURA | HOJA: 47 | DE: 65

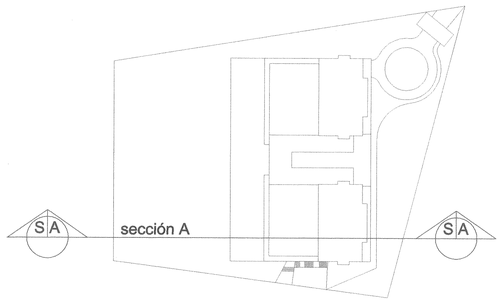

PLANO LLAVE

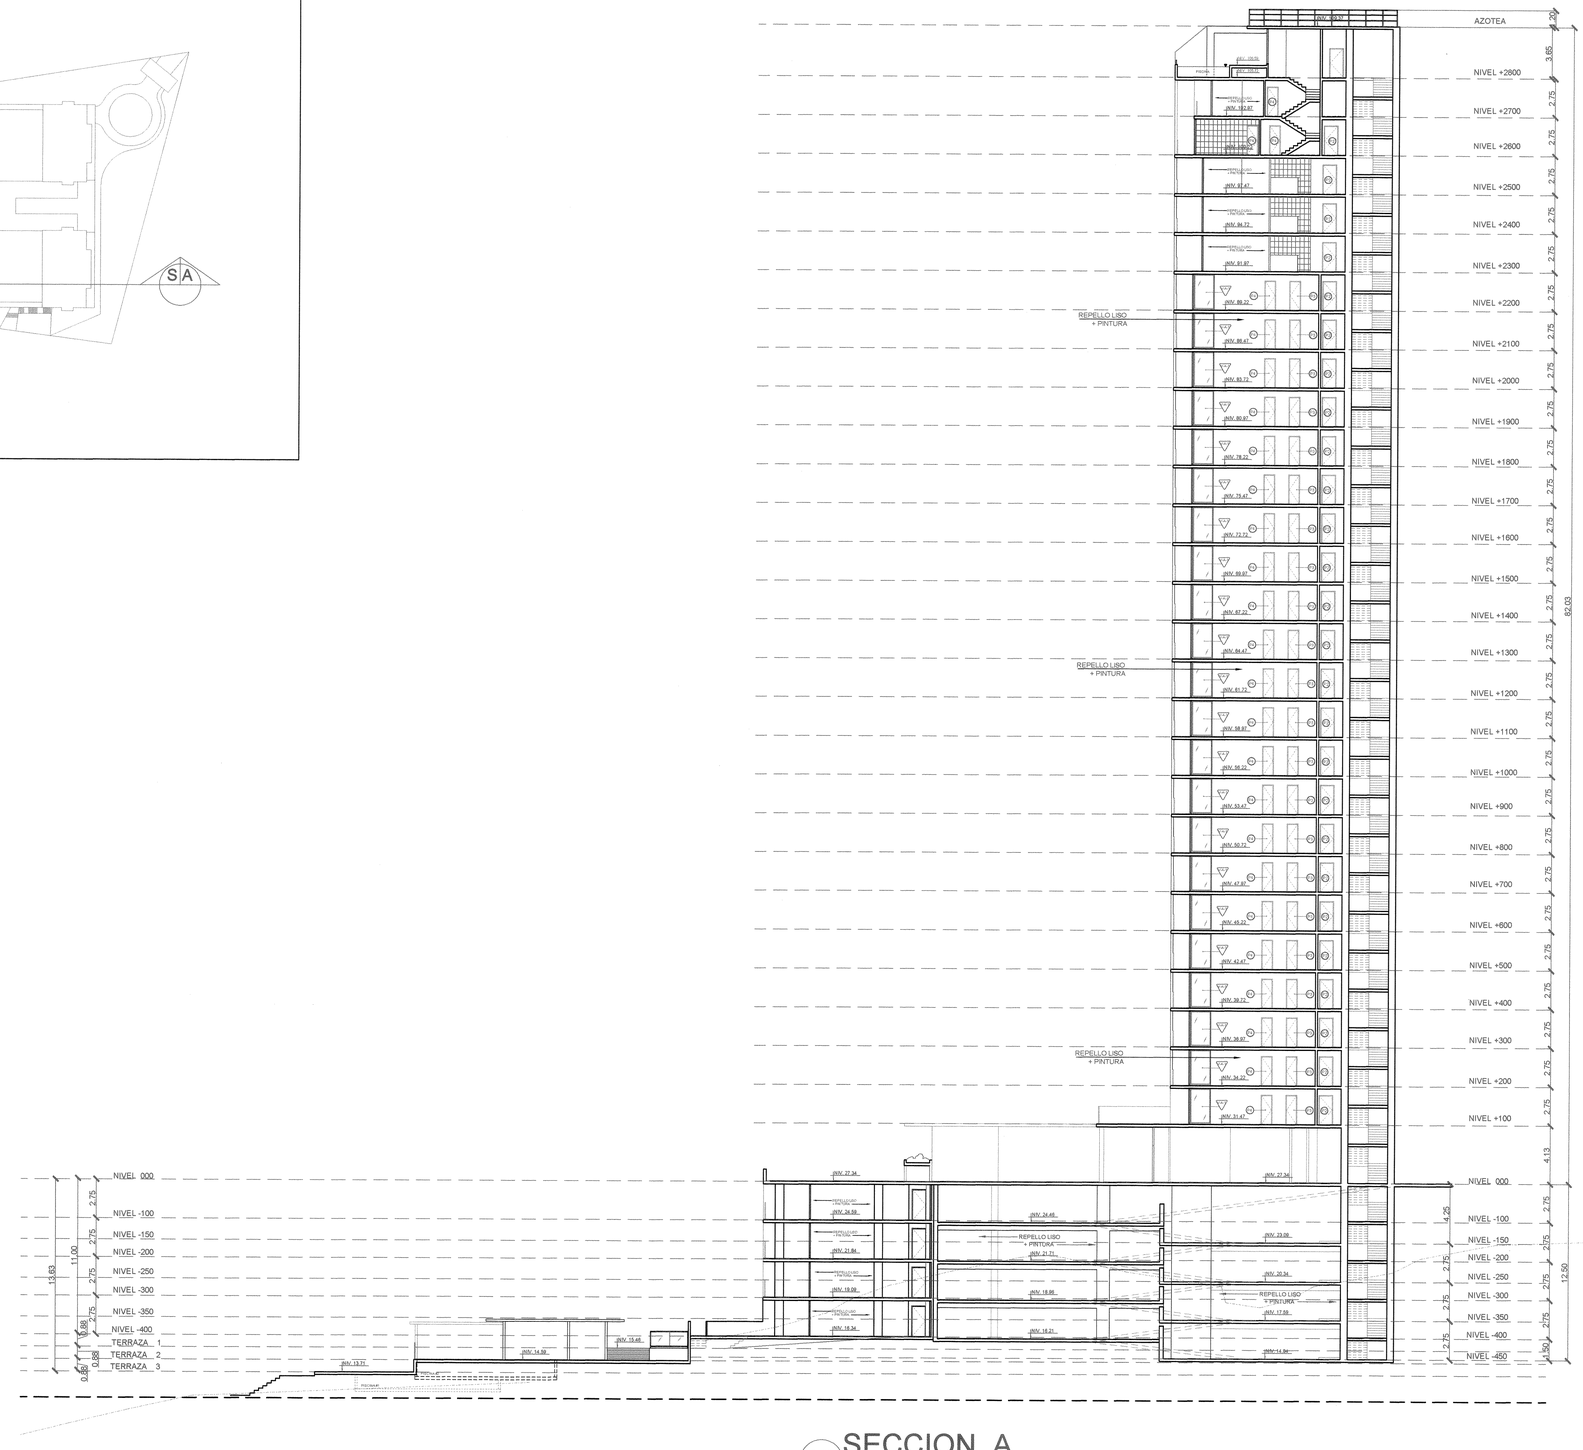

AR SECCION A

ESC. 1:200

INGENIERIA MUNICIPAL
DISTRITO DE SAN CARLOS
APROBADO
INGENIERO MUNICIPAL
FECHA 22/8/11

Cuerpo de Bomberos
OFICINA de SEGURIDAD
La Chorrera, 11 de agosto de 2011
Resolución No. 316 Plano No. 16-18
Se aprueba el registro de este plano por llenar las condiciones requerida.
Jefe de la Oficina de Seguridad

FELIPE GONZALEZ LINCK
ARQUITECTO
LICENCIA No. 7771-198
LEY 15 DEL 26 DE ENERO DE 1959
JUNTA TECNICA DE INGENIERIA Y ARQUITECTURA

FELIFE GONZÁLEZ LINCK
ARQUITECTO
Tel. -- 66771810 -- Fax 392-2457 | 64035839

DISEÑO ARQUITECTÓNICO	Arq. Vicente Cortes Arq. Igor Cortes
DESARROLLO	Arq. Igor Cortes Arq. Ilem Segismond Arq. Nancy Urriola
PROYECTO ESTRUCTURAL	Ing. Ricauter Bowen
PROYECTO ELÉCTRICO	Ing. Edgar Naranjo
PROYECTO DE PLOMERÍA	Ing. Gilberto Ayala

PROYECTO

Residencial El Palmar

UBICACIÓN

COMUNIDAD DE 'EL PALMAR'
DTTO. DE SAN CARLOS - CORREGIMIENTO DE SAN CARLOS
PANAMÁ

SOCIEDAD PROMOTORA

Inversiones Decuria, S.A.

Representante legal: IGOR CORTES
Número de cédula o pasaporte: 8CO54493

INGENIERÍA MUNICIPAL

PLANO

- SECCION A
ESCALA 1:200

ARCHIVO .DWG	SECCION A y B
FECHA	30/08/2010
FECHA MODIFICACIÓN	DD/MM/AAAA

ARQUITECTURA | HOJA: 48 | DE: 65

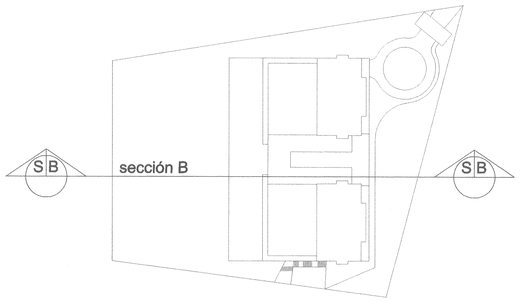

PLANO LLAVE

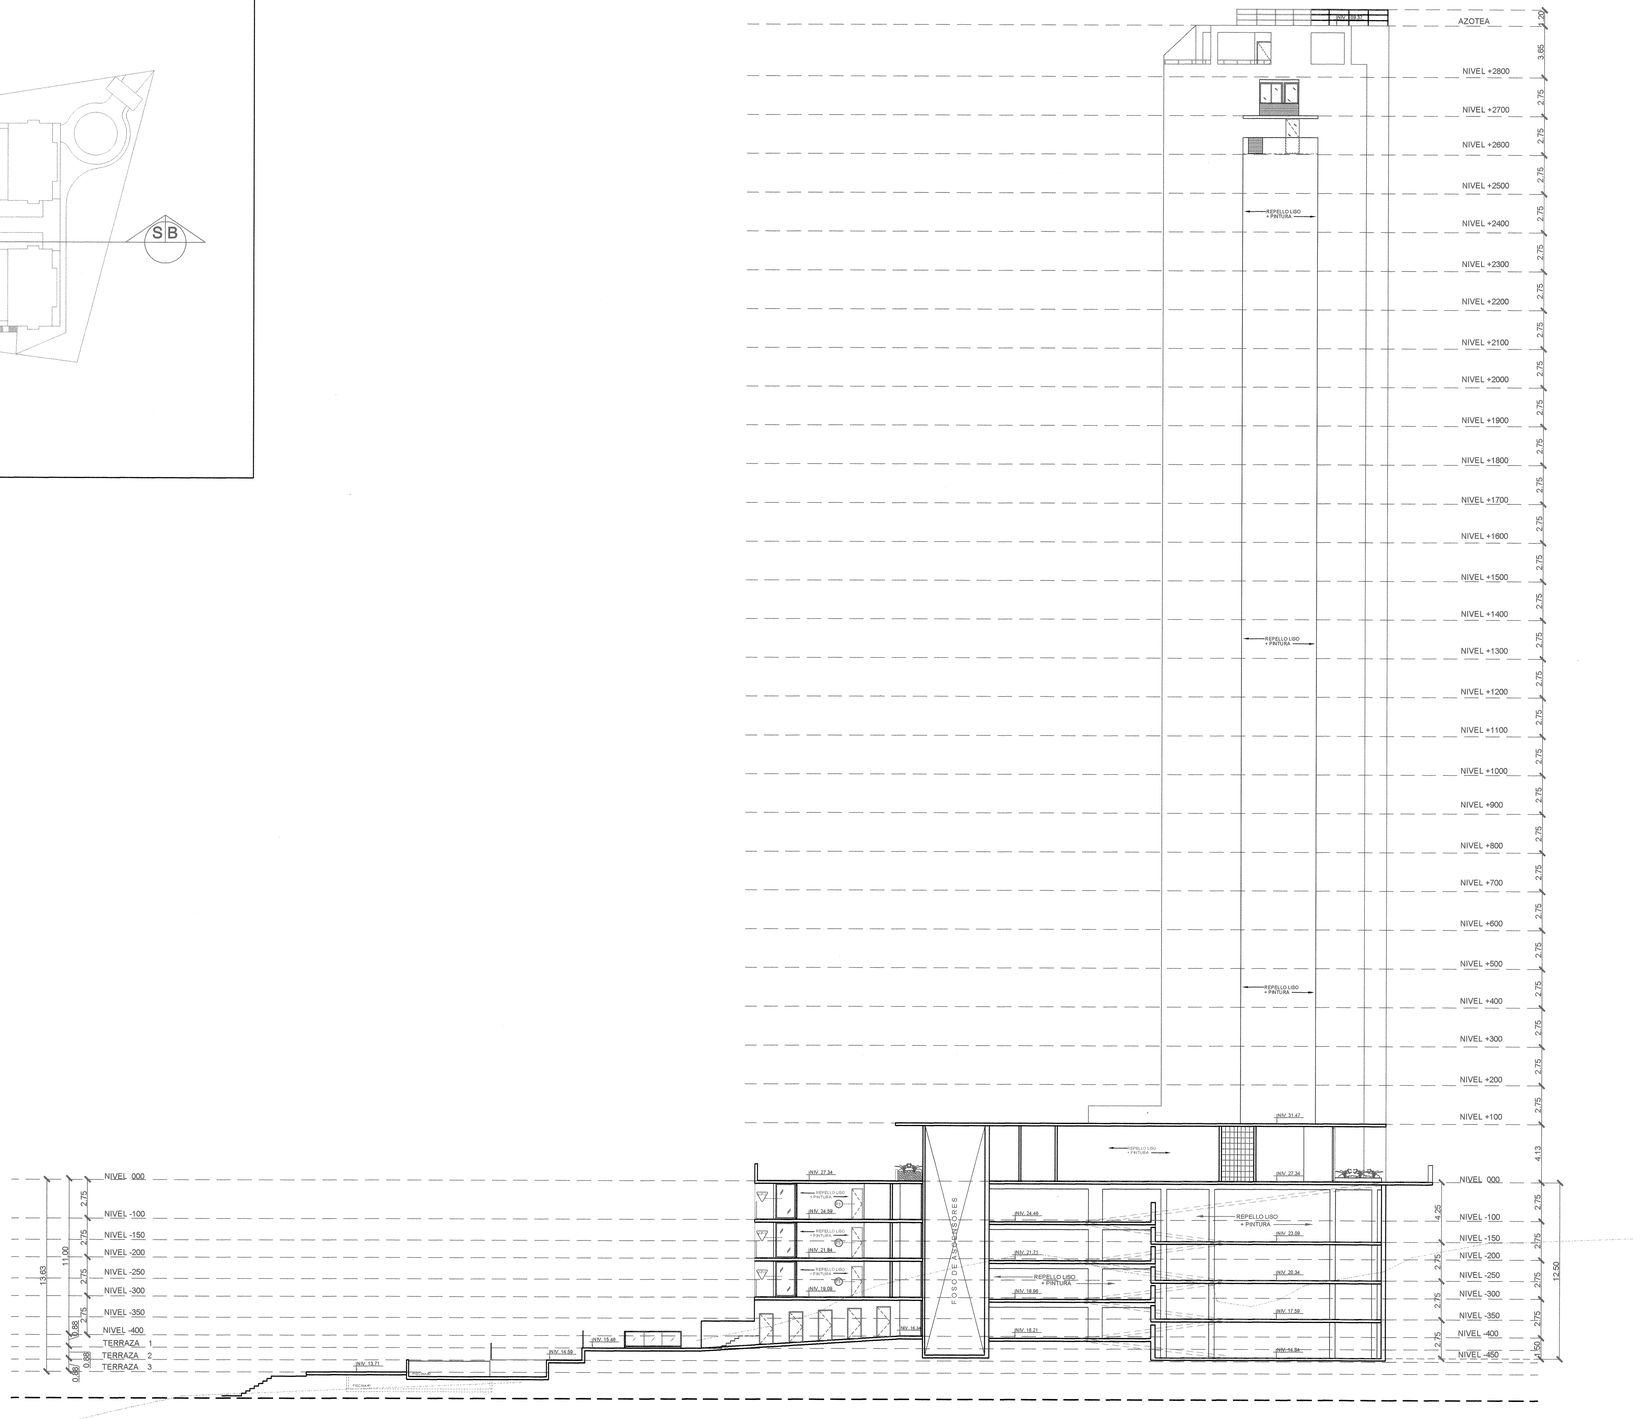

AR SECCION B

ESC. 1:200

INGENIERIA MUNICIPAL
DISTRITO DE SAN CARLOS
APROBADO
INGENIERO MUNICIPAL
FECHA 22/8/11

Cuerpo de Bomb.
OFICINA DE SEGURIDAD
La Chorrera
La Chorrera, ... de .....
Resolución No. ..... Plano No. .....
Se aprueba el registro de este plano por llenar las condiciones requeridas.
Jefe de la Oficina de Seguridad

FELIPE GONZALEZ LINCK
ARQUITECTO
LICENCIA No. 7771-185
LEY 15 DEL 26 DE ENERO DE 1959
JUNTA TECNICA DE INGENIERIA Y ARQUITECTURA

FELIFE GONZÁLEZ LINCK
ARQUITECTO
Tel. - 66771610 - Fax 392-2457 | 64035630

DISEÑO ARQUITECTÓNICO	Arq. Vicente Cortes Arq. Igor Cortes
DESARROLLO	Arq. Igor Cortes Arq. Ilem Segismond Arq. Nancy Urriola
PROYECTO ESTRUCTURAL	Ing. Ricauter Bowen
PROYECTO ELÉCTRICO	Ing. Edgar Naranjo
PROYECTO DE PLOMERÍA	Ing. Gilberto Ayala

PROYECTO

Residencial El Palmar

UBICACIÓN

COMUNIDAD DE 'EL PALMAR'
DTTO. DE SAN CARLOS - CORREGIMIENTO DE SAN CARLOS
PANAMÁ

SOCIEDAD PROMOTORA

Inversiones Decuria, S.A.

Representante legal: IGOR CORTES
Número de cédula o pasaporte: 8C054493

INGENIERÍA MUNICIPAL

PLANO

- SECCION B
ESCALA 1:200

ARCHIVO .DWG	SECCION A y B
FECHA	30/08/2010
FECHA MODIFICACIÓN	DD/MM/AAAA

ARQUITECTURA | HOJA: 49 | DE: 65

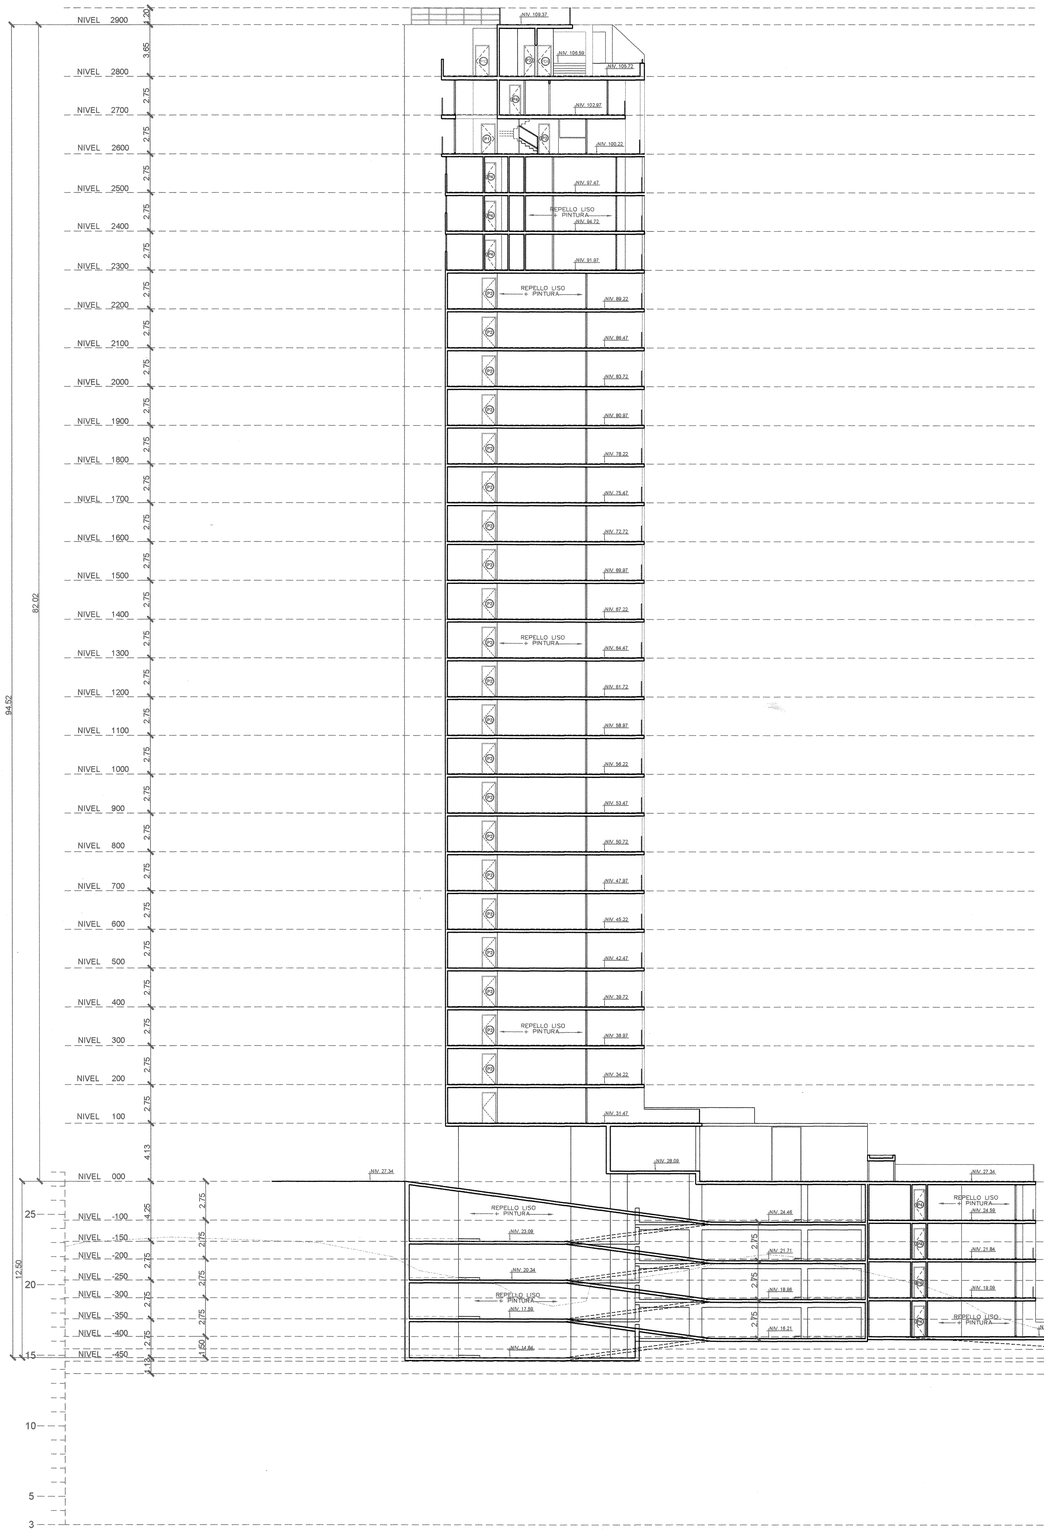

AR SECCION C

ESCALA 1:200

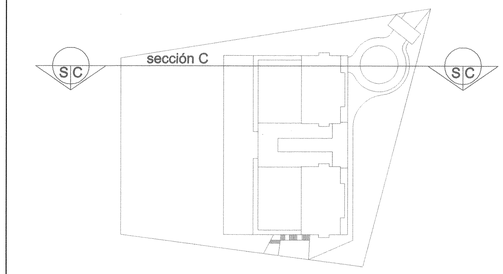

PLANO LLAVE

INGENIERIA MUNICIPAL
DISTRITO DE SAN CARLOS
APROBADO
INGENIERO MUNICIPAL
FECHA 22/8/11

Cuerpo de Bomberos
OFICINA DE SEGURIDAD
La Chorrera

La Chorrera, 11 de Agosto de 2011
Resolución No. 346 Plano No. 1488
Se aprueba el registro de este plano por llenar las condiciones requeridas

Jefe de la Oficina de Seguridad

FELIPE GONZALEZ LINCK
ARQUITECTO
IDONEIDAD No. 7-108
LEY 15 DEL 26 DE ENERO DE 1959
JUNTA TECNICA DE INGENIERIA Y ARQUITECTURA

FELIFE GONZÁLEZ LINCK
ARQUITECTO
Tel. – 66771610 – Fax 382-2457 | 64035839

DISEÑO ARQUITECTÓNICO	Arq. Vicente Cortes Arq. Igor Cortes
DESARROLLO	Arq. Igor Cortes Arq. Ilem Segismond Arq. Nancy Urriola
PROYECTO ESTRUCTURAL	Ing. Ricauter Bowen
PROYECTO ELÉCTRICO	Ing. Edgar Naranjo
PROYECTO DE PLOMERÍA	Ing. Gilberto Ayala

PROYECTO

Residencial El Palmar

UBICACIÓN

COMUNIDAD DE 'EL PALMAR'
DTTO. DE SAN CARLOS - CORREGIMIENTO DE SAN CARLOS
PANAMÁ

SOCIEDAD PROMOTORA

Inversiones Decuria, S.A.

Representante legal: IGOR CORTES
Número de cédula o pasaporte: 8C054493

INGENIERÍA MUNICIPAL

PLANO

- SECCION C
ESCALA 1:200

ARCHIVO .DWG	SECCION C y D
FECHA	30/08/2010
FECHA MODIFICACIÓN	DD/MM/AAAA

ARQUITECTURA | HOJA: 50 | DE: 65

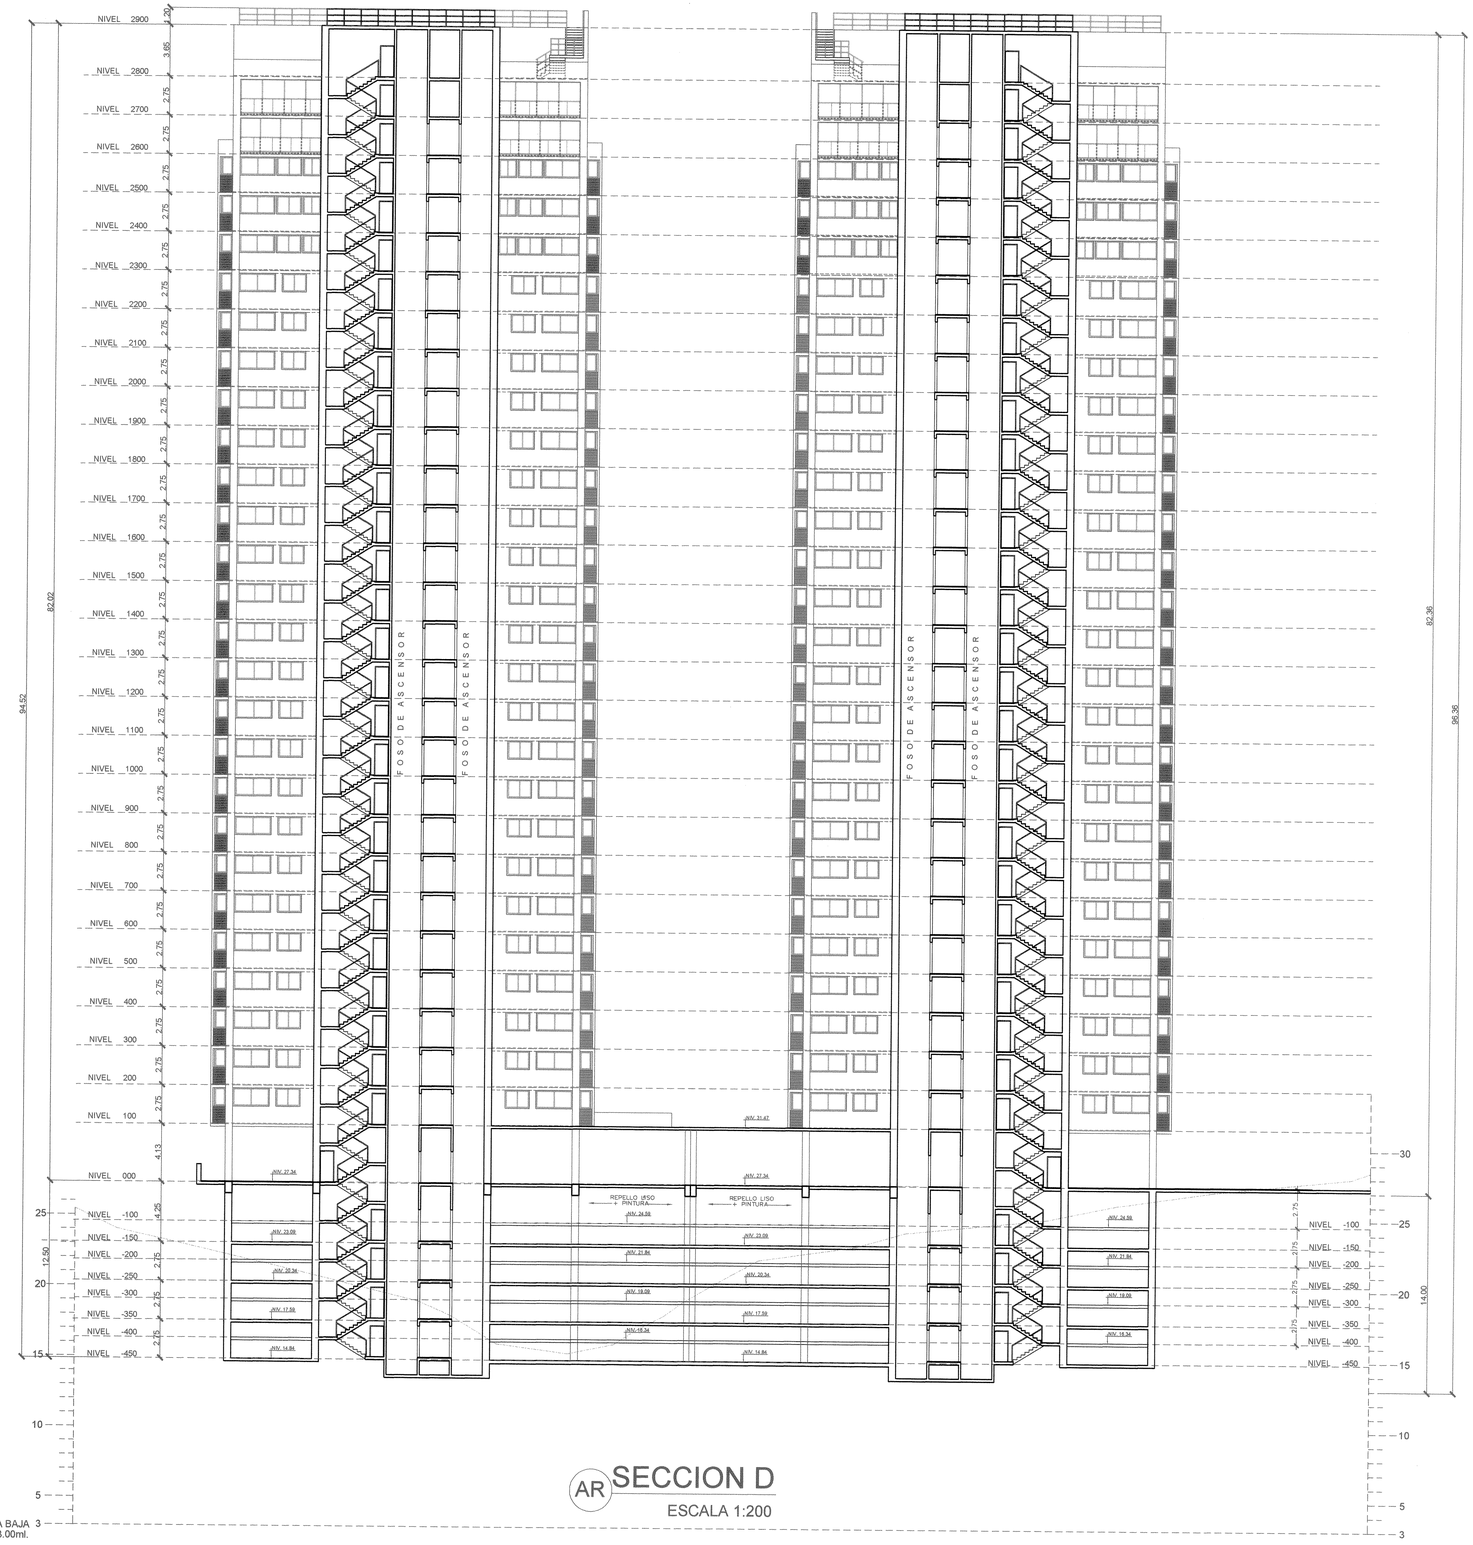

AR SECCION D

ESCALA 1:200

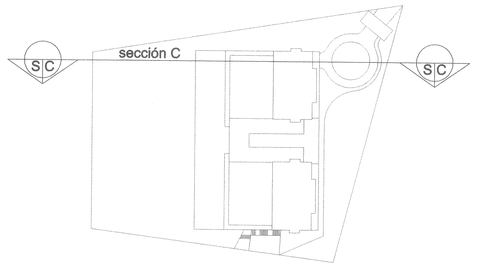

PLANO LLAVE

INGENIERÍA MUNICIPAL
DISTRITO DE SAN CARLOS
APROBADO
INGENIERO MUNICIPAL
FECHA 22/8/11

Cuerpo de Bomberos
OFICINA DE SEGURIDAD
La Chorrera, 11 de agosto de 2011
Resolución No. 316 Plano No. 4.2
Se aprueba el registro de este plano por llenar los condiciones requeridas

Jefe de la Oficina de Seguridad

FELIPE GONZALEZ LINCK
ARQUITECTO
LICENCIA No. 72-1-108
LEY 15 DEL 26 DE ENERO DE 1959
JUNTA TECNICA DE INGENIERIA Y ARQUITECTURA

FELIFE GONZÁLEZ LINCK
ARQUITECTO
Tel. -- 66771610 -- Fax 392-2457 | 64035839

DISEÑO ARQUITECTÓNICO	Arq. Vicente Cortes Arq. Igor Cortes
DESARROLLO	Arq. Igor Cortes Arq. Ilem Segismond Arq. Nancy Urriola
PROYECTO ESTRUCTURAL	Ing. Ricauter Bowen
PROYECTO ELÉCTRICO	Ing. Edgar Naranjo
PROYECTO DE PLOMERÍA	Ing. Gilberto Ayala

PROYECTO

Residencial El Palmar

UBICACIÓN

COMUNIDAD DE 'EL PALMAR'
DTTO. DE SAN CARLOS - CORREGIMIENTO DE SAN CARLOS
PANAMÁ.

SOCIEDAD PROMOTORA

Inversiones Decuria, S.A.

Representante legal: IGOR CORTES
Número de cédula o pasaporte: BC054493

INGENIERÍA MUNICIPAL

PLANO

- SECCION D
ESCALA 1:200

ARCHIVO .DWG	SECCION C y D
FECHA	30/08/2010
FECHA MODIFICACIÓN	DD/MM/AAAA

ARQUITECTURA | HOJA: 51 | DE: 65

CUADRO DE ACABADOS

AMBIENTES	PISO: HORMIGON ACABADO A ESCOBILLON	PISO: HORMIGON ACABADO A FLOTA DE MADERA	PISO: ACABADO ANTIRRESBALANTE PARA EXTERIOR, ESCOGIDO POR EL PROMOTOR	PISO: CERAMICA IMPORTADA ESCOGIDA POR EL PROMOTOR DEL PROY.	ZOCALO: CERAMICA IMPORTADA ESCOGIDA POR EL PROMOTOR DEL PROY.	ZOCALO: ACABADO ANTIRRESBALANTE PARA EXTERIOR, ESCOGIDO POR EL PROMOTOR DEL PROY.	ZOCALO: LOSA IMPERMEABILIZADA	PARED: PAREDES DE BLOQUES + REPELLO USO + PINTURA	PARED: REVEST. DE ACABADOS ESCOGIDOS POR EL PROMOTOR DEL PROY.	PARED: PAREDES REPELLADAS VISTAS	CIELO: LOSA DE HORM. REPELLADA Y PASTEADA + BASE + PINTURA	CIELO: ESTRUCTURA DE TECHO VISTO	CIELO: GYPSUM BOARD PATEADO Y PINTADO	CIELO: LOSA RESANADA VISTA	OBSERVACIONES
NIVEL -400															
VESTIBULO DE ELEVADORES				X		X		X			X				
ESCALERAS				X		X		X			X				
ESTACIONAMIENTOS		X						X						X	
RAMPAS	X							X						X	
PASILLO A APTOS.				X		X		X			X				
SALA				X		X		X			X				
COMEDOR				X		X		X			X				
S. SANITARIOS				X					X				X		
RECAMARAS				X		X		X			X				
COCINA / LAVANDERIA				X					X		X				
BALCON				X		X		X			X				
DEPOSITOS		X						X						X	
TERRAZA #1			X				X				X				
TERRAZA #2			X				X				X				
TERRAZA #3			X				X				X				
S. SANITARIOS PUBLICOS				X					X		X				
PISCINA #1			X												
PISCINA #2			X												
PISCINA #3			X												
NIVEL -300 @ -100															
VESTIBULO DE ELEVADORES				X		X		X			X				
ESCALERAS				X		X		X			X				
ESTACIONAMIENTOS		X						X						X	
RAMPA	X													X	
PASILLO A APTOS.				X		X		X			X				
SALA				X		X		X			X				
COMEDOR				X		X		X			X				
S. SANITARIOS				X					X				X		
RECAMARAS				X		X		X			X				
COCINA / LAVANDERIA				X					X		X				
BALCON				X		X		X			X				
NIVEL 000 (PLANTA BAJA-LOBBY)															
GARITA DE SEGURIDAD				X		X		X			X				
BAÑO DE DE GARITA				X					X		X				
ROTONDA Y ESTACIONAMIENTOS		X													
CTOS. DE BASURA		X								X				X	**BASE + PINTURA EXT.**
CTOS. ELECTRICOS		X								X				X	**BASE + PINTURA EXT.**
CTO. DE GAS		X								X				X	**BASE + PINTURA EXT.**
RAMPA	X							X			X				
VESTIBULO PRINCIPAL (LOBBY)				X		X		X			X				
ESCALERAS DEL EDIFICIO				X		X		X			X				
LOCALES COMERCIALES				X		X		X			X				
SPA				X		X		X			X				
SALON DE FIESTAS				X		X		X			X				
S. SANITARIOS PUBLICOS				X					X		X				
GIMANSIO				X		X		X			X				
DEPOSITOS				X				X			X				
AREA INFANTIL				X		X		X			X				
BAÑO DE AREA INFANTIL				X					X		X				
CANCHA DE SQUACH				X		X		X			X				
TERRAZA EXTERIOR			X				X				X				
SALA/COMEDOR				X		X		X			X				
COCINA / LAVANDERIA				X					X		X				
S. SANITARIO				X					X		X				
RECAMARAS				X		X			X		X				
NIVEL TIPICO DE APTOS. 100 @ 2200															
VESTIBULO DE ELEVADORES				X		X		X			X				
ESCALERAS DEL EDIFICIO				X		X		X			X				
SALA/COMEDOR				X		X		X			X				
COCINA / LAVANDERIA				X					X		X				
RECAMARAS				X		X		X			X				
S. SANITARIOS				X					X				X		
BALCON				X		X		X			X				
NIVEL TIPICO DE APTOS. 2300 @ 2500															
VESTIBULO DE ELEVADORES				X		X		X			X				
ESCALERAS DEL EDIFICIO				X		X		X			X				
SALA/COMEDOR				X		X		X			X				
COCINA				X					X		X				
LAVANDERIA				X					X		X				
RECAMARAS				X		X		X			X				
S. SANITARIOS				X					X				X		
BALCON				X		X		X			X				
NIVEL 2600 (P.H)															
VESTIBULO DE ELEVADORES				x		x		x			x				
ESCALERAS DEL EDIFICIO				x		x		x			x				
SALA/COMEDOR				x		x		x			x				
COCINA				x					x		x				
LAVANDERIA				x					x		x				
RECAMARA				x		x		x			x				
S. SANITARIOS				x					x				x		GYPSUM SEGÚN LO INDICADO EN PLANOS
BALCON				x		x		x			x				
ESCALERAS DEL P.H				x		x		x			x				
TERRAZA				x		x		x			x				
NIVEL 2700 (P.H)															
VESTIBULO DE ELEVADORES				X		X		X			X				
ESCALERAS DEL EDIFICIO				X		X		X			X				
RECAMARA				X		X		X			X				
S. SANITARIOS				X					X				X		GYPSUM SEGÚN LO INDICADO EN PLANOS
BALCONES				X		X		X			X				
ESCALERAS DEL P.H				X		X		X			X				
NIVEL 2800 (P.H)															
VESTIBULO DE ELEVADORES				X		X		X			X				
ESCALERAS DEL EDIFICIO				X		X		X			X				
CTO. DE MAQUINAS					X			X						X	
AREA DE TANQUE DE AGUA					X			X							
ESCALERAS DEL P.H				X		X		X			X				
S. SANITARIO				X					X		X				
ESTUDIO				X		X		X			X				
DEPOSITO				X		X		X			X				
CTO. DE BOMBA DE PISCINA				X		X		X			X				
TERRAZA			X				X				X				
PISCINA			X												
NIVEL 2800 (P.H)															
LOSA DE AZOTEA					X										

NOTAS DE PINTURA

A.- CIELO RASO DE LOSA Y MALLAS REPELLADAS O PASTEADAS

1.- APLICAR 1 MANO DE SELLADOR 5 X 1 REFORZADO (DILUIDO 3 PARTES DE AGUA POR UNA PARTE DEL SELLADOR)

2.- DOS MANOS DE DUREX MASTER (PINTURA ECONOMICA LAVABLE) O UTILIZAR 2 MANOS DE PRO-1000 PLUS (PINTURA ALTAMENTE LAVABLE)

B.- PAREDES DE BLOQUES Y CONCRETO INTERIOR

1.- APLICAR 1 MANO DE PINTURA VINILICA INSTITUCIONAL (COMO BASE BLANCA)

2.- DOS MANOS DE DUREX MASTER (PINTURA ECONOMICA LAVABLE) O UTILIZAR 2 MANOS DE PRO-1000 PLUS (PINTURA ALTAMENTE LAVABLE)

C.- PAREDES DE BLOQUES Y CONRETO REPELLADO AL EXTERIOR

SI EL ACABADO VA A SER LISO

1.- APLICAR 1 MANO DE SELLADOR 5 X 1 REFORZADO, DILUIDO 3 PARTES DE AGUA POR UNA PARTE DEL SELLADOR (PRODUCTO TRANSPARENTE RESISTENTE A LA ALCALINIDAD, TAPAPORO Y PROMOTOR DE ADHERENCIA DE LA PINTURA) SI NECESITA FONDEAR, SE PUEDE ENTINTAR CON LA MISMA PINTURA QUE SE UTILIZARA COMO ACABADO)

* SI EXISTEN GRIETAS PEQUEÑAS: APLICAR CON BROCHA IMPERMEABILIZANTE TOP TOTAL AL COLOR DE LA PINTURA DEL ACABADO

2.- APLICAR 2 MANOS VINIMEX DE COMEX, SI NECESITA UN ACABADO SATINADO ANTIHONGOS DE ALTA LAVABILIDAD, O PRO-1000 PLUS SI NECESITA UN ACABADO MATE ANTIHONGOS

SI EL ACABADO VA A SER TEXTURIZADO

1.- APLICAR 1 MANO DE PRACTICO ADHESIVO PARA TEXTURI DILUIDO 1 PARTE DE AGUA POR 1 PARTE DE ADHESIVO. ESTE MISMO SE PUEDE ENTINTAR CON DUREX MASTER SI NECESITA FONDEAR. DEJAR SECAR 15 MINUTOS PARA APLICAR EL TEXTURIZADO

2.- APLICAR CON LLANA DE ACERO INOXIDABLE TEXTURI MEDIA O GROSA DE COMEX, A UNA MANO E INMEDIATAMENTE DESPUES CON UNA LLANA DE MADERA HACER EL ACABADO DESEADO. PARA UN BUEN ACABADO SE RECOMIENDA APLICAR EL TEXTURI SOBRE MUROS ENTEROS

D.- SUPERFICIES DE HIERRO GRIS (BARANDAS O HERRERIA EN GENERAL)

1.- ELIMINAR EL OXIDO CON LIJA O CARDA

2.- APLICAR 1 MANO DE PRIMARIO ANTICORROSIVO No. 2 CON BROCHA O PISTOLA

3.- APLICAR 2 MANOS DE ESMALTE ANTICORROSIVO VELMAR, CON BROCHA O SI DESEA UN ACABADO LISO, TERSO Y DE ALTO BRILLO, APLICARLO CON PISTOLA

NOTA: EL PRODUCTO DE LOS PUNTOS 2 Y 3, SI SE APLICA CON BROCHA SE RECOMIENDA DILUIRLO CON 10% DE AGUARRAS, PERO SI SE APLICA CON PISTOLA, DILUIRLO CON 15 AL 20% DE THINER

E.- SUPERFICIES METALICAS GALVANIZADAS

1.- LIMPIAR LA SUPERFICIE CON THINER Y UN TRAPO LIMPIO

2.- APLICAR 1 MANO DE PRIMER EPOXICO RP-6, PREVIAMENTE CATALIZADO CON 2 PARTES DE RESINA POR 1 PARTE DE CATALIZADOR (SE PUEDE APLICAR CON BROCHA O RODILLO), ESTE PRODUCTO SE ADHIERE SOBRE SUPERFICIES GALVANIZADAS, CROMADAS, COBRE Y FIBRA DE VIDRIO

3.- APLICAR 2 MANOS DE ESMALTE BRILLANTE VELMAR, CON BROCHA O PISTOLA

F.- SUPERFICIES DE MADERA

ACABADO LACA TRANSPARENTE, SEMI-BRILLANTE Y RESISTENTE

1.- LIJAR LA MADERA, COMENZANDO CON LIJA DE GRANO GRANDE E IR CAMBIANDOLA GRADUALMENTE HASTA LLEGAR A UNA LIJA DE AGUA DE GRANO FINO (No. 350 a 400), PARA DEJAR ASI LA MADERA LISA Y TERSA

2.- APLICAR 2 MANOS DE SELLADOR ALTOS SOLIDOS DE COMEX CON PISTOLA (LIJANDO ENTRE MANO Y MANO) DILUYENDO EL SELLADOR CON 2 PARTES DE THINNER

3.- APLICAR 2 MANOS DE LACA ALTOS SOLIDOS DE COMEX CON PISTOLA (LIJANDO ENTRE MANO Y MANO) DILUYENDOLO CON 2 PARTES DE THINER

ACABADO BARNIZ TRANSPARENTE, BRILLANTE Y DE CUALQUIER COLOR

1.- LIJAR LA MADERA, COMENZANDO CON LIJA DE GRANO GRANDE E IR CAMBIANDOLA GRADUALMENTE HASTA LLEGAR A UNA LIJA DE AGUA DE GRANO FINO (No. 350 a 400), PARA DEJAR ASI LA MADERA LISA Y TERSA

2.- APLICAR 1 MANO DE SELLADOR ALTOS SOLIDOS DE COMEX CON PISTOLA (LIJANDO ENTRE MANO Y MANO) DILUYENDO EL SELLADOR CON 2 PARTES DE THINNER

3.- APLICAR 2 MANOS DE BARNIZ TINTE COLOR CENTER DE COMEX. SE PUEDE APLICAR CON BROCHA O PISTOLA

NOTAS PARA REPELLO EXTERIOR

A. PREPARACION DE LA SUPERFICIE PARA REPELLO EXTERIOR.

1. RESANAR PARED HASTA LOGRAR UNA SUPERFICIE LISA, PARA OBTENER UNIFORMIDAD EN EL ESPESOR DEL MORTERO DE REPELLO AL MOMENTO DE LA APLICACION.

2. ANTES DE APLICAR EL MORTERO DE REPELLO , LA SUPERFICIE SE DEBERA HUMEDECER CON AGUA (ESTO EVITARA RAJADURA POR TEMPERATURA Y DARA TIEMPO PARA LA MANIPULACION DE LA MEZCLA.

B. APLICACION DEL REPELLO EXTERIOR CON ACABADO FINAL TERMINADO A ESPONJA

1. LA MEZCLA PARA EL MORTERO DE REPELLO TENDRA UNA PORCION 1 : 3 (1 DE CEMENTO POR 3 DE ARENA). AGREGAR AGUA HASTA OBTENER UNA CONSISTENCIA PASTOSA, TRABAJAR CON UN ESPESOR DEL MORTERO MINIMO DE 1/2".

2. EL ESPESOR DEL MORTERO DE REPELLO A UTILIZAR , SE DEFINIRA COLOCANDO REGLAS FIJADAS (ALINEADAS Y SUJETADAS CON LA SUPERFICIE DE LA PARED).

3. SE APLICARA EL MORTERO PARA REPELLO A LA SUPERFICIE PREPARADA , TALLANDOLA HASTA OBTENER EL ESPESOR MARCADO.

4. UTILIZAR FLOTA DE MADERA SOBRE EL MORTERO DE REPELLO HASTA OBTENER UNA SUPERFICIE PAREJA.

5. APLICAR UNA ESPONJA SEMI-HUMEDA PARA EL ACABADO FINAL SOBRE LA SUPERFICIE ACABADA A FLOTA, PARA ELIMINAR LAS ONDULACIONES, RAYADURAS U OTROS DEFECTOS.

SE RECOMIENDA UTILIZAR ESPONJA DE 2" ESP. MINIMO.

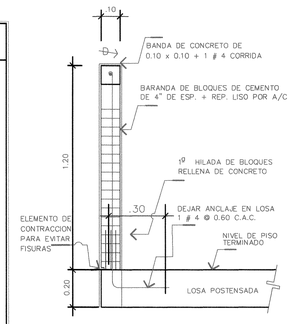

DETALLE DE BARANDA DE CONCRETO

ESCALA 1:15

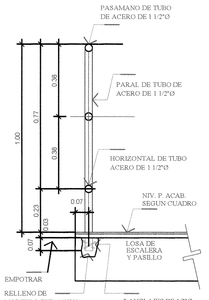

DET. DE BARANDA

ESCALERAS, ESTACIONAMIENTOS GENERALES

ESC. 1/15

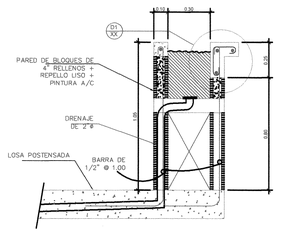
PARED DE BLOQUES DE 4" RELLENOS + REPELLO USO + PINTURA A/C
DRENAJE DE 2"Ø
LOSA POSTENSADA
BARRA DE 1/2" @ 1.00
0.30
0.30
0.30

APART. 1 REC. TIPO " A " NIVEL 100 @ -2200

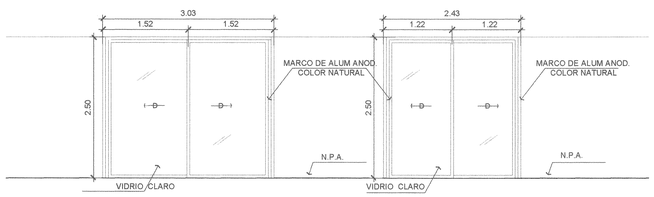

PUERTA P-A-1 — ESC. 1/20

PUERTA P-A-2 — ESC. 1/20

APART. 2 REC. TIPO " B " NIVEL 100 @ 2200

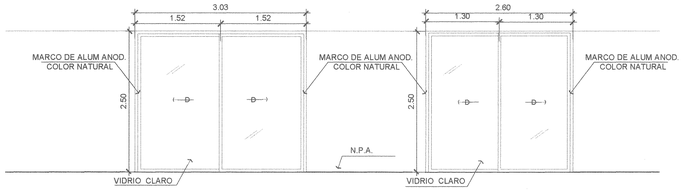

PUERTA P-B-1 — ESC. 1/20

PUERTA P-B-2 — ESC. 1/20

APART. 3 REC. TIPO " C " NIVEL 2300 @ 2500

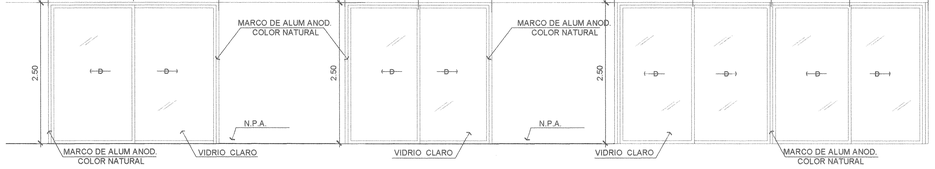

PUERTA P-C-1 — ESC. 1/20

PUERTA P-C-2 — ESC. 1/20

PUERTA P-C-3 — ESC. 1/20

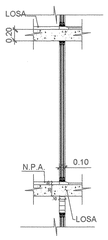

CORTE DE PUERTAS APTO — ESC. 1/50

APART. 4 REC. TIPO " D " NIVEL 2600 @ 2800

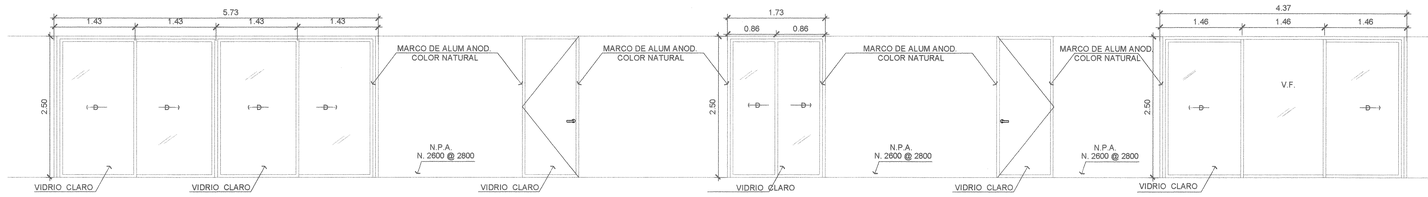

PUERTA P-D-1 — ESC. 1/50

PUERTA P-D-2 — ESC. 1/50

PUERTA P-D-3 — ESC. 1/50

PUERTA P-D-4 — ESC. 1/50

PUERTA P-D-5 — ESC. 1/50

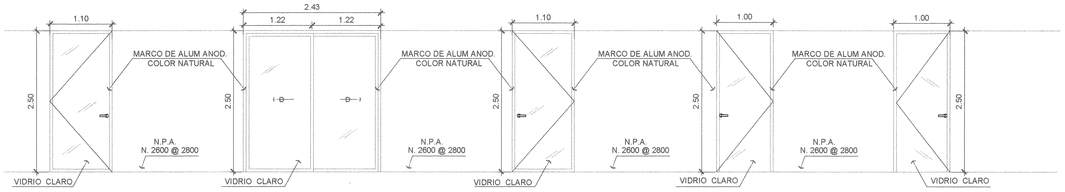

PUERTA P-D-6 — ESC. 1/50

PUERTA P-D-7 — ESC. 1/50

PUERTA P-D-8 — ESC. 1/50

PUERTA P-D-9 — ESC. 1/50

PUERTA P-D-10 — ESC. 1/50

CUADRO DE PUERTAS TORRE " A "

UBICACION	NIVEL	Nº	VANO ANCHO	VANO ALTO	ABAT. IZQ.	ABAT. DER.	ABAT. DOBLE	CORREDIZA	CANT. X NIVEL	NUM. NIVELES	CANT. TOTAL	SUP. UNIT. VIDRIO (M2)	SUP. TOTAL VIDRIO (M2)	DESCRIPCIÓN	MARCO FERRETERIA	UBICACION	OBSERVACION
	NIVEL 000	P - 2	1.00	2.15		-			2	1	2			MADERA	MARCOS NTEGRALES DE MADERA	S.S LOBBY Y DEP.COMERCIO 1	
		P - 3	0.80	2.15	-				2	1	2			MADERA	MARCOS NTEGRALES DE MADERA	DEPOSITOS 1 Y 2	
		P - 5	0.70	2.15	-				1	1	1			MADERA	MARCOS NTEGRALES DE MADERA	S.S. AREA DE NIÑOS	
		P - 7	1.00	2.15		-			2	1	2			METAL	MARCOS NTEGRALES DE METAL	ESTACION DE TRANSFORMADORES Y MEDIDORES.	
		P - 15	1.00	2.15	-				1	1	1			METAL	MARCOS NTEGRALES DE METAL	ESTACIÓN DE MEDIDORES	
		P - 17	------	----	----	----	----	----	1	1	1	------	-----	ALUMINIO + VIDRIO CLARO	MARCO DE ALUM ANOD. COLOR NATURAL	VESTIBULO- ENTRADA AL EDIFICIO	VER DETALLE
		P - 18	1.00	3.88				-	2	1	2	3.88	7.76	ALUMINIO + VIDRIO CLARO	MARCO DE ALUM ANOD. COLOR NATURAL	SALA DE EVENTOS	VER DETALLE
		P - 19	1.10	3.88				-	1	1	1	4.27	4.27	ALUMINIO + VIDRIO CLARO	MARCO DE ALUM ANOD. COLOR NATURAL	SALA DE EVENTOS	VER DETALLE
		P - 20	5.55	3.88				-	1	1	1	21.53	21.53	ALUMINIO + VIDRIO CLARO	MARCO DE ALUM ANOD. COLOR NATURAL	SALA DE EVENTOS	VER DETALLE
		P - 21	3.25	3.88				-	1	1	1	12.61	12.61	ALUMINIO + VIDRIO CLARO	MARCO DE ALUM ANOD. COLOR NATURAL	AREA INFANTIL	VER DETALLE
		P - 22	2.63	3.88				-	1	1	1	10.20	10.20	ALUMINIO + VIDRIO CLARO	MARCO DE ALUM ANOD. COLOR NATURAL	ÁREA INFANTIL	VER DETALLE
		P - 23	2.93	3.88		-			1	1	1	11.36	11.36	ALUMINIO + VIDRIO CLARO	MARCO DE ALUM ANOD. COLOR NATURAL	ÁREA INFANTIL	
		P - 24	1.35	3.88				-	1	1	1	5.24	5.24	ALUMINIO + VIDRIO CLARO	MARCO DE ALUM ANOD. COLOR NATURAL	SALA DE AUDIOVISUALES	VER DETALLE
		P - 25	2.10	3.88				-	1	1	1	8.15	8.15	ALUMINIO + VIDRIO CLARO	MARCO DE ALUM ANOD. COLOR NATURAL	PASILLO	VER DETALLE
		P - 32	1.00	2.15	-				1	1	1			PERSIANERA DE ALUMINIO	MARCO DE ACERO GALV.	TINAQUERA	
		P - 33	3.29	2.15			-		1	1	1			METAL	MARCOS NTEGRALES DE METAL	MAQUINA	
	VESTIBULO	P - 8	1.14	2.15			-		3	29	87			PERSIANERA DE ALUMINIO	MARCO DE ACERO GALV.	CUARTO TÉCNICOS	
		P - 10	0.59	2.15		-			1	29	29			PERSIANERA DE ALUMINIO	MARCO DE ACERO GALV.	CUARTO TÉCNICOS	
		P - 12	1.00	2.15		-			1	33	33			PUERTA PRESURIZADA	AISLAMIENTO TERMICO RESISTENTE AL FUEGO	ESCALERA DE EMERGENCIAS	
		P - 14	0.80	2.15		-			1	29	29			PERSIANERA DE ALUMINIO	MARCO DE ACERO GALV.	CUARTO TÉCNICOS	
	TIPO "A - B" NIVEL 100 @ 2200	P - A - 1	3.03	2.50				-	2	22	44	7.58	333.30	ALUMINIO + VIDRIO CLARO	MARCO DE ALUM ANOD. COLOR NATURAL	SALA/ COMEDOR	
		P - A - 2	2.43	2.50				-	2	22	44	6.08	267.30	ALUMINIO + VIDRIO CLARO	MARCO DE ALUM ANOD. COLOR NATURAL	RECAMARA #1	
		P - B - 1	3.03	2.50				-	2	22	44	7.58	333.30	ALUMINIO + VIDRIO CLARO	MARCO DE ALUM ANOD. COLOR NATURAL	SALA/ COMEDOR	
		P - B - 3	2.60	2.50				-	2	22	44	6.50	286.00	ALUMINIO + VIDRIO CLARO	MARCO DE ALUM ANOD. COLOR NATURAL	RECAMARA #1	
		P - 1	1.00	2.15	-				2	22	44			MADERA	MARCOS NTEGRALES DE MADERA	ENTRADA PRINCIPAL	
		P - 2	1.00	2.15		-			2	22	44			MADERA	MARCOS NTEGRALES DE MADERA	ENTRADA PRINCIPAL	
		P - 3	0.80	2.15	-				6	22	132			MADERA	MARCOS NTEGRALES DE MADERA	REC. Y S.S. DE TODOS LOS MODELOS APTOS.	
		P - 4	0.80	2.15		-			6	22	132			MADERA	MARCOS NTEGRALES DE MADERA	REC. Y S.S. DE TODOS LOS MODELOS APTOS.	
	APART. 3 REC. TIPO "C" NIVEL 2300 @ 2500	P - C - 1	3.02	2.50				-	2	3	6	7.55	45.30	ALUMINIO + VIDRIO CLARO	MARCO DE ALUM ANOD. COLOR NATURAL	RECAMARA #1	
		P - C - 2	2.60	2.50				-	2	3	6	6.50	39.00	ALUMINIO + VIDRIO CLARO	MARCO DE ALUM ANOD. COLOR NATURAL	RECAMARA #2	
		P - C - 3	5.55	2.50				-	2	3	6	13.88	83.25	ALUMINIO + VIDRIO CLARO	MARCO DE ALUM ANOD. COLOR NATURAL	SALA/ COMEDOR	
		P - 1	1.00	2.15	-				1	3	3			MADERA	MARCOS NTEGRALES DE MADERA	ENTRADA PRINCIPAL	
		P - 2	1.00	2.15		-			1	3	3			MADERA	MARCOS NTEGRALES DE MADERA	ENTRADA PRINCIPAL	
		P - 3	0.80	2.15	-				8	3	24			MADERA	MARCOS NTEGRALES DE MADERA	PASILLOS INTERNOS, REC. Y S.S #1 Y #2	
		P - 4	0.80	2.15		-			8	3	24			MADERA	MARCOS NTEGRALES DE MADERA	PASILLOS INTERNOS, REC. Y S.S #1 Y #2	
		P - 5	0.70	2.15	-				1	3	3			MADERA	MARCOS NTEGRALES DE MADERA	SERVICIO SANITARIO C-3	
		P - 6	0.70	2.15		-			1	3	3			MADERA	MARCOS NTEGRALES DE MADERA	SERVICIO SANITARIO C-3	
	APART. 4 REC. TIPO "D" NIVEL 2600 @ 2800	P - D - 1	5.73	2.50				-	4	1	4	14.33	57.30	ALUMINIO + VIDRIO CLARO	MARCO DE ALUM ANOD. COLOR NATURAL	SALA/ COMEDOR	VER DETALLE
		P - D - 2	1.00	2.50	-				1	1	1	2.50	2.50	ALUMINIO + VIDRIO CLARO	MARCO DE ALUM ANOD. COLOR NATURAL	BALCON DE SALA/ COMEDOR	
		P - D - 3	1.73	2.50				-	2	1	2	4.33	8.65	ALUMINIO + VIDRIO CLARO	MARCO DE ALUM ANOD. COLOR NATURAL	DESAYUNADOR	VER DETALLE
		P - D - 4	1.00	2.50		-			1	1	1	2.50	2.50	ALUMINIO + VIDRIO CLARO	MARCO DE ALUM ANOD. COLOR NATURAL	BALCON DE SALA/ COMEDOR	
		P - D - 5	4.37	2.50				-	2	1	2	10.93	21.86	ALUMINIO + VIDRIO CLARO	MARCO DE ALUM ANOD. COLOR NATURAL	RECAMARA #1	VER DETALLE
		P - D - 6	1.10	2.50	-				1	1	1	2.64	2.64	ALUMINIO + VIDRIO CLARO	MARCO DE ALUM ANOD. COLOR NATURAL	BALCON NIVEL 2700	
		P - D - 7	2.43	2.50				-	4	1	4	6.08	24.20	ALUMINIO + VIDRIO CLARO	MARCO DE ALUM ANOD. COLOR NATURAL	RECAMARAS # 2 Y#3	
		P - D - 8	1.10	2.50		-			1	1	1	2.50	2.50	ALUMINIO + VIDRIO CLARO	MARCO DE ALUM ANOD. COLOR NATURAL	BALCON DE SALA/ COMEDOR	
		P - D - 9	1.00	2.50		-			1	1	1	2.50	2.50	ALUMINIO + VIDRIO CLARO	MARCO DE ALUM ANOD. COLOR NATURAL	TERRAZA NIVEL 2900	
		P - D - 10	1.00	2.50	-				1	1	1	2.50	2.50	ALUMINIO + VIDRIO CLARO	MARCO DE ALUM ANOD. COLOR NATURAL	TERRAZA NIVEL 2900	
		P - 1	1.00	2.15	-				3	1	3			MADERA	MARCOS NTEGRALES DE MADERA	ENTRADA, DEPTO NIVEL 2800, CUARTO DE B.P	
		P - 2	1.00	2.15		-			3	1	3			MADERA	MARCOS NTEGRALES DE MADERA	ENTRADA, DEPTO NIVEL 2800, CUARTO DE B.P	
		P - 3	0.80	2.15	-				13	1	13			MADERA	MARCOS NTEGRALES DE MADERA	REC. Y S.S. DE TODOS LOS MODELOS APTO.	
		P - 4	0.80	2.15		-			13	1	13			MADERA	MARCOS NTEGRALES DE MADERA	REC. Y S.S. DE TODOS LOS MODELOS APTO.	
		P - 7	1.00	2.15		-			1	1	1			METAL	MARCOS NTEGRALES DE METAL	CUARTO DE MAQUINA	
		P - 15	1.00	2.15	-				1	1	1			METAL	MARCOS NTEGRALES DE METAL	CUARTO DE MAQUINA	
		P - 11	1.00	2.15	-				1	1	1			PUERTA PRESURIZADA	AISLAMIENTO TERMICO RESISTENTE AL FUEGO	ESCALERA DE AZOTEA	
		P - 12	1.00	2.15		-			1	1	1			PUERTA PRESURIZADA	AISLAMIENTO TERMICO RESISTENTE AL FUEGO	CUARTO DE BOMBA DE AGUA	

INGENIERIA MUNICIPAL
DISTRITO DE SAN CARLOS
APROBADO
INGENIERO MUNICIPAL
FECHA: 22/10/10

Cuerpo de Bomberos
OFICINA DE SEGURIDAD
La Chorrera
Resolución No. 2010 Plano No. 10-1
Se aprueba el registro de este plano por llenar los condiciones requerida

Jefe de la Oficina de Seguridad

FELIPE GONZALEZ LINCK
ARQUITECTO
LICENCIA No. 87-1-185
LEY 15 DEL 3 DE ENERO DE 1959
JUNTA TECNICA DE INGENIERIA Y ARQUITECTURA

FELIFE GONZÁLEZ LINCK
ARQUITECTO
Tel. – 66771610 – Fax 392-2457 | 64035839

DISEÑO ARQUITECTÓNICO	Arq. Vicente Cortes Arq. Igor Cortes
DESARROLLO	Arq. Igor Cortes Arq. Ilem Segismond Arq. Nancy Urriola
PROYECTO ESTRUCTURAL	Ing. Ricauter Bowen
PROYECTO ELÉCTRICO	Ing. Edgar Naranjo
PROYECTO DE PLOMERÍA	Ing. Gilberto Ayala

PROYECTO

Residencial El Palmar

UBICACIÓN

COMUNIDAD DE "EL PALMAR"
DTTO. DE SAN CARLOS - CORREGIMIENTO DE SAN CARLOS
PANAMÁ

SOCIEDAD PROMOTORA

Inversiones Decuria, S.A.
Representante legal: IGOR CORTES
Número de cédula o pasaporte: BC054493

INGENIERÍA MUNICIPAL

PLANO

- CUADRO DE PUERTAS TORRE A

ARCHIVO .DWG	PUERTAS
FECHA	30/08/2010
FECHA MODIFICACIÓN	DD/MM/AAAA

ARQUITECTURA | HOJA: 53 | DE: 65

NIVEL 000 TORRE " A "

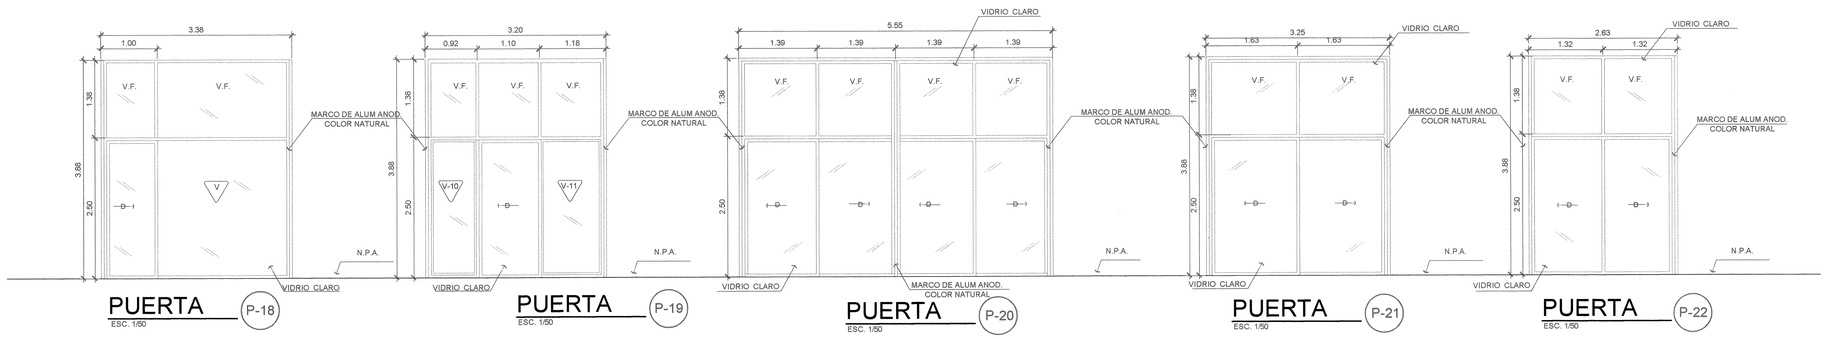

PUERTA P-18 ESC. 1/50

PUERTA P-19 ESC. 1/50

PUERTA P-20 ESC. 1/50

PUERTA P-21 ESC. 1/50

PUERTA P-22 ESC. 1/50

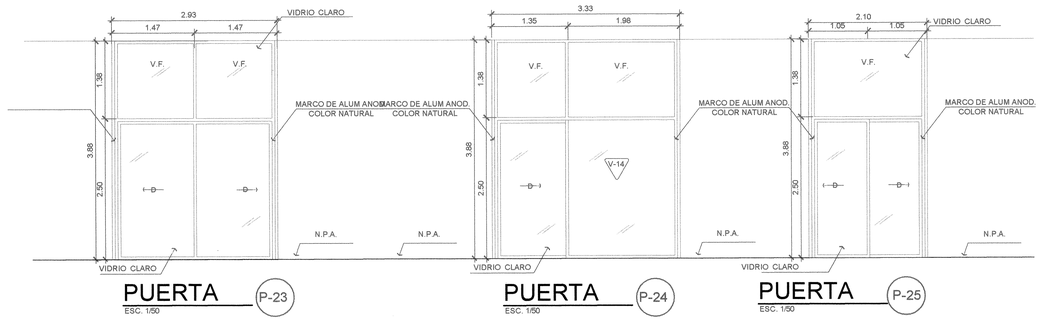

PUERTA P-23 ESC. 1/50

PUERTA P-24 ESC. 1/50

PUERTA P-25 ESC. 1/50

CORTE DE PUERTAS NIVEL 000
ESC. 1/50

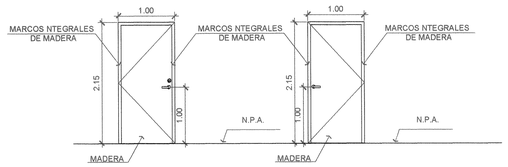

PUERTA P-1 ESC. 1/50

PUERTA P-2 ESC. 1/50

ESPECIFICACION:
DE LAMINAS DECORATIVAS CON RELLENO DE POLIESTIRENO, ACABADO EN COLOR A ESCOGER
EL DISEÑO Y EL COLOR SERA ESCOGIDO POR EL ARQ. Y/O PROMOTOR DEL PROYECTO.

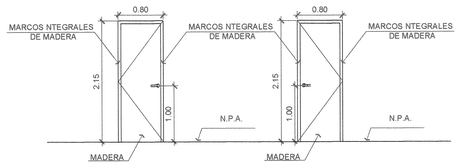

PUERTA P-3 ESC. 1/50

PUERTA P-4 ESC. 1/50

ESPECIFICACION:
CON RELLENO DE POLIESTIRENO ACUSTICO LAMINADAS CON CHAPAS DDE MDF PREPINTADAS EN COLOR A ESCOGER POR EL ARQ. Y/O PROMOTOR
EL DISEÑO Y EL COLOR SERA ESCOGIDO POR EL ARQ. Y/O PROMOTOR DEL PROYECTO.

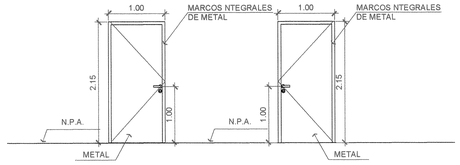

PUERTA P-6 ESC. 1/50

PUERTA P-7 ESC. 1/50

PUERTA P-15 ESC. 1/50

ESPECIFICACION:
PUERTA CONTRA INCENDIO DE METAL DE CON ESTRUCTURA METALICA CAL. 16
MARCO DE 1-1/2 X 5 CAL. 15 CON 3 BISAGRAS DE 4" RESISTENTE AL FUEGO

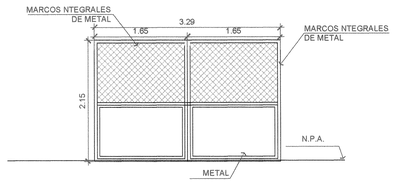

PUERTA P-33 ESC. 1/50

ESPECIFICACION:
PUERTA CONTRA INCENDIO DE METAL DE CON ESTRUCTURA METALICA CAL. 16
MARCO DE 1-1/2 X 5 CAL. 15 CON 3 BISAGRAS DE 4" RESISTENTE AL FUEGO

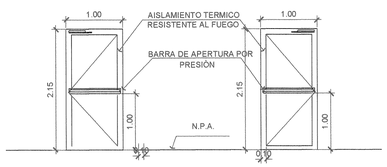

PUERTA P-11 ESC. 1/50

PUERTA P-12 ESC. 1/50

ESPECIFICACION:
PUERTA CONTRA INCENDIO DE METAL DE CON ESTRUCTURA METALICA CAL. 16
MARCO DE 1-1/2 X 5 CAL. 15 CON 3 BISAGRAS DE 4" RESISTENTE AL FUEGO

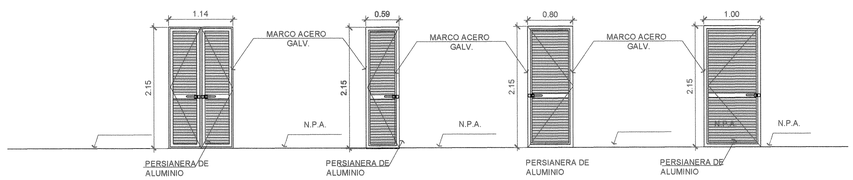

PUERTA P-8 ESC. 1/50

PUERTA P-10 ESC. 1/50

PUERTA P-14 ESC. 1/50

PUERTA P-32 ESC. 1/50

ESPECIFICACION:
PUERTA DE PERSIANA CON ESTRUCTURA METALICA INTERNA.
MARCO DE ACERO GALV. CAL #20 DE 1X4 CON 3 BISAGRAS EN COLOR A ESCOGER POR EL ARQ.

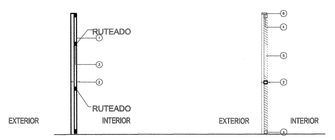

CORTE GENERAL P. DE MADERA

CORTE GENERAL P. DE PERSIANAS

LEYENDA:
1. LAMINAS DECORATIVAS CON RELLENO DE POLIESTIRENO ACABADO EN ESCOGER POR EL PROMOTOR O ARQ.
2. MANIJA
3. BASTIDOR DE MADERA
4. MARCO PRESURIZADO CON EMPAQUETADURA RESISTENTE AL FUEGO
5.PERSIANERA DE ALUMINIO
6. MARCO DE ACERO GALVANIZADO.

INGENIERIA MUNICIPAL
DISTRITO DE SAN CARLOS
APROBADO
FECHA 22/8/11

Cuerpo de Bomberos
OFICINA DE SEGURIDAD
La Chorrera
Resolución No. 2-11 de 22/11
Se aprueba el registro de este plano por llenar las condiciones requeridas.
Jefe de la Oficina de Seguridad

FELIPE GONZALEZ LINCK
ARQUITECTO
LICENCIA No. 92-1-108
LEY 15 DEL 26 DE ENERO DE 1959
JUNTA TECNICA DE INGENIERIA Y ARQUITECTURA

FELIFE GONZÁLEZ LINCK
ARQUITECTO
Tel. - 6677610 -- Fax 392-2457 | 64035839

DISEÑO ARQUITECTÓNICO	Arq. Vicente Cortes Arq. Igor Cortes
DESARROLLO	Arq. Igor Cortes Arq. Ilem Segismond Arq. Nancy Urriola
PROYECTO ESTRUCTURAL	Ing. Ricauter Bowen
PROYECTO ELÉCTRICO	Ing. Edgar Naranjo
PROYECTO DE PLOMERÍA	Ing. Gilberto Ayala

PROYECTO
Residencial El Palmar

UBICACIÓN
COMUNIDAD DE 'EL PALMAR'
DTTO. DE SAN CARLOS - CORREGIMIENTO DE SAN CARLOS
PANAMÁ

SOCIEDAD PROMOTORA
Inversiones Decuria, S.A.
Representante legal: IGOR CORTES
Número de cédula o pasaporte: 8C054493

INGENIERÍA MUNICIPAL

PLANO
- DETALLES DE PUERTAS TORRE A

ARCHIVO .DWG	PUERTAS
FECHA	30/08/2010
FECHA MODIFICACIÓN	DD/MM/AAAA

ARQUITECTURA | HOJA: 54 | DE: 65

APART. 1 REC. TIPO " A " NIVEL 100 @ -2200

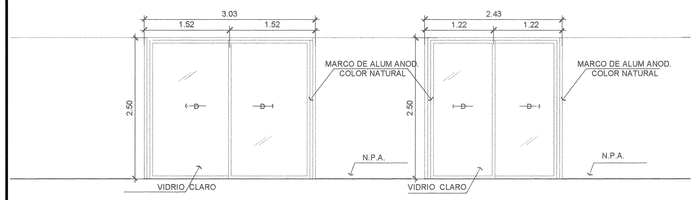

PUERTA P-A-1 ESC. 1/20

PUERTA P-A-2 ESC. 1/20

APART. 2 REC. TIPO " B " NIVEL 100 @ 2200

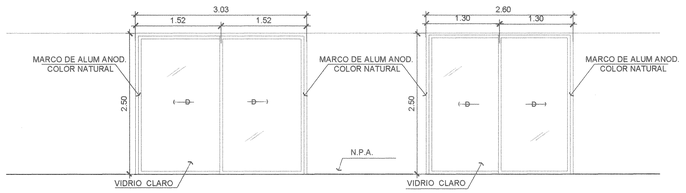

PUERTA P-B-1 ESC. 1/20

PUERTA P-B-2 ESC. 1/20

APART. 3 REC. TIPO " C " NIVEL 2300 @ 2500

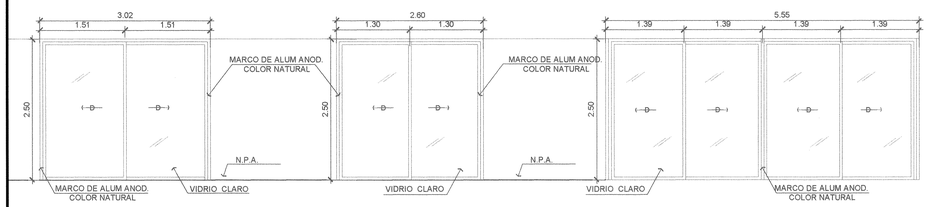

PUERTA P-C-1 ESC. 1/20

PUERTA P-C-2 ESC. 1/20

PUERTA P-C-3 ESC. 1/20

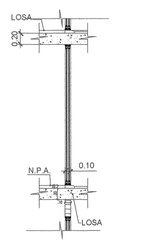

CORTE DE PUERTAS APTO
ESC. 1/50

APART. 4 REC. TIPO " D " NIVEL 2600 @ 2800

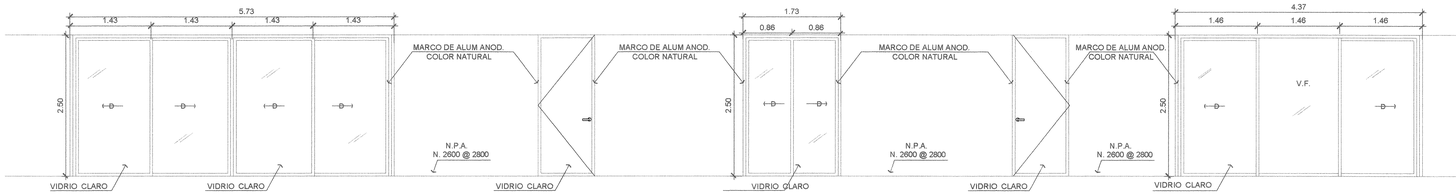

PUERTA P-D-1 ESC. 1/50

PUERTA P-D-2 ESC. 1/50

PUERTA P-D-3 ESC. 1/50

PUERTA P-D-4 ESC. 1/50

PUERTA P-D-5 ESC. 1/50

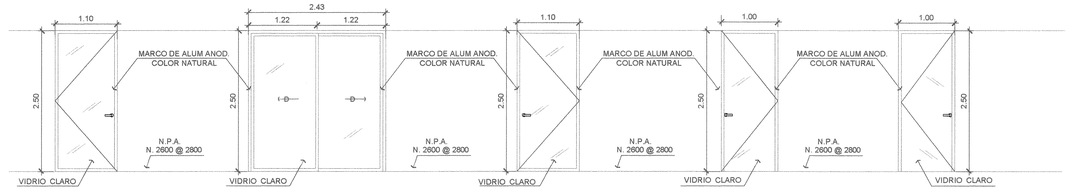

PUERTA P-D-6 ESC. 1/50

PUERTA P-D-7 ESC. 1/50

PUERTA P-D-8 ESC. 1/50

PUERTA P-D-9 ESC. 1/50

PUERTA P-D-10 ESC. 1/50

CUADRO DE PUERTAS TORRE "B"

UBICACION	NIVEL	N°	VANO ANCHO	VANO ALTO	ABAT. IZQ.	ABAT. DER.	ABAT. DOBLE	CORREDIZA	CANT. X NIVEL	NUM. NIVELES	CANT. TOTAL	SUP. UNIT. VIDRIO (M2)	SUP. TOTAL VIDRIO (M2)	DESCRIPCIÓN	MARCO FERRETERIA	UBICACION	OBSERVACION
	NIVEL 000	P - 1	1.00	2.15	-				5	1	5			MADERA	MARCOS NTEGRALES DE MADERA	S.S LOBBY, DEPOSITO 3 Y 4, SPA, APTO DEL CONSERJE	
		P - 2	1.00	2.15		-			1	1	1			MADERA	MARCOS NTEGRALES DE MADERA	SPA	
		P - 3	0.80	2.15	-				2	1	2			MADERA	MARCOS NTEGRALES DE MADERA	REC. #2 DE APTO DE CONSERJE, S.S. CONSERJE	
		P - 4	0.80	2.15		-			2	1	2			MADERA	MARCOS NTEGRALES DE MADERA	REC. #1 DEL CONSERJE. Y S.S. COMERCIO #2	
		P - 5	0.70	2.15	-				2	1	2			MADERA	MARCOS NTEGRALES DE MADERA	VESTIDORES DEL SPA	
		P - 6	0.70	2.15		-			2	1	2			MADERA	MARCOS NTEGRALES DE MADERA	VESTIDOR DEL SPA	
		P - 16	1.00		-				1	1	1	4.08	4.08	ALUMINIO + VIDRIO CLARO	MARCO DE ALUM ANOD. COLOR NATURAL	COMERCIO # 2	VER DETALLE
		P - 18	1.00	3.88				-	3	1	3	3.88	11.64	ALUMINIO + VIDRIO CLARO	MARCO DE ALUM ANOD. COLOR NATURAL	GIMNASIO Y SPA	VER DETALLE
		P - 25	2.10	3.88					2	1	2	8.15	16.30	ALUMINIO + VIDRIO CLARO	MARCO DE ALUM ANOD. COLOR NATURAL	PASILLO	VER DETALLE
		P - 26	0.60	2.15		-			2	1	2			PLYWOOD REVEST. DE PLASTICO LAMINADO	MARCOS NTEGRALES DE MADERA	DUCHAS DEL SPA	VER DETALLE
		P - 27	0.90	2.15	-				1	1	1			MADERA CON MIRILLA	MARCOS NTEGRALES DE MADERA	SAUNA	
		P - 28	0.90	2.15		-			1	1	1			MADERA CON MIRILLA	MARCOS NTEGRALES DE MADERA	SAUNA	
		P - 29	0.60	2.15	-				2	1	2			PLYWOOD REVEST. DE PLASTICO LAMINADO	MARCOS NTEGRALES DE MADERA	DUCHAS DEL SPA	
		P - 30	5.90	3.88				-	1	1	1	22.89	22.89	ALUMINIO + VIDRIO CLARO	MARCO DE ALUM ANOD. COLOR NATURAL	GIMNASIO	VER DETALLE
VESTIBULO		P - 8	1.14	2.15			-		3	29	87			PERSIANERA DE ALUMINIO	MARCO DE ACERO GALV.	CUARTO TÉCNICOS	
		P - 9	0.59	2.15	-				1	29	29			PERSIANERA DE ALUMINIO	MARCO DE ACERO GALV.	CUARTO TÉCNICOS	
		P - 11	1.00	2.15	-				1	34	34			PUERTA PRESURIZADA	AISLAMIENTO TERMICO RESISTENTE AL FUEGO	ESCALERA DE EMERGENCIAS	
		P - 13	0.80	2.15	-				1	29	29			PERSIANERA DE ALUMINIO	MARCO DE ACERO GALV.	CUARTO TÉCNICOS	
TIPO "A - B"	NIVEL 100 @ 2200	P - A - 1	3.03	2.50				-	2	22	44	7.58	333.30	ALUMINIO + VIDRIO CLARO	MARCO DE ALUM ANOD. COLOR NATURAL	SALA/ COMEDOR	
		P - A - 2	2.43	2.50				-	2	22	44	6.08	267.30	ALUMINIO + VIDRIO CLARO	MARCO DE ALUM ANOD. COLOR NATURAL	RECAMARA #1	
		P - B - 1	3.03	2.50				-	2	22	44	7.58	333.30	ALUMINIO + VIDRIO CLARO	MARCO DE ALUM ANOD. COLOR NATURAL	SALA/ COMEDOR	
		P - B - 3	2.60	2.50				-	2	22	44	6.50	286.00	ALUMINIO + VIDRIO CLARO	MARCO DE ALUM ANOD. COLOR NATURAL	RECAMARA #1	
		P - 1	1.00	2.15	-				2	22	44			MADERA	MARCOS NTEGRALES DE MADERA	ENTRADA PRINCIPAL	
		P - 2	1.00	2.15		-			2	22	44			MADERA	MARCOS NTEGRALES DE MADERA	ENTRADA PRINCIPAL	
		P - 3	0.80	2.15	-				6	22	132			MADERA	MARCOS NTEGRALES DE MADERA	REC. Y S.S. DE TODOS LOS MODELOS APTOS.	
		P - 4	0.80	2.15		-			6	22	132			MADERA	MARCOS NTEGRALES DE MADERA	REC. Y S.S. DE TODOS LOS MODELOS APTOS.	
APART. 3 REC. TIPO "C"	NIVEL 2300 @ 2500	P - C - 1	3.02	2.50				-	2	3	6	7.55	45.30	ALUMINIO + VIDRIO CLARO	MARCO DE ALUM ANOD. COLOR NATURAL	RECAMARA #1	
		P - C - 2	2.60	2.50				-	2	3	6	6.50	39.00	ALUMINIO + VIDRIO CLARO	MARCO DE ALUM ANOD. COLOR NATURAL	RECAMARA #2	
		P - C - 3	5.55	2.50				-	2	3	6	13.88	83.25	ALUMINIO + VIDRIO CLARO	MARCO DE ALUM ANOD. COLOR NATURAL	SALA/ COMEDOR	
		P - 1	1.00	2.15	-				1	3	3			MADERA	MARCOS NTEGRALES DE MADERA	ENTRADA PRINCIPAL	
		P - 2	1.00	2.15		-			1	3	3			MADERA	MARCOS NTEGRALES DE MADERA	ENTRADA PRINCIPAL	
		P - 3	0.80	2.15	-				8	3	24			MADERA	MARCOS NTEGRALES DE MADERA	PASILLOS INTERNOS, REC. Y S.S #1 Y #2	
		P - 4	0.80	2.15		-			8	3	24			MADERA	MARCOS NTEGRALES DE MADERA	PASILLOS INTERNOS, REC. Y S.S #1 Y #2	
		P - 5	0.70	2.15	-				1	3	3			MADERA	MARCOS NTEGRALES DE MADERA	SERVICIO SANITARIO C-3	
		P - 6	0.70	2.15		-			1	3	3			MADERA	MARCOS NTEGRALES DE MADERA	SERVICIO SANITARIO C-3	
APART. 4 REC. TIPO "D"	NIVEL 2600 @ 2800	P - D - 1	5.73	2.50				-	4	1	4	14.33	57.30	ALUMINIO + VIDRIO CLARO	MARCO DE ALUM ANOD. COLOR NATURAL	SALA/ COMEDOR	~~VER DETALLE~~
		P - D - 2	1.00	2.50	-				1	1	1	2.50	2.50	ALUMINIO + VIDRIO CLARO	MARCO DE ALUM ANOD. COLOR NATURAL	BALCON DE SALA/ COMEDOR	
		P - D - 3	1.73	2.50				-	2	1	2	4.33	8.65	ALUMINIO + VIDRIO CLARO	MARCO DE ALUM ANOD. COLOR NATURAL	DESAYUNADOR	~~VER DETALLE~~
		P - D - 4	1.00	2.50		-			1	1	1	2.50	2.50	ALUMINIO + VIDRIO CLARO	MARCO DE ALUM ANOD. COLOR NATURAL	BALCON DE SALA/ COMEDOR	
		P - D - 5	4.37	2.50				-	2	1	2	10.93	21.86	ALUMINIO + VIDRIO CLARO	MARCO DE ALUM ANOD. COLOR NATURAL	RECAMARA #1	~~VER DETALLE~~
		P - D - 6	1.10	2.50	-				1	1	1	2.64	2.64	ALUMINIO + VIDRIO CLARO	MARCO DE ALUM ANOD. COLOR NATURAL	BALCON NIVEL 2700	
		P - D - 7	2.43	2.50				-	4	1	4	6.08	24.20	ALUMINIO + VIDRIO CLARO	MARCO DE ALUM ANOD. COLOR NATURAL	RECAMARAS # 2 Y#3	
		P - D - 8	1.10	2.50		-			1	1	1	2.50	2.50	ALUMINIO + VIDRIO CLARO	MARCO DE ALUM ANOD. COLOR NATURAL	BALCON DE SALA/ COMEDOR	
		P - D - 9	1.00	2.50		-			1	1	1	2.50	2.50	ALUMINIO + VIDRIO CLARO	MARCO DE ALUM ANOD. COLOR NATURAL	TERRAZA NIVEL 2900	
		P - D - 10	1.00	2.50	-				1	1	1	2.50	2.50	ALUMINIO + VIDRIO CLARO	MARCO DE ALUM ANOD. COLOR NATURAL	TERRAZA NIVEL 2900	
		P - 1	1.00	2.15	-				3	1	3			MADERA	MARCOS NTEGRALES DE MADERA	ENTRADA: DEPTO NIVEL 2800, CUARTO DE B.P.	
		P - 2	1.00	2.15		-			3	1	3			MADERA	MARCOS NTEGRALES DE MADERA	ENTRADA: DEPTO NIVEL 2800, CUARTO DE B.P.	
		P - 3	0.80	2.15	-				13	1	13			MADERA	MARCOS NTEGRALES DE MADERA	REC. Y S.S. DE TODOS LOS MODELOS APTO.	
		P - 4	0.80	2.15		-			13	1	13			MADERA	MARCOS NTEGRALES DE MADERA	REC. Y S.S. DE TODOS LOS MODELOS APTO.	
		P - 7	1.00	2.15		-			1	1	1			METAL	MARCOS NTEGRALES DE METAL	CUARTO DE MAQUINA	
		P - 15	1.00	2.15	-				1	1	1			METAL	MARCOS NTEGRALES DE METAL	CUARTO DE MAQUINA	
		P - 11	1.00	2.15	-				1	1	1			PUERTA PRESURIZADA	AISLAMIENTO TERMICO RESISTENTE AL FUEGO	ESCALERA DE AZOTEA	
		P - 12	1.00	2.15		-			1	1	1			PUERTA PRESURIZADA	AISLAMIENTO TERMICO RESISTENTE AL FUEGO	CUARTO DE BOMBA DE AGUA	

INGENIERIA MUNICIPAL
DISTRITO DE SAN CARLOS
APROBADO
INGENIERO MUNICIPAL
FECHA: 22/8/11

Cuerpo de Bomberos
OFICINA DE SEGURIDAD
La Chorrera
La Chorrera, 31 de Agosto de 2011
Resolución No. 31-11
Se aprueba el registro de este plano para llenar las condiciones requeridas.
Oficina de Seguridad

FELIPE GONZALEZ LINCK
ARQUITECTO
LICENCIA No. AY-1-102
LEY 15 DEL 26 DE ENERO DE 1959
JUNTA TECNICA DE INGENIERIA Y ARQUITECTURA

FELIFE GONZÁLEZ LINCK
ARQUITECTO
Tel: -- 66771610 -- Fax 392-2457 | 64035839

DISEÑO ARQUITECTÓNICO	Arq. Vicente Cortes Arq. Igor Cortes
DESARROLLO	Arq. Igor Cortes Arq. Ilem Segismond Arq. Nancy Urriola
PROYECTO ESTRUCTURAL	Ing. Ricauter Bowen
PROYECTO ELÉCTRICO	Ing. Edgar Naranjo
PROYECTO DE PLOMERÍA	Ing. Gilberto Ayala

PROYECTO

Residencial El Palmar

UBICACIÓN

COMUNIDAD DE 'EL PALMAR'
DTTO. DE SAN CARLOS - CORREGIMIENTO DE SAN CARLOS
PANAMÁ

SOCIEDAD PROMOTORA

Inversiones Decuria, S.A.

Representante legal: IGOR CORTES
Número de cédula o pasaporte: 8-705-1493

INGENIERÍA MUNICIPAL

PLANO

- DETALLE DE PUERTAS TORRE B

ARCHIVO .DWG	PUERTAS
FECHA	30/08/2010
FECHA MODIFICACIÓN	DD/MM/AAAA

ARQUITECTURA | HOJA: 55 | DE: 65

NIVEL 000 TORRE " B "

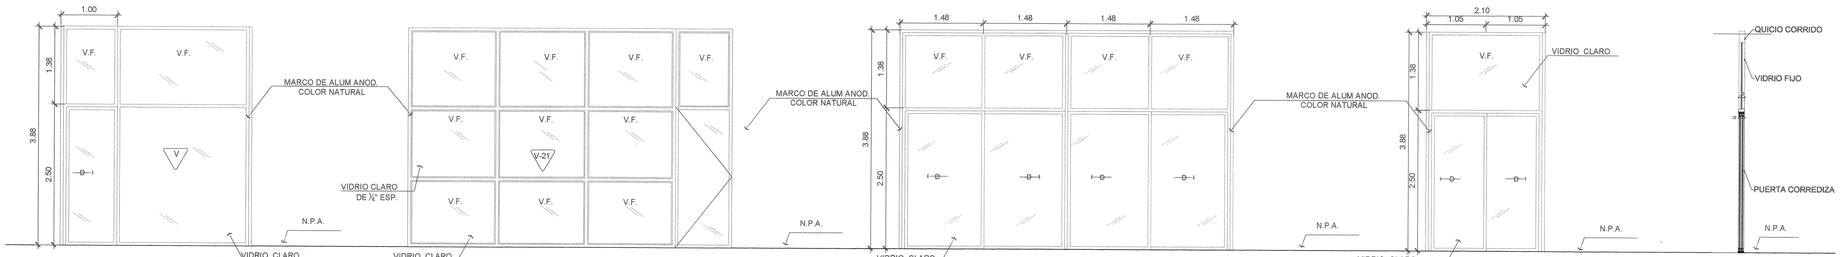

PUERTA P-18 ESC. 1/50

PUERTA P-16 ESC. 1/50

PUERTA P-30 ESC. 1/50

PUERTA P-25 ESC. 1/50

CORTE DE PUERTAS NIVEL 000
ESC. 1/50

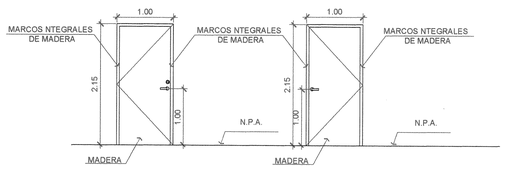

PUERTA P-1 ESC. 1/50

PUERTA P-2 ESC. 1/50

ESPECIFICACION:
DE LAMINAS DECORATIVAS CON RELLENO DE POLIESTIRENO, ACABADO EN COLOR A ESCOGER.
EL DISEÑO Y EL COLOR SERA ESCOGIDO POR EL ARQ. Y/O PROMOTOR DEL PROYECTO.

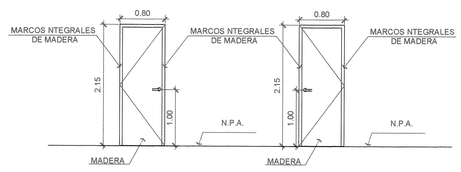

PUERTA P-3 ESC. 1/50

PUERTA P-4 ESC. 1/50

ESPECIFICACION:
CON RELLENO DE POLIESTIRENO ACUSTICO LAMINADAS CON CHAPAS DDE MDF PREPINTADAS EN COLOR A ESCOGER POR EL ARQ. Y/O PROMOTOR.
EL DISEÑO Y EL COLOR SERA ESCOGIDO POR EL ARQ. Y/O PROMOTOR DEL PROYECTO.

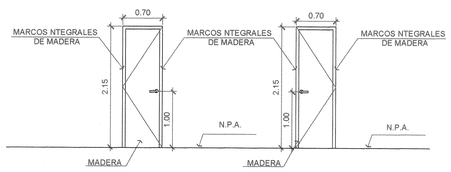

PUERTA P-5 ESC. 1/50

PUERTA P-6 ESC. 1/50

ESPECIFICACION:
CON RELLENO DE POLIESTIRENO ACUSTICO LAMINADAS CON CHAPAS DDE MDF PREPINTADAS EN COLOR A ESCOGER POR EL ARQ. Y/O PROMOTOR.
EL DISEÑO Y EL COLOR SERA ESCOGIDO POR EL ARQ. Y/O PROMOTOR DEL PROYECTO.

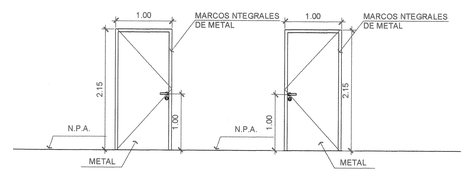

PUERTA P-6 ESC. 1/50

PUERTA P-7 ESC. 1/50

PUERTA P-15 ESC. 1/50

ESPECIFICACION:
PUERTA CONTRA INCENDIO DE METAL DE CON ESTRUCTURA METALICA CAL. 16
MARCO DE 1-1/2 X 5 CAL. 15 CON 3 BISAGRAS DE 4" RESISTENTE AL FUEGO

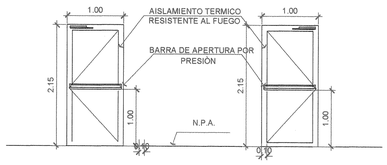

PUERTA P-11 ESC. 1/50

PUERTA P-12 ESC. 1/50

ESPECIFICACION:
PUERTA CONTRA INCENDIO DE METAL DE CON ESTRUCTURA METALICA CAL. 16
MARCO DE 1-1/2 X 5 CAL. 15 CON 3 BISAGRAS DE 4" RESISTENTE AL FUEGO

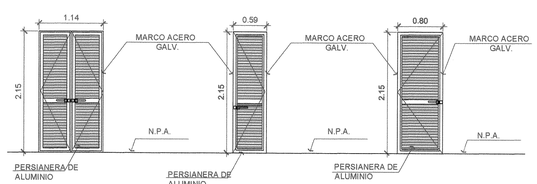

PUERTA P-8 ESC. 1/50

PUERTA P-9 ESC. 1/50

PUERTA P-13 ESC. 1/50

ESPECIFICACION:
PUERTA DE PERSIANA CON ESTRUCTURA METALICA INTERNA.
MARCO DE ACERO GALV. CAL #20 DE 1X4 CON 3 BISAGRAS EN COLOR A ESCOGER POR EL ARQ.

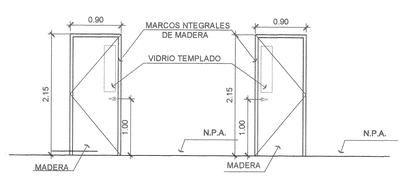

PUERTA P-27 ESC. 1/50

PUERTA P-28 ESC. 1/50

ESPECIFICACION:
PUERTA COORDINADA POR EL DUEÑO SEGÚN ESPECIFICACIÓN DE SAUNA

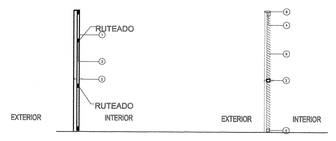

CORTE GENERAL P. DE MADERA

CORTE GENERAL P. DE PERSIANAS

LEYENDA:
1. LAMINAS DECORATIVAS CON RELLENO DE POLIESTIRENO ACABADO EN ESCOGER POR EL PROMOTOR O ARQ.
2. MANIJA
3. BASTIDOR DE MADERA
4. MARCO PRESURIZADO CON EMPAQUETADURA RESISTENTE AL FUEGO
5.PERSIANERA DE ALUMINIO
6. MARCO DE ACERO GALVANIZADO.

INGENIERIA MUNICIPAL
DISTRITO DE SAN CARLOS
APROBADO
INGENIERO MUNICIPAL
FECHA 22/8/11

Cuerpo de Bomberos
OFICINA DE SEGURIDAD
La Chorrera, 19/8/11
Resolución No. 2011
Se aprueba el registro de este plano por decir las condiciones exigidas
Jefa Regional de la Oficina de Seguridad

FELIPE GONZALEZ LINCK
ARQUITECTO
LICENCIA No. 97-1-108
LEY 15 DEL 26 DE ENERO DE 1959
JUNTA TECNICA DE INGENIERIA Y ARQUITECTURA

FELIFE GONZÁLEZ LINCK
ARQUITECTO
Tel. – 66771610 – Fax 392-2457 | 64035839

DISEÑO ARQUITECTÓNICO	Arq. Vicente Cortes Arq. Igor Cortes
DESARROLLO	Arq. Igor Cortes Arq. Ilem Segismond Arq. Nancy Urriola
PROYECTO ESTRUCTURAL	Ing. Ricauter Bowen
PROYECTO ELÉCTRICO	Ing. Edgar Naranjo
PROYECTO DE PLOMERÍA	Ing. Gilberto Ayala

PROYECTO
Residencial El Palmar

UBICACIÓN
COMUNIDAD DE 'EL PALMAR'
DTTO. DE SAN CARLOS - CORREGIMIENTO DE SAN CARLOS
PANAMÁ

SOCIEDAD PROMOTORA
Inversiones Decuria, S.A.
Representante legal: IGOR CORTES
Número de cédula o pasaporte: 8C054493

INGENIERÍA MUNICIPAL

PLANO
- DETALLES DE PUERTAS TORRE B

ARCHIVO .DWG	PUERTAS
FECHA	30/08/2010
FECHA MODIFICACIÓN	DD/MM/AAAA

ARQUITECTURA | HOJA: 56 | DE: 65

CUADRO DE VENTANAS TORRE "A"

UBICACION	NIVEL	N°	VANO ANCHO	VANO ALTO	ANTEPECHO	CANT. X NIVEL	NUM. NIVELES	CANT. TOTAL	SUP. UNIT. VIDRIO (M2)	SUP. TOTAL VIDRIO (M2)	VIDRIO	FERRETERIA	DESCRIPCION	UBICACION
	NIVEL 000	V - 1	2.11	3.48	0.40	1	1	1	7.34	7.34	VIDRIO CLARO DE ¼" ESP.	MARCO DE 1 ¾" X 4" DE ALUM. ANODIZADO NATURAL	4 PAÑOS FIJOS	ÁREA DE ASENSORES
		V - 2	2.03	3.88	0.00	1	1	1	7.88	7.88	VIDRIO CLARO DE ¼" ESP.	MARCO DE 1 ¾" X 4" DE ALUM. ANODIZADO NATURAL	2 PAÑOS FIJOS	SALA DE EVENTOS
		V - 3	2.38	3.88	0.00	2	1	2	9.23	18.46	VIDRIO CLARO DE ¼" ESP.	MARCO DE 1 ¾" X 4" DE ALUM. ANODIZADO NATURAL	2 PAÑOS FIJOS	SALA DE EVENTOS
		V - 4	1.00	3.88	0.00	1	1	1	3.88	3.88	VIDRIO CLARO DE ¼" ESP.	MARCO DE 1 ¾" X 4" DE ALUM. ANODIZADO NATURAL	2 PAÑOS FIJOS	COMERCIO # 1
		V - 5	0.92	3.88	0.00	1	1	1	3.57	3.57	VIDRIO CLARO DE ¼" ESP.	MARCO DE 1 ¾" X 4" DE ALUM. ANODIZADO NATURAL	2 PAÑOS FIJOS	COMERCIO #1
		V - 6	1.18	3.88	0.00	1	1	1	4.58	4.58	VIDRIO CLARO DE ¼" ESP.	MARCO DE 1 ¾" X 4" DE ALUM. ANODIZADO NATURAL	2 PAÑOS FIJOS	COMERCIO #1
		V - 7	1.00	3.88	0.00	1	1	1	3.88	3.88	VIDRIO CLARO DE ¼" ESP.	MARCO DE 1 ¾" X 4" DE ALUM. ANODIZADO NATURAL	3 PAÑOS FIJOS	SALA DE EVENTOS
		V - 8	3.10	3.88	0.00	1	1	1	12.00	12.00	VIDRIO CLARO DE ¼" ESP.	MARCO DE 1 ¾" X 4" DE ALUM. ANODIZADO NATURAL	2 PAÑOS FIJOS	ÁREA INFANTIL
		V - 9	1.60	3.88	0.00	1	1	1	6.21	6.21	VIDRIO CLARO DE ¼" ESP.	MARCO DE 1 ¾" X 4" DE ALUM. ANODIZADO NATURAL	3 PAÑOS FIJOS	SALA DE AUDIOVISUALES
		V - 10	1.98	3.88	0.00	1	1	1	7.69	7.69	VIDRIO CLARO DE ¼" ESP.	MARCO DE 1 ¾" X 4" DE ALUM. ANODIZADO NATURAL	3 PAÑOS FIJOS	SALA DE AUDIOVISUALES
		V - 11	2.50	3.88	0.00	1	1	1	9.70	9.70	VIDRIO CLARO DE ¼" ESP.	MARCO DE 1 ¾" X 4" DE ALUM. ANODIZADO NATURAL	6 PAÑOS FIJOS	AREA DE ASENSORES NIV. -100@-400
		V - 24	2.11	0.95	1.25	1	27	27	2.00	54.12	VIDRIO CLARO DE ¼" ESP.	MARCO DE 1 ¾" X 4" DE ALUM. ANODIZADO NATURAL	2 PAÑOS CORREDIZOS	AREA DE ASENSORES NIV. 100@ 2700
TIPO "A - B"	NIVEL 100 @ 2200	V - B - 1	2.60	1.25	1.25	2	22	44	3.25	143.00	VIDRIO CLARO DE ¼" ESP.	MARCO DE 1 ¾" X 4" DE ALUM. ANODIZADO NATURAL	2 PAÑOS CORREDIZOS	RECAMARA #2
		V - B - 2	1.73	1.25	1.25	2	22	44	2.16	95.04	VIDRIO CLARO DE ¼" ESP.	MARCO DE 1 ¾" X 4" DE ALUM. ANODIZADO NATURAL	2 PAÑOS CORREDIZOS	COCINA
		V - B - 3	0.80	0.95	1.25	2	22	44	0.84	36.96	VIDRIO CLARO DE ¼" ESP.	MARCO DE 1 ¾" X 4" DE ALUM. ANODIZADO NATURAL	1 PAÑO TIPO ABATIBLE	S. SANITARIO # B2
		V - B - 4	0.80	0.95	1.25	2	22	44	0.84	36.96	VIDRIO CLARO DE ¼" ESP.	MARCO DE 1 ¾" X 4" DE ALUM. ANODIZADO NATURAL	1 PAÑO TIPO ABATIBLE	S. SANITARIO # B1
		V - B - 5	1.80	2.50	0.00	2	22	44	4.50	198.00	VIDRIO CLARO DE ¼" ESP.	MARCO DE 1 ¾" X 4" DE ALUM. ANODIZADO NATURAL	DOS PAÑOS FIJOS	RECAMARA #1
		V - A - 1	1.42	2.50	0.00	2	22	44	3.75	165.00	VIDRIO CLARO DE ¼" ESP.	MARCO DE 1 ¾" X 4" DE ALUM. ANODIZADO NATURAL	1 PAÑO FIJO	SALA/ COMEDOR
TIPO "C"	NIVEL 2300 @ 2500	V - C - 1	2.50	1.25	1.25	2	3	6	3.13	18.78	VIDRIO CLARO DE ¼" ESP.	MARCO DE 1 ¾" X 4" DE ALUM. ANODIZADO NATURAL	2 PAÑOS CORREDIZOS	RECAMARA #3
		V - C - 2	1.78	1.25	1.25	2	3	6	2.22	13.32	VIDRIO CLARO DE ¼" ESP.	MARCO DE 1 ¾" X 4" DE ALUM. ANODIZADO NATURAL	2 PAÑOS CORREDIZOS	REC. SERVICIO
		V - C - 3	0.80	0.95	1.25	2	3	6	0.84	5.04	VIDRIO CLARO DE ¼" ESP.	MARCO DE 1 ¾" X 4" DE ALUM. ANODIZADO NATURAL	1 PAÑO TIPO ABATIBLE	S. SANITARIO # C2
		V - C - 4	0.80	0.95	1.25	2	3	6	0.84	5.04	VIDRIO CLARO DE ¼" ESP.	MARCO DE 1 ¾" X 4" DE ALUM. ANODIZADO NATURAL	1 PAÑO TIPO ABATIBLE	S. SANITARIO # C1
		V - C - 5	1.25	0.95	1.25	2	3	6	1.19	7.14	VIDRIO CLARO DE ¼" ESP.	MARCO DE 1 ¾" X 4" DE ALUM. ANODIZADO NATURAL	2 PAÑOS CORREDIZOS	S. SANITARIO #C3
TIPO "D"	NIVEL 2600 @ 2800	V - D - 1	1.20	1.25	1.25	2	1	2	1.50	3.00	VIDRIO CLARO DE ¼" ESP.	MARCO DE 1 ¾" X 4" DE ALUM. ANODIZADO NATURAL	2 PAÑOS CORREDIZOS	REC. DE SERVICIO
		V - D - 2	4.47	2.50	0.00	2	1	2	11.18	22.35	VIDRIO CLARO DE ¼" ESP.	MARCO DE 1 ¾" X 4" DE ALUM. ANODIZADO NATURAL	3 VIDRIOS FIJOS	BALCON
		V - D - 3	1.05	1.90	0.40	2	1	2	1.10	2.20	VIDRIO CLARO DE ¼" ESP.	MARCO DE 1 ¾" X 4" DE ALUM. ANODIZADO NATURAL	1 PAÑO TIPO ABATIBLE	S. SANITARIO # D3
		V - D - 4	1.65	1.90	0.40	2	1	2	3.16	6.32	VIDRIO CLARO DE ¼" ESP.	MARCO DE 1 ¾" X 4" DE ALUM. ANODIZADO NATURAL	2 PAÑOS CORREDIZOS	S. SANITARIO # D3
		V - D - 5	0.60	0.60	1.60	2	1	2	0.36	0.72	VIDRIO CLARO DE ¼" ESP.	MARCO DE 1 ¾" X 4" DE ALUM. ANODIZADO NATURAL	2 PAÑOS CORREDIZOS	S. SANITARIO # D4
		V - D - 6	1.50	1.25	1.25	2	1	2	1.88	3.76	VIDRIO CLARO DE ¼" ESP.	MARCO DE 1 ¾" X 4" DE ALUM. ANODIZADO NATURAL	2 PAÑOS CORREDIZOS	ESTUDIO

NOTAS DE INSTALACION:

"- LOS PERFILES QUE SUGERIMOS SON PARA ESTABLECER UN PATRON PARA LOS LICITANTES. CADA PROVEEDOR SUMINISTRARA SUS PERFILES PARA QUE TODAS LAS VENTANAS OPEREN SIN PROBLEMAS Y CUMPLAN CON TODOS LOS REQUERIMIENTOS DE SEGURIDAD Y PROTECCION CONTRA LOS ELEMENTOS NATURALES.

NIVEL 000

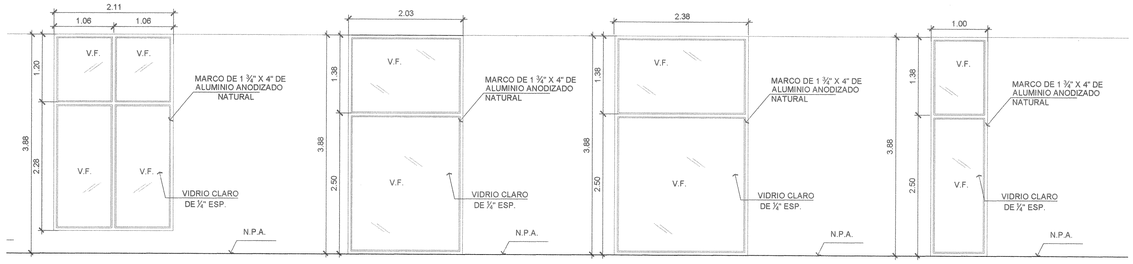

VENTANA V-1 ESC. 1/50 | VENTANA V-2 ESC. 1/50 | VENTANA V-3 ESC. 1/50 | VENTANA V-4 ESC. 1/50

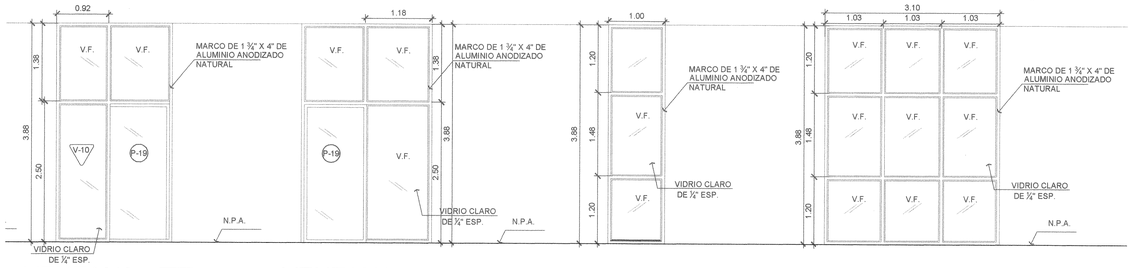

VENTANA V-5 ESC. 1/50 | VENTANA V-6 ESC. 1/50 | VENTANA V-7 ESC. 1/50 | VENTANA V-8 ESC. 1/50

APART. 1 REC. TIPO " A " NIVEL 100 @ 2200

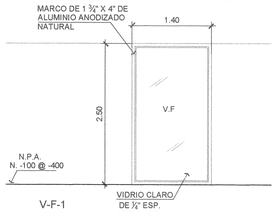

VENTANA V-A-1 ESC. 1/50

VENTANA DE AREA DE A/A EN NIV. 100 @ 2700

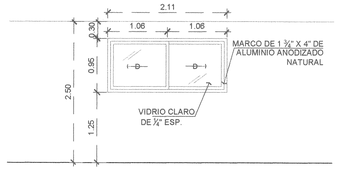

VENTANA V-24 ESC. 1/50

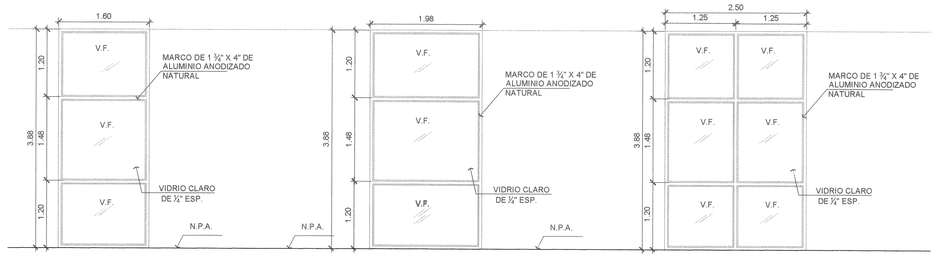

VENTANA V-9 ESC. 1/50 | VENTANA V-10 ESC. 1/50 | VENTANA V-11 ESC. 1/50

APART. 2 REC. TIPO " B " NIVEL 100 @ 2200

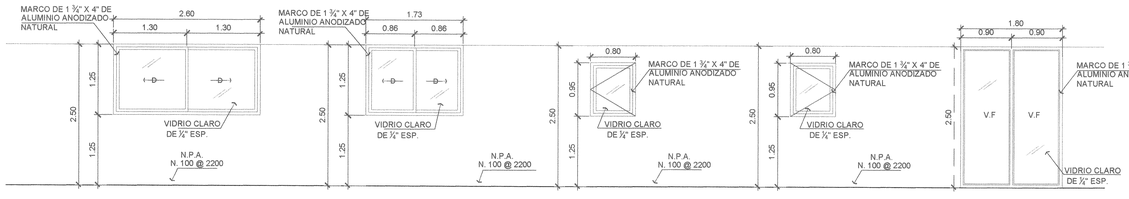

VENTANA V-B-1 ESC. 1/50 | VENTANA V-B-2 ESC. 1/50 | VENTANA V-B-3 ESC. 1/50 | VENTANA V-B-4 ESC. 1/50 | VENTANA V-B-5 ESC. 1/50

APART. 3 REC. TIPO " C " NIVEL 2300 @ 2500

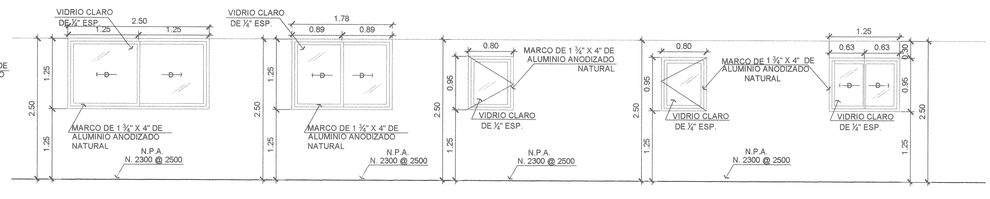

VENTANA V-C-1 ESC. 1/50 | VENTANA V-C-2 ESC. 1/50 | VENTANA V-C-3 ESC. 1/50 | VENTANA V-C-4 ESC. 1/50 | VENTANA V-C-5 ESC. 1/50

APART. 4 REC. TIPO " D " NIVEL 2600 @ 2800

VENTANA V-D-1 ESC. 1/50 | VENTANA V-D-2 ESC. 1/50 | VENTANA V-D-3 ESC. 1/50 | VENTANA V-D-4 ESC. 1/50 | VENTANA V-D-5 ESC. 1/50 | VENTANA V-D-6 ESC. 1/50

INGENIERIA MUNICIPAL
DISTRITO DE SAN CARLOS
APROBADO
INGENIERO MUNICIPAL
FECHA: 22 / 8 / 11

Cuerpo de Bomberos de Panamá
OFICINA DE SEGURIDAD
La Chorrera, 11 de Agosto de 2011
Resolución No. 2-11
Se aprueba el cuadro de ventanas, plano, para llenar las condiciones requeridas.
Jefe Oficina de Seguridad

FELIPE GONZALEZ LINCK
ARQUITECTO
EXCENCIA No. 77-1-188
LEY 15 DEL 26 DE ENERO DE 1959
JUNTA TECNICA DE INGENIERIA Y ARQUITECTURA

FELIPE GONZÁLEZ LINCK
ARQUITECTO
Tel: – 66771610 – Fax 392-2457 | 64035830

DISEÑO ARQUITECTÓNICO	Arq. Vicente Cortes Arq. Igor Cortes
DESARROLLO	Arq. Igor Cortes Arq. Ilem Segismond Arq. Nancy Urriola
PROYECTO ESTRUCTURAL	Ing. Ricauter Bowen
PROYECTO ELÉCTRICO	Ing. Edgar Naranjo
PROYECTO DE PLOMERÍA	Ing. Gilberto Ayala

PROYECTO

Residencial El Palmar

UBICACIÓN
COMUNIDAD DE 'EL PALMAR'
DTTO. DE SAN CARLOS - CORREGIMIENTO DE SAN CARLOS
PANAMÁ

SOCIEDAD PROMOTORA
Inversiones Decuria, S.A.
Representante legal: IGOR CORTES
Número de cédula o pasaporte: 8C054493

INGENIERÍA MUNICIPAL

PLANO
- CUADRO DE VENTANAS TORRE A

ARCHIVO .DWG	VENTANAS
FECHA	30/08/2010
FECHA MODIFICACIÓN	DD/MM/AAAA

ARQUITECTURA | HOJA: 57 | DE: 65

CUADRO DE VENTANAS TORRE " B"

UBICACION	NIVEL	N°	VANO ANCHO	VANO ALTO	ANTEPECHO	CANT. X NIVEL	NUM. NIVELES	CANT. TOTAL	SUP. UNIT. VIDRIO (M2)	SUP. TOTAL VIDRIO (M2)	VIDRIO	FERRETERIA	DESCRIPCION	UBICACION
	NIVEL 000	V - 1	2.11	3.48	0.40	1	1	1	7.34	7.34	VIDRIO CLARO DE ¼" ESP.	MARCO DE 1 ¾" X 4" DE ALUM. ANODIZADO NATURAL	4 PAÑOS FIJOS	ÁREA DE ASENSORES
		V - 12	1.00	1.20	2.68	1	1	1	1.20	1.20	VIDRIO CLARO DE ¼" ESP.	MARCO DE 1 ¾" X 4" DE ALUM. ANODIZADO NATURAL	1 PAÑO FIJO	DEPOSITO #4
		V - 13	1.20	3.88	0.00	1	1	1	4.67	4.67	VIDRIO CLARO DE ¼" ESP.	MARCO DE 1 ¾" X 4" DE ALUM. ANODIZADO NATURAL	3 PAÑOS FIJOS	CANCHA DE SQUACH
		V - 14	3.15	3.88	0.00	2	1	2	12.30	24.60	VIDRIO CLARO DE ¼" ESP.	MARCO DE 1 ¾" X 4" DE ALUM. ANODIZADO NATURAL	6 PAÑOS FIJOS	SAUNA
		V - 15	2.86	2.68	1.20	2	1	2	7.66	15.32	VIDRIO CLARO DE ¼" ESP.	MARCO DE 1 ¾" X 4" DE ALUM. ANODIZADO NATURAL	4 PAÑOS FIJOS	JACUZZI
		V - 16	2.00	1.25	1.25	1	1	1	2.50	2.50	VIDRIO CLARO DE ¼" ESP.	MARCO DE 1 ¾" X 4" DE ALUM. ANODIZADO NATURAL	2 PAÑOS CORREDIZOS	SALA/ COMEDOR APTO CONSERJE
		V - 17	1.50	1.25	1.25	1	1	1	1.88	1.88	VIDRIO CLARO DE ¼" ESP.	MARCO DE 1 ¾" X 4" DE ALUM. ANODIZADO NATURAL	2 PAÑOS CORREDIZOS	REC. #1 CONSERJE
		V - 18	0.69	0.60	1.60	1	1	1	0.41	0.41	VIDRIO CLARO DE ¼" ESP.	MARCO DE 1 ¾" X 4" DE ALUM. ANODIZADO NATURAL	2 PAÑOS CORREDIZOS	S.S. CONSERJE
		V - 19	1.30	1.25	1.25	1	1	1	1.63	1.63	VIDRIO CLARO DE ¼" ESP.	MARCO DE 1 ¾" X 4" DE ALUM. ANODIZADO NATURAL	2 PAÑOS CORREDIZOS	REC. #2 CONSERJE
		V - 20	0.60	0.60	1.60	1	1	1	0.36	0.36	VIDRIO CLARO DE ¼" ESP.	MARCO DE 1 ¾" X 4" DE ALUM. ANODIZADO NATURAL	2 PAÑOS CORREDIZOS	S.S. COMERCIO # 2
		V - 21	4.73	3.88	0.00	1	1	1	18.35	18.35	VIDRIO CLARO DE ¼" ESP.	MARCO DE 1 ¾" X 4" DE ALUM. ANODIZADO NATURAL	6 PAÑOS CORREDIZOS	COMERCIO #2
		V - 22	1.30	3.88	0.00	1	1	1			VIDRIO CLARO DE ¼" ESP.	MARCO DE 1 ¾" X 4" DE ALUM. ANODIZADO NATURAL	2 PAÑOS CORREDIZOS	COMERCIO #2
		V - 24	2.11	0.95	1.25	1	27	27	2.00	54.12	VIDRIO CLARO DE ¼" ESP.	MARCO DE 1 ¾" X 4" DE ALUM. ANODIZADO NATURAL	2 PAÑOS CORREDIZOS	AREA DE ASENSORES NIV. 100 @ 2700
TIPO "A - B"	NIVEL 100 @ 2200	V - B - 1	2.60	1.25	1.25	2	22	44	3.25	143.00	VIDRIO CLARO DE ¼" ESP.	MARCO DE 1 ¾" X 4" DE ALUM. ANODIZADO NATURAL	2 PAÑOS CORREDIZOS	RECAMARA #2
		V - B - 2	1.73	1.25	1.25	2	22	44	2.16	95.04	VIDRIO CLARO DE ¼" ESP.	MARCO DE 1 ¾" X 4" DE ALUM. ANODIZADO NATURAL	2 PAÑOS CORREDIZOS	COCINA
		V - B - 3	0.80	0.95	1.25	2	22	44	0.84	36.96	VIDRIO CLARO DE ¼" ESP.	MARCO DE 1 ¾" X 4" DE ALUM. ANODIZADO NATURAL	1 PAÑO TIPO ABATIBLE	S. SANITARIO # B2
		V - B - 4	0.80	0.95	1.25	2	22	44	0.84	36.96	VIDRIO CLARO DE ¼" ESP.	MARCO DE 1 ¾" X 4" DE ALUM. ANODIZADO NATURAL	1 PAÑO TIPO ABATIBLE	S. SANITARIO # B1
		V - A - 1	1.42	2.50	0.00	2	22	44	3.75	165.00	VIDRIO CLARO DE ¼" ESP.	MARCO DE 1 ¾" X 4" DE ALUM. ANODIZADO NATURAL	1 PAÑO FIJO	SALA/ COMEDOR
		V - C - 1	2.50	1.25	1.25	2	3	6	3.13	18.78	VIDRIO CLARO DE ¼" ESP.	MARCO DE 1 ¾" X 4" DE ALUM. ANODIZADO NATURAL	2 PAÑOS CORREDIZOS	RECAMARA #3
TIPO "C"	NIVEL 2300 @ 2500	V - C - 2	1.78	1.25	1.25	2	3	6	2.22	13.32	VIDRIO CLARO DE ¼" ESP.	MARCO DE 1 ¾" X 4" DE ALUM. ANODIZADO NATURAL	2 PAÑOS CORREDIZOS	REC. SERVICIO
		V - C - 3	0.80	0.95	1.25	2	3	6	0.84	5.04	VIDRIO CLARO DE ¼" ESP.	MARCO DE 1 ¾" X 4" DE ALUM. ANODIZADO NATURAL	1 PAÑO TIPO ABATIBLE	S. SANITARIO # C2
		V - C - 4	0.80	0.95	1.25	2	3	6	0.84	5.04	VIDRIO CLARO DE ¼" ESP.	MARCO DE 1 ¾" X 4" DE ALUM. ANODIZADO NATURAL	1 PAÑO TIPO ABATIBLE	S. SANITARIO # C1
		V - C - 5	1.25	0.95	1.25	2	3	6	1.19	7.14	VIDRIO CLARO DE ¼" ESP.	MARCO DE 1 ¾" X 4" DE ALUM. ANODIZADO NATURAL	2 PAÑOS CORREDIZOS	S. SANITARIO #C3
		V - D - 1	2.43	1.25	1.25	2	1	2	3.04	6.08	VIDRIO CLARO DE ¼" ESP.	MARCO DE 1 ¾" X 4" DE ALUM. ANODIZADO NATURAL	2 PAÑOS CORREDIZOS	REC. DE SERVICIO
TIPO "D"	NIVEL 2600 @ 2800	V - D - 1	1.20	1.25	1.25	2	1	2	1.50	3.00	VIDRIO CLARO DE ¼" ESP.	MARCO DE 1 ¾" X 4" DE ALUM. ANODIZADO NATURAL	1 PAÑO TIPO ABATIBLE	SALA COMEDOR
		V - D -2	4.47	2.50	0.00	2	1	2	11.18	22.35	VIDRIO CLARO DE ¼" ESP.	MARCO DE 1 ¾" X 4" DE ALUM. ANODIZADO NATURAL	3 VIDRIOS FIJOS	BALCON
		V - D - 3	1.05	1.90	0.40	2	1	2	1.10	2.20	VIDRIO CLARO DE ¼" ESP.	MARCO DE 1 ¾" X 4" DE ALUM. ANODIZADO NATURAL	1 PAÑO TIPO ABATIBLE	S. SANITARIO # D3
		V - D - 4	1.65	1.90	0.40	2	1	2	3.16	6.32	VIDRIO CLARO DE ¼" ESP.	MARCO DE 1 ¾" X 4" DE ALUM. ANODIZADO NATURAL	2 PAÑOS CORREDIZOS	S. SANITARIO # D3
		V - D - 5	0.60	0.60	1.60	2	1	2	0.36	0.72	VIDRIO CLARO DE ¼" ESP.	MARCO DE 1 ¾" X 4" DE ALUM. ANODIZADO NATURAL	2 PAÑOS CORREDIZOS	S. SANITARIO # D4
		V - D - 6	1.50	1.25	1.25	2	1	2	1.88	3.76	VIDRIO CLARO DE ¼" ESP.	MARCO DE 1 ¾" X 4" DE ALUM. ANODIZADO NATURAL	2 PAÑOS CORREDIZOS	ESTUDIO

NOTAS DE INSTALACION:

*- LOS PERFILES QUE SUGERIMOS SON PARA ESTABLECER UN PATRON PARA LOS LICITANTES. CADA PROVEEDOR SUMINISTRARA SUS PERFILES PARA QUE TODAS LAS VENTANAS OPEREN SIN PROBLEMAS Y CUMPLAN CON TODOS LOS REQUERIMIENTOS DE SEGURIDAD Y PROTECCION CONTRA LOS ELEMENTOS NATURALES.

NIVEL 000

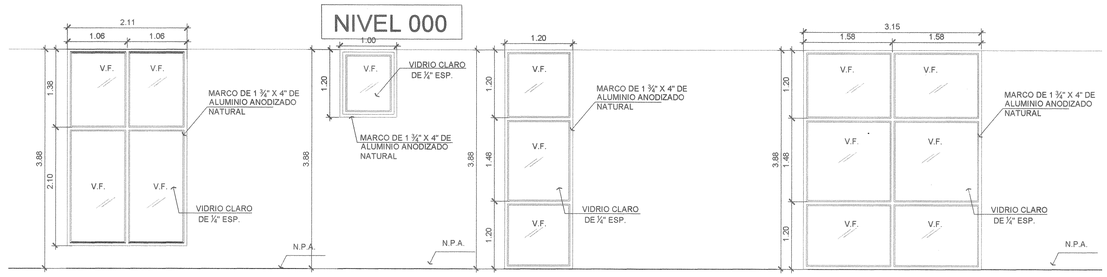

VENTANA V-1 ESC. 1/50 — VENTANA V-12 ESC. 1/50 — VENTANA V-13 ESC. 1/50 — VENTANA V-14 ESC. 1/50

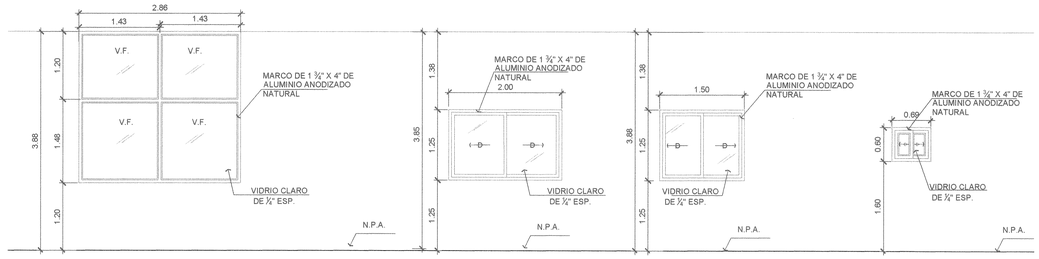

VENTANA V-15 ESC. 1/50 — VENTANA V-16 ESC. 1/50 — VENTANA V-17 ESC. 1/50 — VENTANA V-18 ESC. 1/50

APART. 1 REC. TIPO " A " NIVEL 100 @ 2200

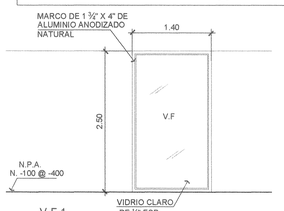

V-F-1

VENTANA V-A-1 ESC. 1/50

VENTANA DE AREA DE A/A EN NIV. 100 @ 2700

VENTANA V-24 ESC. 1/50

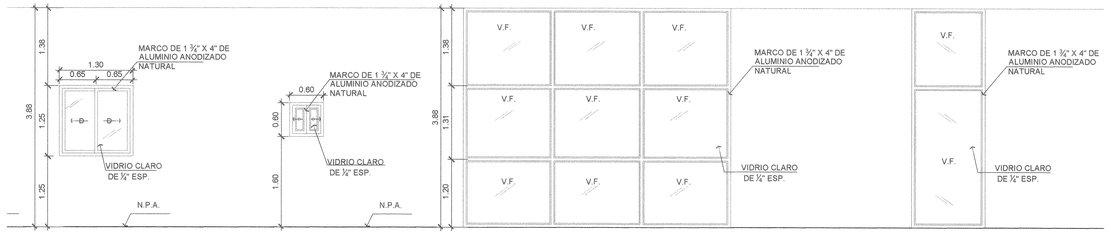

VENTANA V-19 ESC. 1/50 — VENTANA V-20 ESC. 1/50 — VENTANA V-21 ESC. 1/50 — VENTANA V-22 ESC. 1/50

APART. 2 REC. TIPO " B " NIVEL 100 @ 2200

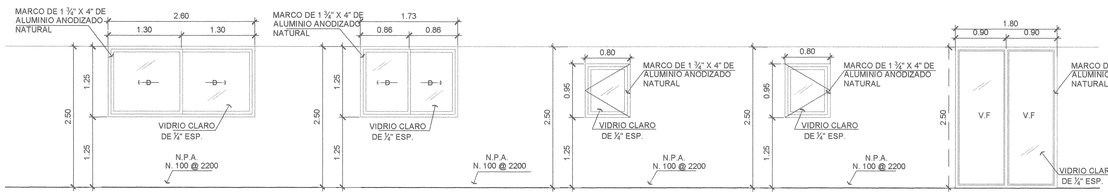

VENTANA V-B-1 ESC. 1/50 — VENTANA V-B-2 ESC. 1/50 — VENTANA V-B-3 ESC. 1/50 — VENTANA V-B-4 ESC. 1/50 — VENTANA V-B-5 ESC. 1/50

APART. 3 REC. TIPO " C " NIVEL 2300 @ 2500

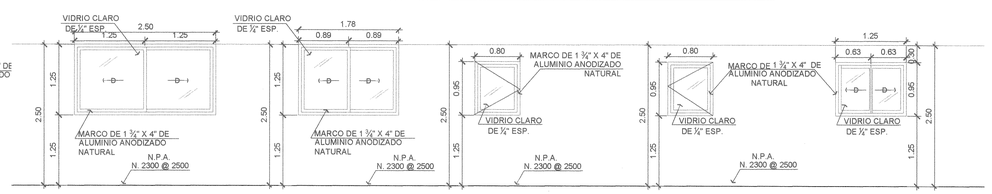

VENTANA V-C-1 ESC. 1/50 — VENTANA V-C-2 ESC. 1/50 — VENTANA V-C-3 ESC. 1/50 — VENTANA V-C-4 ESC. 1/50 — VENTANA V-C-5 ESC. 1/50

APART. 4 REC. TIPO " D " NIVEL 2600 @ 2800

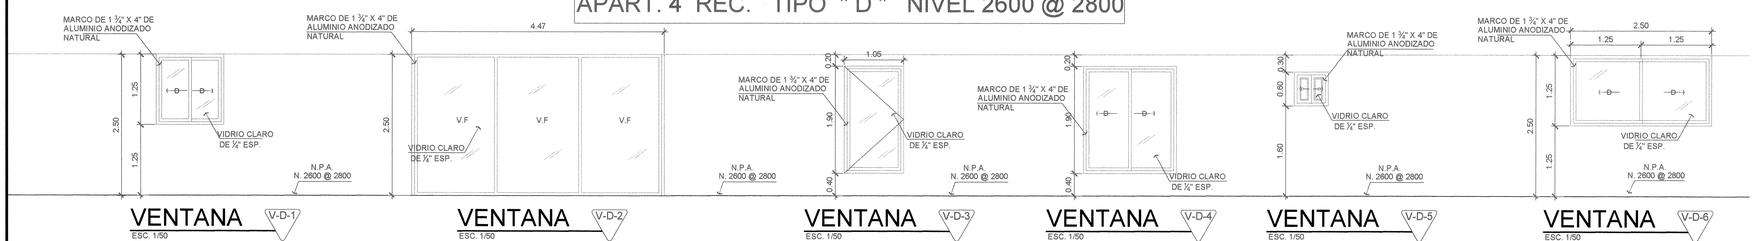

VENTANA V-D-1 ESC. 1/50 — VENTANA V-D-2 ESC. 1/50 — VENTANA V-D-3 ESC. 1/50 — VENTANA V-D-4 ESC. 1/50 — VENTANA V-D-5 ESC. 1/50 — VENTANA V-D-6 ESC. 1/50

INGENIERIA MUNICIPAL
DISTRITO DE SAN CARLOS
APROBADO
INGENIERO MUNICIPAL
FECHA 22 / 11

Cuerpo de Bomberos
OFICINA DE SEGURIDAD
La Chorrera, ... de 2011
Resolución No. ..... Plano No. .....
Se aprueba el registro de este plano por llenar las condiciones requeridas

FELIPE GONZALEZ LINCK
ARQUITECTO
LICENCIA No. 77-188
LEY 15 DEL 26 DE ENERO DE 1959
JUNTA TECNICA DE INGENIERIA Y ARQUITECTURA

FELIPE GONZÁLEZ LINCK
ARQUITECTO
Tel. – 66771610 – Fax 392-2457 | 64035939

DISEÑO ARQUITECTÓNICO	Arq. Vicente Cortes Arq. Igor Cortes
DESARROLLO	Arq. Igor Cortes Arq. Ilem Segismond Arq. Nancy Urriola
PROYECTO ESTRUCTURAL	Ing. Ricauter Bowen
PROYECTO ELÉCTRICO	Ing. Edgar Naranjo
PROYECTO DE PLOMERÍA	Ing. Gilberto Ayala

PROYECTO

Residencial El Palmar

UBICACIÓN

COMUNIDAD DE 'EL PALMAR'
DTTO. DE SAN CARLOS - CORREGIMIENTO DE SAN CARLOS
PANAMÁ

SOCIEDAD PROMOTORA

Inversiones Decuria, S.A.
Representante legal: IGOR CORTES
Número de cédula o pasaporte: BC054493

INGENIERÍA MUNICIPAL

PLANO

- CUADRO DE VENTANAS TORRE B

ARCHIVO .DWG	VENTANAS
FECHA	30/08/2010
FECHA MODIFICACIÓN	DD/MM/AAAA

ARQUITECTURA	HOJA: 58	DE: 65

CUADRO DE VENTANAS NIVEL - 400 @ -100

UBICACION	NIVEL	N°	VANO ANCHO	VANO ALTO	ANTEPECHO	CANT. X NIVEL	NUM. NIVELES	CANT. TOTAL	SUP. UNIT. VIDRIO (M2)	SUP. TOTAL VIDRIO (M2)	VIDRIO	FERRETERIA	DESCRIPCION	UBICACION
TIPO "E - F - G"	NIVEL -100 @ -400	V - E - 1	1.20	1.25	1.25	2	4	8	1.50	12.00	VIDRIO CLARO DE ¼" ESP.	MARCO DE 1 ½" X 4" DE ALUM. ANODIZADO NATURAL	2 PAÑOS CORREDIZOS	REC. SERVICIO
		V - E - 2	0.62	0.95	1.25	1	4	4	0.59	2.36	VIDRIO CLARO DE ¼" ESP.	MARCO DE 1 ½" X 4" DE ALUM. ANODIZADO NATURAL	1 PAÑO ABATIBLE A LA DERECHA	S. SANITARIO # E1
		V - E - 3	0.62	0.95	1.25	1	4	4	0.59	2.36	VIDRIO CLARO DE ¼" ESP.	MARCO DE 1 ½" X 4" DE ALUM. ANODIZADO NATURAL	1 PAÑO ABATIBLE A LA IZQUIERDA	S. SANITARIO # E1
		V - F - 1	1.42	2.50	0.00	6	4	24	3.55	85.20	VIDRIO CLARO DE ¼" ESP.	MARCO DE 1 ½" X 4" DE ALUM. ANODIZADO NATURAL	1 PAÑO FIJO	SALA/ COMEDOR
		V - F - 1	1.42	2.50	0.00	6	4	24	3.55	85.20	VIDRIO CLARO DE ¼" ESP.	MARCO DE 1 ½" X 4" DE ALUM. ANODIZADO NATURAL	1 PAÑO FIJO	SALA/ COMEDOR

NOTAS DE INSTALACION:

*- LOS PERFILES QUE SUGERIMOS SON PARA ESTABLECER UN PATRON PARA LOS LICITANTES. CADA PROVEEDOR SUMINISTRARA SUS PERFILES PARA QUE TODAS LAS VENTANAS OPEREN SIN PROBLEMAS Y CUMPLAN CON TODOS LOS REQUERIMIENTOS DE SEGURIDAD Y PROTECCION CONTRA LOS ELEMENTOS NATURALES.

APART. 3 REC. TIPO " E " NIVEL -100 @ -400

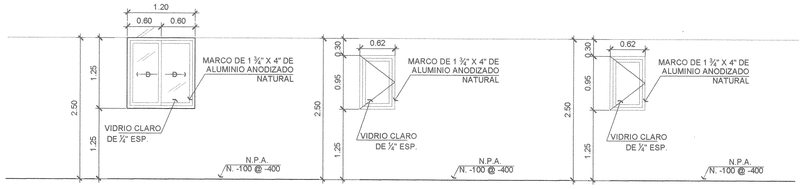

VENTANA V-E-1 ESC. 1/50

VENTANA V-E-2 ESC. 1/50

VENTANA V-E-3 ESC. 1/50

APART. 1 REC. TIPO " F " NIVEL -100 @ -400

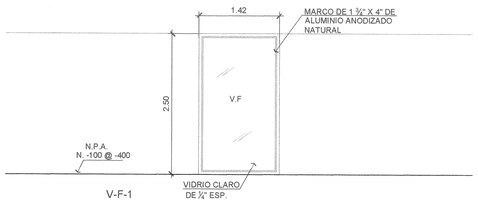

VENTANA V-F-1 ESC. 1/50

APART. 1 REC. TIPO " G " NIVEL -100 @ -400

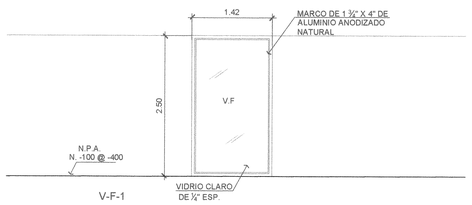

VENTANA V-G-1 ESC. 1/50

LEYENDA.
1. RETAQUEO DE BLOQUES + REPELLO LISO + PINTURA
2. BANDA DE AMARRE
3. PARDE DE 4" + REPELLO + PINTURA EN AMBAS CARAS
4. LOSA
5.VENTANA CORREDIZA
6. VENTANA ABATIBLE
7. VIDRIO FIJO

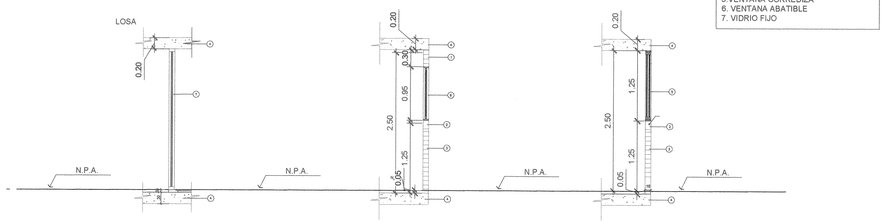

CORTE DE V.F. ESC. 1/50

CORTE DE V. DE BAÑO ESC. 1/50

CORTE DE V. DE REC. SERV. ESC. 1/50

CUADRO DE PUERTAS TORRE C

UBICACION	NIVEL	N°	VANO ANCHO	VANO ALTO	ABAT. IZQ.	ABAT. DER.	ABAT. DOBLE	CORREDIZA	CANT. X NIVEL	NUM. NIVELES	CANT. TOTAL	SUP. UNIT. VIDRIO (M2)	SUP. TOTAL VIDRIO (M2)	DESCRIPCIÓN	MARCO FERRETERIA	UBICACION	OBSERVACION
TIPO "E - F - G"	NIVEL -100 @ -400	P - E - 1	2.25	2.50				-	2	4	8	5.63	45.00	ALUMINIO + VIDRIO CLARO	MARCO DE ALUM ANOD. COLOR NATURAL	RECAMARA # 1	VER DETALLE
		P - E - 2	2.35	2.50				-	2	4	8	5.88	47.00	ALUMINIO + VIDRIO CLARO	MARCO DE ALUM ANOD. COLOR NATURAL	RECAMARA # 2	VER DETALLE
		P - E - 3	3.15	2.50				-	2	4	8	7.88	63.00	ALUMINIO + VIDRIO CLARO	MARCO DE ALUM ANOD. COLOR NATURAL	SALA/ COMEDOR	VER DETALLE
		P - F - 1	3.07	2.50				-	6	4	24	7.68	184.20	ALUMINIO + VIDRIO CLARO	MARCO DE ALUM ANOD. COLOR NATURAL	SALA/ COMEDOR	VER DETALLE
		P - F - 2	2.60	2.50				-	6	4	24	6.50	156.00	ALUMINIO + VIDRIO CLARO	MARCO DE ALUM ANOD. COLOR NATURAL	RECAMARA #1	
		P - G - 1	2.95	2.50				-	2	4	8	7.38	59.00	ALUMINIO + VIDRIO CLARO	MARCO DE ALUM ANOD. COLOR NATURAL	SALA/ COMEDOR	
		P - G - 2	1.41	2.50				-	2	4	8	3.53	28.20	ALUMINIO + VIDRIO CLARO	MARCO DE ALUM ANOD. COLOR NATURAL	SALA/ COMEDOR	
		P - G - 3	2.60	2.50				-	2	4	8	6.50	52.00	ALUMINIO + VIDRIO CLARO	MARCO DE ALUM ANOD. COLOR NATURAL	RECAMARA # 1	
		P - 1	1.00	2.15	-				5	4	20			MADERA	MARCOS NTEGRALES DE MADERA	ENTRADA PRINCIPAL	
		P - 2	1.00	2.15		-			5	4	20			MADERA	MARCOS NTEGRALES DE MADERA	ENTRADA PRINCIPAL	
		P - 3	0.80	2.15	-				15	4	60			MADERA	MARCOS NTEGRALES DE MADERA	REC. Y S.S. DE TODOS LOS MODELOS APTOS	
		P - 4	0.80	2.15		-			15	4	60			MADERA	MARCOS NTEGRALES DE MADERA	REC. Y S.S. DE TODOS LOS MODELOS APTOS.	
		P - 11	1.00	2.15	-				2	4	8			PUERTA PRESURIZADA	AISLAMIENTO TERMICO RESISTENTE AL FUEGO	ESCALERA DE EMERGENCIAS	
	NIVEL -400	P - 35	1.00	2.15	-				4	1	4			HIERRO	MARCOS NTEGRALES DE METAL	BALCONES AL AREA SOCIAL DE APTOS. NIVEL -400	
		P - 36	1.00	2.15		-			5	1	5			HIERRO	MARCOS NTEGRALES DE METAL	BALCONES AL AREA SOCIAL DE APTOS. NIVEL -400	

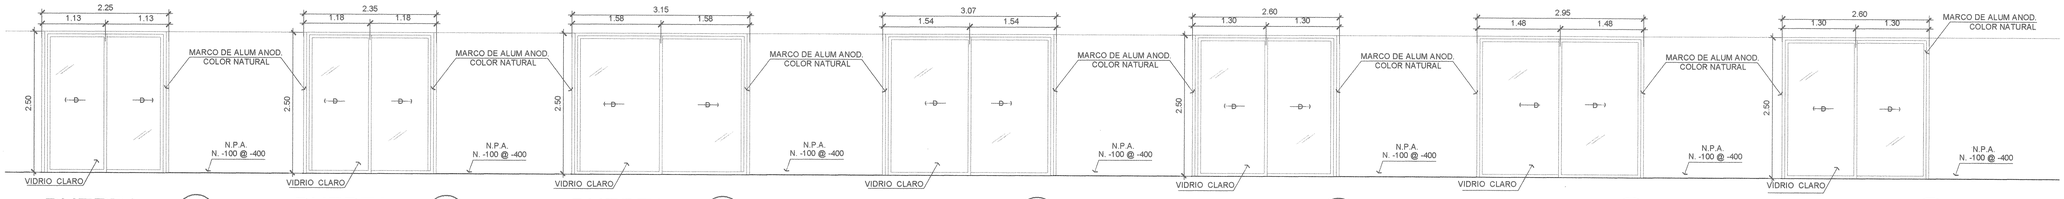

PUERTA P-E-1 ESC. 1/20

PUERTA P-E-2 ESC. 1/20

PUERTA P-E-3 ESC. 1/20

PUERTA P-F-1 ESC. 1/20

PUERTA P-F-2 ESC. 1/20

PUERTA P-G-1 ESC. 1/20

PUERTA P-G-2 ESC. 1/20

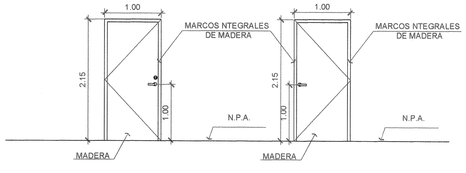

PUERTA P-1 ESC. 1/50

PUERTA P-2 ESC. 1/50

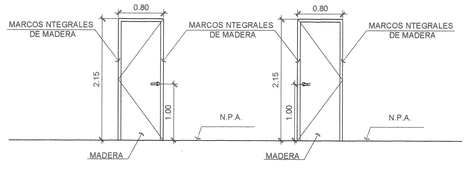

PUERTA P-3 ESC. 1/50

PUERTA P-4 ESC. 1/50

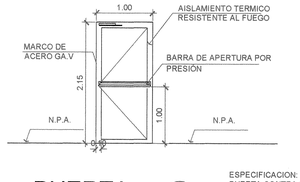

PUERTA P-11 ESC. 1/50

ESPECIFICACION:
PUERTA CONTRA INCENDIO DE METAL DE CON ESTRUCTURA METALICA CAL. 18
MARCO DE 1-1/2 X 5 CAL. 15 CON 3 BISAGRAS DE 4" RESISTENTE AL FUEGO

ESPECIFICACION:

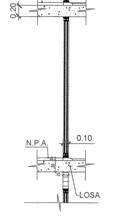

CORTE DE PUERTAS APTO ESC. 1/50

CORTE GENERAL P. DE MADERA

CORTE GENERAL P. DE PERSIANAS

ESPECIFICACION:
CON RELLENO DE POLIESTIRENO ACUSTICO LAMINADAS CON CHAPAS DDE MDF PREPINTADAS EN COLOR A ESCOGER POR EL ARQ. Y/O PROMOTOR.
EL DISEÑO Y EL COLOR SERA ESCOGIDO POR EL ARQ. Y/O PROMOTOR DEL PROYECTO.

LEYENDA.
1. LAMINIAS DECORATIVAS CON RELLENO DE POLIESTIRENO ACABADO EN ESCOGER POR EL PROMOTOR O ARQ.
2. MANIJA
3. BASTIDOR DE MADERA
4. MARCO PRESURIZADO CON EMPAQUETADURA RESISTENTE AL FUEGO
5.PERSIANERA DE ALUMINIO
6. MARCO DE ACERO GALVANIZADO.

INGENIERIA MUNICIPAL
DISTRITO DE SAN CARLOS
APROBADO
FECHA: 22/8/11

Cuerpo de Bomb.
OFICINA DE SEGURIDAD
La Chorrera
La Chorrera, 4 de agosto de 2010
Resolución No. 2010 Plano No. M-1-08
Se aprueba el registro de este plano por llenar las condiciones requeridas
Jefe de la Oficina de Seguridad

FELIPE GONZALEZ LINCK
ARQUITECTO
EGRESADO No. 71-1-188
LEY 15 (DEL 26 DE ENERO DE 1959)
JUNTA TECNICA DE INGENIERIA Y ARQUITECTURA

FELIPE GONZÁLEZ LINCK
ARQUITECTO
Tel: -- 66771610 -- Fax 392-2457 | 64035839

DISEÑO ARQUITECTÓNICO	Arq. Vicente Cortes Arq. Igor Cortes
DESARROLLO	Arq. Igor Cortes Arq. Ilem Segismond Arq. Nancy Urriola
PROYECTO ESTRUCTURAL	Ing. Ricauter Bowen
PROYECTO ELÉCTRICO	Ing. Edgar Naranjo
PROYECTO DE PLOMERÍA	Ing. Gilberto Ayala

PROYECTO
Residencial El Palmar

UBICACIÓN
COMUNIDAD DE "EL PALMAR"
DITTO. DE SAN CARLOS - CORREGIMIENTO DE SAN CARLOS
PANAMÁ

SOCIEDAD PROMOTORA
Inversiones Decuria, S.A.
Representante legal: IGOR CORTES
Número de cédula o pasaporte: 8C054493

INGENIERÍA MUNICIPAL

PLANO
- DETALLES DE PUERTAS Y VENTANAS TORRE C

ARCHIVO .DWG	PUERTAS
FECHA	30/08/2010
FECHA MODIFICACIÓN	DD/MM/AAAA

ARQUITECTURA | HOJA: 59 | DE: 65

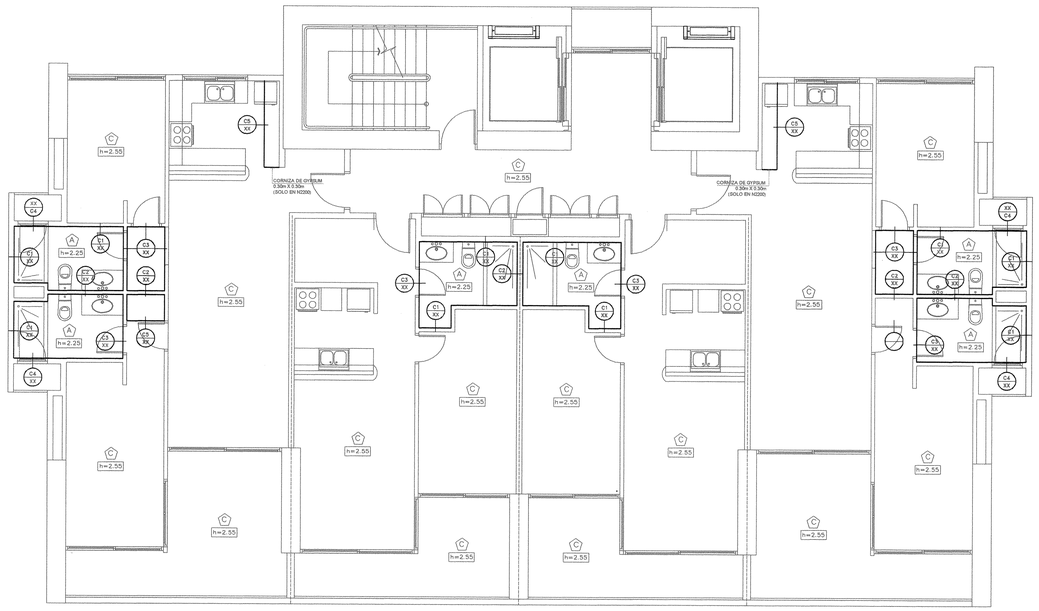

PLANTA DE CIELO RASO NIVEL 100 @ 2200

ESCALA 1:75

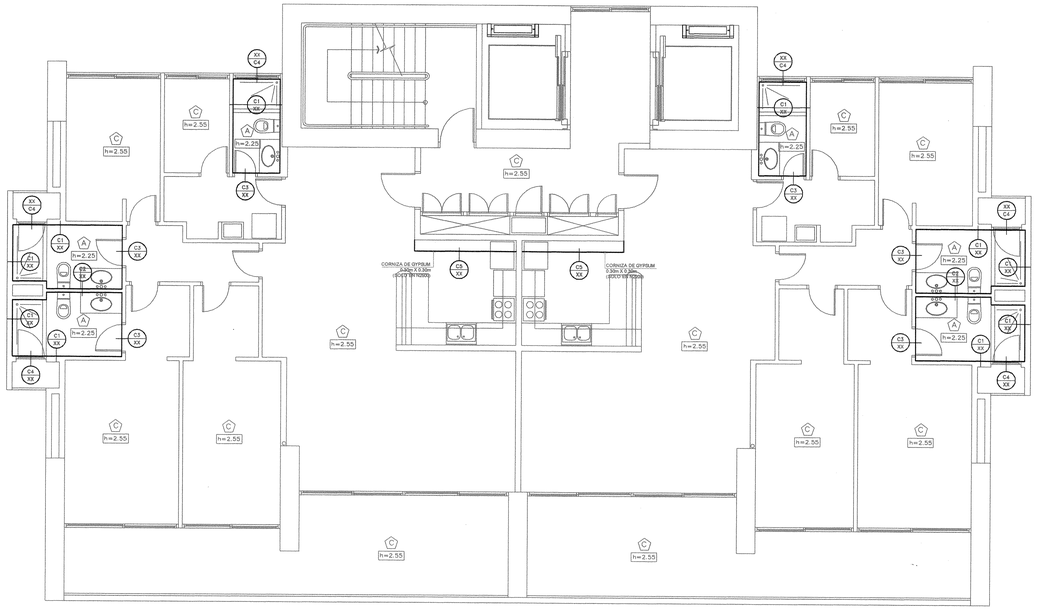

PLANTA DE CIELO RASO NIVEL 2300 @ 2500

ESCALA 1:75

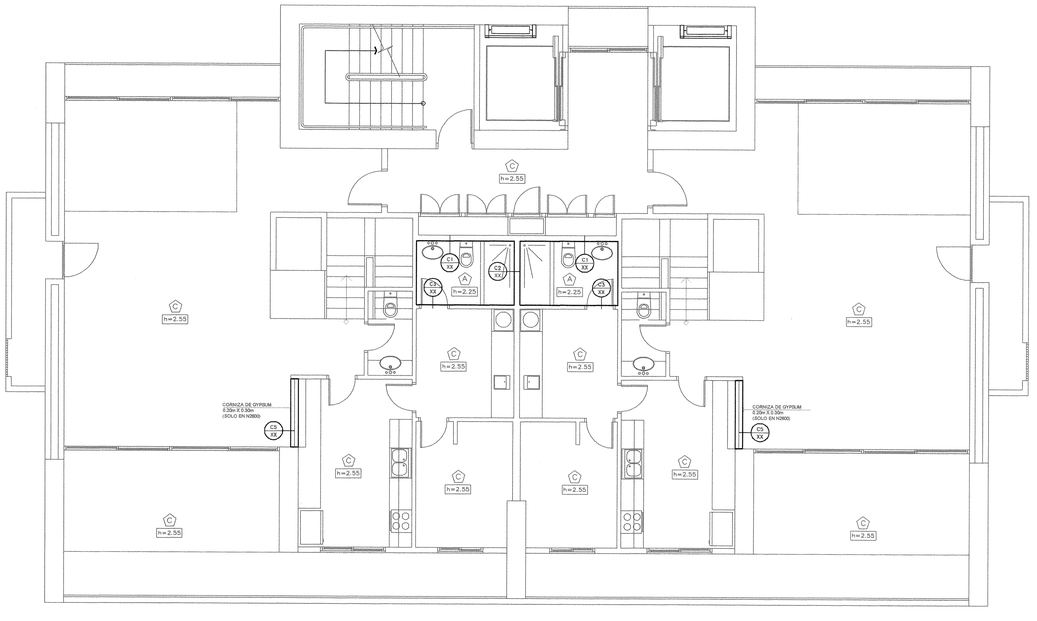

PLANTA DE CIELO RASO NIVEL 2600

ESCALA 1:75

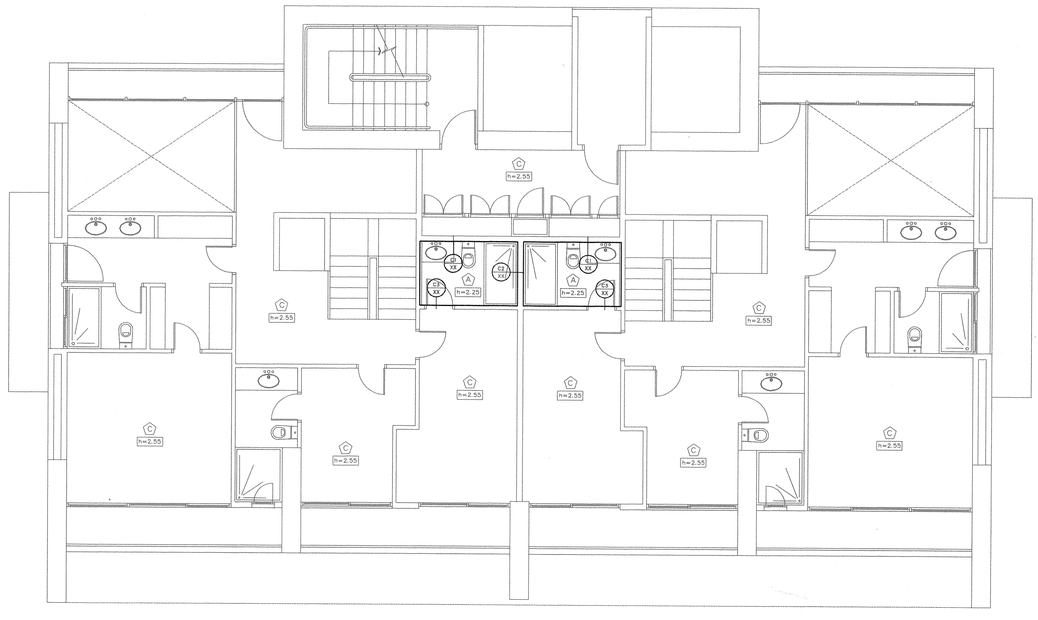

PLANTA DE CIELO RASO NIVEL 2700

ESCALA 1:75

INGENIERIA MUNICIPAL
DISTRITO DE SAN CARLOS
APROBADO
INGENIERO MUNICIPAL
FECHA

La Chorrera, ... 2011
Resolución No. ... Plano No. ...
Se aprueba el registro de este plano por llenar las condiciones requeridas.

Cuerpo de Bomberos
OFICINA DE SEGURIDAD
La Chorrera
Jefe de la Oficina de Seguridad

FELIPE GONZALEZ LINCK
ARQUITECTO
LICENCIA No. 7...-...-92
LEY 15 DEL 26 DE ENERO DE 1959
JUNTA TECNICA DE INGENIERIA Y ARQUITECTURA

FELIFE GONZÁLEZ LINCK
ARQUITECTO
Tel. – 66771610 – Fax 392-2457 | 64035830

DISEÑO ARQUITECTÓNICO	Arq. Vicente Cortes Arq. Igor Cortes
DESARROLLO	Arq. Igor Cortes Arq. Ilem Segismond Arq. Nancy Urriola
PROYECTO ESTRUCTURAL	Ing. Ricauter Bowen
PROYECTO ELÉCTRICO	Ing. Edgar Naranjo
PROYECTO DE PLOMERÍA	Ing. Gilberto Ayala

PROYECTO

Residencial El Palmar

UBICACIÓN

COMUNIDAD DE 'EL PALMAR'
DTTO. DE SAN CARLOS - CORREGIMIENTO DE SAN CARLOS
PANAMÁ

SOCIEDAD PROMOTORA

Inversiones Decuria, S.A.

Representante legal: IGOR CORTES
Número de cédula o pasaporte: 8C054493

INGENIERÍA MUNICIPAL

PLANO

- PLANTA DE CIELO RASO
NIVEL 100 @ 2700
ESCALA 1:75

ARCHIVO .DWG	CIELO RASO
FECHA	30/08/2010
FECHA MODIFICACIÓN	DD/MM/AAAA

ARQUITECTURA | HOJA: 60 | DE: 65

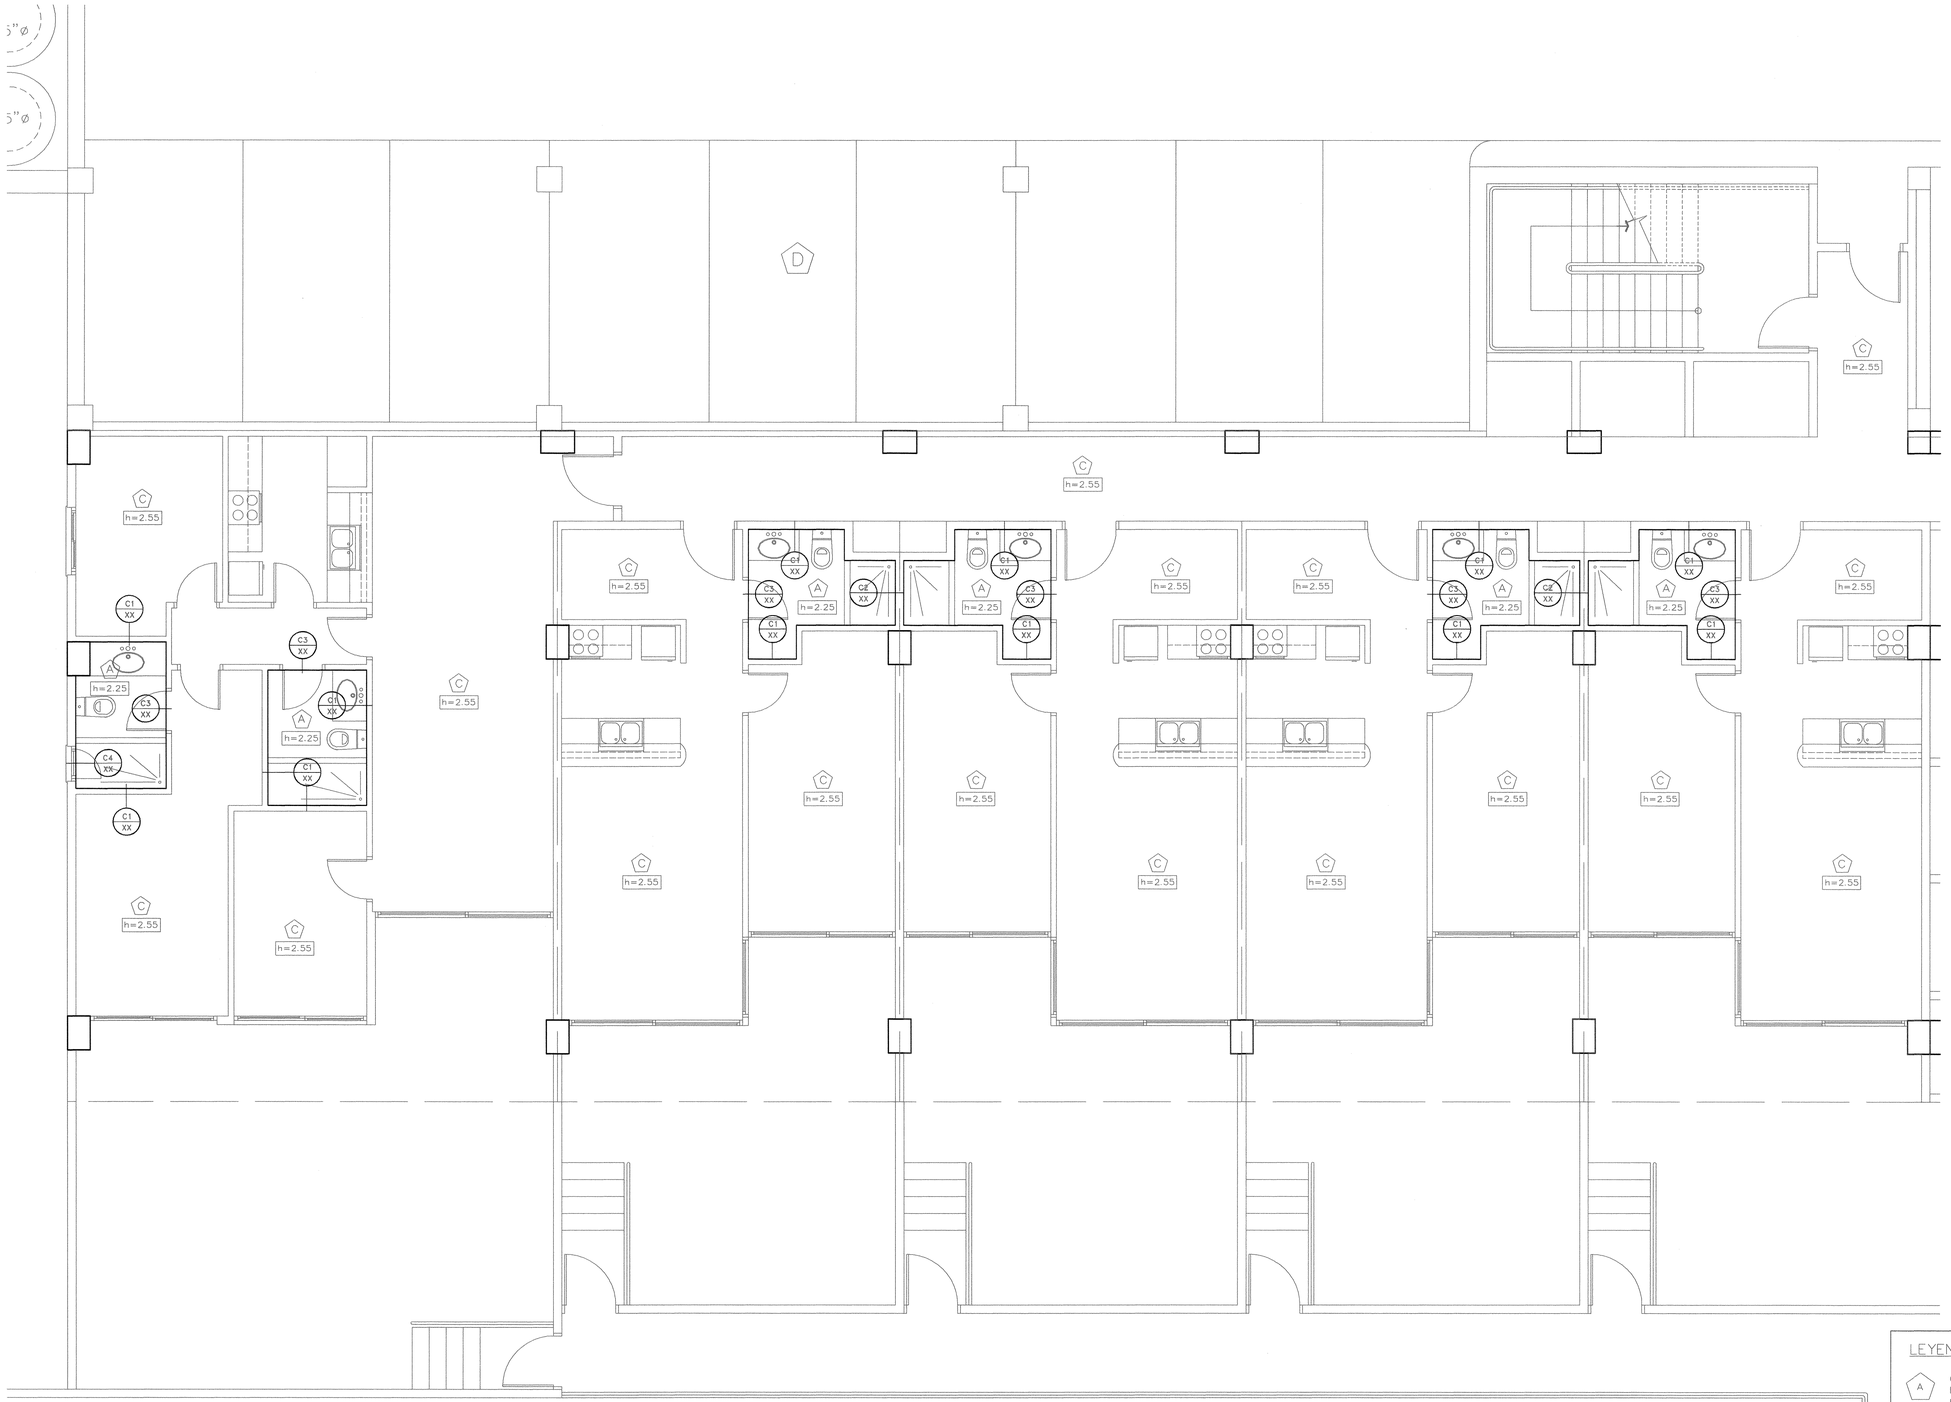

PLANTA DE CIELO RASO NIVEL -400

AMPLIACION 'A' (IZQUIERDA)

ESCALA 1:50

LEYENDA DE CIELO RASO

- A — CIELO RASO DE GYPSUM BOARD DE 1/2" ESP. PASTEADA Y PINTADA EN ESTRUCT. DE METAL
- B — CIELO RASO DE GYPSUM BOARD DE 1/2" ESP. PARA EXTERIORES PASTEADA Y PINTADA EN ESTRUCT. DE METAL
- C — LOSA POSTENSADA VISTA PASTEADA Y PINTADA
- D — LOSA POSTENSADA CONCRETO VISTO

h= 2.25 INDICA ALTURA DE C./RASO DEL NIVEL SUP. DE LOSA

INGENIERIA MUNICIPAL
DISTRITO DE SAN CARLOS
APROBADO
INGENIERO MUNICIPAL
FECHA 22/6/11

Cuerpo de Bomberos
OFICINA DE SEGURIDAD
La Chorrera
La Chorrera, Plano No. 1-2-10
Resolución No. 2010
Se aprueba el registro de este plano por llenar las condiciones requeridas.
Jefe de la Oficina de Seguridad

FELIPE GONZALEZ LINCK
ARQUITECTO
LICENCIA No. 1-1-185
LEY 15 DEL 23 DE ENERO DE 1959
JUNTA TECNICA DE INGENIERIA Y ARQUITECTURA

FELIFE GONZÁLEZ LINCK
ARQUITECTO
Tel. - 66771610 - Fax 392-2457 | 64035839

DISEÑO ARQUITECTÓNICO	Arq. Vicente Cortes Arq. Igor Cortes
DESARROLLO	Arq. Igor Cortes Arq. Ilem Segismond Arq. Nancy Urriola
PROYECTO ESTRUCTURAL	Ing. Ricauter Bowen
PROYECTO ELÉCTRICO	Ing. Edgar Naranjo
PROYECTO DE PLOMERÍA	Ing. Gilberto Ayala

PROYECTO

Residencial El Palmar

UBICACIÓN

COMUNIDAD DE 'EL PALMAR'
DTTO. DE SAN CARLOS - CORREGIMIENTO DE SAN CARLOS
PANAMÁ

SOCIEDAD PROMOTORA

Inversiones Decuria, S.A.

Representante legal: IGOR CORTES
Número de cédula o pasaporte: BC054483

INGENIERÍA MUNICIPAL

PLANO

- PLANTA DE CIELO RASO
NIVEL -400 - AMPLIACION A (IZQUIERDO)
ESCALA 1:50

ARCHIVO .DWG	CIELO RASO
FECHA	30/08/2010
FECHA MODIFICACIÓN	DD/MM/AAAA

ARQUITECTURA | HOJA: 61 | DE: 65

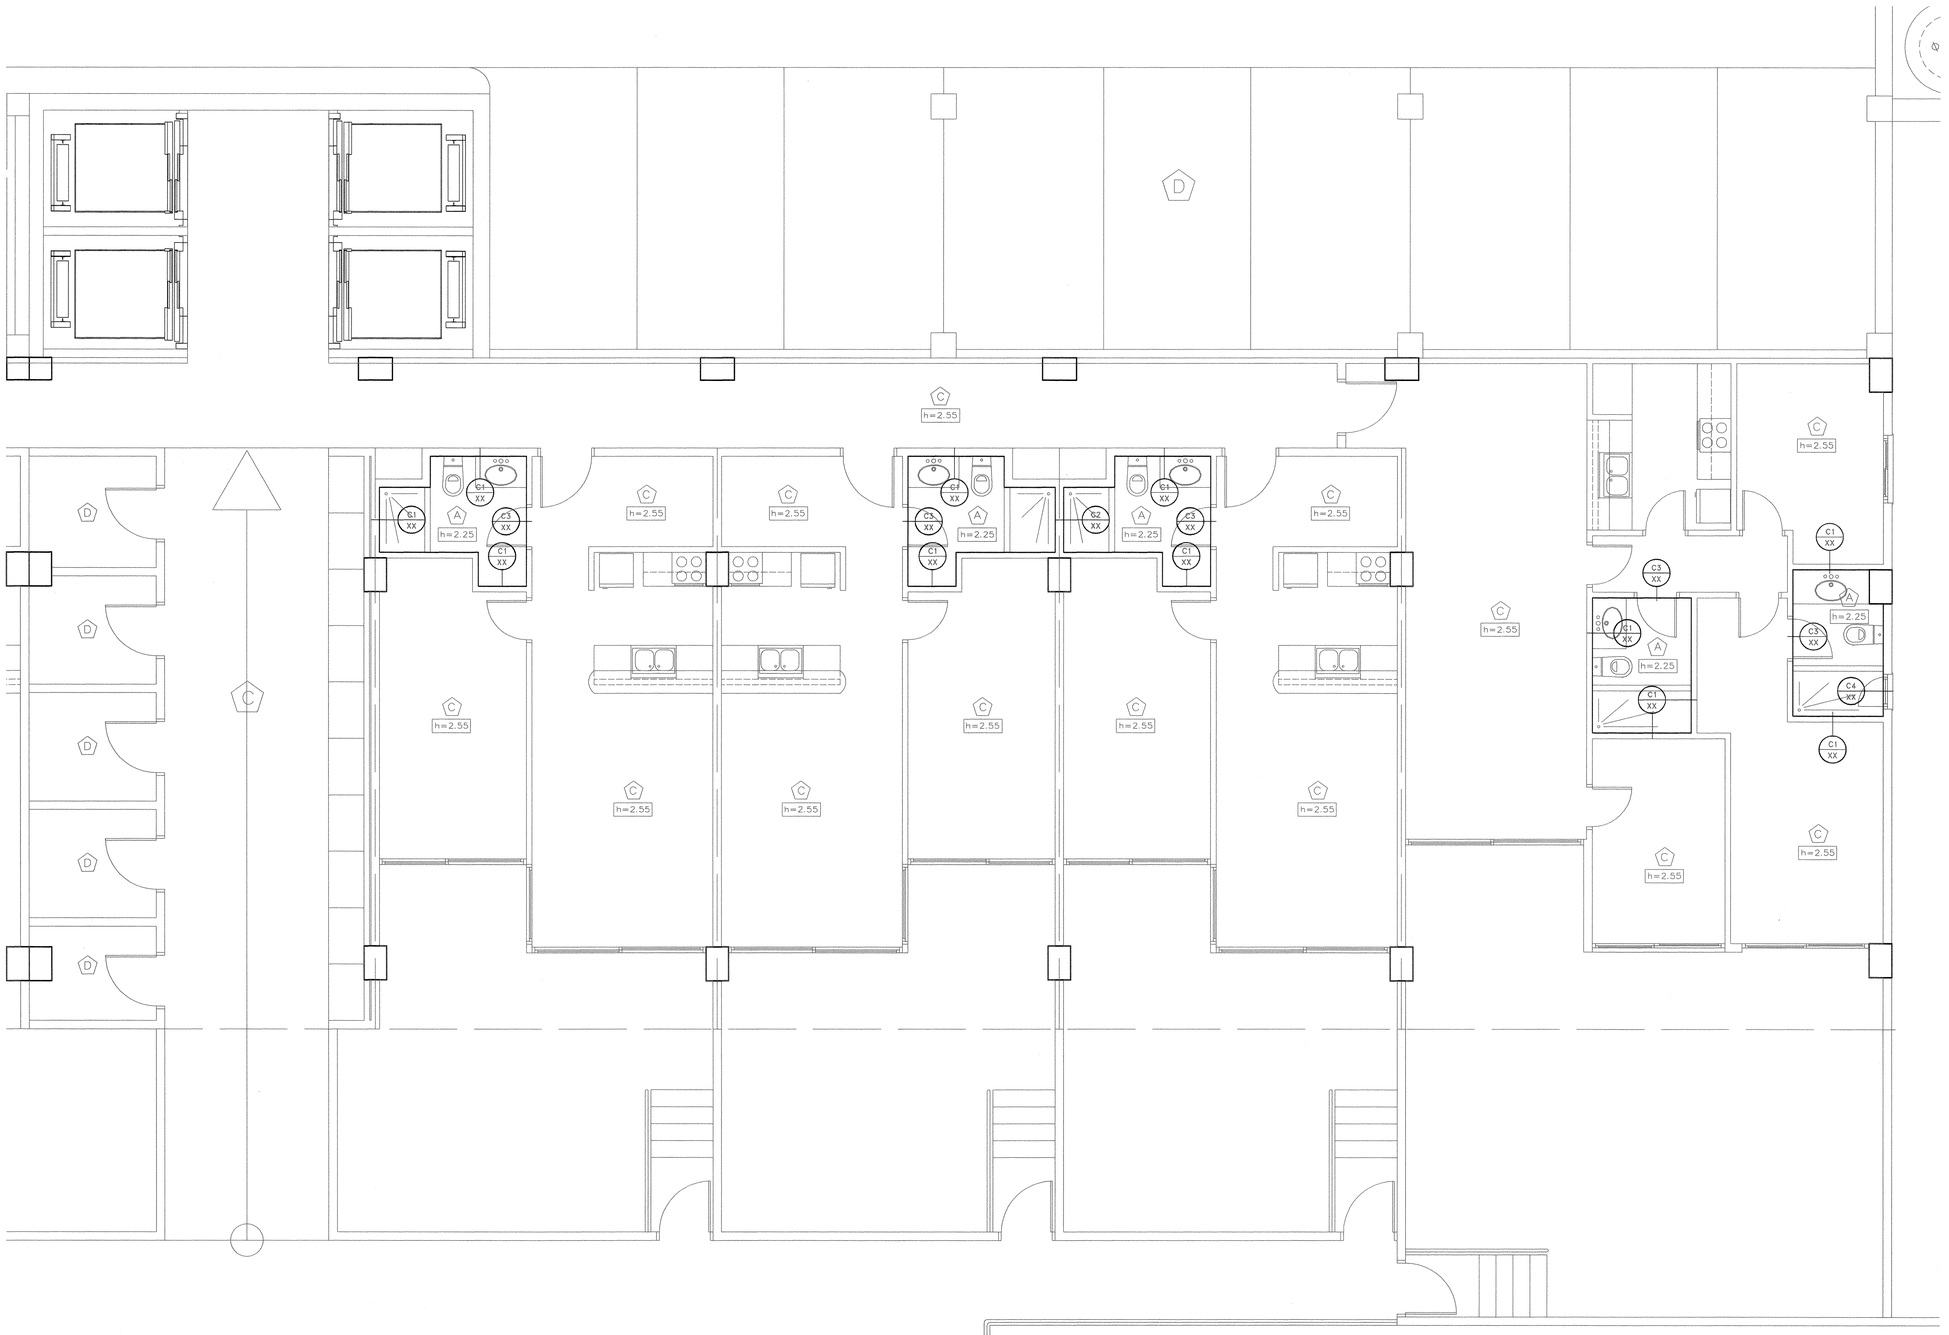

PLANTA DE CIELO RASO NIVEL -400

AMPLIACION 'B' (DERECHA)

ESCALA 1:50

LEYENDA DE CIELO RASO

- A — CIELO RASO DE GYPSUM BOARD DE 1/2" ESP. PASTEADA Y PINTADA EN ESTRUCT. DE METAL
- B — CIELO RASO DE GYPSUM BOARD DE 1/2" ESP. PARA EXTERIORES PASTEADA Y PINTADA EN ESTRUCT. DE METAL
- C — LOSA POSTENSADA VISTA PASTEADA Y PINTADA
- D — Llosa POSTENSADA CONCRETO VISTO

h= 2.25 INDICA ALTURA DE C./RASO DEL NIVEL SUP. DE LOSA

INGENIERIA MUNICIPAL
DISTRITO DE SAN CARLOS
APROBADO
INGENIERO MUNICIPAL
FECHA 22/8/11

Cuerpo de Bomberos
OFICINA DE SEGURIDAD
La Chorrera
La Chorrera, 11 de agosto de 2011
Resolución No. 3916 Plano No. 11-18
Se aprueba el requisito de gas planta por llenar las condiciones requeridas.
Jef. de la Oficina de Seguridad

FELIPE GONZALEZ LINCK
ARQUITECTO
LICENCIA No. 4,135
LEY 15 DEL 26 DE ENERO DE 1959
JUNTA TECNICA DE INGENIERIA Y ARQUITECTURA

FELIFE GONZÁLEZ LINCK
ARQUITECTO
Tel. -- 66771610 -- Fax 392-2457 | 64035839

DISEÑO ARQUITECTÓNICO	Arq. Vicente Cortes Arq. Igor Cortes
DESARROLLO	Arq. Igor Cortes Arq. Ilem Segismond Arq. Nancy Urriola
PROYECTO ESTRUCTURAL	Ing. Ricauter Bowen
PROYECTO ELÉCTRICO	Ing. Edgar Naranjo
PROYECTO DE PLOMERÍA	Ing. Gilberto Ayala

PROYECTO

Residencial El Palmar

UBICACIÓN

COMUNIDAD DE 'EL PALMAR'
DTTO. DE SAN CARLOS - CORREGIMIENTO DE SAN CARLOS
PANAMÁ

SOCIEDAD PROMOTORA

Inversiones Decuria, S.A.
Representante legal: IGOR CORTES
Número de cédula o pasaporte: BC054493

INGENIERÍA MUNICIPAL

PLANO

- PLANTA DE CIELO RASO
NIVEL -400 - AMPLIACION B (DERECHO)
ESCALA 1:50

ARCHIVO .DWG	CIELO RASO
FECHA	30/08/2010
FECHA MODIFICACIÓN	DD/MM/AAAA

ARQUITECTURA | HOJA: 62 | DE: 65

PLANTA DE CIELO RASO NIVEL -100 @-300

AMPLIACION 'A' (IZQUIERDA)

ESCALA 1:50

NOTA:
COLOCAR CIELO RASO DE GYPSUM SEGUN LO INDICADO, A EXCEPCION DEL NIVEL -100

LEYENDA DE CIELO RASO

- A — CIELO RASO DE GYPSUM BOARD DE 1/2" ESP. PASTEADA Y PINTADA EN ESTRUCT. DE METAL
- B — CIELO RASO DE GYPSUM BOARD DE 1/2" ESP. PARA EXTERIORES PASTEADA Y PINTADA EN ESTRUCT. DE METAL
- C — LOSA POSTENSADA VISTA PASTEADA Y PINTADA
- D — LOSA POSTENSADA CONCRETO VISTO

h= 2.25 INDICA ALTURA DE C./RASO DEL NIVEL SUP. DE LOSA

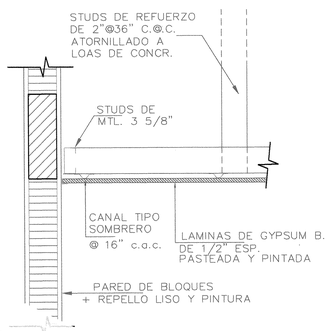

DETALLE C1/XX ESCALA 1:10

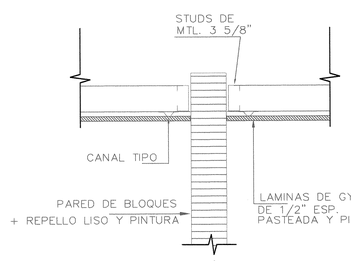

DETALLE C2/XX ESCALA 1:10

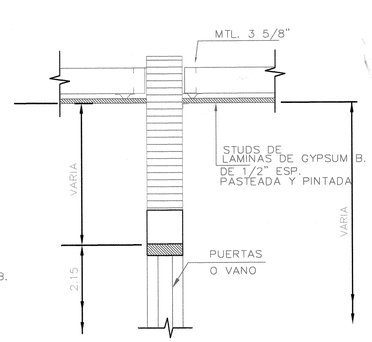

DETALLE C3/XX ESCALA 1:10

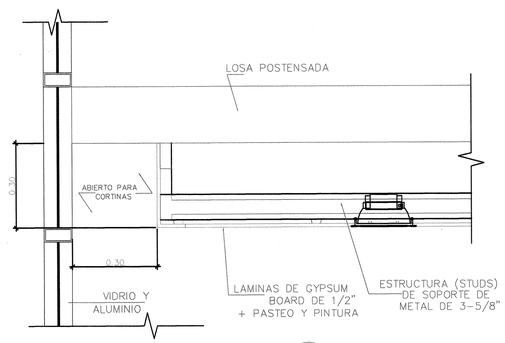

DETALLE C4/XX ESCALA 1:10

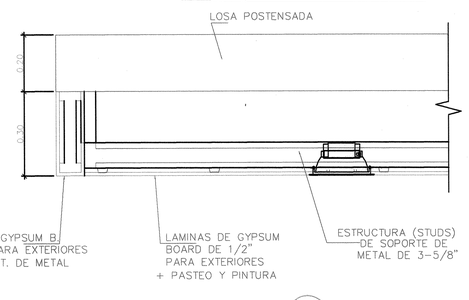

DETALLE C5/XX ESCALA 1:10

INGENIERIA MUNICIPAL
DISTRITO DE SAN CARLOS
APROBADO
INGENIERO MUNICIPAL
FECHA 22/8/11

Cuerpo de Bomberos
OFICINA DE SEGURIDAD
La Chorrera, 11 de Agosto de 2011
Resolución No. 0178 Plano No. 63 de 65
Se aprueba el diseño por llenar las condiciones requerid...
Jefe de la Oficina de Seguridad

FELIPE GONZALEZ LINCK
ARQUITECTO
LICENCIA No. 87-1-108
LEY 15 DEL 26 DE ENERO DE 1959
JUNTA TECNICA DE INGENIERIA Y ARQUITECTURA

FELIFE GONZÁLEZ LINCK
ARQUITECTO
Tel. – 66771610 – Fax 392-2457 | 64035839

DISEÑO ARQUITECTÓNICO	Arq. Vicente Cortes Arq. Igor Cortes
DESARROLLO	Arq. Igor Cortes Arq. Ilem Segismond Arq. Nancy Urriola
PROYECTO ESTRUCTURAL	Ing. Ricauter Bowen
PROYECTO ELÉCTRICO	Ing. Edgar Naranjo
PROYECTO DE PLOMERÍA	Ing. Gilberto Ayala

PROYECTO
Residencial El Palmar

UBICACIÓN
COMUNIDAD DE 'EL PALMAR'
DTTO. DE SAN CARLOS - CORREGIMIENTO DE SAN CARLOS
PANAMÁ

SOCIEDAD PROMOTORA
Inversiones Decuria, S.A.
Representante legal: IGOR CORTES
Número de cédula o pasaporte: 8CO54483

INGENIERÍA MUNICIPAL

PLANO
- PLANTA Y DETALLES DE CIELO RASO
NIVEL -100@-300
AMPLIACION A (IZQUIERDO)
ESCALA 1:50

ARCHIVO .DWG	CIELO RASO
FECHA	30/08/2010
FECHA MODIFICACIÓN	DD/MM/AAAA

ARQUITECTURA | HOJA: 63 | DE: 65

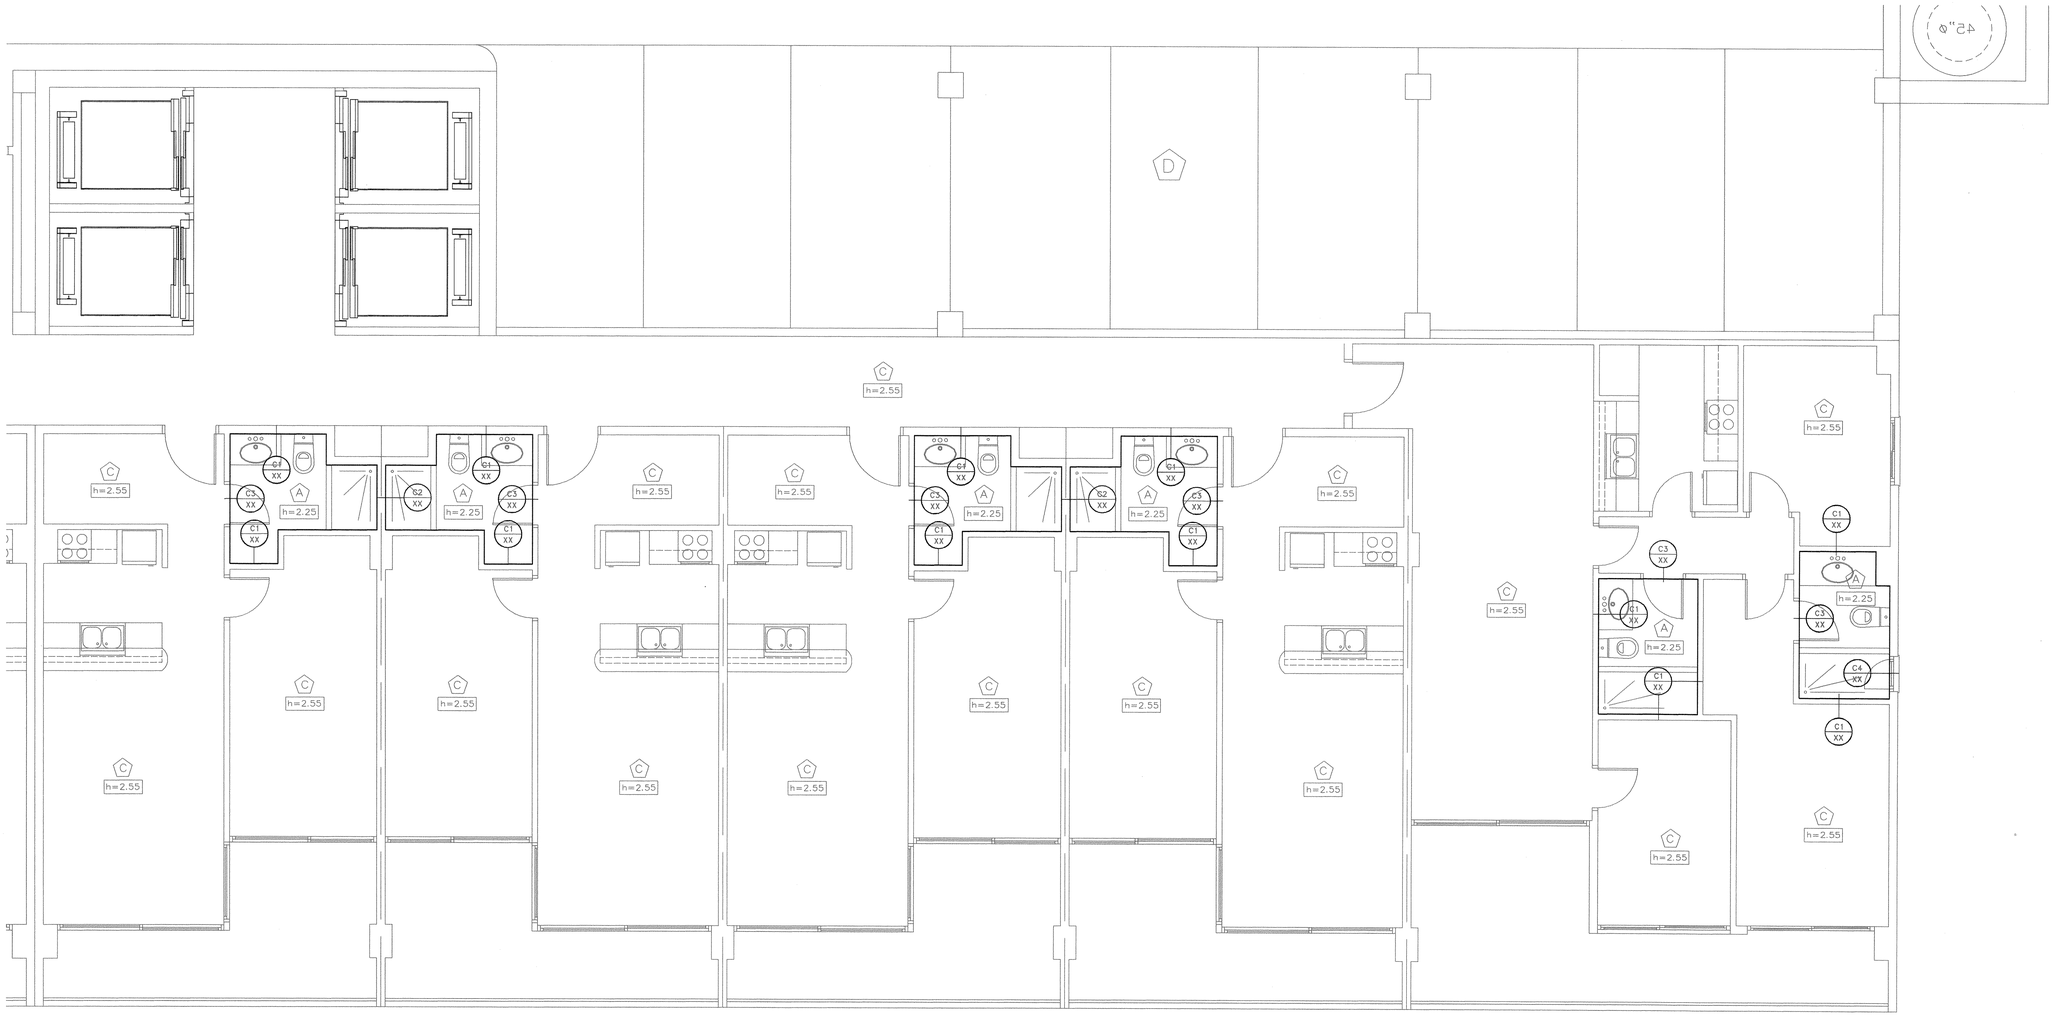

PLANTA DE CIELO RASO NIVEL -100 @-300

AMPLIACION 'B' (DERECHA)

ESCALA 1:50

NOTA:
COLOCAR CIELO RASO DE GYPSUM SEGUN LO INDICADO, A EXCEPCION DEL NIVEL -100

LEYENDA DE CIELO RASO

- A — CIELO RASO DE GYPSUM BOARD DE 1/2" ESP. PASTEADA Y PINTADA EN ESTRUCT. DE METAL
- B — CIELO RASO DE GYPSUM BOARD DE 1/2" ESP. PARA EXTERIORES PASTEADA Y PINTADA EN ESTRUCT. DE METAL
- C — LOSA POSTENSADA VISTA PASTEADA Y PINTADA
- D — LOSA POSTENSADA CONCRETO VISTO
- h= 2.25 — INDICA ALTURA DE C./RASO DEL NIVEL SUP. DE Llosa

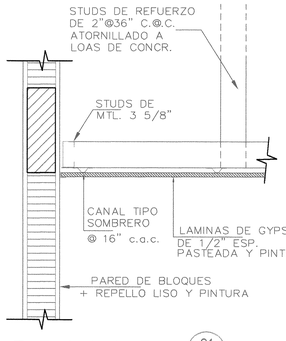

DETALLE C1 XX ESCALA 1:10

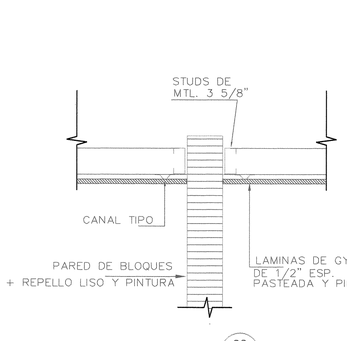

DETALLE C2 XX ESCALA 1:10

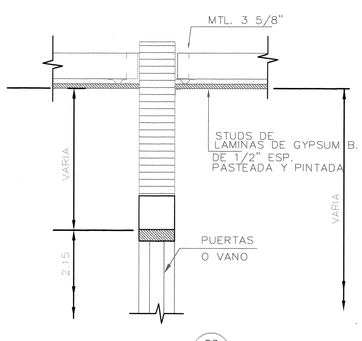

DETALLE C3 XX ESCALA 1:10

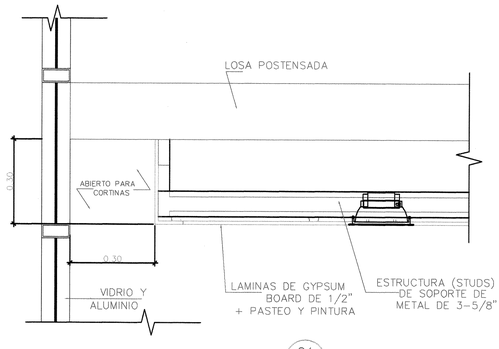

DETALLE C4 XX ESCALA 1:10

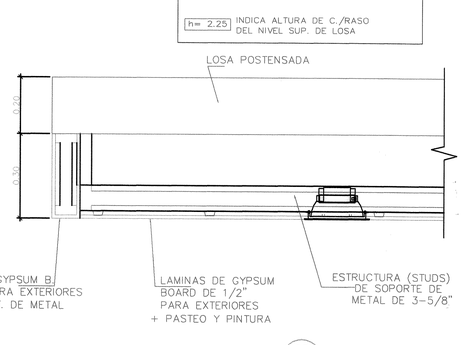

DETALLE C5 XX ESCALA 1:10

INGENIERIA MUNICIPAL
DISTRITO DE SAN CARLOS
APROBADO
INGENIERO MUNICIPAL
FECHA 22/9/11

Cuerpo de Bomberos
OFICINA DE SEGURIDAD
La Chorrera
La Chorrera, 11 de Agosto de 2011
Resolución No. 318 Folio No. 168
Se aprueba el registro de esta planta por llenar las condiciones requerida.
Jefe de la Oficina de Seguridad

FELIPE GONZALEZ LINCK
ARQUITECTO
LICENCIA No. 7771-108
LEY 15 DEL 26 DE ENERO DE 1959
JUNTA TECNICA DE INGENIERIA Y ARQUITECTURA

FELIFE GONZÁLEZ LINCK
ARQUITECTO
Tel. -- 66771610 -- Fax 392-2457 | 64035839

DISEÑO ARQUITECTÓNICO	Arq. Vicente Cortes Arq. Igor Cortes
DESARROLLO	Arq. Igor Cortes Arq. Ilem Segismond Arq. Nancy Urriola
PROYECTO ESTRUCTURAL	Ing. Ricauter Bowen
PROYECTO ELÉCTRICO	Ing. Edgar Naranjo
PROYECTO DE PLOMERÍA	Ing. Gilberto Ayala

PROYECTO
Residencial El Palmar

UBICACIÓN
COMUNIDAD DE 'EL PALMAR'
DTTO. DE SAN CARLOS - CORREGIMIENTO DE SAN CARLOS
PANAMÁ

SOCIEDAD PROMOTORA
Inversiones Decuria, S.A.
Representante legal: IGOR CORTES
Número de cédula o pasaporte: 8C054493

INGENIERÍA MUNICIPAL

PLANO
- PLANTA Y DETALLES DE CIELO RASO
NIVEL -100@-300
AMPLIACION B (DERECHO)
ESCALA 1:50

ARCHIVO .DWG	CIELO RASO
FECHA	30/08/2010
FECHA MODIFICACIÓN	DD/MM/AAAA

ARQUITECTURA | HOJA: 64 | DE: 65

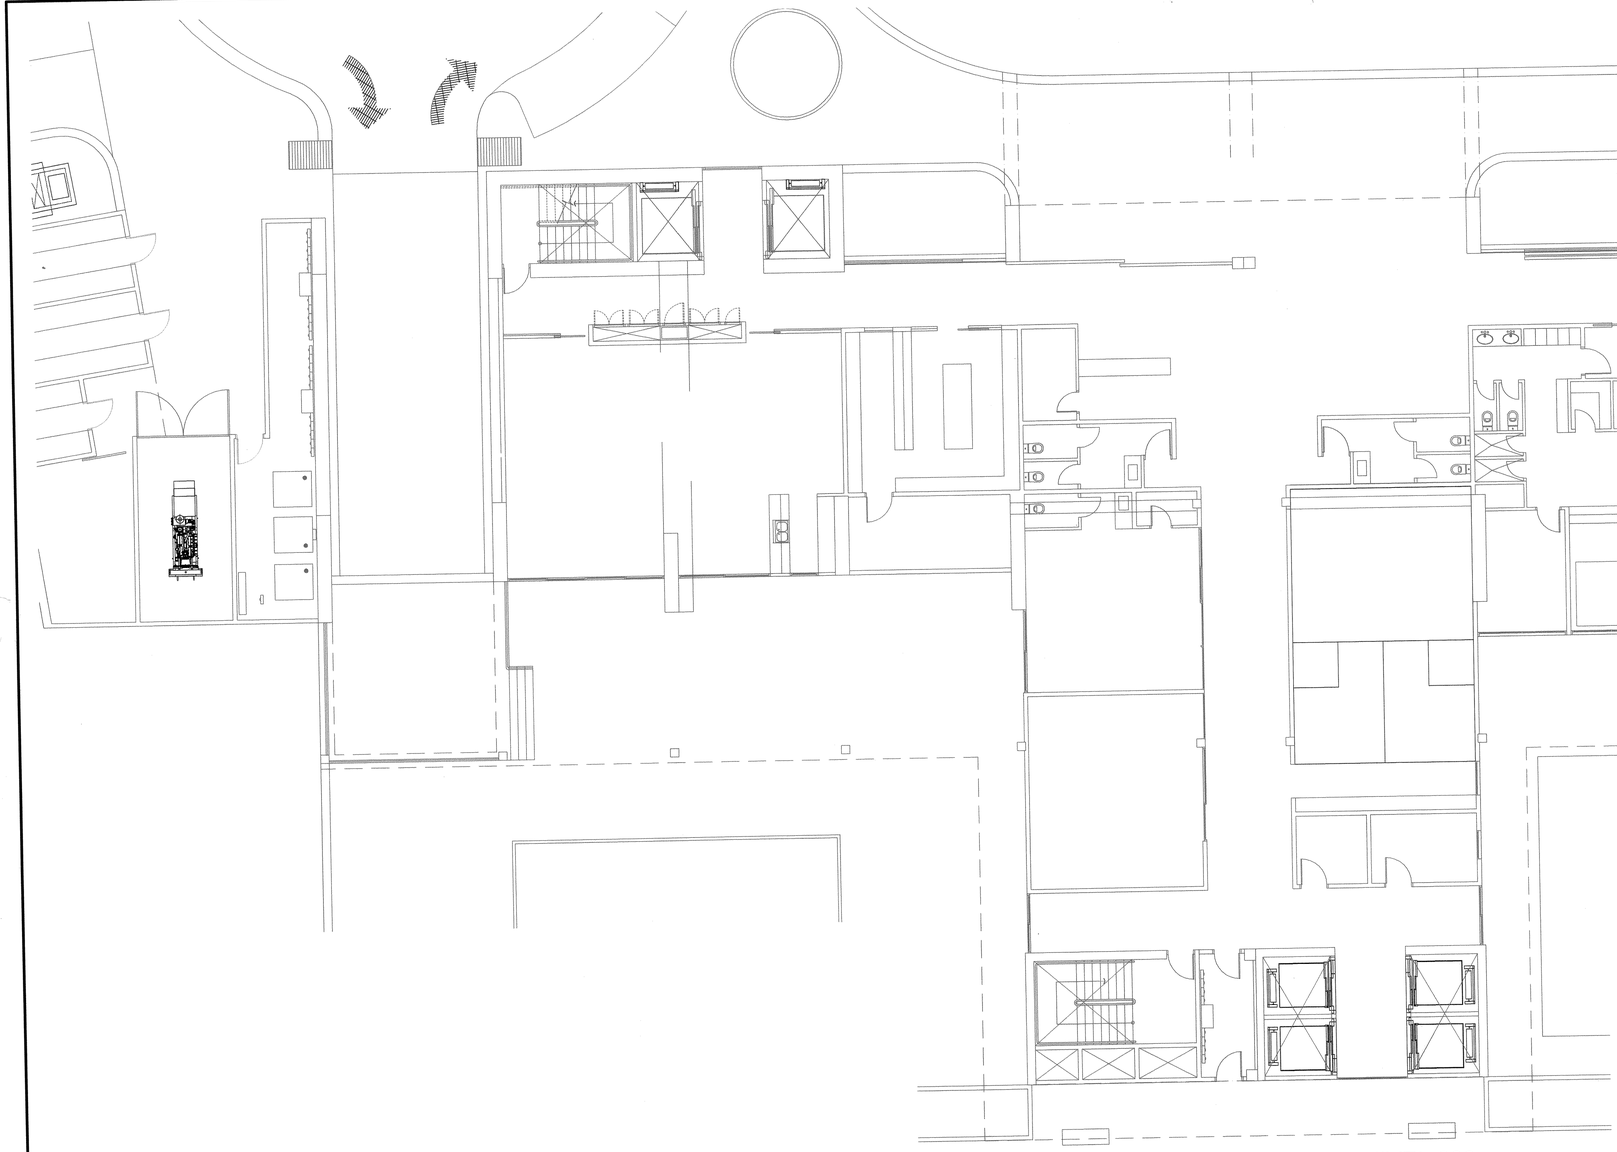

PLANTA DE CIELO RASO NIVEL 000

LOBBY - PLANTA BAJA ESCALA 1:100

LEYENDA DE CIELO RASO

- A — CIELO RASO DE GYPSUM BOARD DE 1/2" ESP. PASTEADA Y PINTADA EN ESTRUCT. DE METAL
- B — CIELO RASO DE GYPSUM BOARD DE 1/2" ESP. PARA EXTERIORES PASTEADA Y PINTADA EN ESTRUCT. DE METAL
- C — LOSA POSTENSADA VISTA PASTEADA Y PINTADA
- D — LOSA POSTENSADA CONCRETO VISTO
- h= 2.25 — INDICA ALTURA DE C./RASO DEL NIVEL SUP. DE Llosa

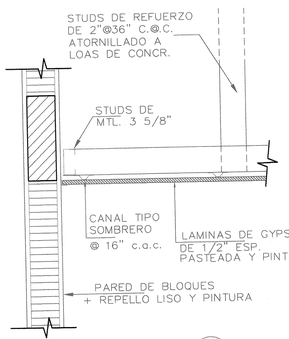

DETALLE C1/xx ESCALA 1:10

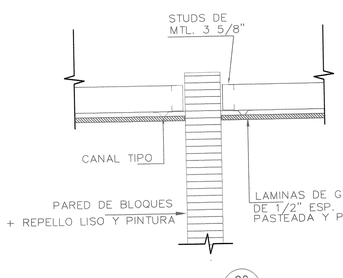

DETALLE C2/xx ESCALA 1:10

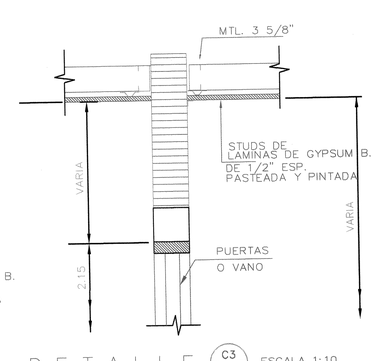

DETALLE C3/xx ESCALA 1:10

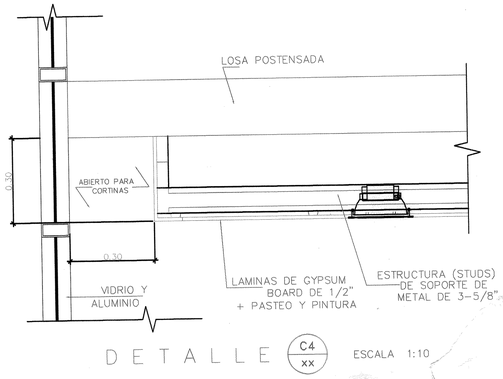

DETALLE C4/xx ESCALA 1:10

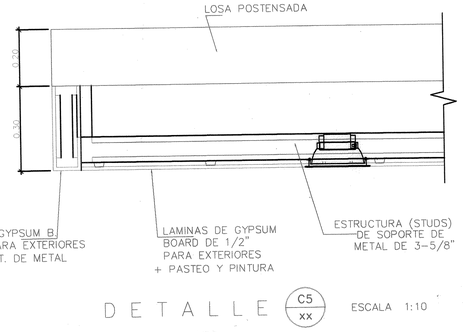

DETALLE C5/xx ESCALA 1:10

INGENIERIA MUNICIPAL
DISTRITO DE SAN CARLOS
APROBADO
INGENIERO MUNISIPAL
FECHA 22/8/11

Cuerpo de Bomberos
OFICINA DE SEGURIDAD
La Chorrera, 11 de agosto de 2011
Resolución No. 3496 Plano No. 1165
Se remite el presente plano por llenar las condiciones requeridas.
Jefe de la Oficina de Seguridad

FELIPE GONZÁLEZ LINCK
ARQUITECTO
LICENCIA No. 97-188
LEY 15 DEL 26 DE ENERO DE 1959
JUNTA TECNICA DE INGENIERIA Y ARQUITECTURA

FELIFE GONZÁLEZ LINCK
ARQUITECTO
Tel. -- 66771610 -- Fax 392-2457 | 64035839

DISEÑO ARQUITECTÓNICO	Arq. Vicente Cortes Arq. Igor Cortes
DESARROLLO	Arq. Igor Cortes Arq. Ilem Segismond Arq. Nancy Urriola
PROYECTO ESTRUCTURAL	Ing. Ricauter Bowen
PROYECTO ELÉCTRICO	Ing. Edgar Naranjo
PROYECTO DE PLOMERÍA	Ing. Gilberto Ayala

PROYECTO

Residencial El Palmar

UBICACIÓN

COMUNIDAD DE "EL PALMAR"
DTTO. DE SAN CARLOS - CORREGIMIENTO DE SAN CARLOS
PANAMÁ

SOCIEDAD PROMOTORA

Inversiones Decuria, S.A.

Representante legal: IGOR CORTES
Número de cédula o pasaporte: 8C054493

INGENIERÍA MUNICIPAL

PLANO

- PLANTA Y DETALLES DE CIELO RASO NIVEL -000 ESCALA 1:100

ARCHIVO .DWG	CIELO RASO
FECHA	30/08/2010
FECHA MODIFICACIÓN	DD/MM/AAAA

ARQUITECTURA | HOJA: 65 | DE: 65