ARQUITECTURA Y DETALLES-P4-R01

TORRE EL PALMAR

PANAMA - 23 DE JUNIO DE 2023


LOA

LUIS CARBALLEDA/ARQUITECTURA

TORRE C | NIVEL -400

PLANTA ARQUITECTONICA

T O R R E C | N I V E L - 4 0 0

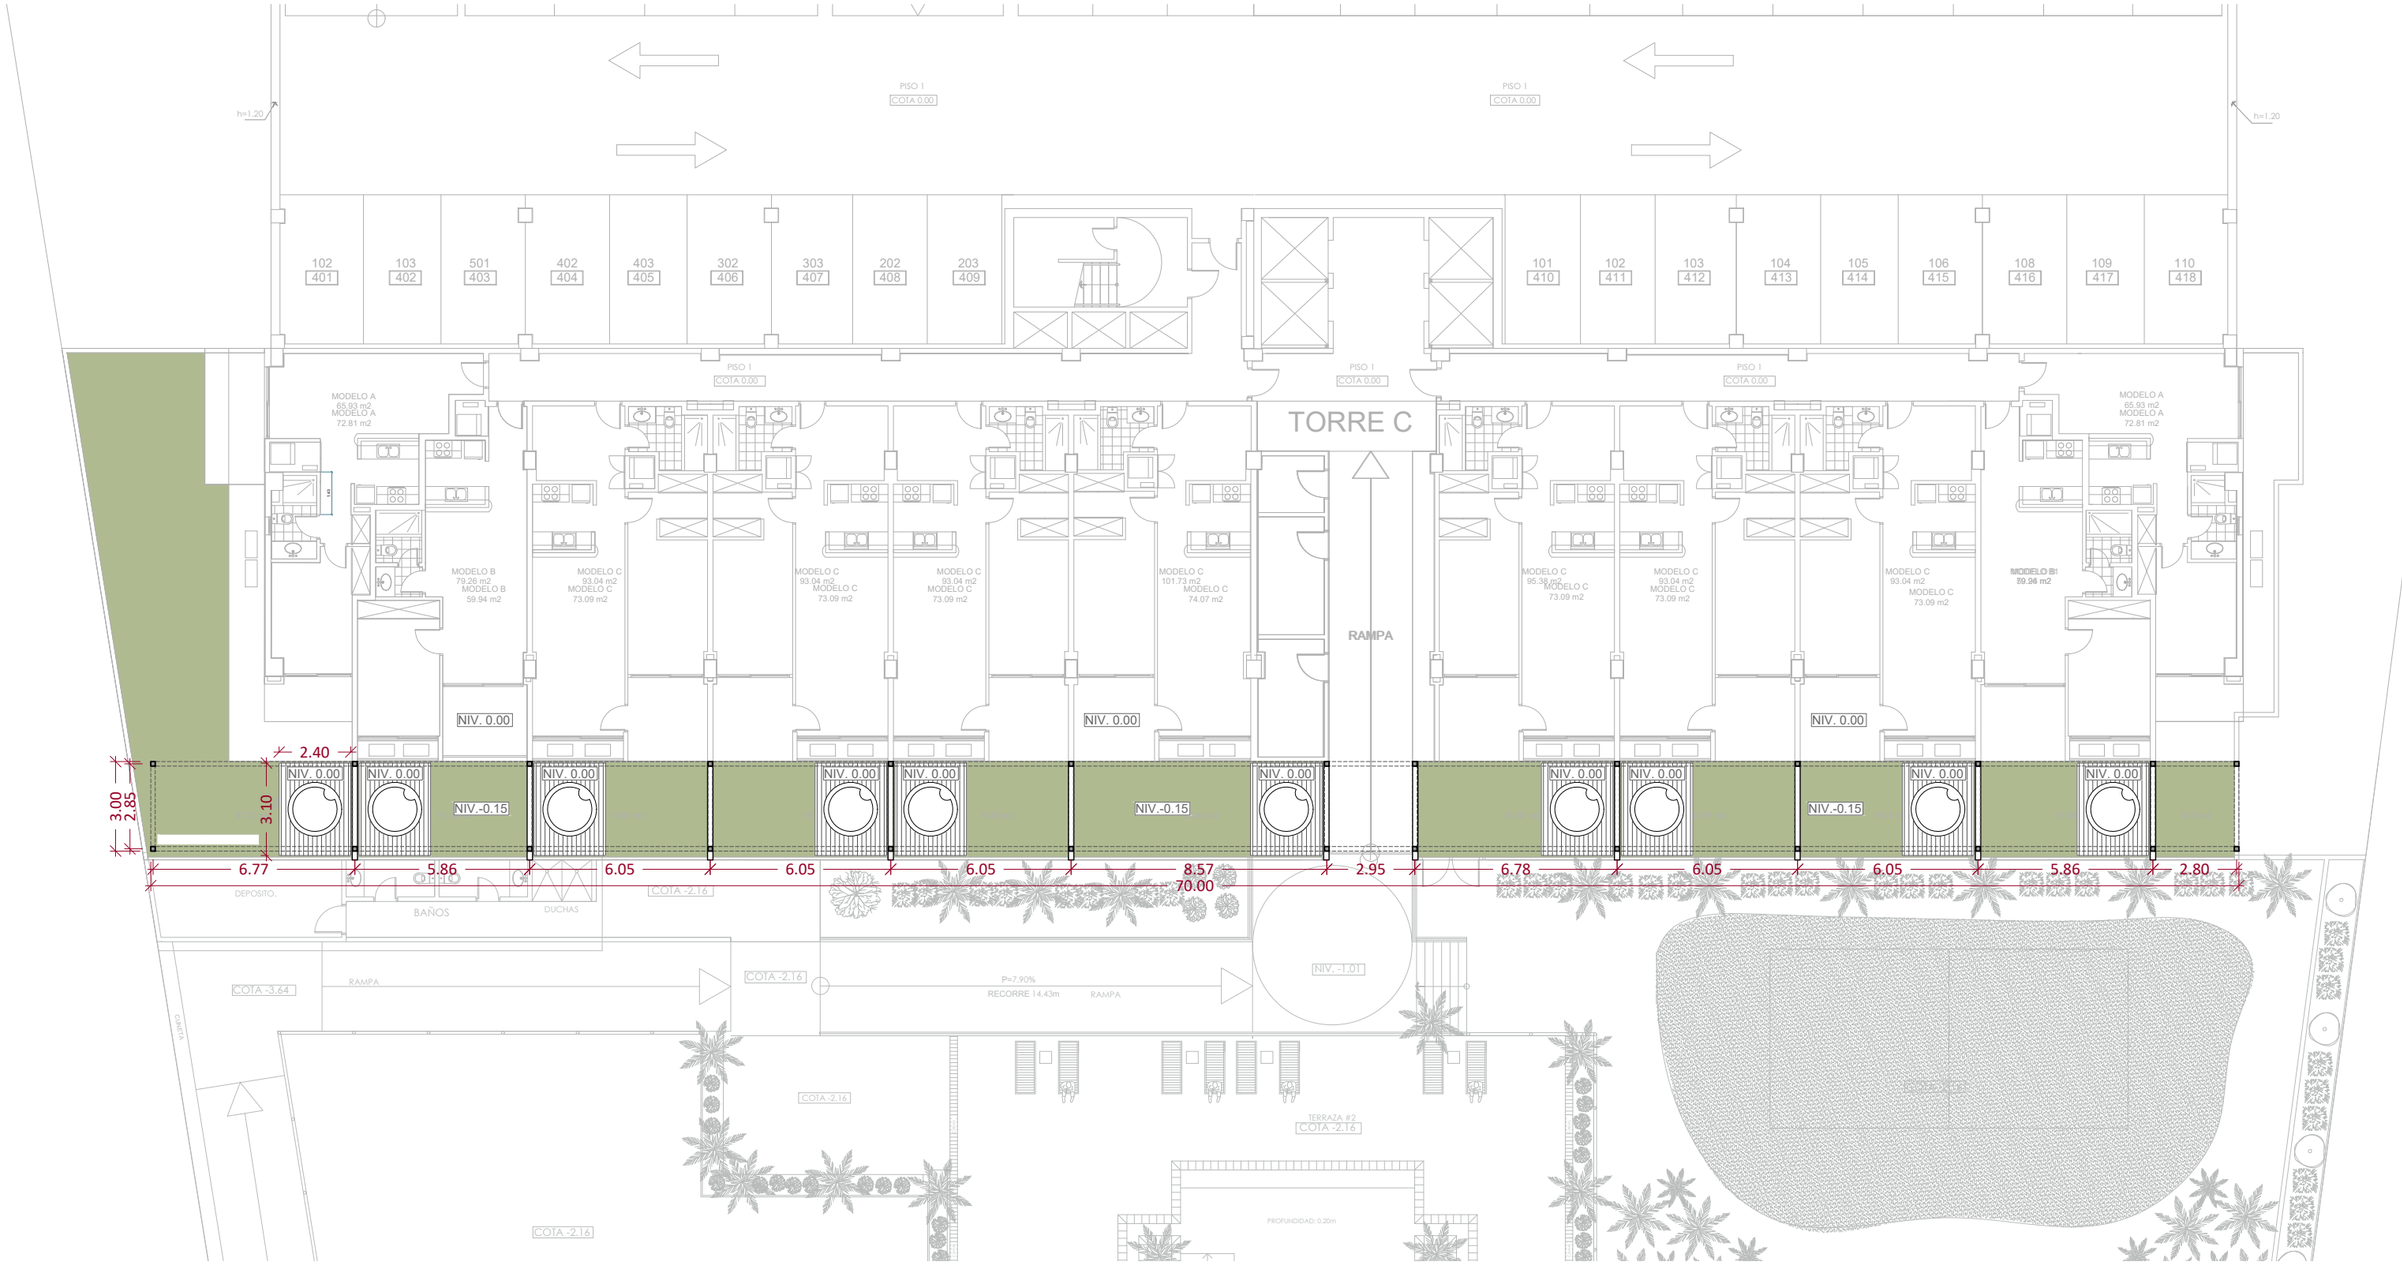

PLANTA ARQUITECTONICA - PLANTA BAJA - TORRE C

ESC: 1:200


PH Evolution Tower | Oficina 3904
Apdo. 0816 - 03096 Panamá

LOA

TORRE C | PLANTA AZOTEA

PLANTA ARQUITECTONICA

TORRE C | PLANTA AZOETA

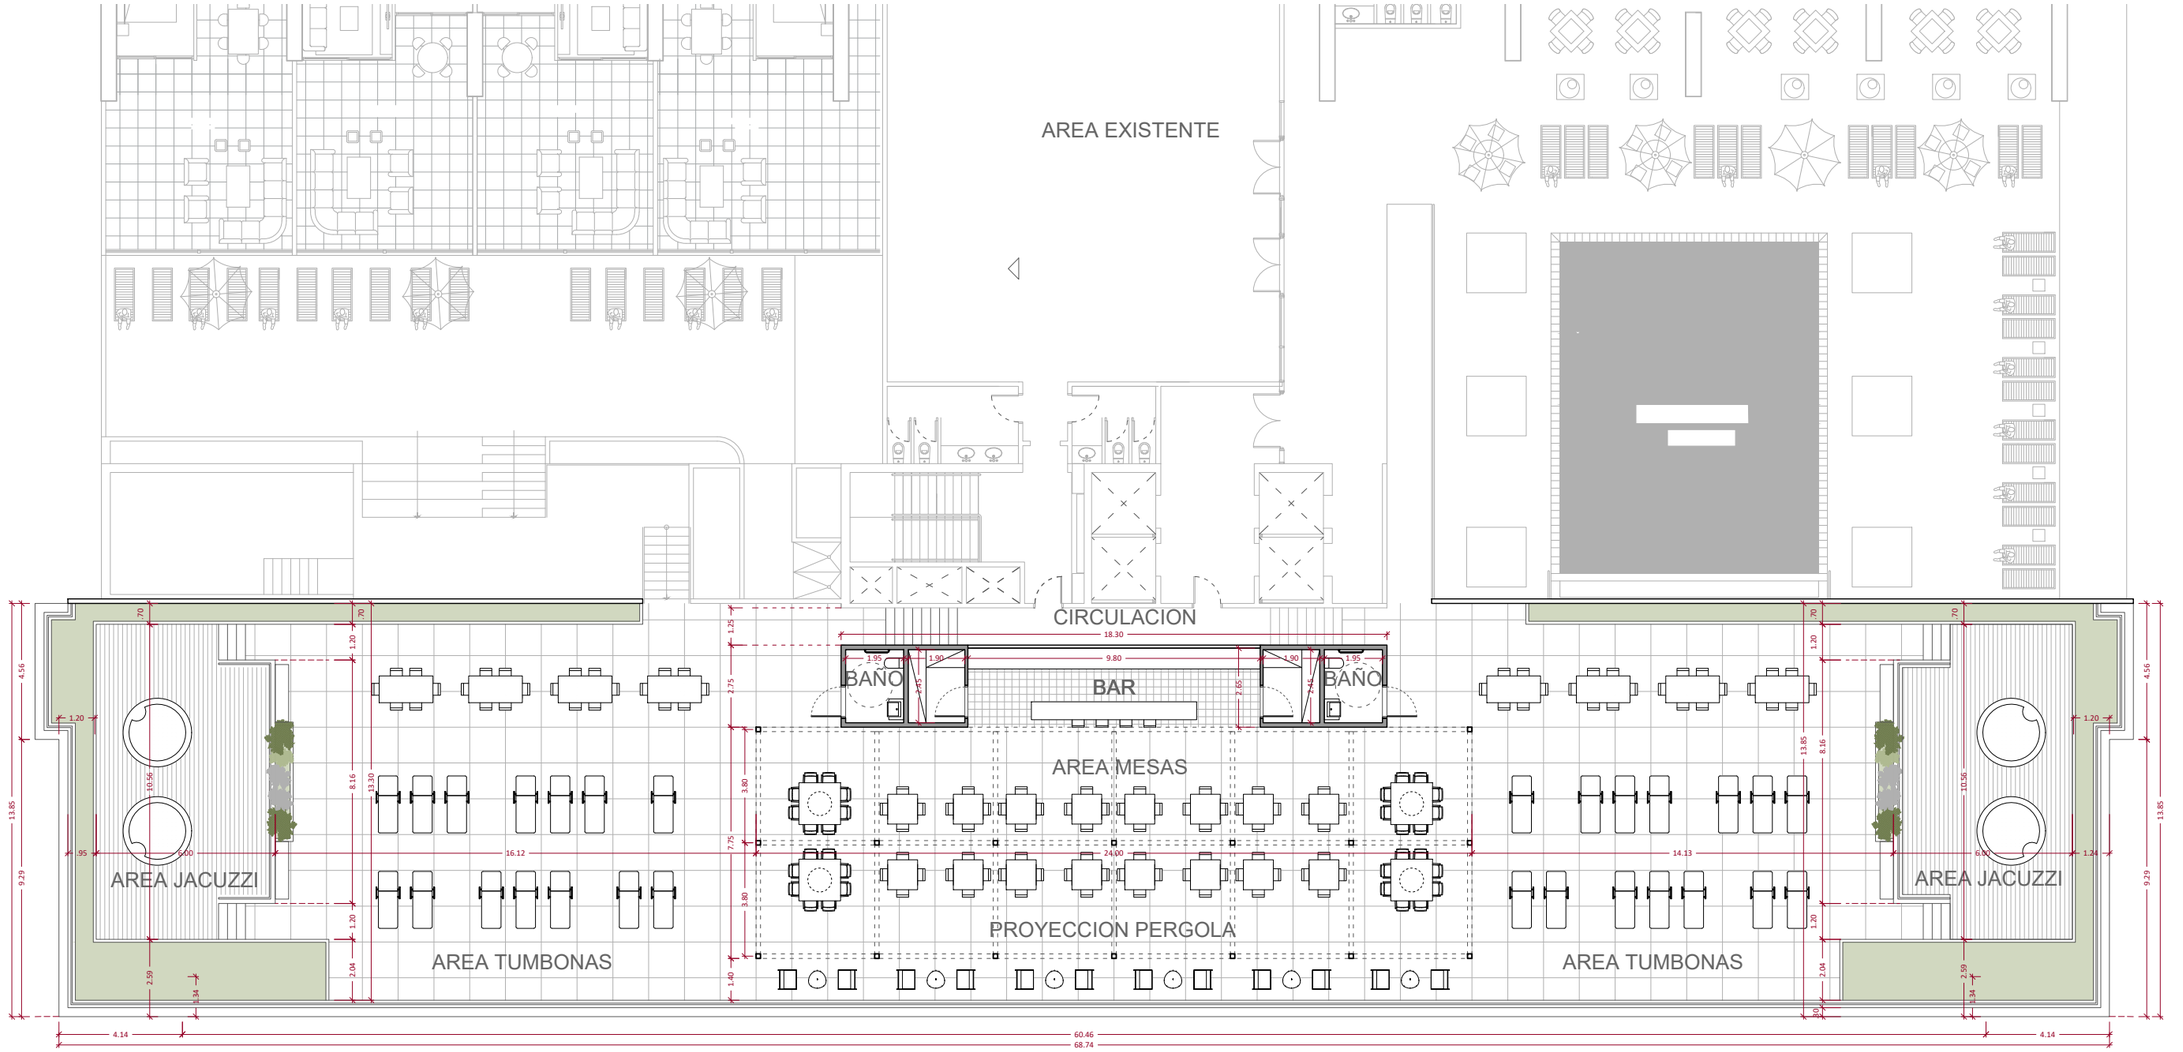


PLANTA ARQUITECTONICA - TORRE C - AZOTEA

ESC: 1:200

PH Evolution Tower | Oficina 3904
Apdo. 0816 - 03096 Panamá

PLANTA ARQUITECTONICA

TORRE C | AMPLIACION AZOTEA ALA D+I

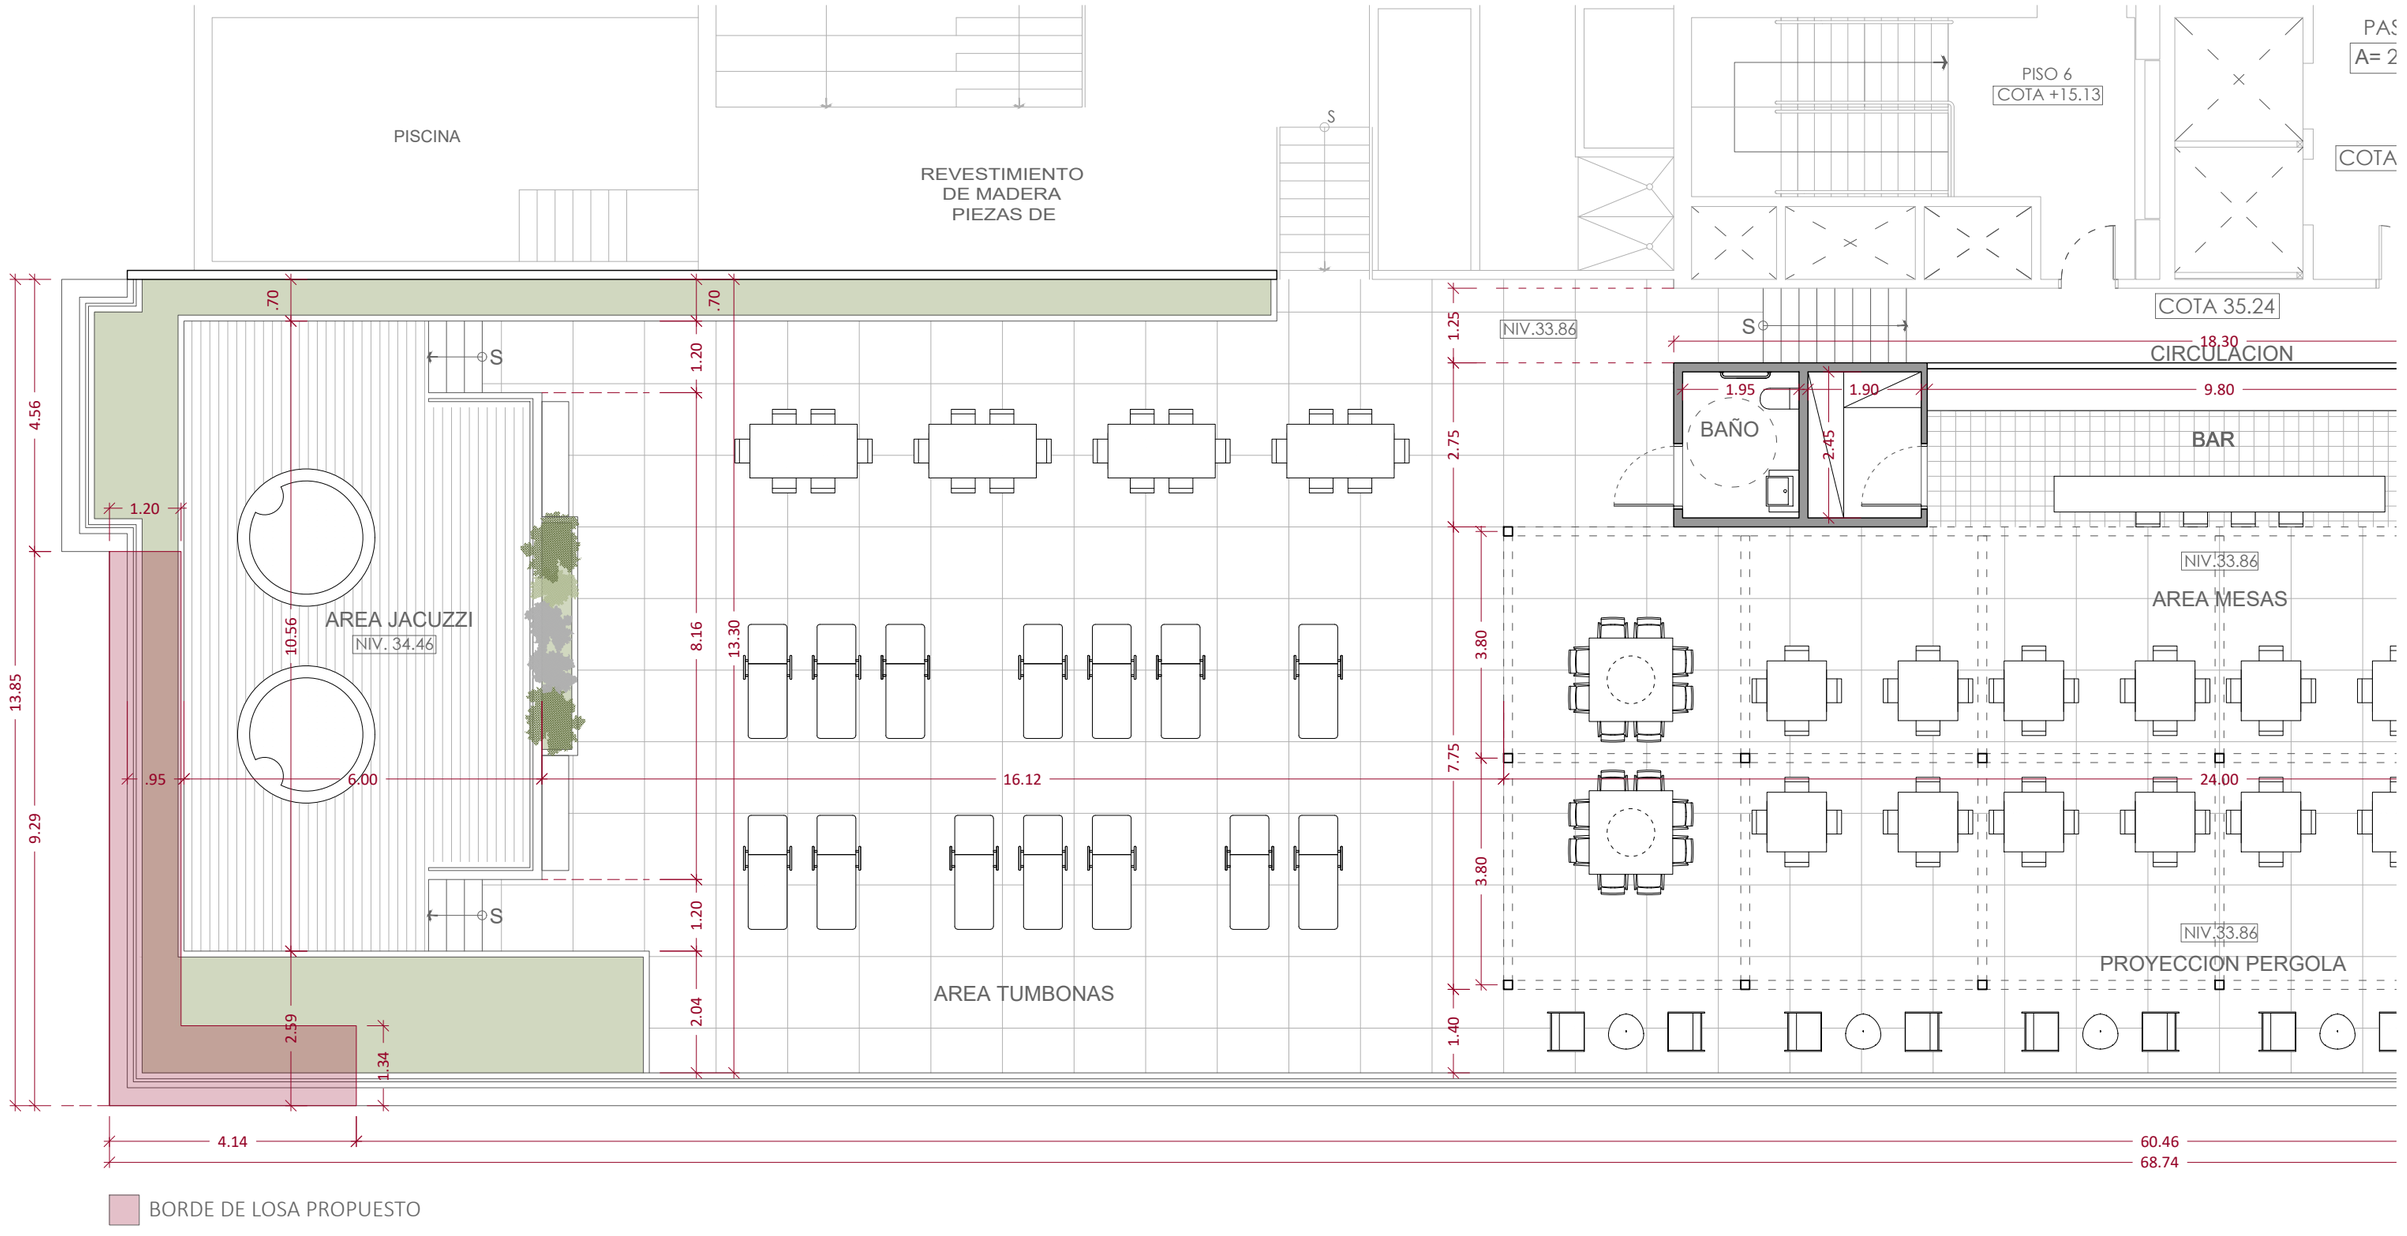


AMPLIACION AZOTEA - AREA DE JACUZZI Y TUMBONAS

ESC: 1:100

PH Evolution Tower | Oficina 3904
Apdo. 0816 - 03096 Panamá

PLANTA ARQUITECTONICA

TORRE C | AMPLIACION AZOTEA AREA CENTRAL

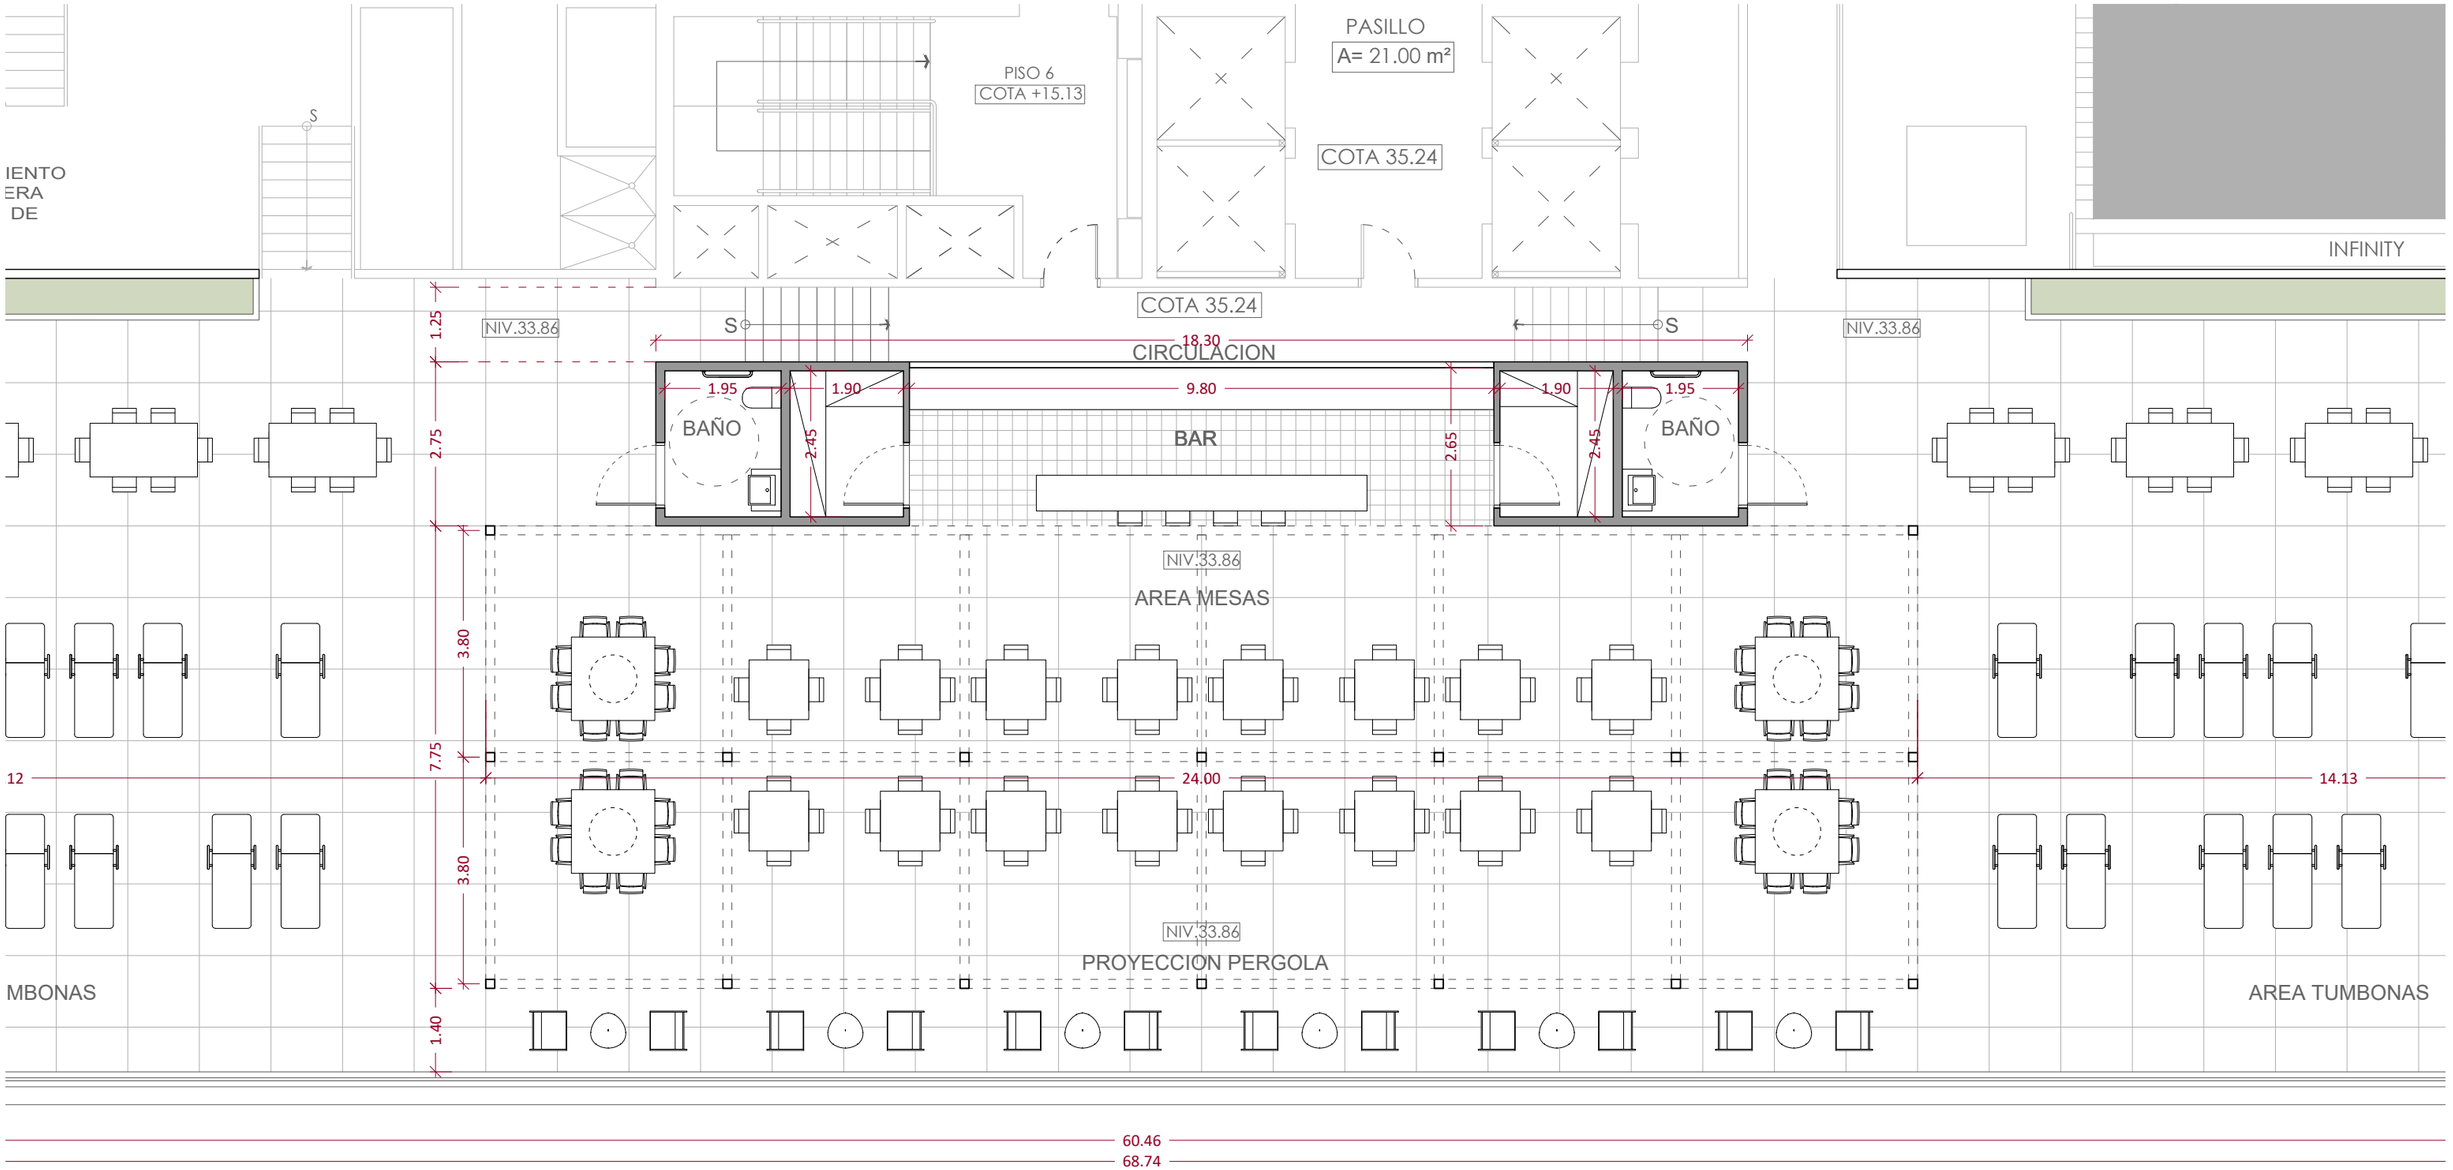

AMPLIACION AZOTEA - AREA DE JACUZZI Y TUMBONAS


ESC: 1:100

PH Evolution Tower | Oficina 3904
Apdo. 0816 - 03096 Panamá

TORRE C | ELEVACIONES PROPUESTA

E L E V A C I O N E S

T O R R E C | E L E V A C I O N F R O N T A L

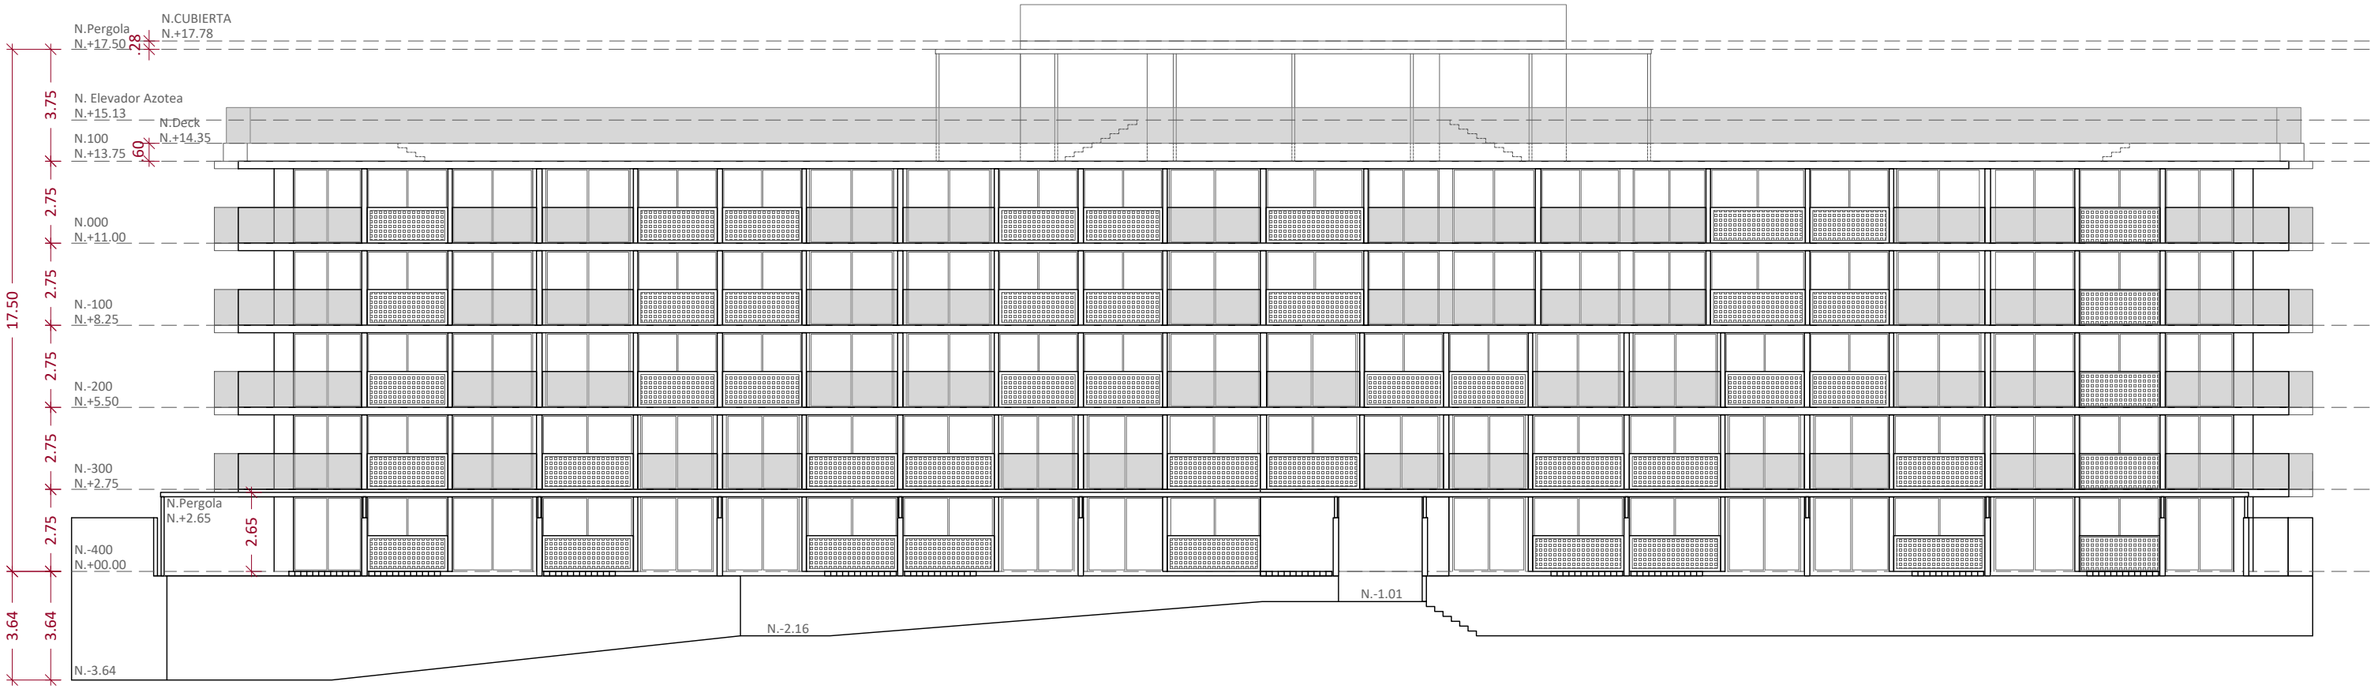

ELEVACION FRONTAL


ESC: 1:200

PH Evolution Tower | Oficina 3904
Apdo. 0816 - 03096 Panamá

LOA

E L E V A C I O N E S

TORRE C 1 ELEVACION LATERAL D+I

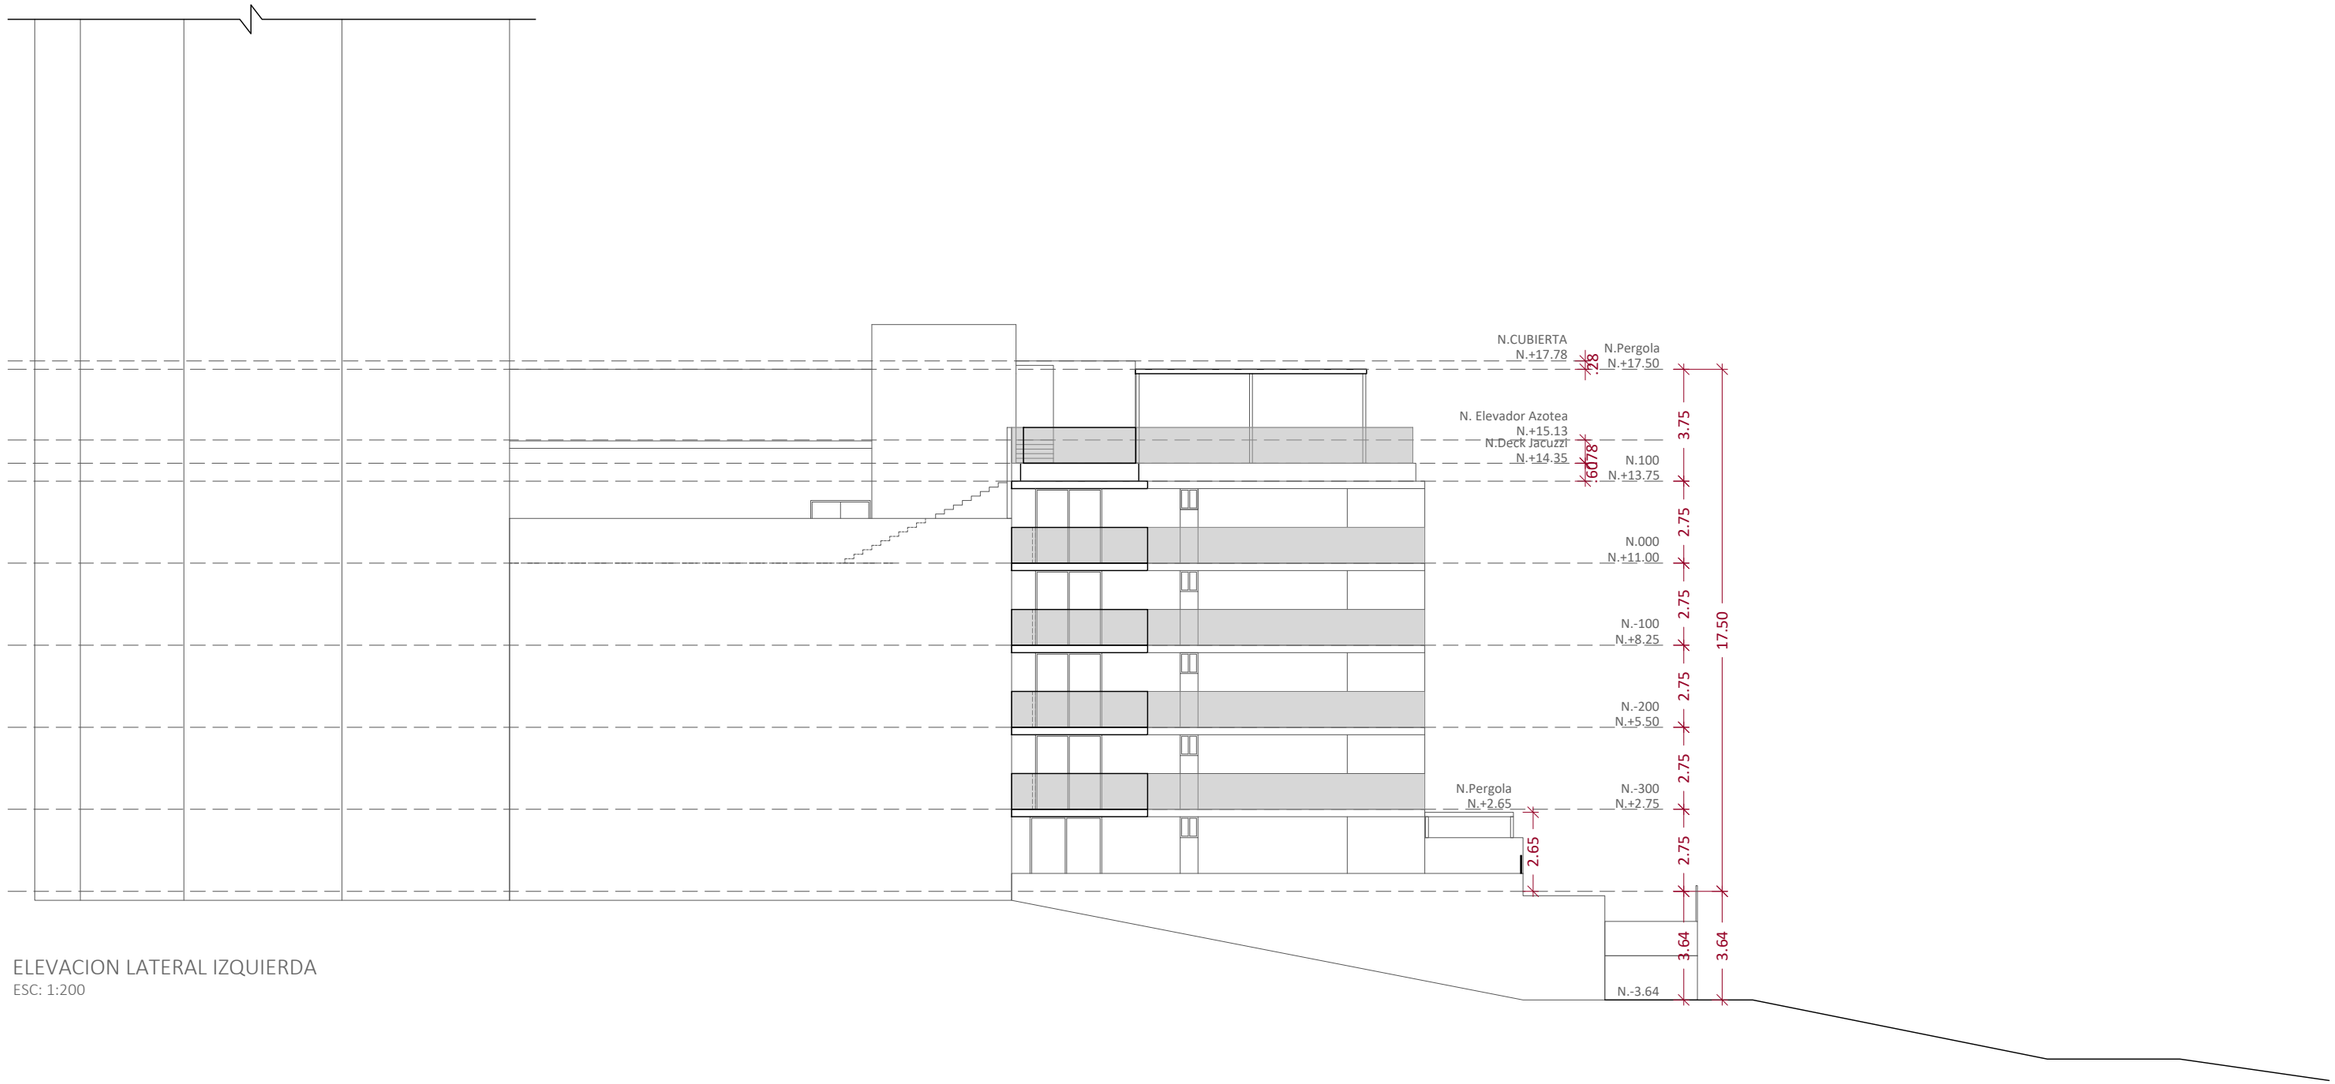


ELEVACION LATERAL IZQUIERDA


ESC: 1:200


PH Evolution Tower | Oficina 3904
Apdo. 0816 - 03096 Panamá

TORRE C | DETALLES CONSTRUCTIVOS

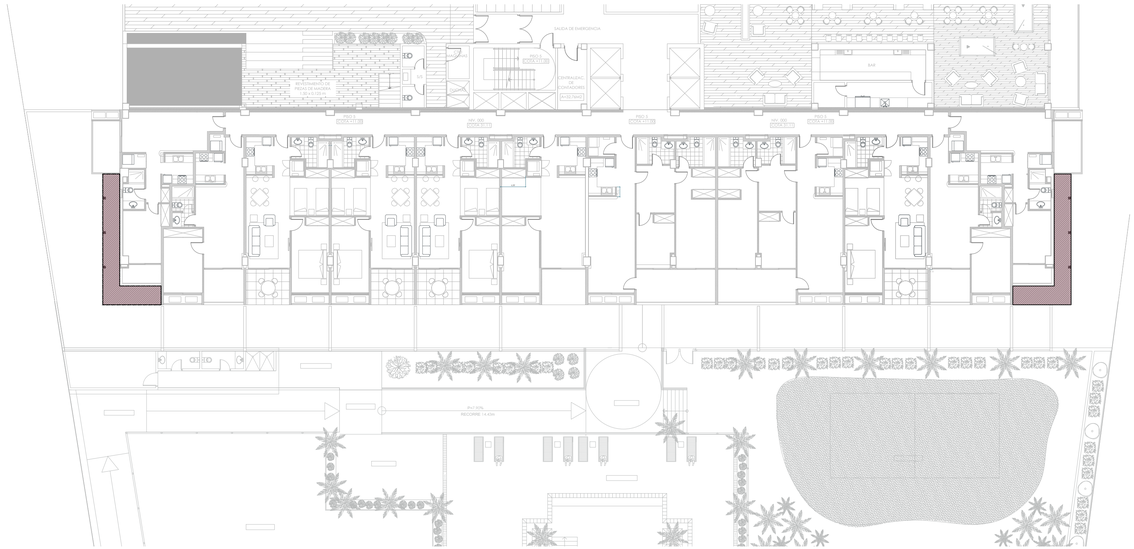


PLANTA GENERAL - UBICACION LOSAS NUEVAS
ESC: 1/500

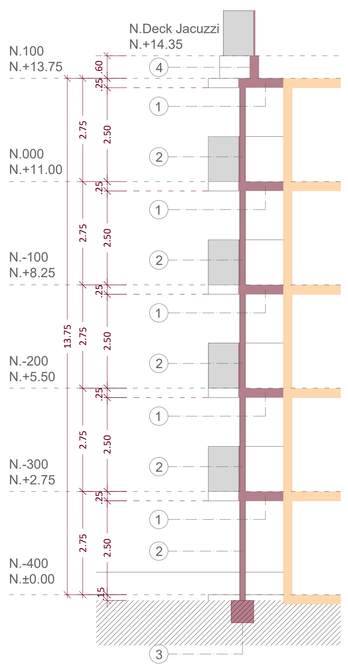

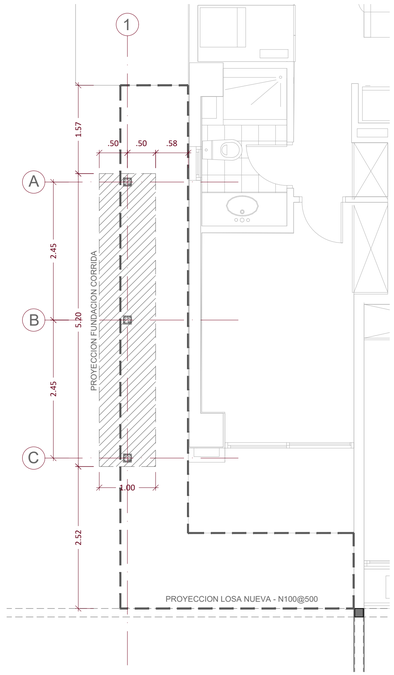

PLANTA ESTRUCTURAL LOSA NUEVA TIPO - NIVEL -400
ESC 1:50

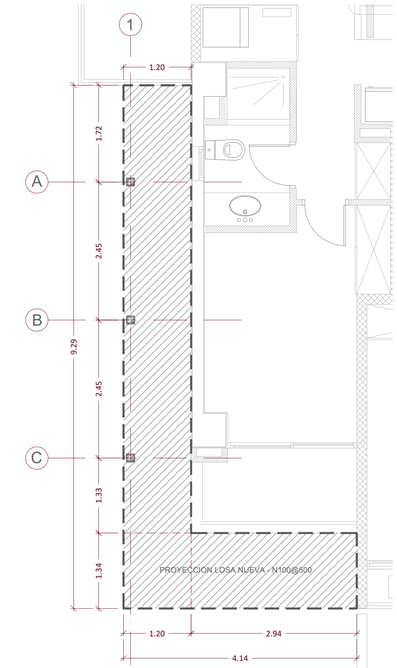

PLANTA ESTRUCTURAL LOSA NUEVA TIPO - NIVEL -300@100
ESC 1:50


LEYENDA

1-Losa de balcon adicional anclada a la estructura existente (espera+epoxi)
2-Portico para voladizo de losa de balcon adicional
3-Cimentacion portico
4-Quicio perimetral


EXISTENTE
PROPUESTA

NOTAS:
- INTERCALAR LAS "3" OPCIONES DE BARRA LISA PARA ANCLAJE.


NOTAS:
- TODAS LAS MEDIDAS GENERALES DEBERAN SER VERIFICADAS EN SITIO.
- LAS MEDIDAS Y CANTIDADES DE PIEZAS METALICAS, ANCLAJES, PERNOS, BARRAS Y OTROS AQUI REPRESENTADOS, SON DE REFERENCIA. VERIFICAR Y ESPECIFICAR CON ING. ESTRUCTURAL.
- LOS DETALLES TECNICOS E INFORMACION RELACIONADA A ESTRUCTURA, ANCLAJE Y SEGURIDAD, DEBERAN SER REVISADOS Y PRESCRITOS POR ING. DE ESTRUCTURA.

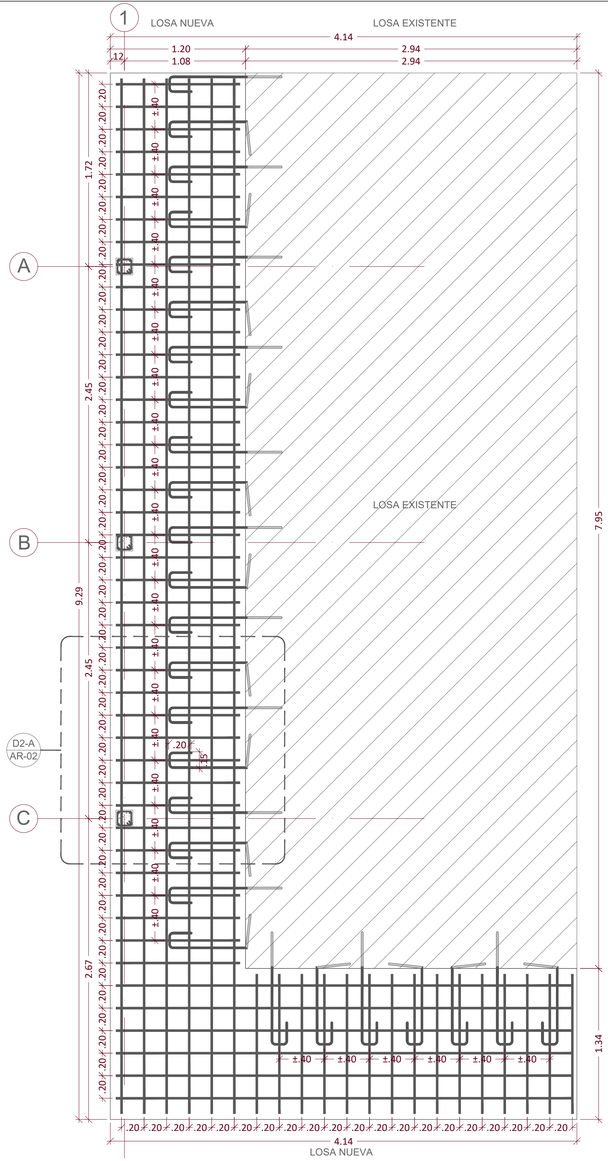


DETALLE ANCLAJE LOSA EXISTENTE - LOSA NUEVA - PLANTA
ESC 1:25

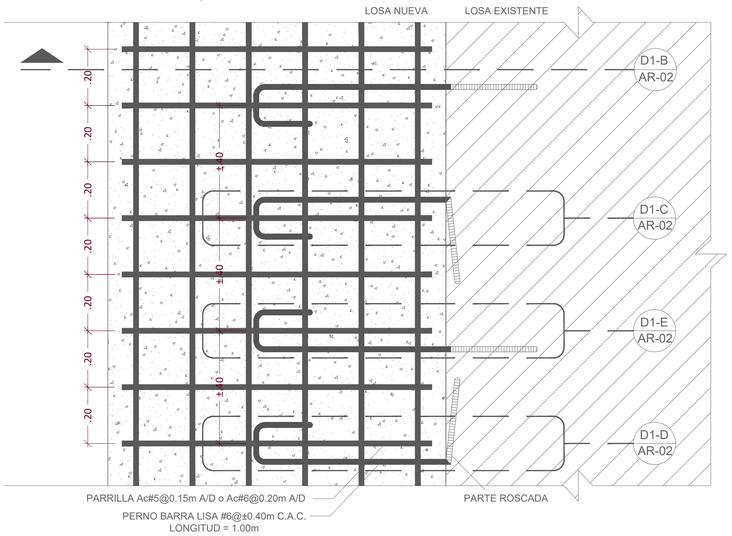


DETALLE DE ANCLAJE LOSA EXISTENTE - LOSA NUEVA - PLANTA
D2-A
ESC 1:10

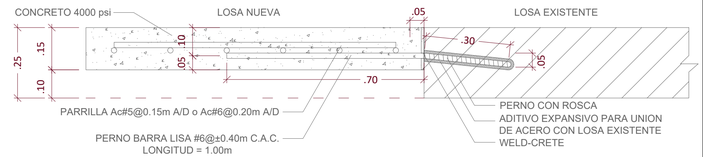

DETALLE DE ANCLAJE LOSA EXISTENTE - LOSA NUEVA - SECCION
D2-B
ESC 1:10

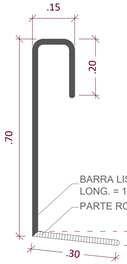


DETALLE BARRA LISA 1
D2-C
ESC 1:10

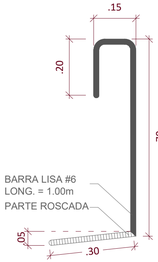


DETALLE BARRA LISA 1
D2-D
ESC 1:10




DETALLE BARRA LISA 1
D2-E
ESC 1:10

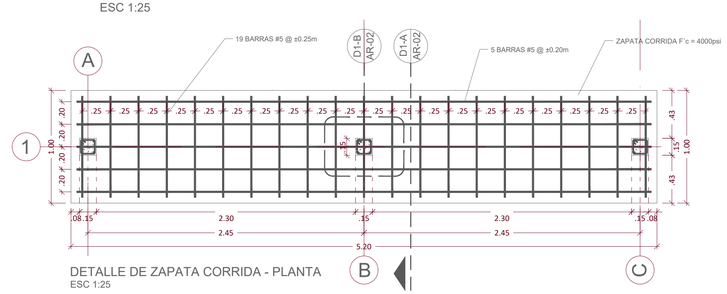

DETALLE DE ZAPATA CORRIDA - PLANTA
ESC 1:25

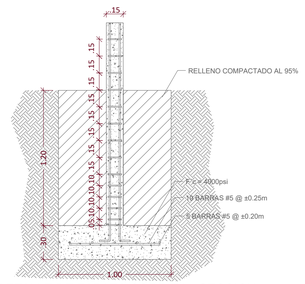

DETALLE DE ZAPATA CORRIDA - SECCION
D1-A - ESC 1:25

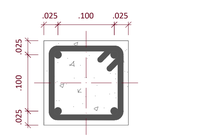

COLUMNA DE CONCRETO 0.15m X 0.15m
CON 4 BARRAS #4 CORRUGADAS + ESTRIBOS #3

ESTRIBOS #3:
- 2 @ 0.05m
- 5 @ 0.10m
- RESTO @ 0.15m

DETALLE DE COLUMNA
D1-B
ESC 1:5

NOT APPROVED


LOA
LUIS CARBALLEDA/ARQUITECTURA

PROYECTO:	ARQUITECTURA
PROPIEDAD:	CALCULO Y ESTRUCTURA
UBICACION:	DISEÑO ELECTRICO
CONTENIDO:	DISEÑO HIDROSANITARIO
ESCALA Indicada	SISTEMAS ESPECIALES
HOJA	DIBUJO Y DESARROLLO
ING. MUNICIPAL / REP. LEGAL	FECHA

FECHA	REVISION	POR


DETALLES CONSTRUCTIVOS

TORRE C | BARANDILLA METALICA

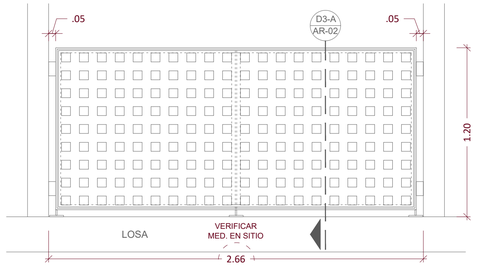


BARANDA LAMIN. PERFORADA - VISTA EXTERIOR

ESC 1:20

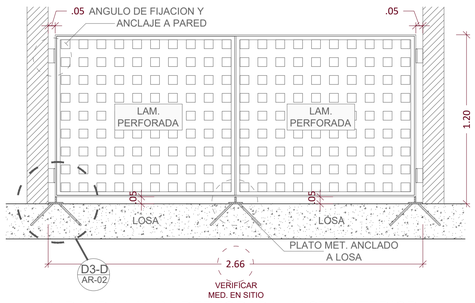


BARANDA LAMIN. PERFORADA - VISTA INTERIOR

ESC 1:20

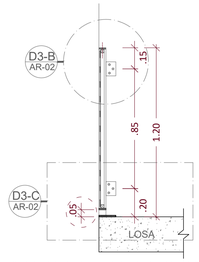


BARANDA LAMIN. PERFORADA
SECCION D3-A

ESC 1:20

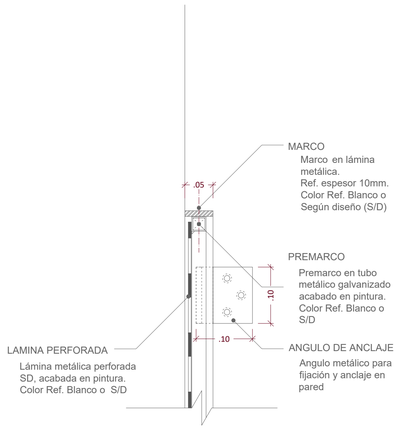


DETALLE DE BARANDA LAMINA PERFORADA
D3-B

ESC 1:5

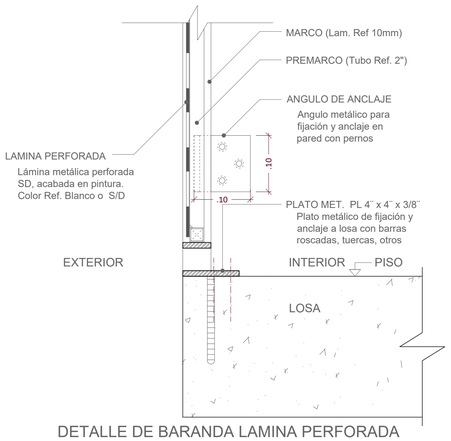

DETALLE DE BARANDA LAMINA PERFORADA
D3-C

ESC 1:5

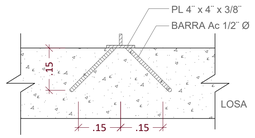

DETALLE BARANDA - ANCLAJE A LOSA
D3-D

ESC 1:10

DETALLES CONSTRUCTIVOS

TORRE C | BARANDILLA VIDRIO Ttemplado




BLOQUE DE ALUMINIO PARA VIDRIOS
Longitud de pieza 150mm. Con tacos de anclaje, cuñas de vidrios de PVC. Recomendación de fabricante: usar 2 piezas por cada panel de vidrio de 1 metro.




COBERTORES
Tapa de los bloques de aluminio, para acabado.
Con goma para sellar vidrio. Para exteriores




TAPA FINAL DE TRAMO

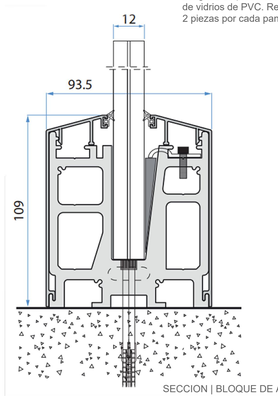

SECCION | BLOQUE DE ALUMINIO

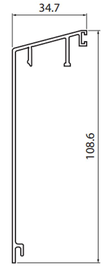

SECCION | COBERTOR

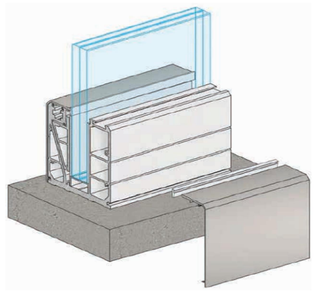

VISTA DEL SISTEMA

NOTAS:

- TODAS LAS BARANDAS DEBEN TENER UNA ALTURA DE h = 1.20 m, PARA CUMPLIMIENTO DE NORMA.
- ENTRAR EN CONTACTO CON PROVEEDOR Y USAR DETALLE SIMILAR AL AQUI EXPUESTO.
- LOS DETALLES AQUI EXPUESTOS SON DE REFERENCIA, FUERON EXTRAIDOS DEL MANUAL DEL FABRICANTE. PARA MAYORES DETALLES TECNICOS SOBRE PERFILES, ANCLAJES, ESPESORES DE VIDRIO, INSTALACION, ENTRE OTROS, ENTRAR EN CONTACTO CON EMPRESAS CARBONE, www.empresascarbone.com.
- VERIFICAR EN SITIO Y EN AREAS DE INSTALACION, SISTEMAS DE DRENAJES DE AGUA. EN CASO DE QUE LAS AREAS NO CUENTEN CON SISTEMAS DE DRENAJES, ENTRAR EN CONTACTO CON "LOA" PARA ESTUDIAR SOLUCION.
- SE RECOMIENDA LA INSTALACION DE (2) PIEZAS DE HERRRAJES, "PISA VIDRIO" O SOPORTES DE VIDRIO EN LOS EXTREMOS LATERALES, PARA FIJACION EN PARED. VER OPCIONES CON PROVEEDOR.
- LA BARANDA PUEDE QUEDAR SIN PASAMANOS, POR LO QUE LOS CANTOS DE LOS VIDRIOS TIENEN QUE TENER ACABADO PARA USARLOS PARA TAL FIN, SIN RIESGO DE CORTE. EN CASO DE REQUERIRSE PASAMANOS, SE RECOMIENDA ELEGIR CON PROVEEDOR UN TUBO DE ACERO INOXIDABLE O MISMO ACABADO DEL PERFIL Y BLOQUE DE FIJACION DEL VIDRIO.







NOT APPROVED

LOA
LUIS CARBALLEDA/ARQUITECTURA

PROYECTO:			ARQUITECTURA
PROPIEDAD:			CALCULO Y ESTRUCTURA
UBICACION:			DISEÑO ELECTRICO
CONTENIDO:			DISEÑO HIDROSANITARIO
		ESCALA Indicada	SISTEMAS ESPECIALES
		HOJA	DIBUJO Y DESARROLLO
ING. MUNICIPAL	REP. LEGAL		FECHA

FECHA	REVISION	POR

TORRE C | VISTAS 3D

IMAGENES PROPUESTA

TORRE C | VISTAS DEL PROYECTO



PH Evolution Tower | Oficina 3904
Apdo. 0816 - 03096 Panamá

LOA

IMAGENES PROPUESTA

TORRE C | VISTAS DEL PROYECTO



PH Evolution Tower | Oficina 3904
Apdo. 0816 - 03096 Panamá

LOA

IMAGENES PROPUESTA

TORRE C | VISTAS DEL PROYECTO



PH Evolution Tower | Oficina 3904
Apdo. 0816 - 03096 Panamá

IMAGENES PROPUESTA

TORRE C | VISTAS DEL PROYECTO



PH Evolution Tower | Oficina 3904
Apdo. 0816 - 03096 Panamá

LOA



LOA es una oficina abierta y colaborativa de arquitectura dirigida por el arquitecto Luis Carballeda.

Con sede en ciudad de Panamá y con un alcance global, LOA cuenta con amplia experiencia en diseño, arquitectura, interiorismo, urbanismo, planes maestros y gestión integral en obras y proyectos.

La oficina se enfoca en la investigación y en un método de diseño colaborativo que involucra a un equipo multidisciplinar conformado por profesionales de varias partes del mundo, abocados a ofrecer soluciones innovadoras en proyectos que mejoran la calidad de los espacios que habitamos y de nuestras ciudades.

Actualmente, contamos con un portafolio diverso de proyectos; residenciales, hoteleros, corporativos, comerciales e institucionales, donde se ha tomado como premisa la valoración del paisaje y su contexto para obtener espacios armónicos que generan nuevas experiencias entre sus habitantes, con una arquitectura propia del lugar, sostenible y más comprometida con el medio ambiente.

LOA

LUIS CARBALLEDA / ARQUITECTURA